
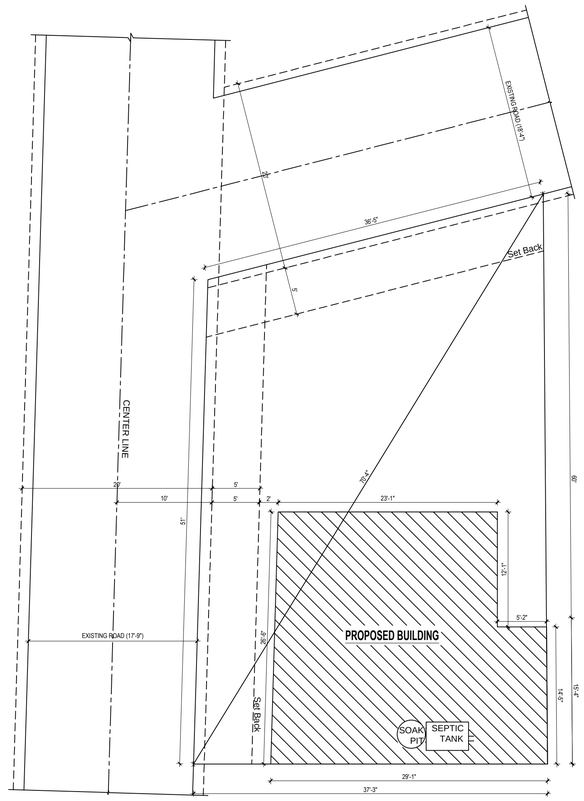



SITE PLAN

LAND AREA : 2012.53 SQ.FT.
SITE AREA : 2008.47 SQ.FT.
PLINTH AREA: 692.96 SQ.FT.

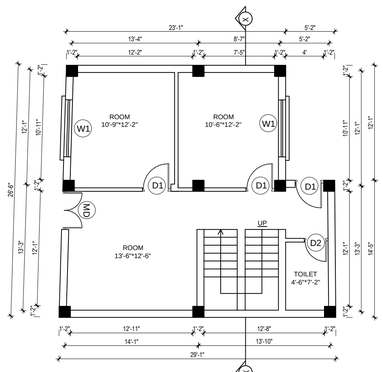


GROUND FLOOR PLAN

AREA : 692.96 SQ. FT.

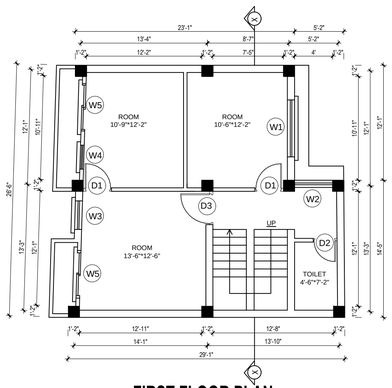


FIRST FLOOR PLAN

AREA : 737.88 SQ. FT.

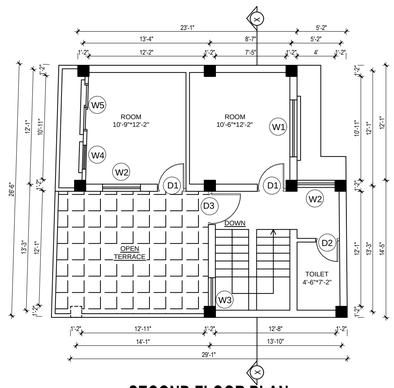


SECOND FLOOR PLAN

AREA : 539.35 SQ. FT.

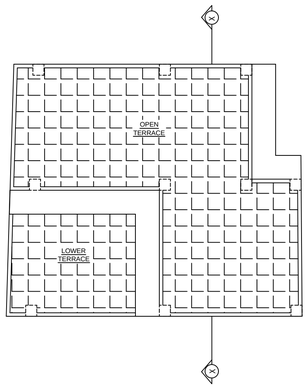


ROOF FLOOR PLAN

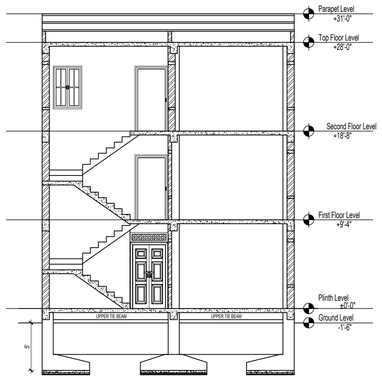


SECTION AT X-X

OPENING SCHEDULE


SN	DESCRIPTION	SYM.	SIZE	NO.	REMARKS
1	MAIN DOOR	MD	4'-0" X 8'-0"	1	
2	DOOR	D1	3'-0"x7'-0"	7	
3	DOOR	D2	2'-6"x7'-0"	3	
4	DOOR	D3	3'-6" X 7'-0"	2	
5	WINDOW	W1	6'-0" X 4'-6"	4	
6	WINDOW	W2	4'-0" x 4'-6"	3	
7	WINDOW	W3	3'-0" x 4'-6"	1	
8	WINDOW	W4	2'-6" x 4'-6"	2	
9	WINDOW	W5	5'-0" x 6'-6"	3	

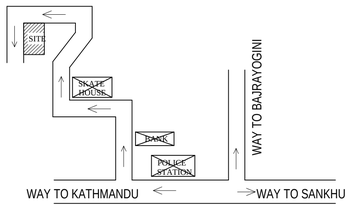


LOCATION PLAN
NOT IN SCALE

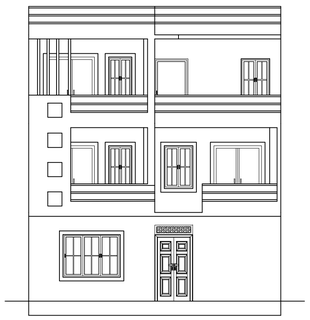


WEST ELEVATION

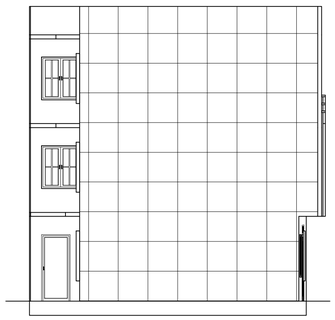

NORTH ELEVATION

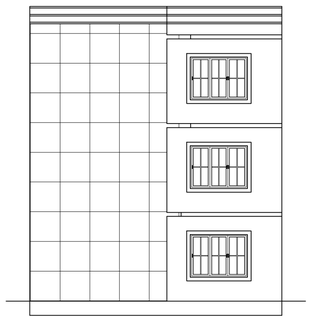

EAST ELEVATION

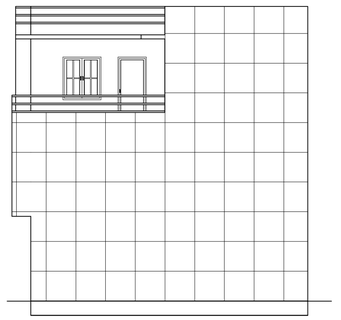

SOUTH ELEVATION

FOR OFFICIAL USE ONLY

OWNER SIGNATURE
MRS. LAXMI ROKAYA

BUILDING TYPE: RESIDENTIAL	LOCATION: SHANKHARAPUR 6, SHANKHARAPUR MUNICIPALITY	
PLOT NO: 353, 142	LAND AREA:0-3-2-0.505, 0-2-1-1.58 as purja PLINTH AREA: 692.96 sq.ft.	FAR=0.98 GCR=34.43
DETAILS: ARCHITECTURAL DRAWING		
DRAWN BY: DINESH KHOTEJA	CHECKED BY: ER. MENAKA SUWAL	
NEC NO: 14037 CIVIL "A"		
DATE:2083	SCALE: 1/8"=1'-0"	SHEET NO. 1 /1