
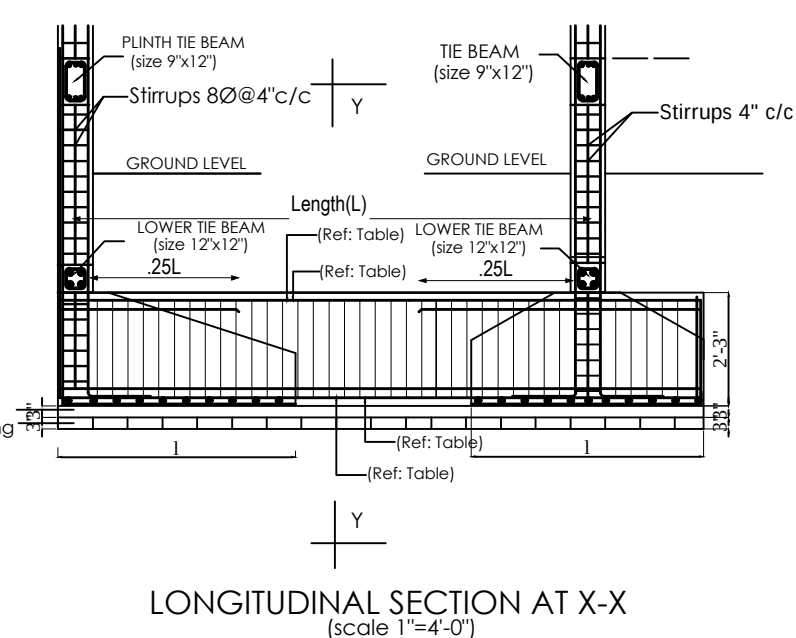
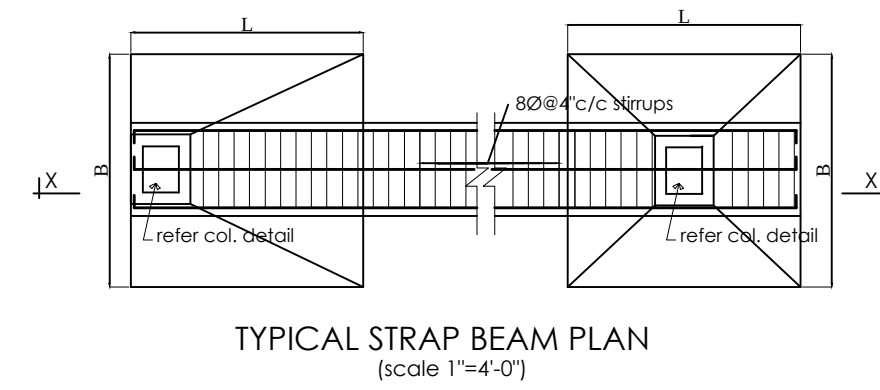
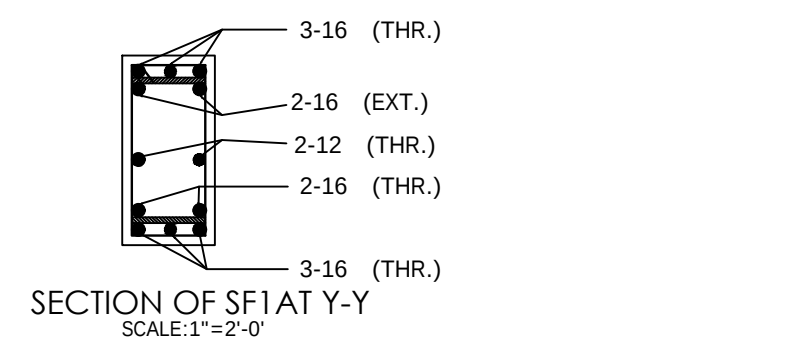
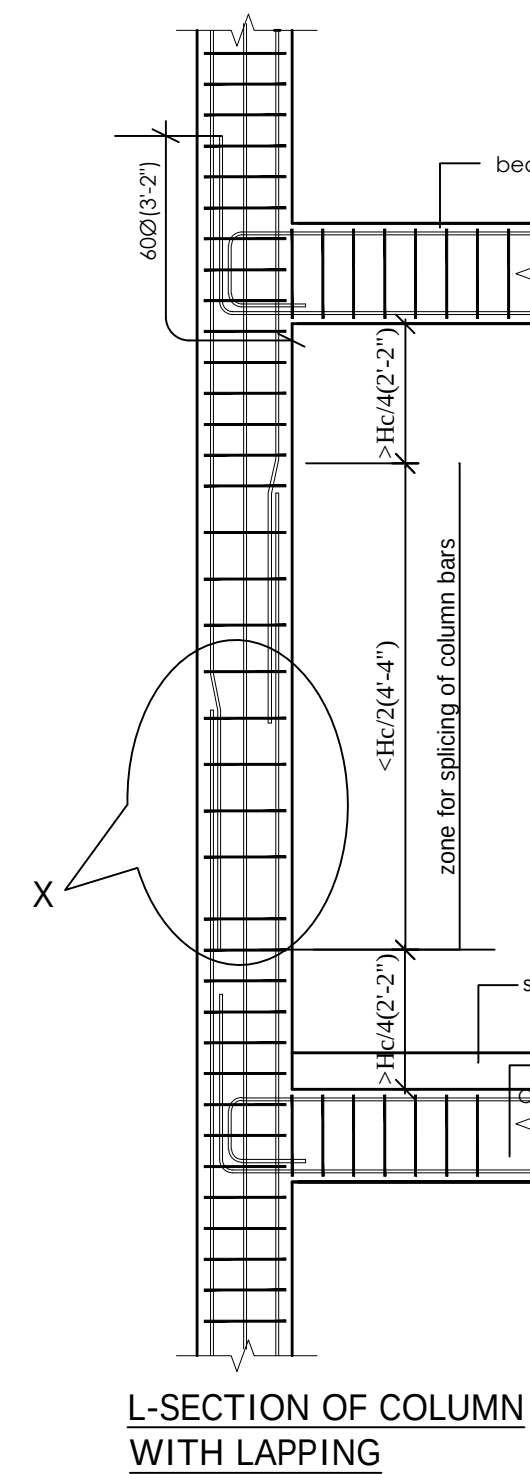
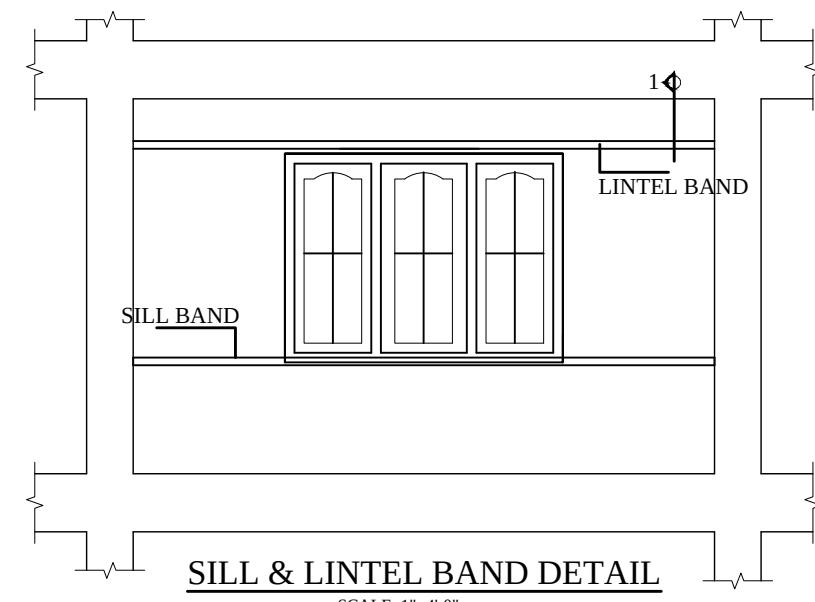
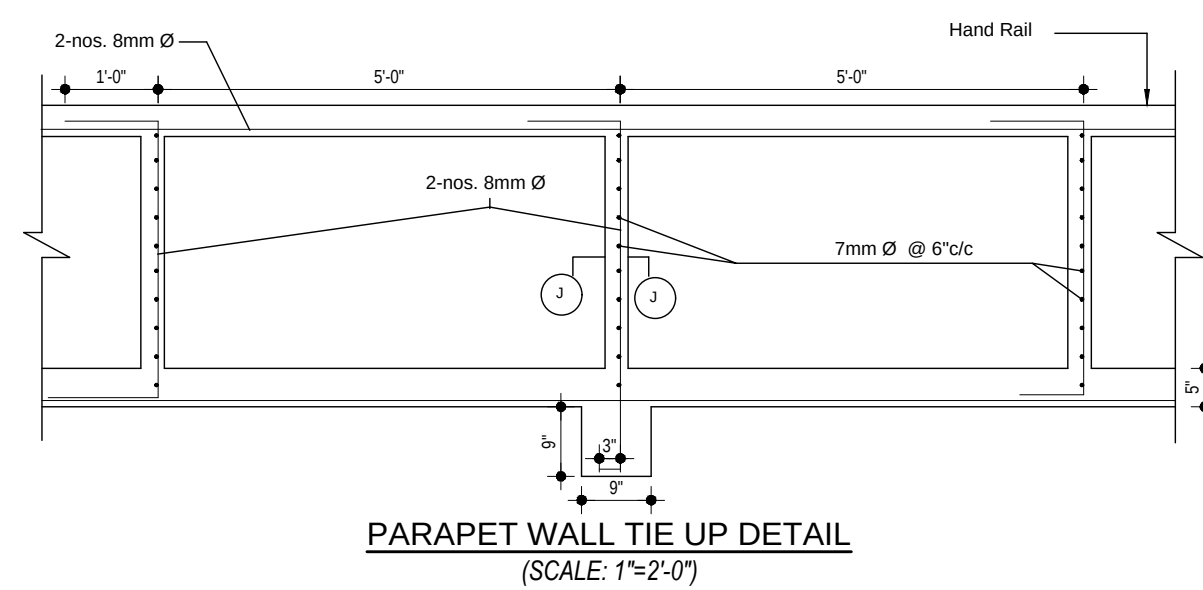
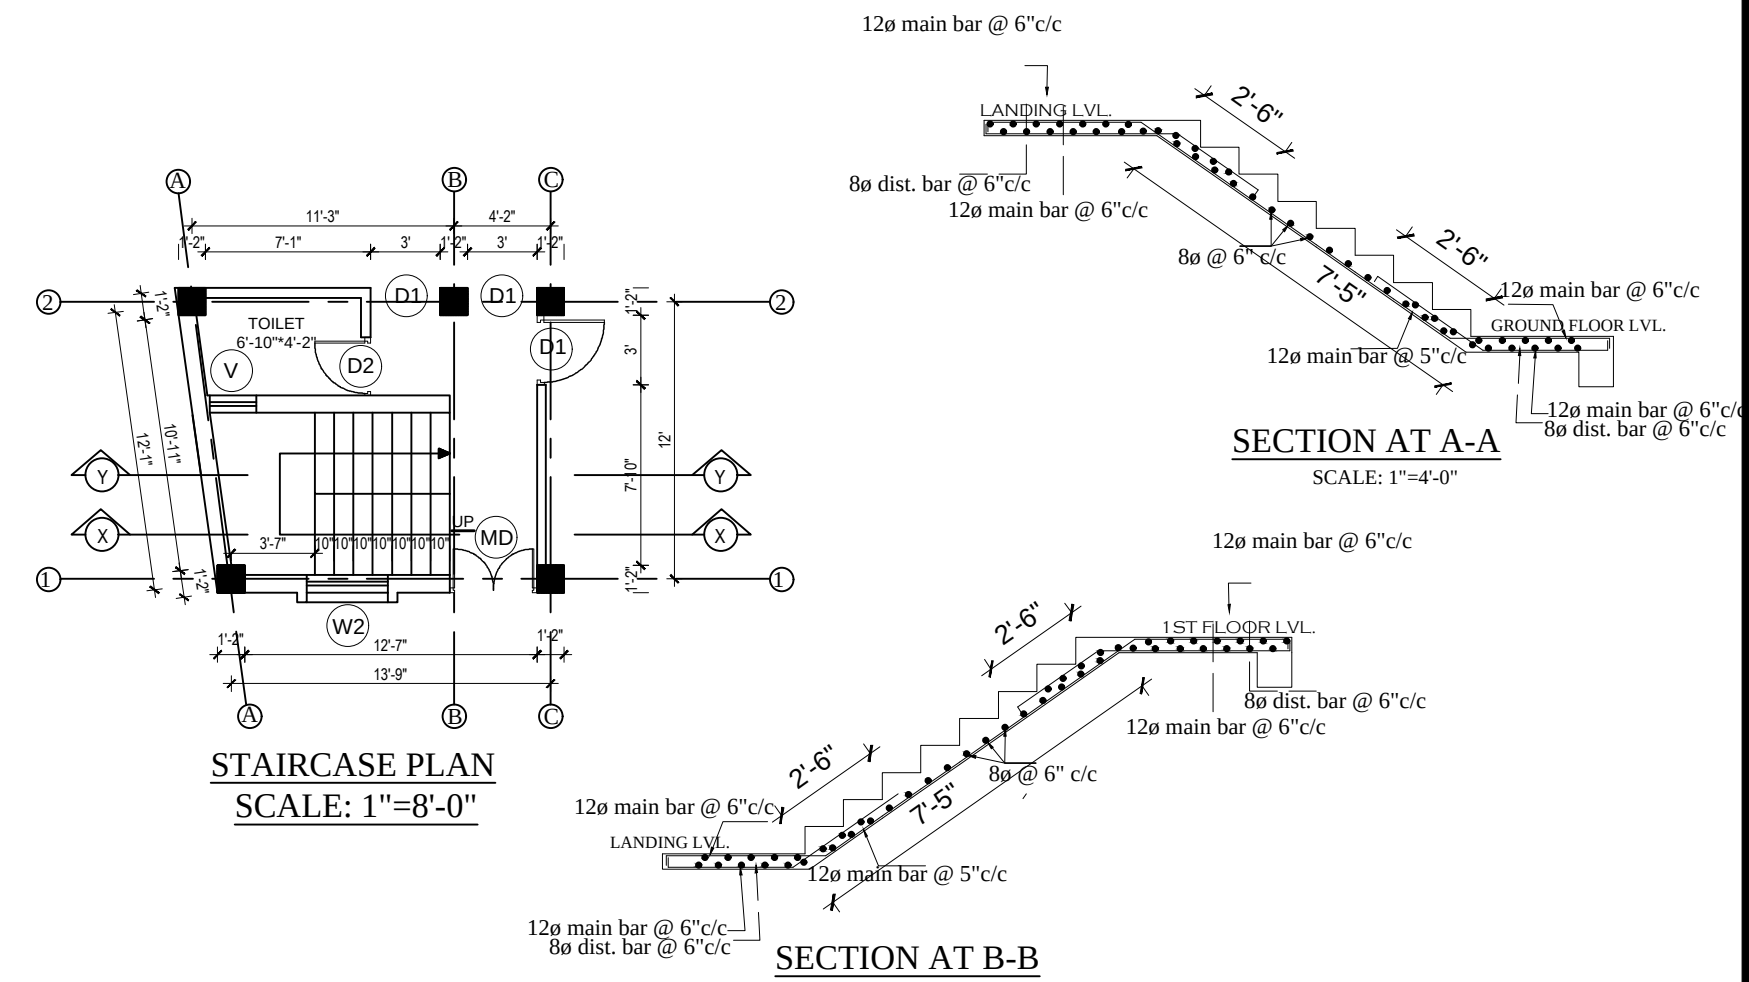
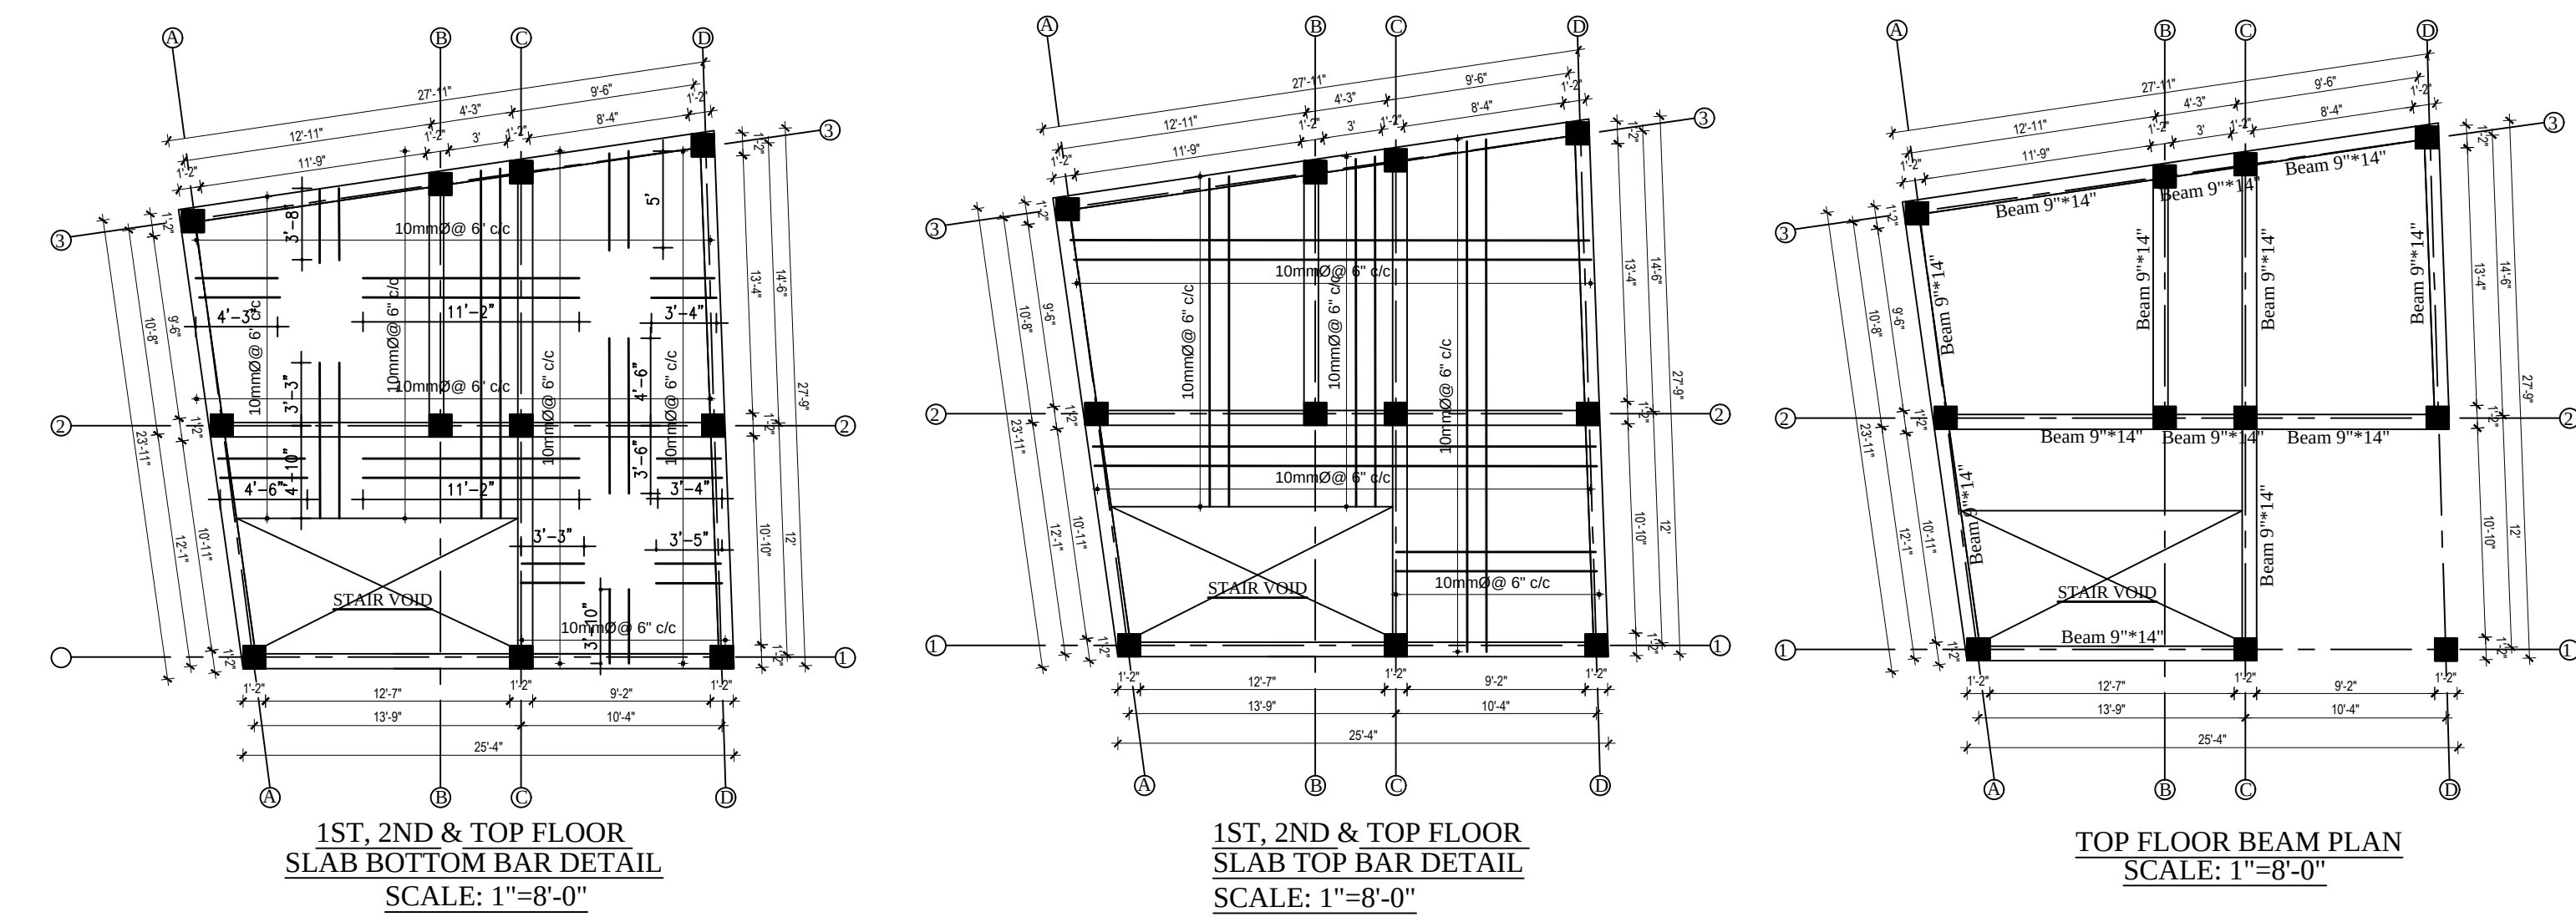


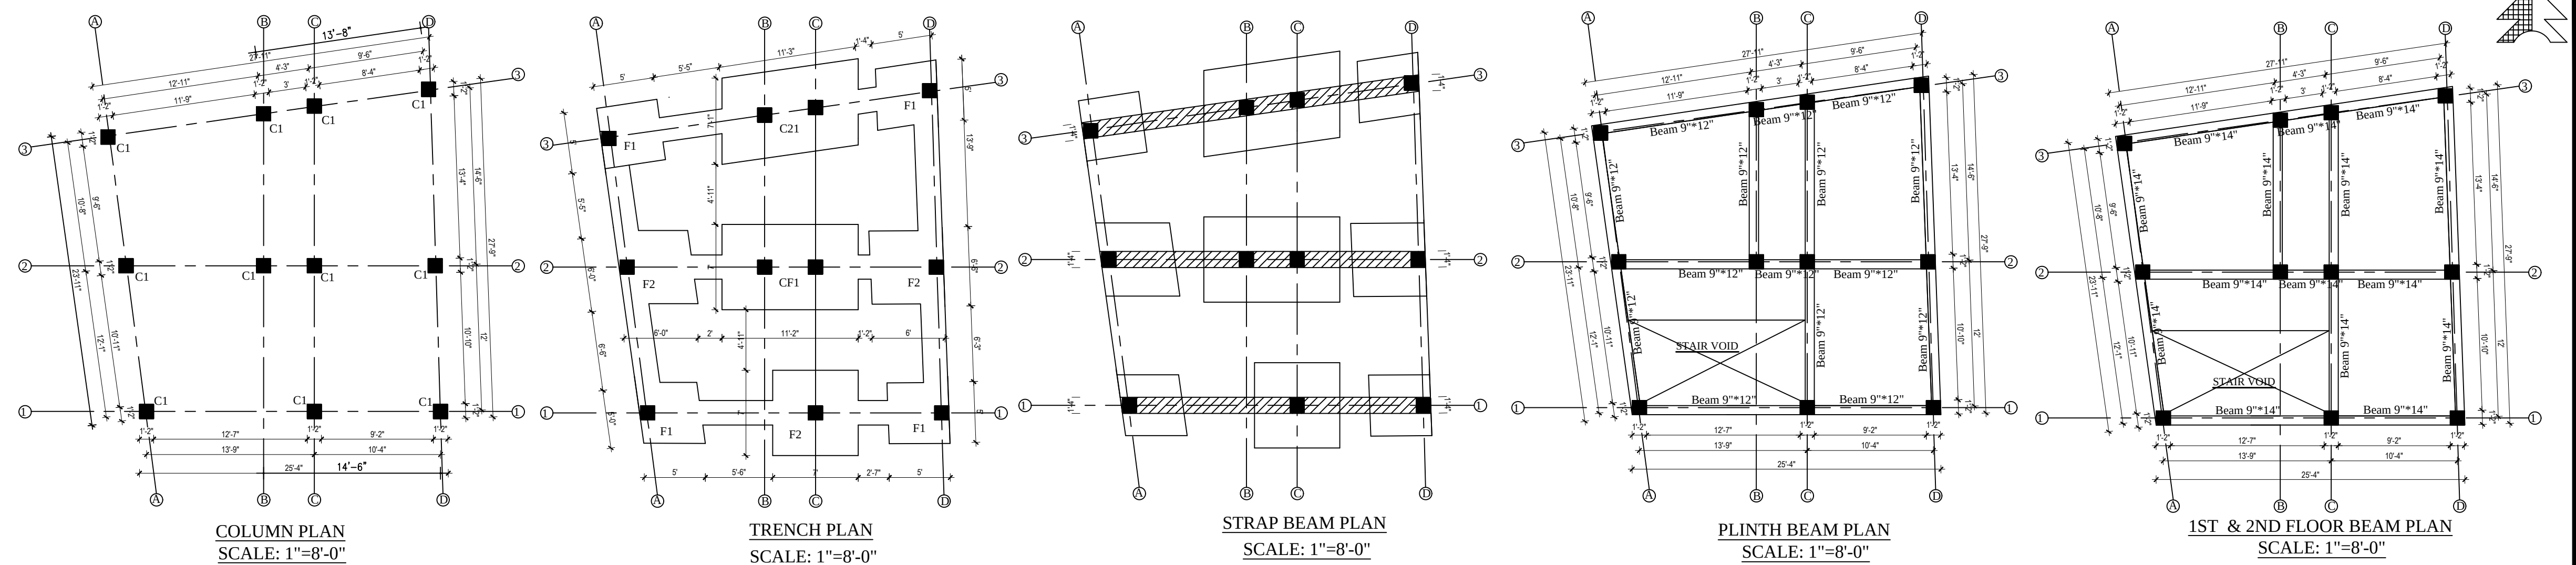

GRADE=Fe 500

|                  | B2, B3, C2 & C3                     | A1, A2, A3,<br>C1, D1, D2 & D3      |
|------------------|-------------------------------------|-------------------------------------|
| GR FLOOR COLUMN  | <br>4-20mm + 4-16mm<br>SCALE: 1"=2' | <br>8-16mm<br>SCALE: 1"=2'          |
| 1st FLOOR COLUMN | <br>8-16mm<br>SCALE: 1"=2'          | <br>8-16mm<br>SCALE: 1"=2'          |
| 2nd FLOOR COLUMN | <br>4-16mm + 4-12mm<br>SCALE: 1"=2' | <br>4-16mm + 4-12mm<br>SCALE: 1"=2' |

COLUMN DETAILS  
SCALE: 12"=1'-0"

| Floor                  | Grid                                       | Size   | Section at N-N | Section at M-M |
|------------------------|--------------------------------------------|--------|----------------|----------------|
| PLINTH & BASE TIE BEAM | A-A / B-B<br>C-C / D-D<br>1-1 / 2-2<br>3-3 | 9"x12" | <br>3-100 Th   | <br>3-100 Th   |
| FIRST FLOOR            | A-A / B-B<br>C-C / D-D<br>1-1 / 2-2<br>3-3 | 9"x14" | <br>3-100 Th   | <br>3-100 Th   |
| SECOND FLOOR           | A-A / B-B<br>C-C / D-D<br>1-1 / 2-2<br>3-3 | 9"x14" | <br>3-100 Th   | <br>3-100 Th   |

BEAM DETAILS  
SCALE: 12"=1'-0"

