
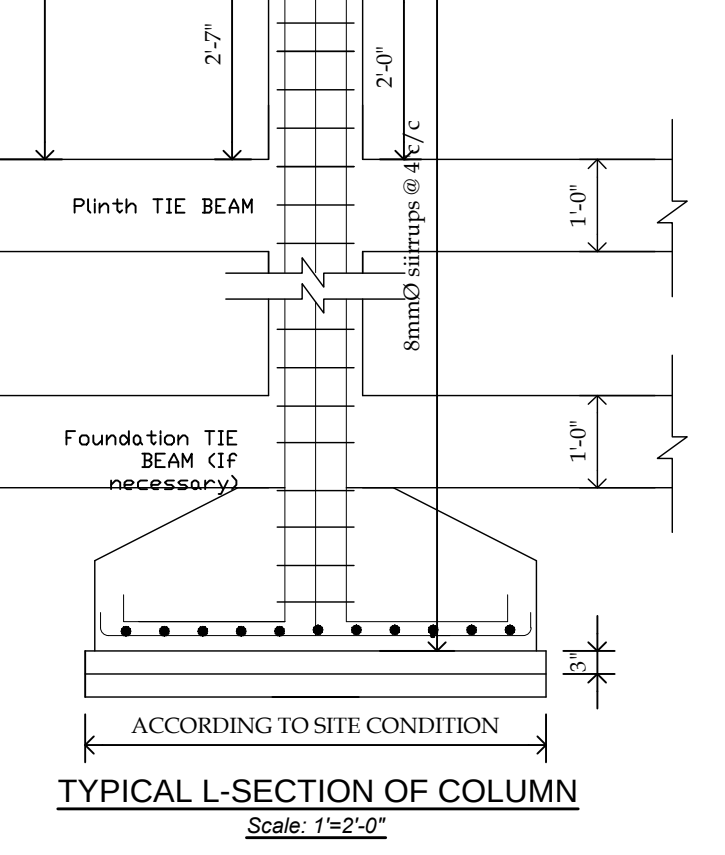
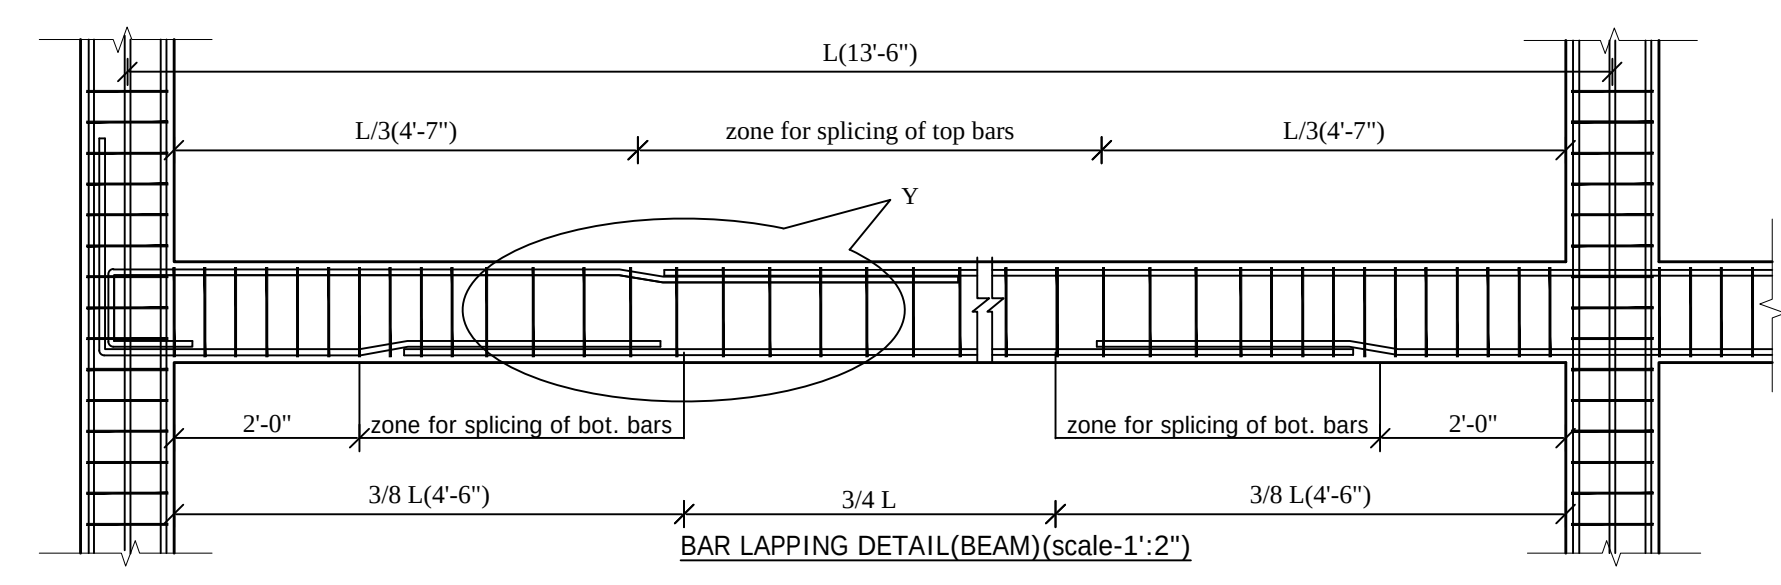
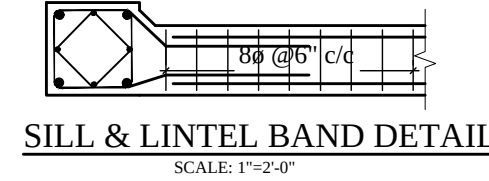
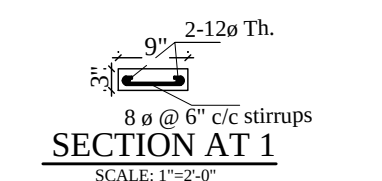
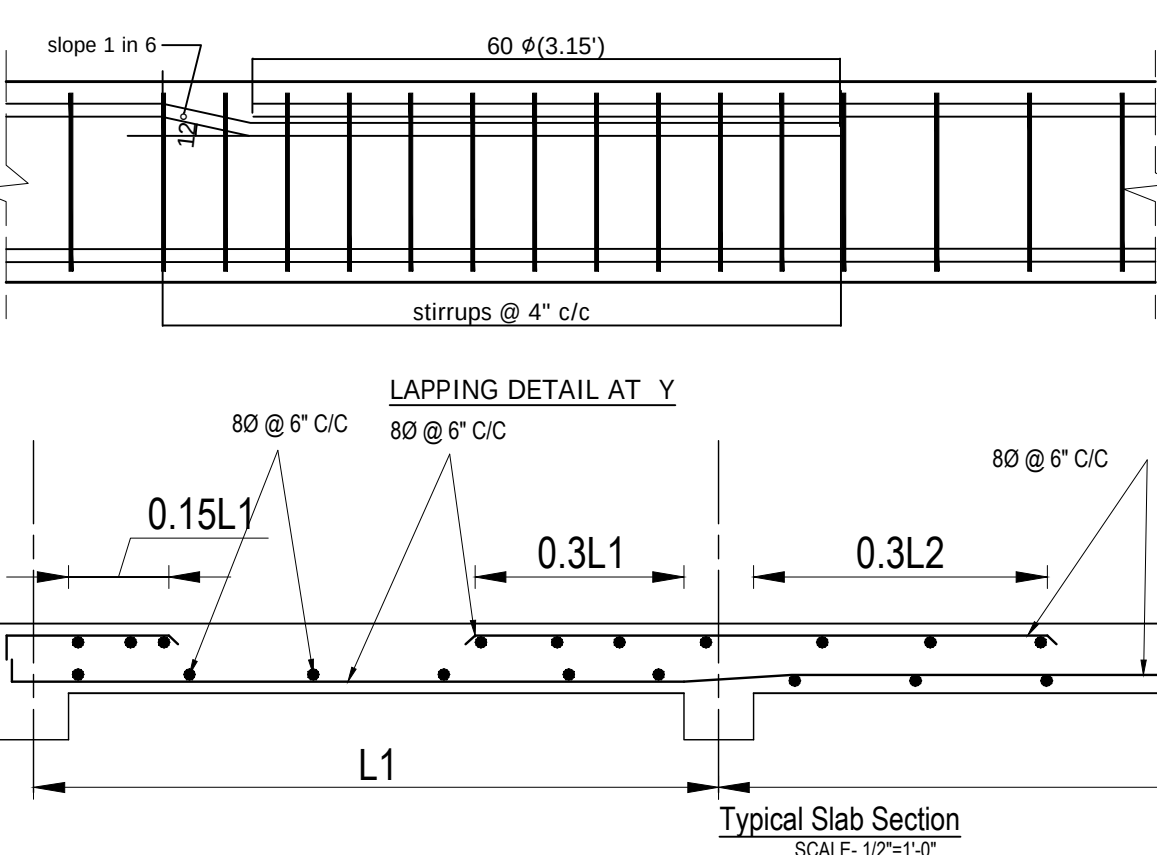
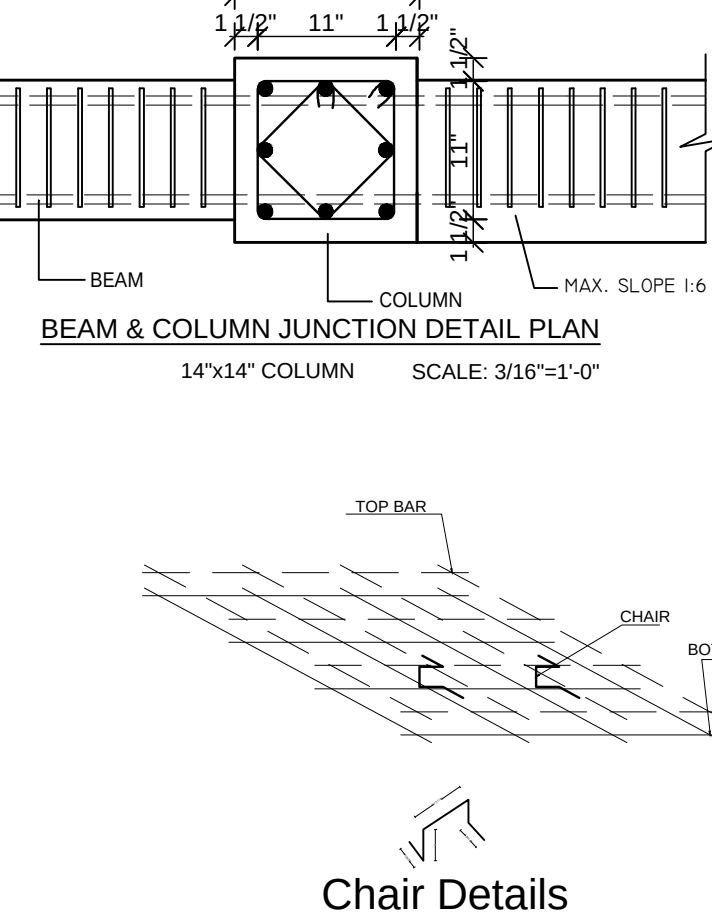
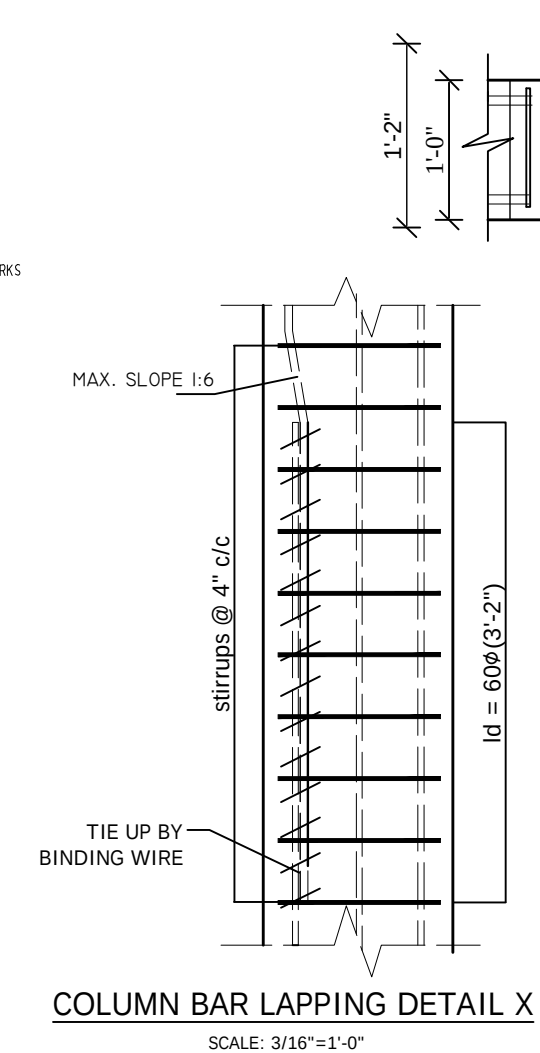
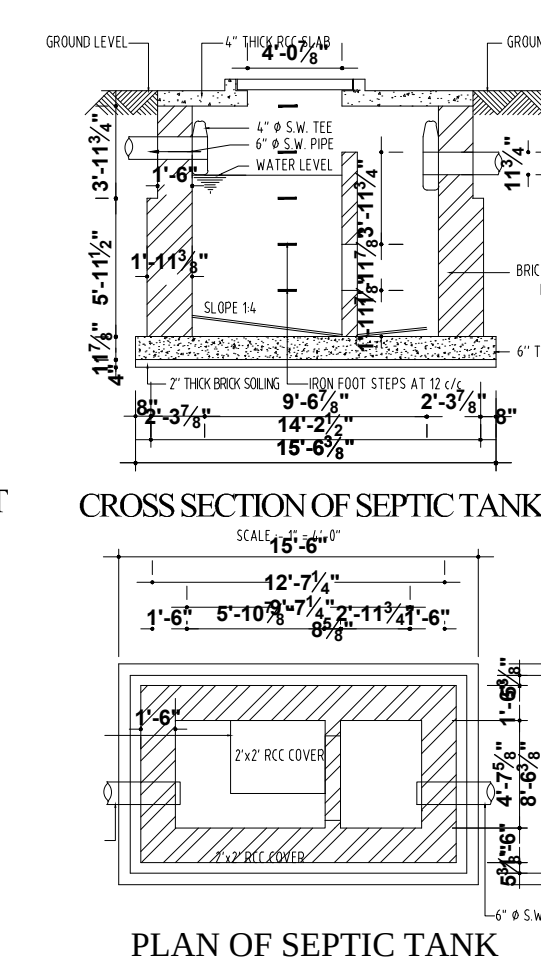
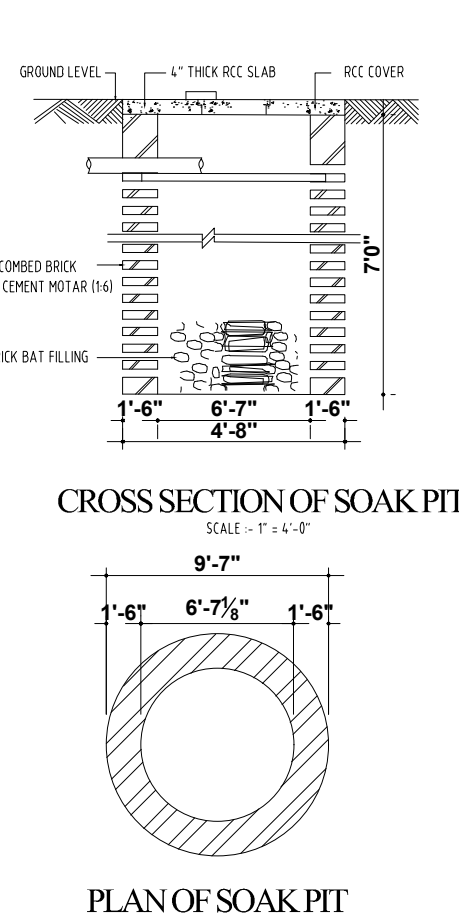
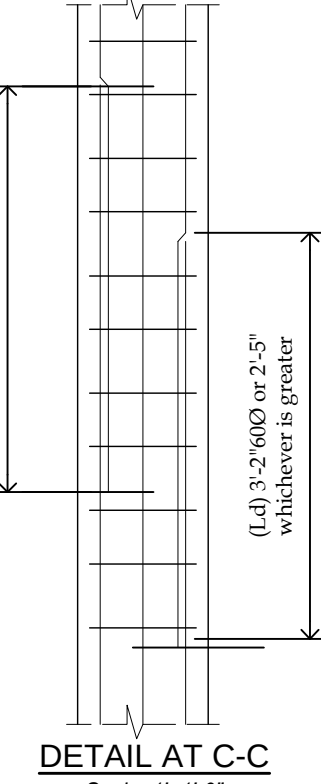
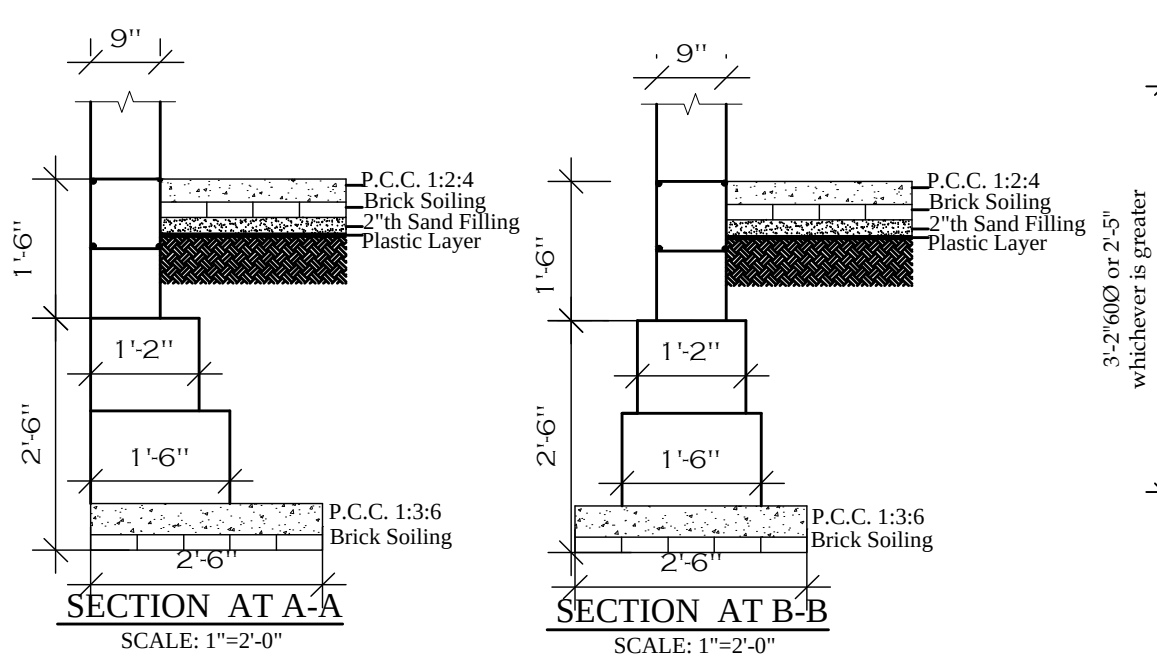
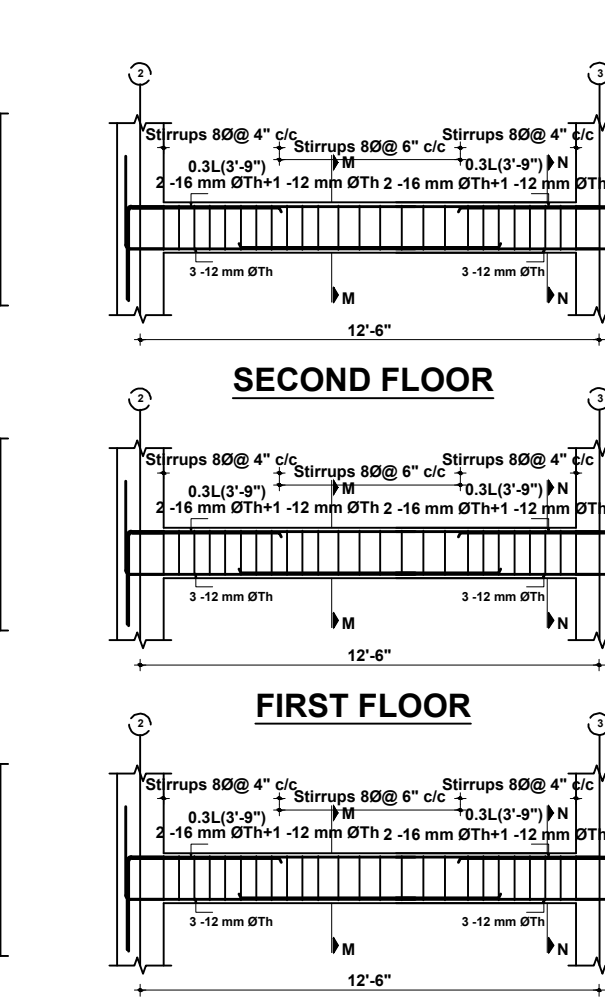
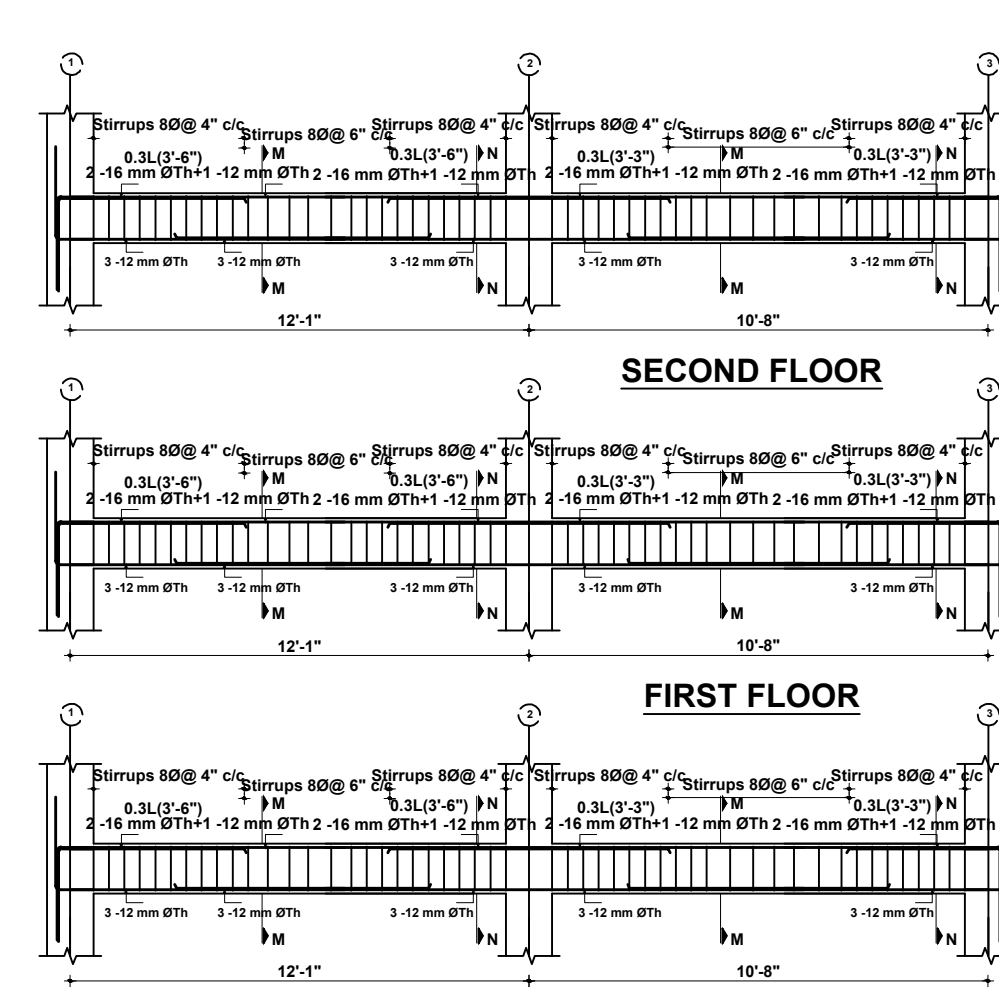
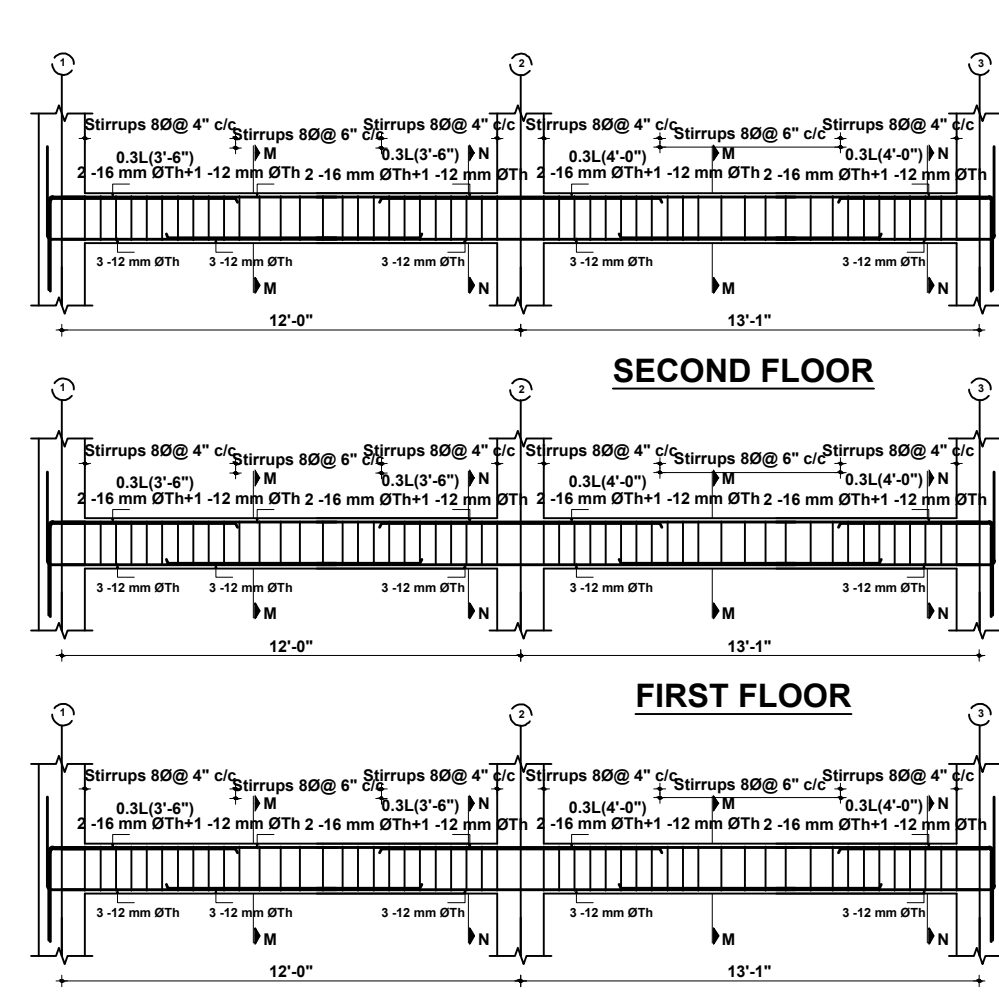
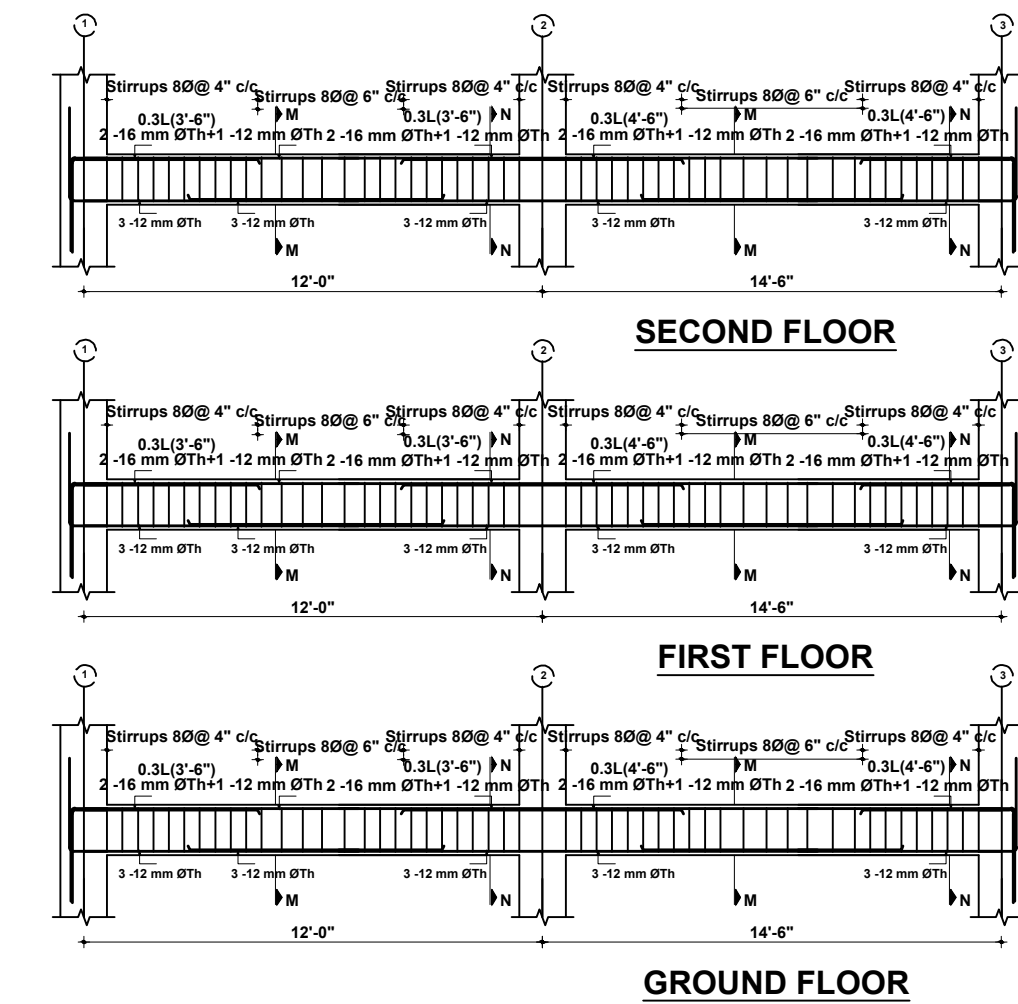
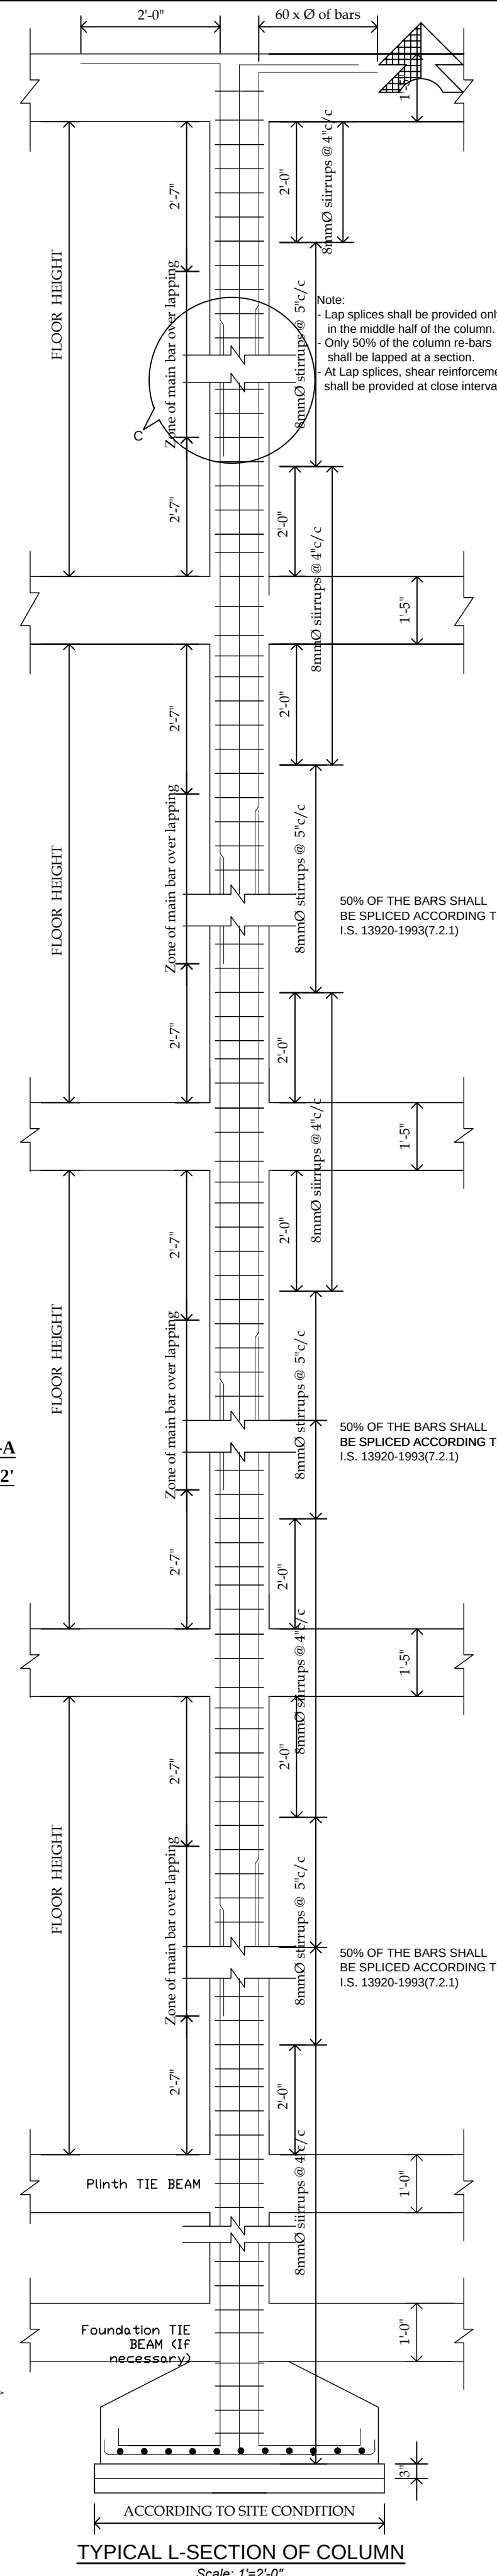
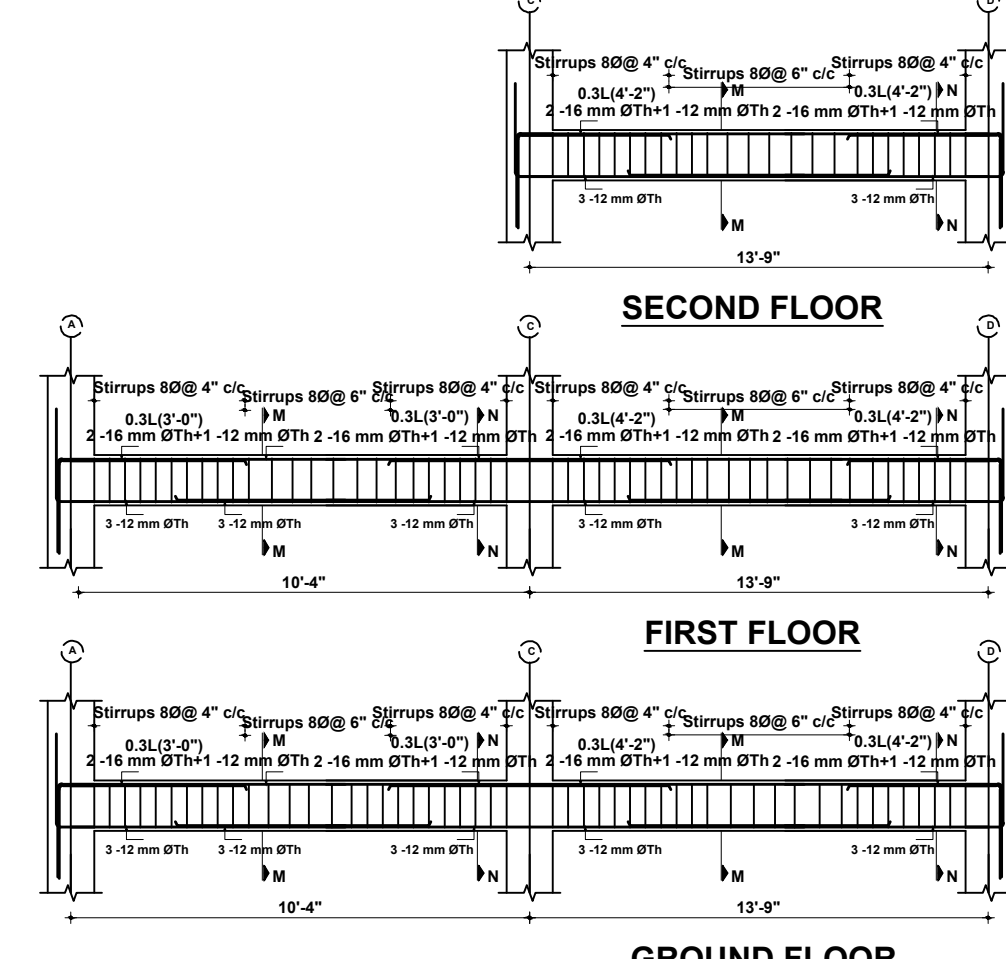
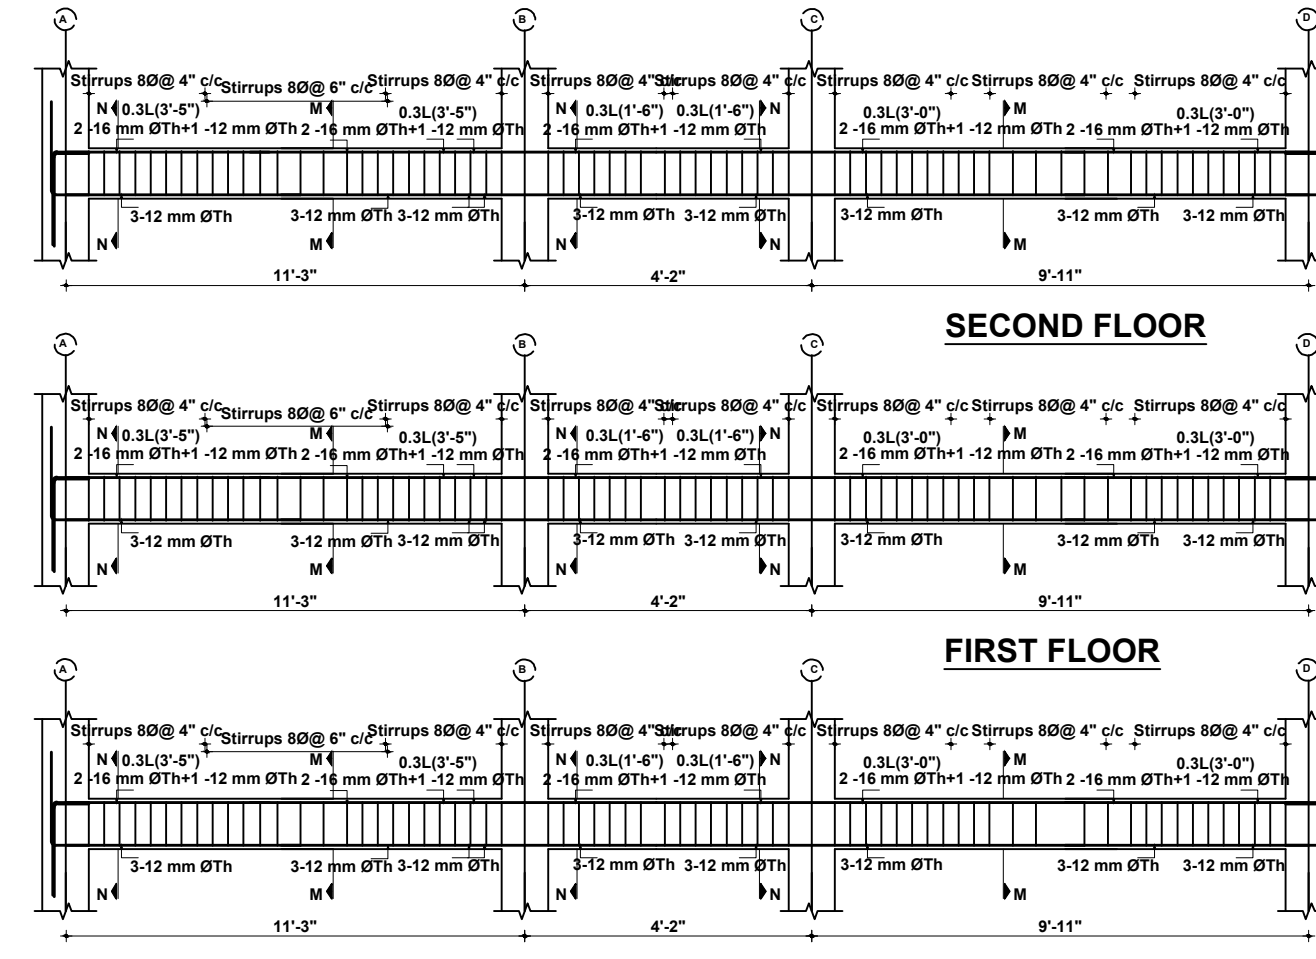


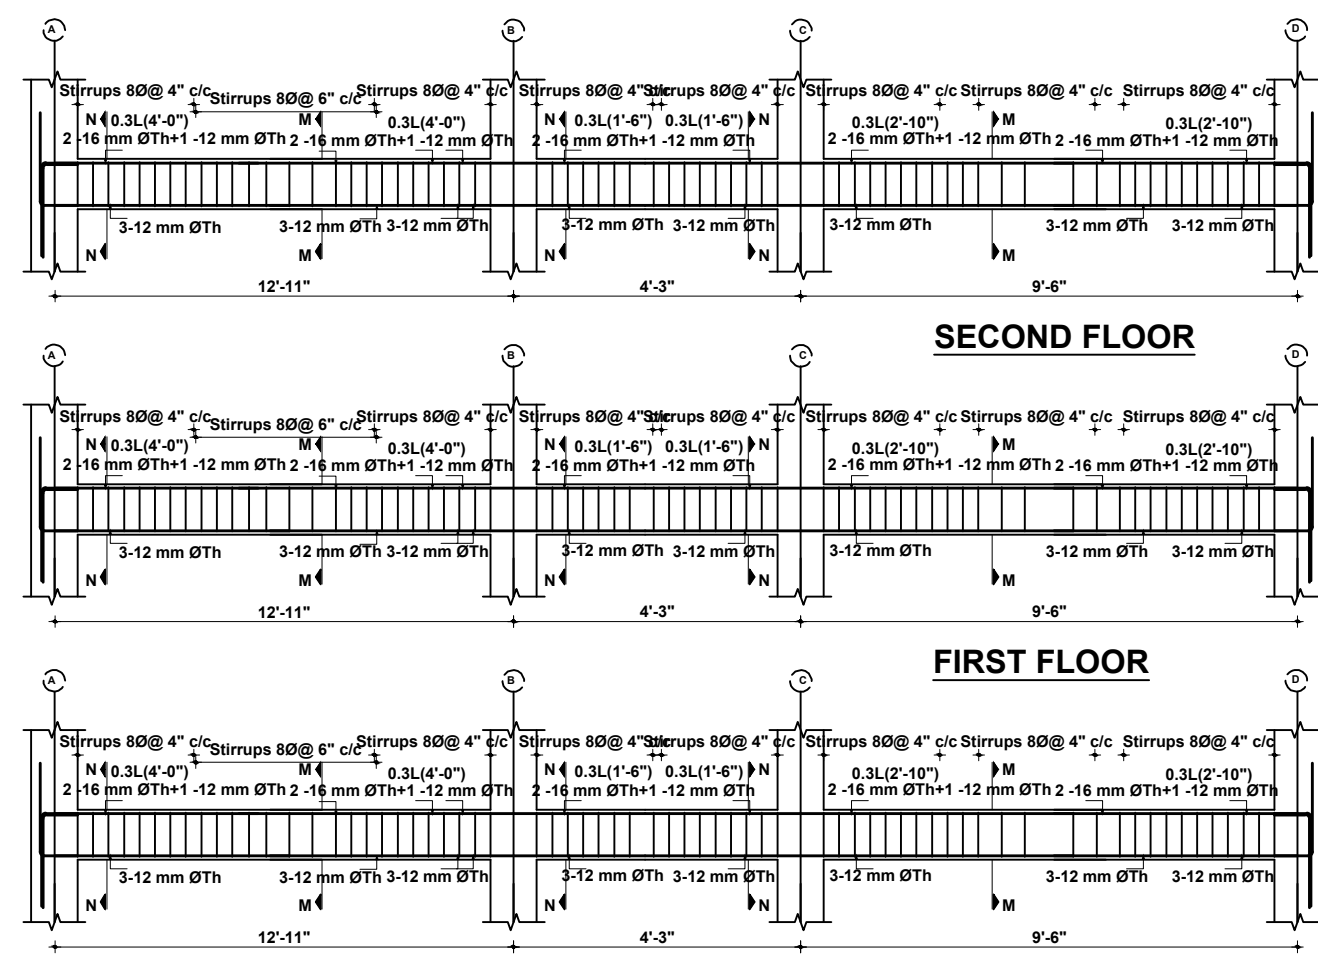

50% OF THE BARS SHALL BE SPICED ACCORDING TO I.S. 13920-1993(7.2.1)

50% OF THE BARS SHALL BE SPICED ACCORDING TO I.S. 13920-1993(7.2.1)

50% OF THE BARS SHALL BE SPICED ACCORDING TO I.S. 13920-1993(7.2.1)