
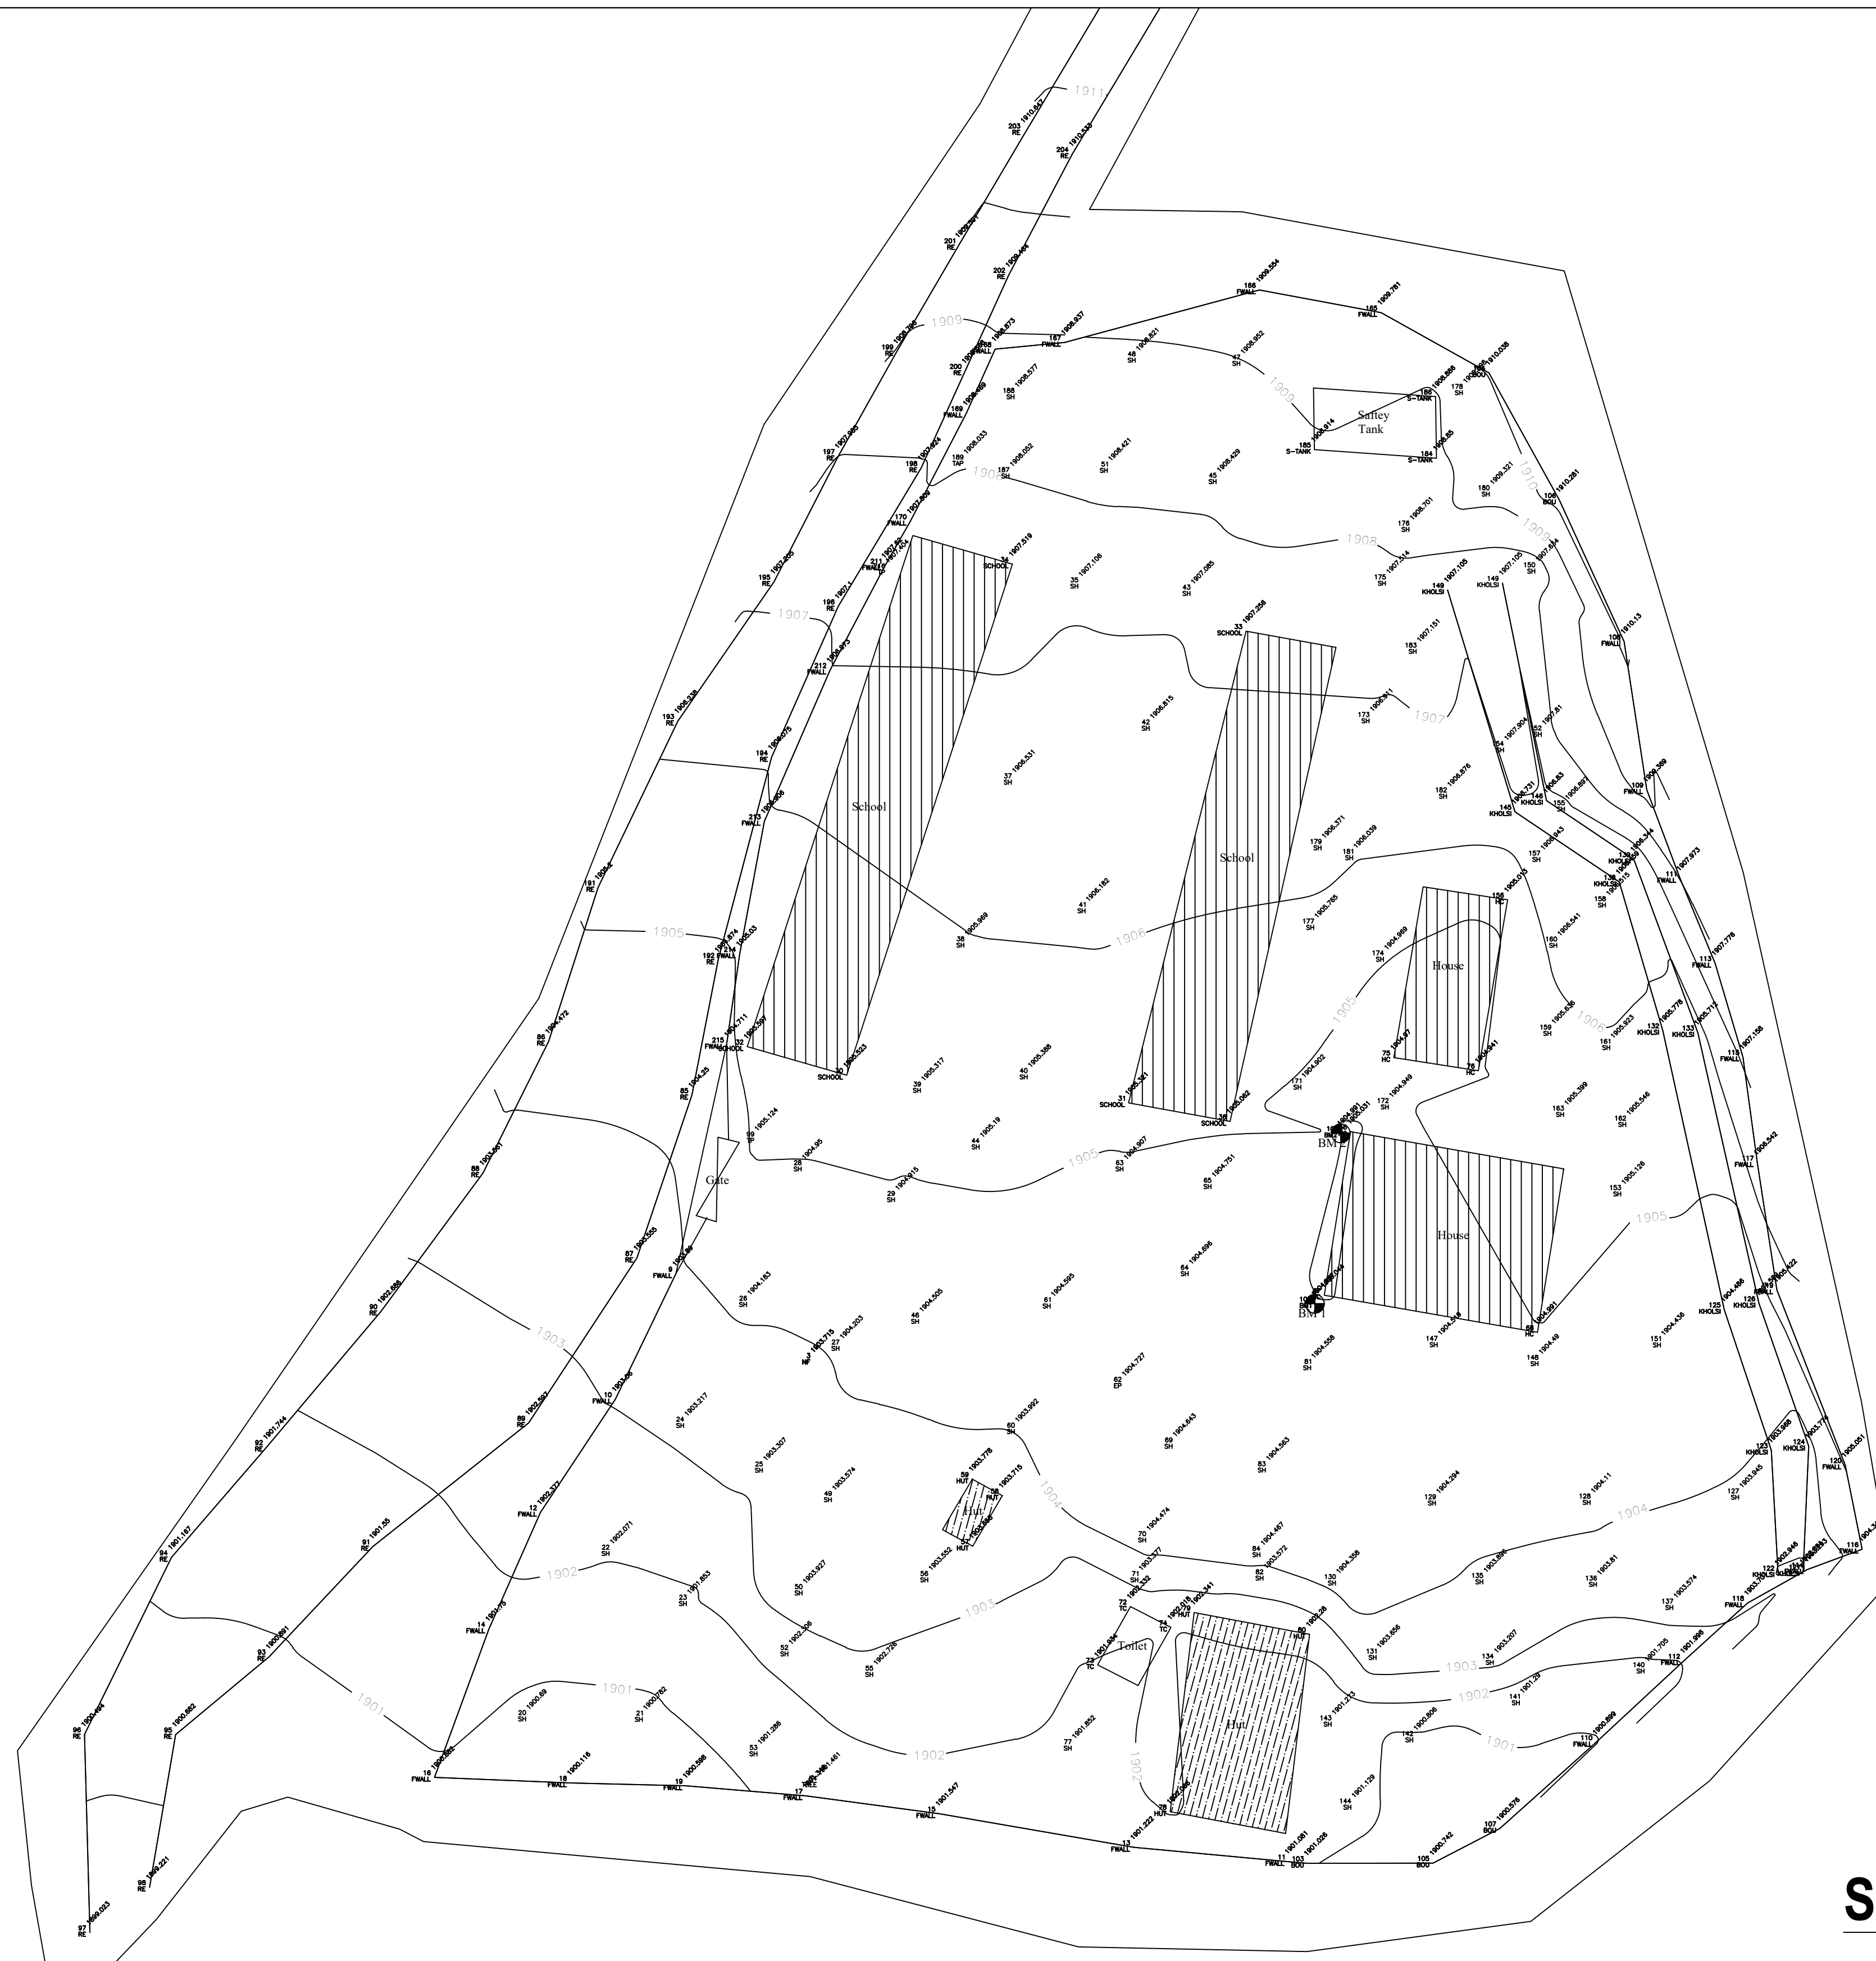
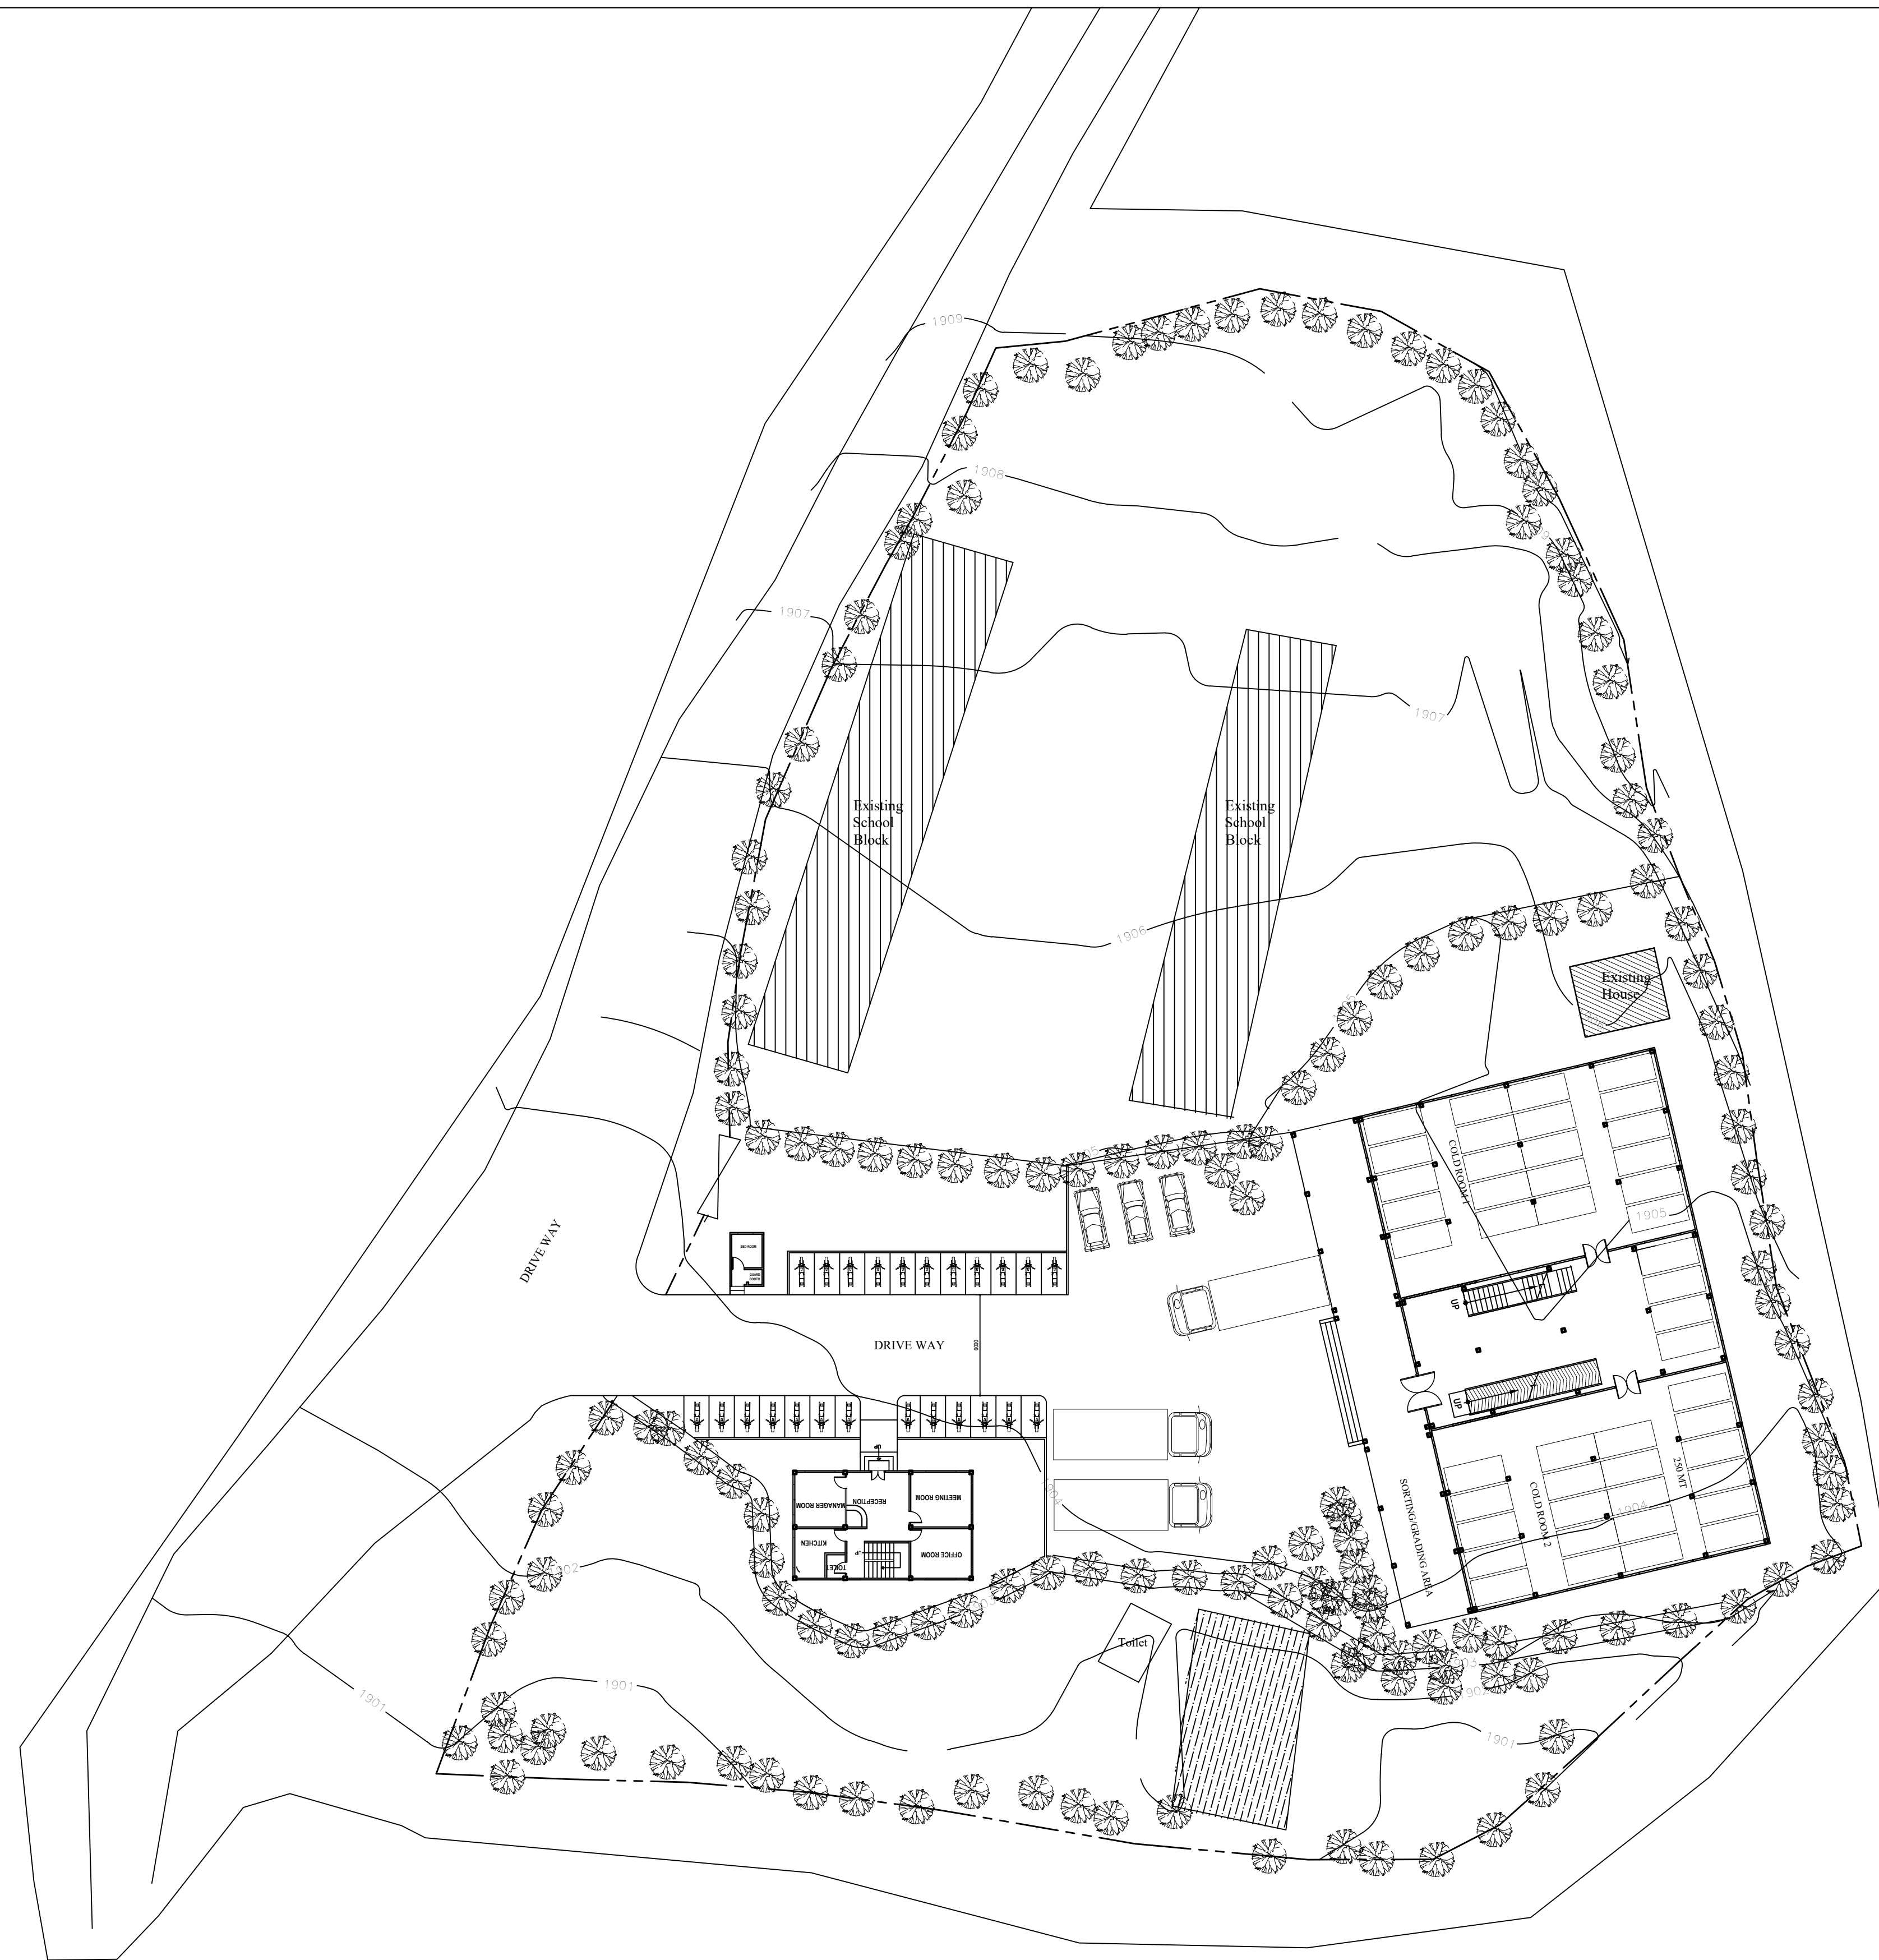


SURVEY MAP



<u>LEGEND</u>	<u>SYMBOL</u>
Road	
Bench Mark	
Tahara	
Property Boundary	
Extened Boundary	
Gate	
Saftey Tank	
Tahara	
EP/TP	

PROJECT: DPR OF 500MT COLD STORE AT JIRI, DOLAKHA		SURVEY MAP		CHECKED BY: APPROVED BY :		CONSULTANT: Sworaj Consultants Pvt. Ltd. Samkhushi, Kathmandu		Sheet No AR 01	
CLIENT: Government of Province Ministry of Land Management, Agriculture and Cooperative Province No. 3, Hetauda		FINAL DRAWING		SCALE : DATE: REVISION:					

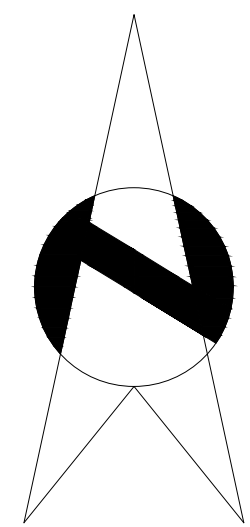


MASTER PLAN

PROJECT: DPR OF 500MT COLD STORE AT JIRI, DOLAKHA		SURVEY MAP		CHECKED BY:		CONSULTANT: Sworaj Consultants Pvt. Ltd. Samkhushi, Kathmandu		Sheet No	
CLIENT: Government of Province Ministry of Land Management, Agriculture and Cooperative Province No. 3, Hetauda		FINAL DRAWING		APPROVED BY :				AR 02	
				SCALE :					
				DATE:	REVISION:				

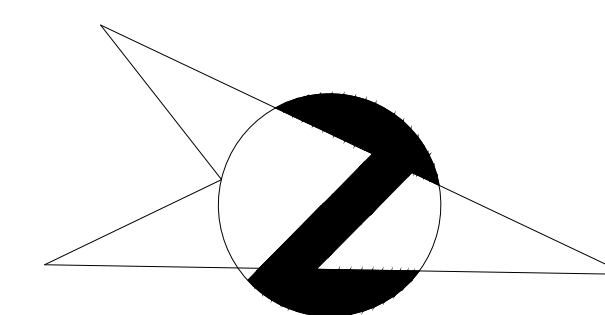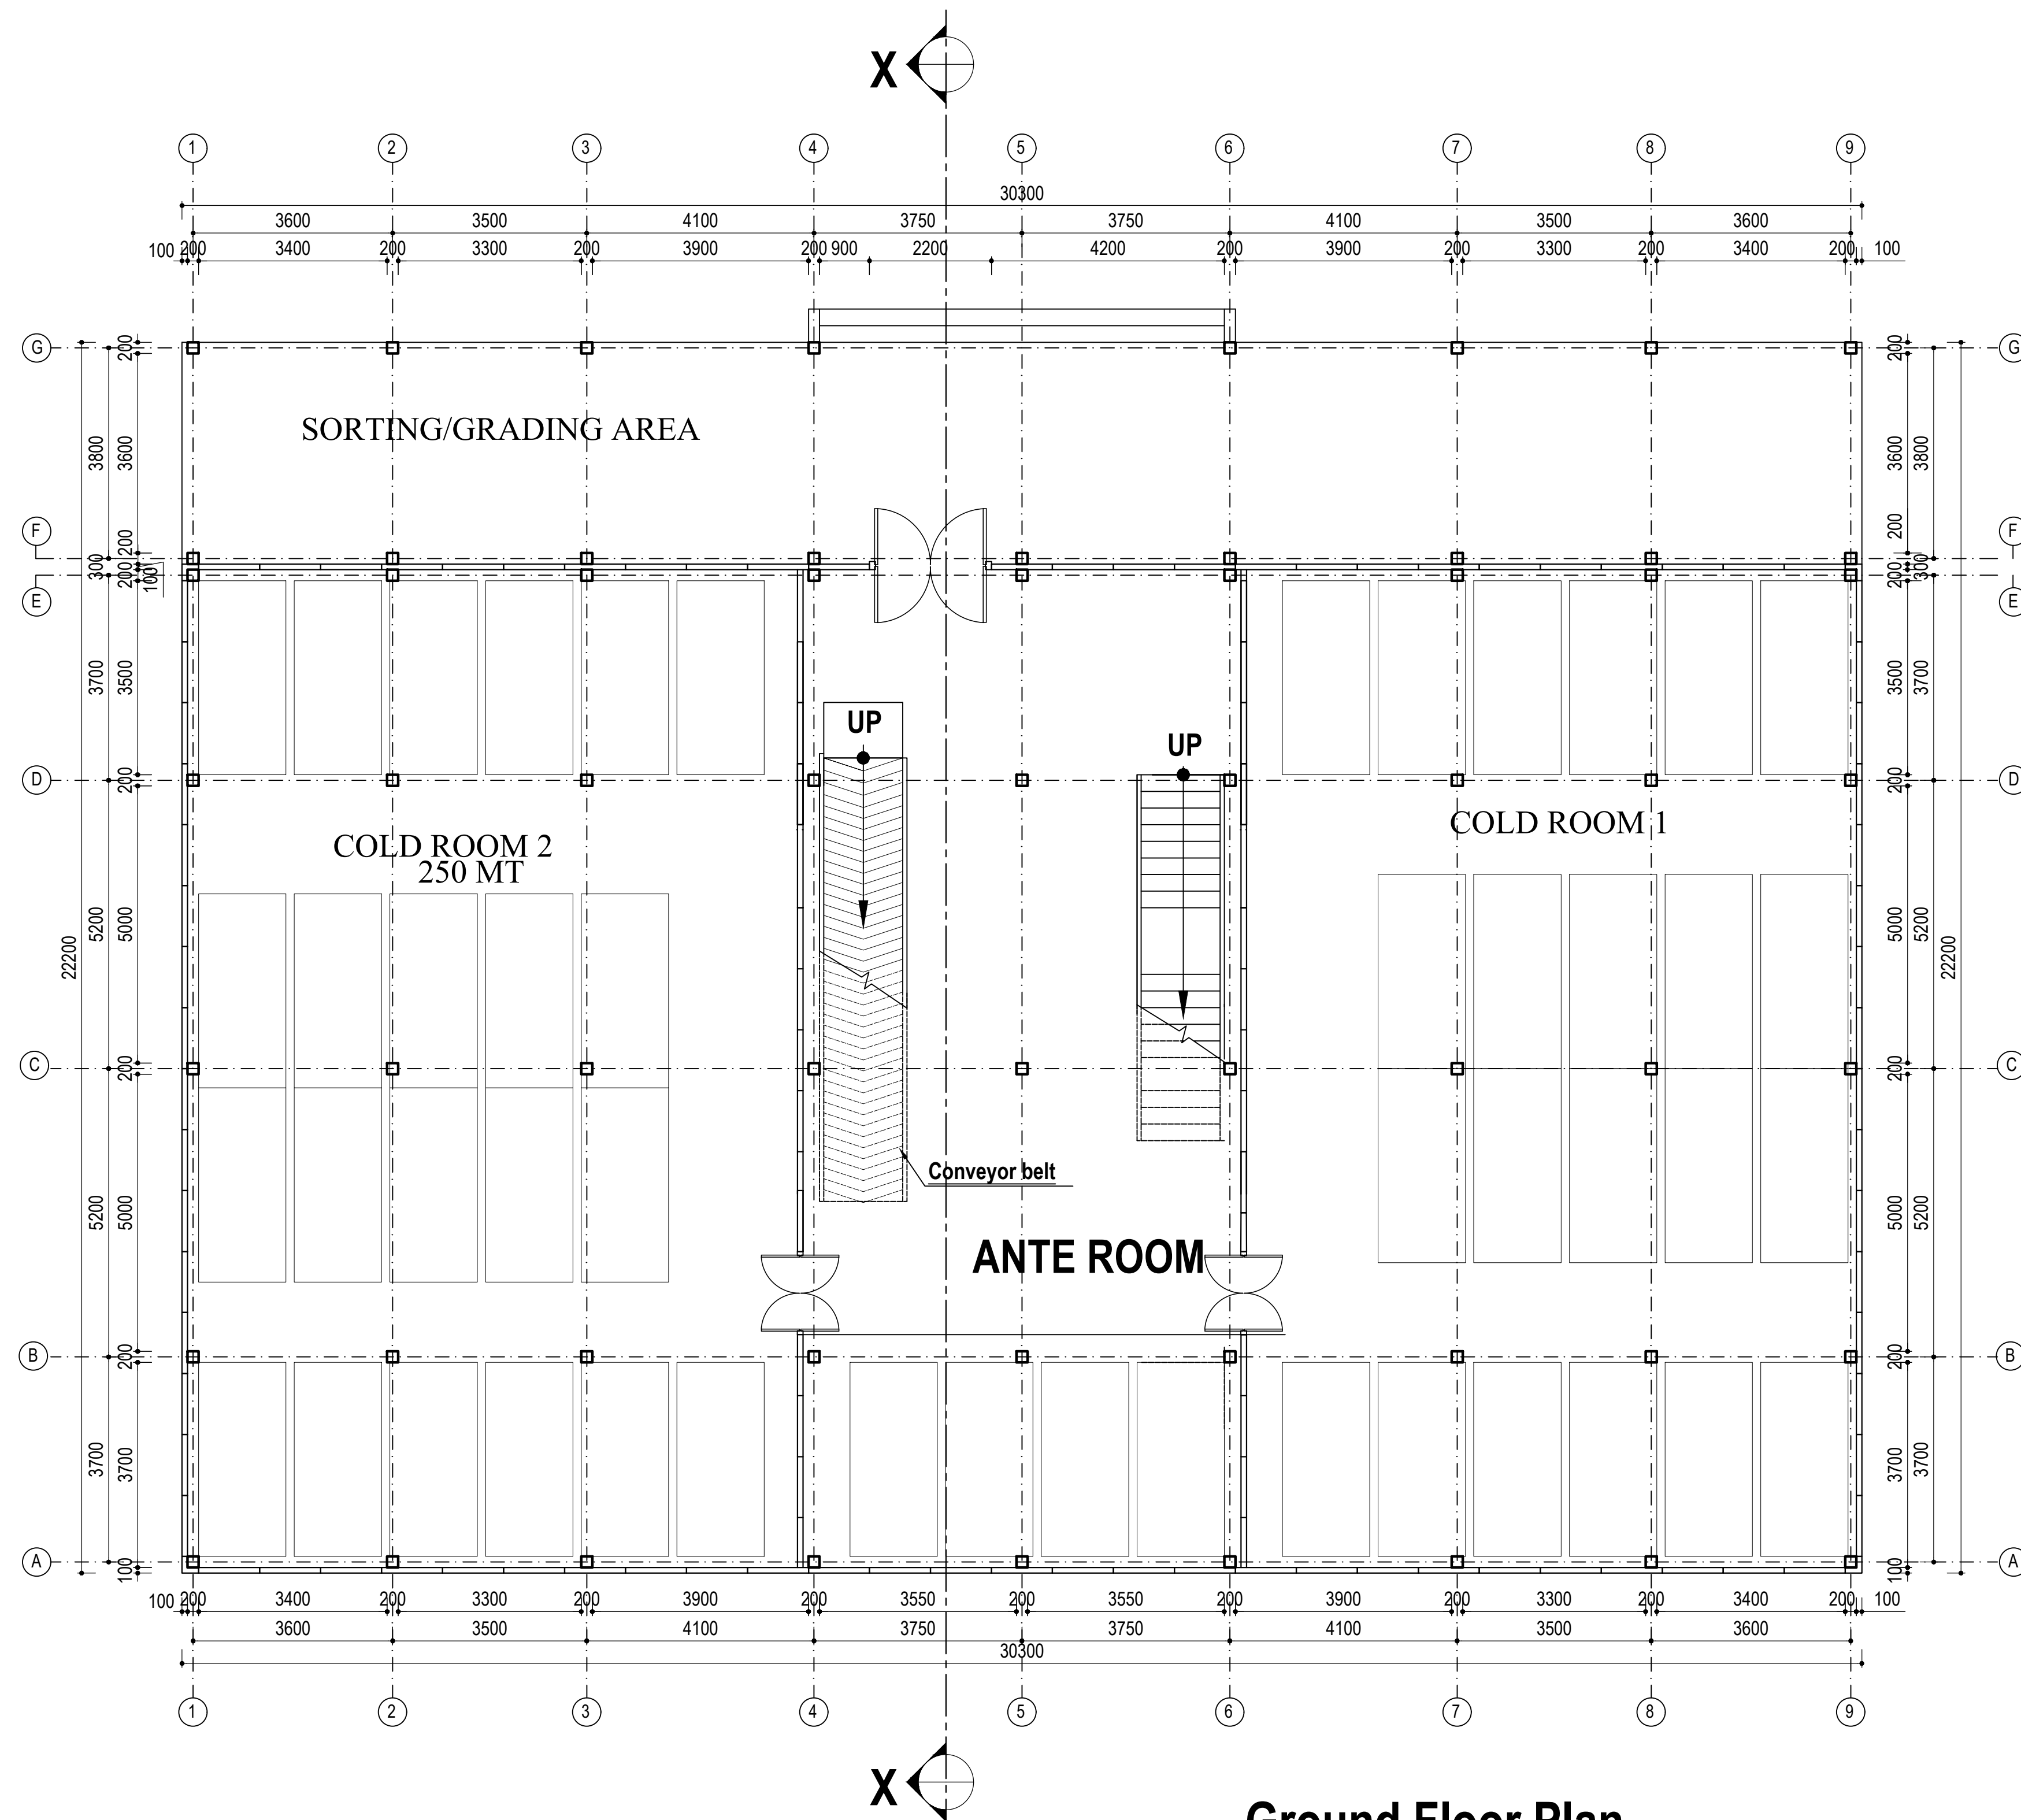



Ground Floor Plan
Floor Area:672.660 sq.m

PROJECT: DPR OF 500MT COLD STORE AT JIRI, DOLAKHA		CONTENT: FLOOR PLAN	ARCHITECT :	CHECKED BY:	CONSULTANT: Sworaj Consultants Pvt. Ltd. Samkhushi, Kathmandu	Sheet No AR 03
CLIENT: Government of Province Ministry of Land Management, Agriculture and Cooperative Province No. 3, Hetauda		FINAL DRAWING	STR. ENGINEER:	APPROVED BY :		
				SCALE : 1:200		
				DATE:	REVISION:	

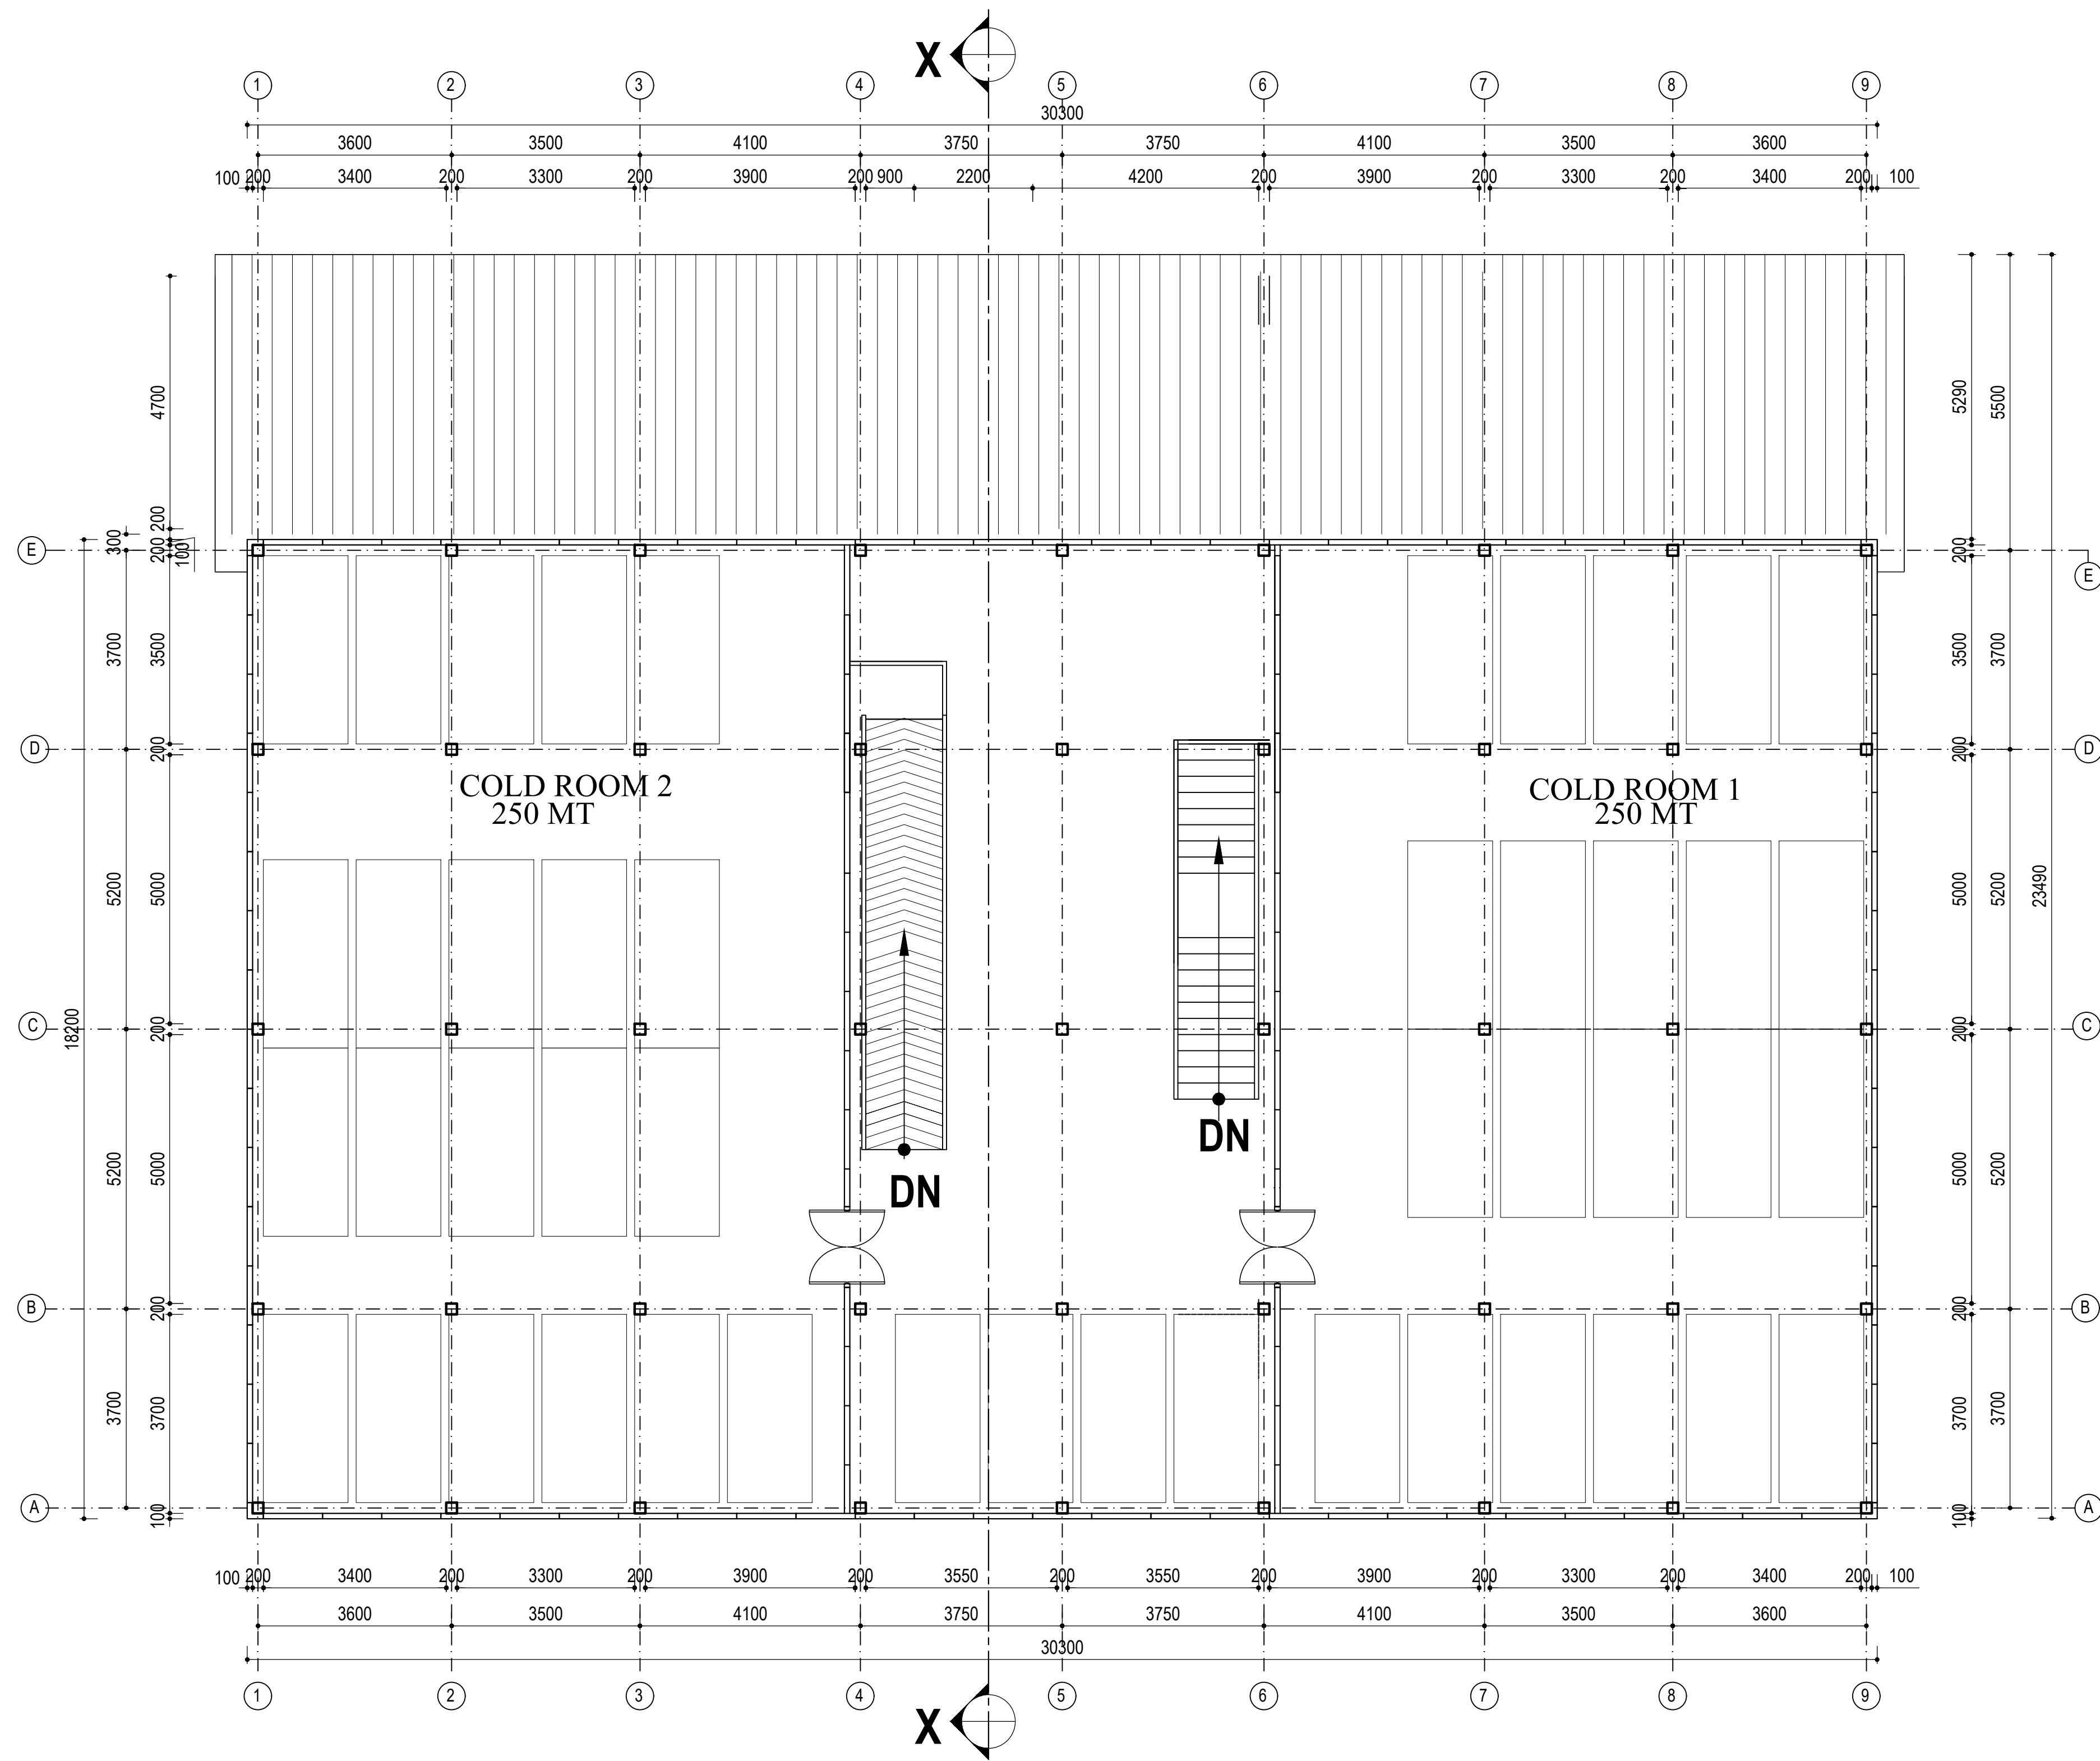


FIRST Floor Plan
Floor Area: 551.4576 sq.m

PROJECT: DPR OF 500MT COLD STORE AT JIRI, DOLAKHA		CONTENT: FLOOR PLAN	ARCHITECT :	CHECKED BY:	CONSULTANT: Sworaj Consultants Pvt. Ltd. Samkhushi, Kathmandu	Sheet No AR 04
CLIENT: Government of Province Ministry of Land Management, Agriculture and Cooperative Province No. 3, Hetauda		FINAL DRAWING	STR. ENGINEER:	APPROVED BY :		
				SCALE : 1:200 DATE: REVISION:		

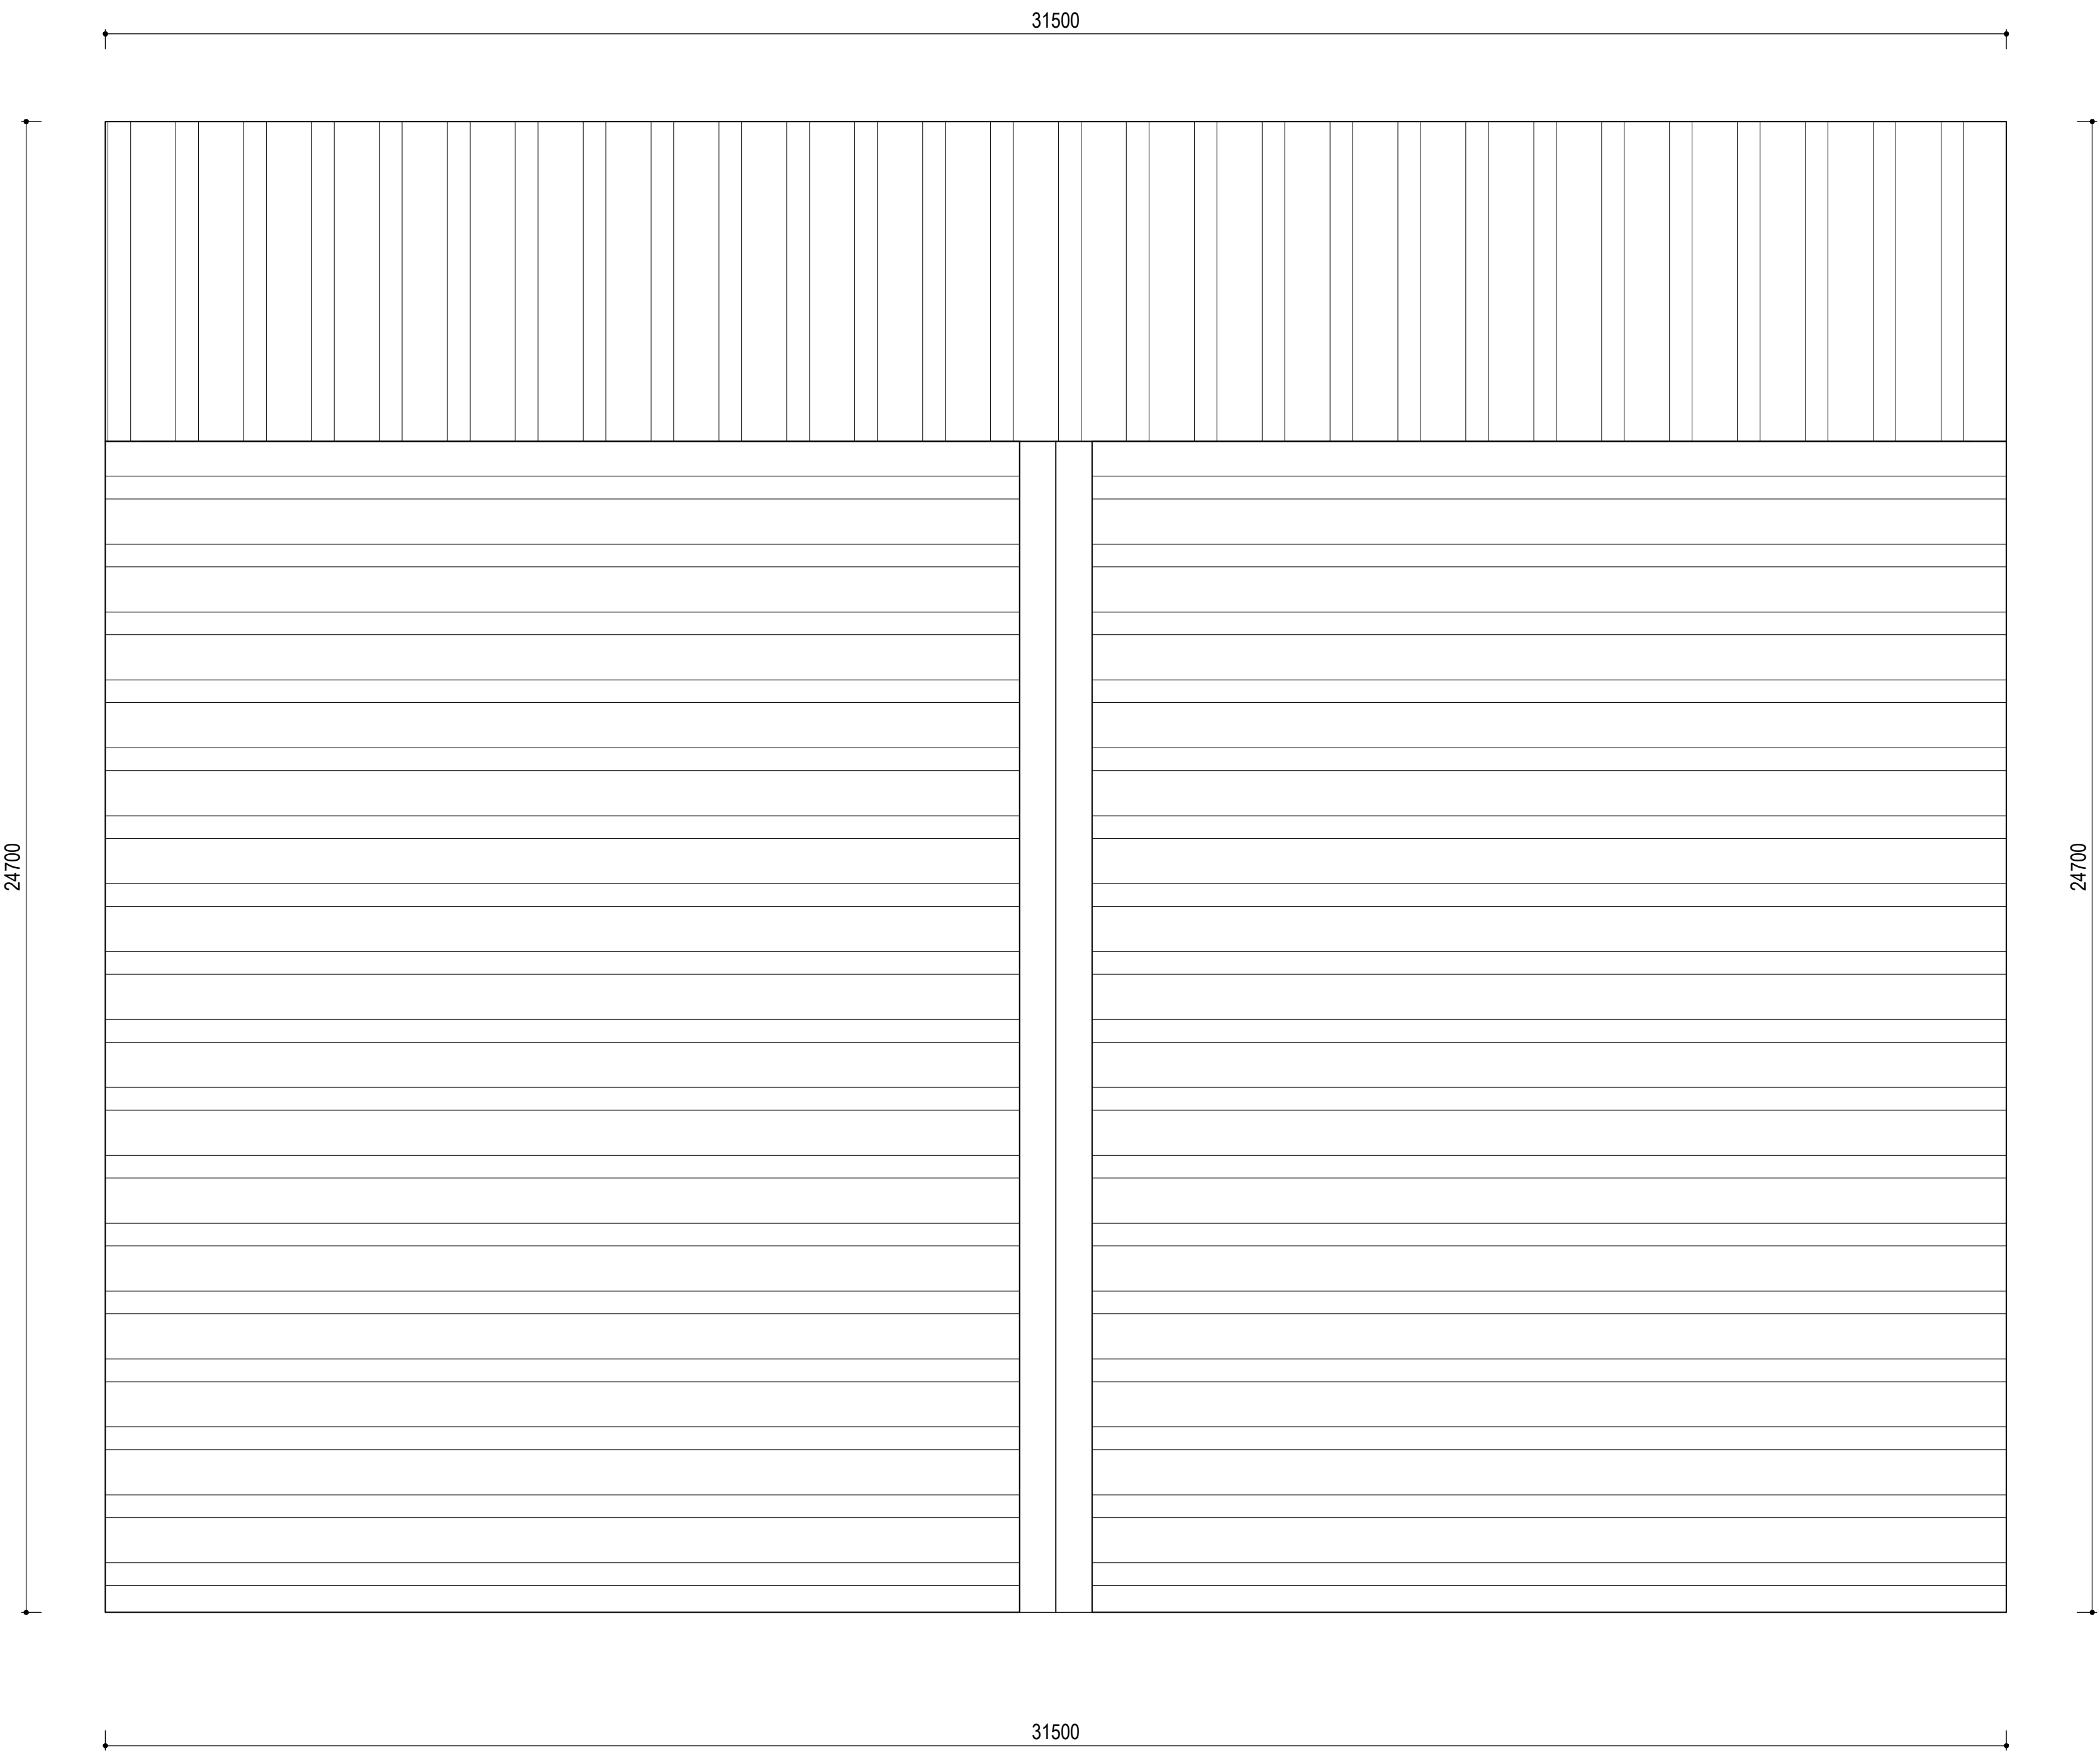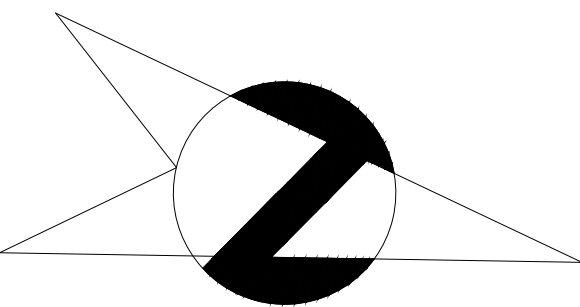


Roof Plan


PROJECT: DPR OF 500MT COLD STORE AT JIRI, DOLAKHA	CONTENT: FLOOR PLAN	ARCHITECT :	CHECKED BY: APPROVED BY :	CONSULTANT: Sworaj Consultants Pvt. Ltd. Samkhushi, Kathmandu	Sheet No AR 05
CLIENT: Government of Province Ministry of Land Management, Agriculture and Cooperative Province No. 3, Hetauda	FINAL DRAWING	STR. ENGINEER:	SCALE : 1:200 DATE: REVISION:		

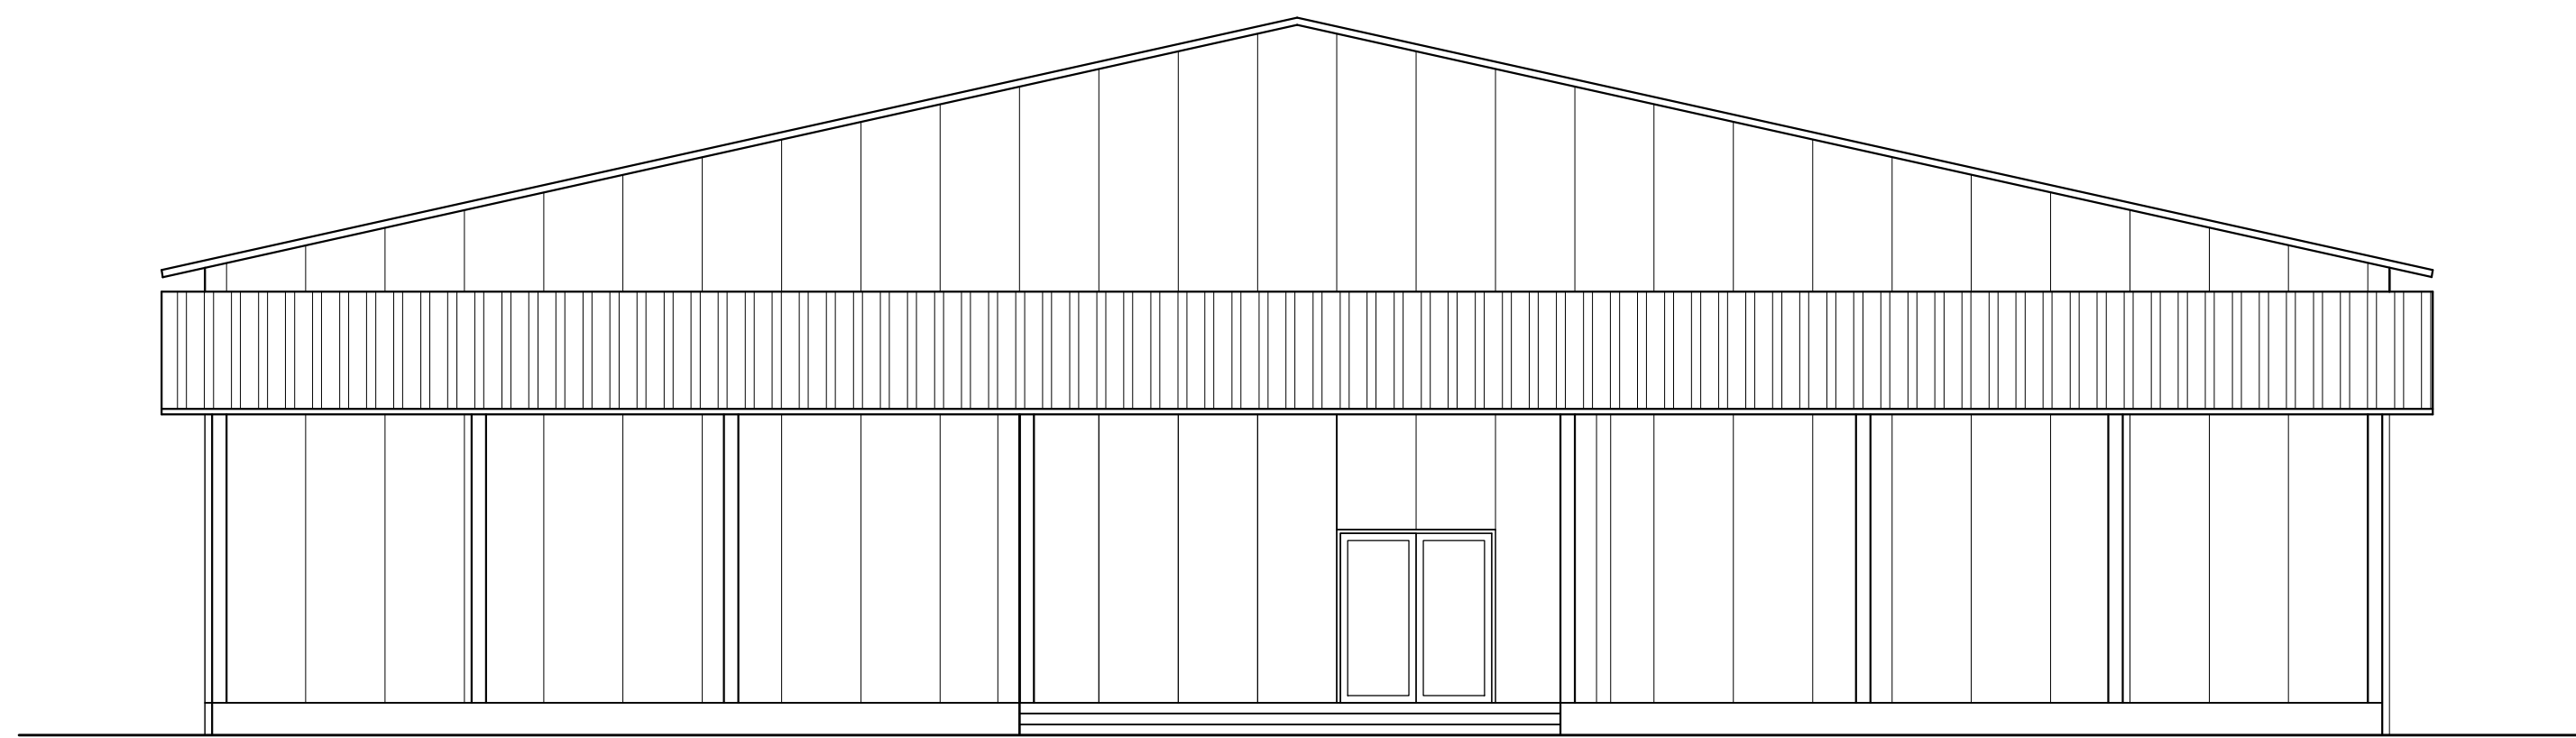


WEST ELEVATION

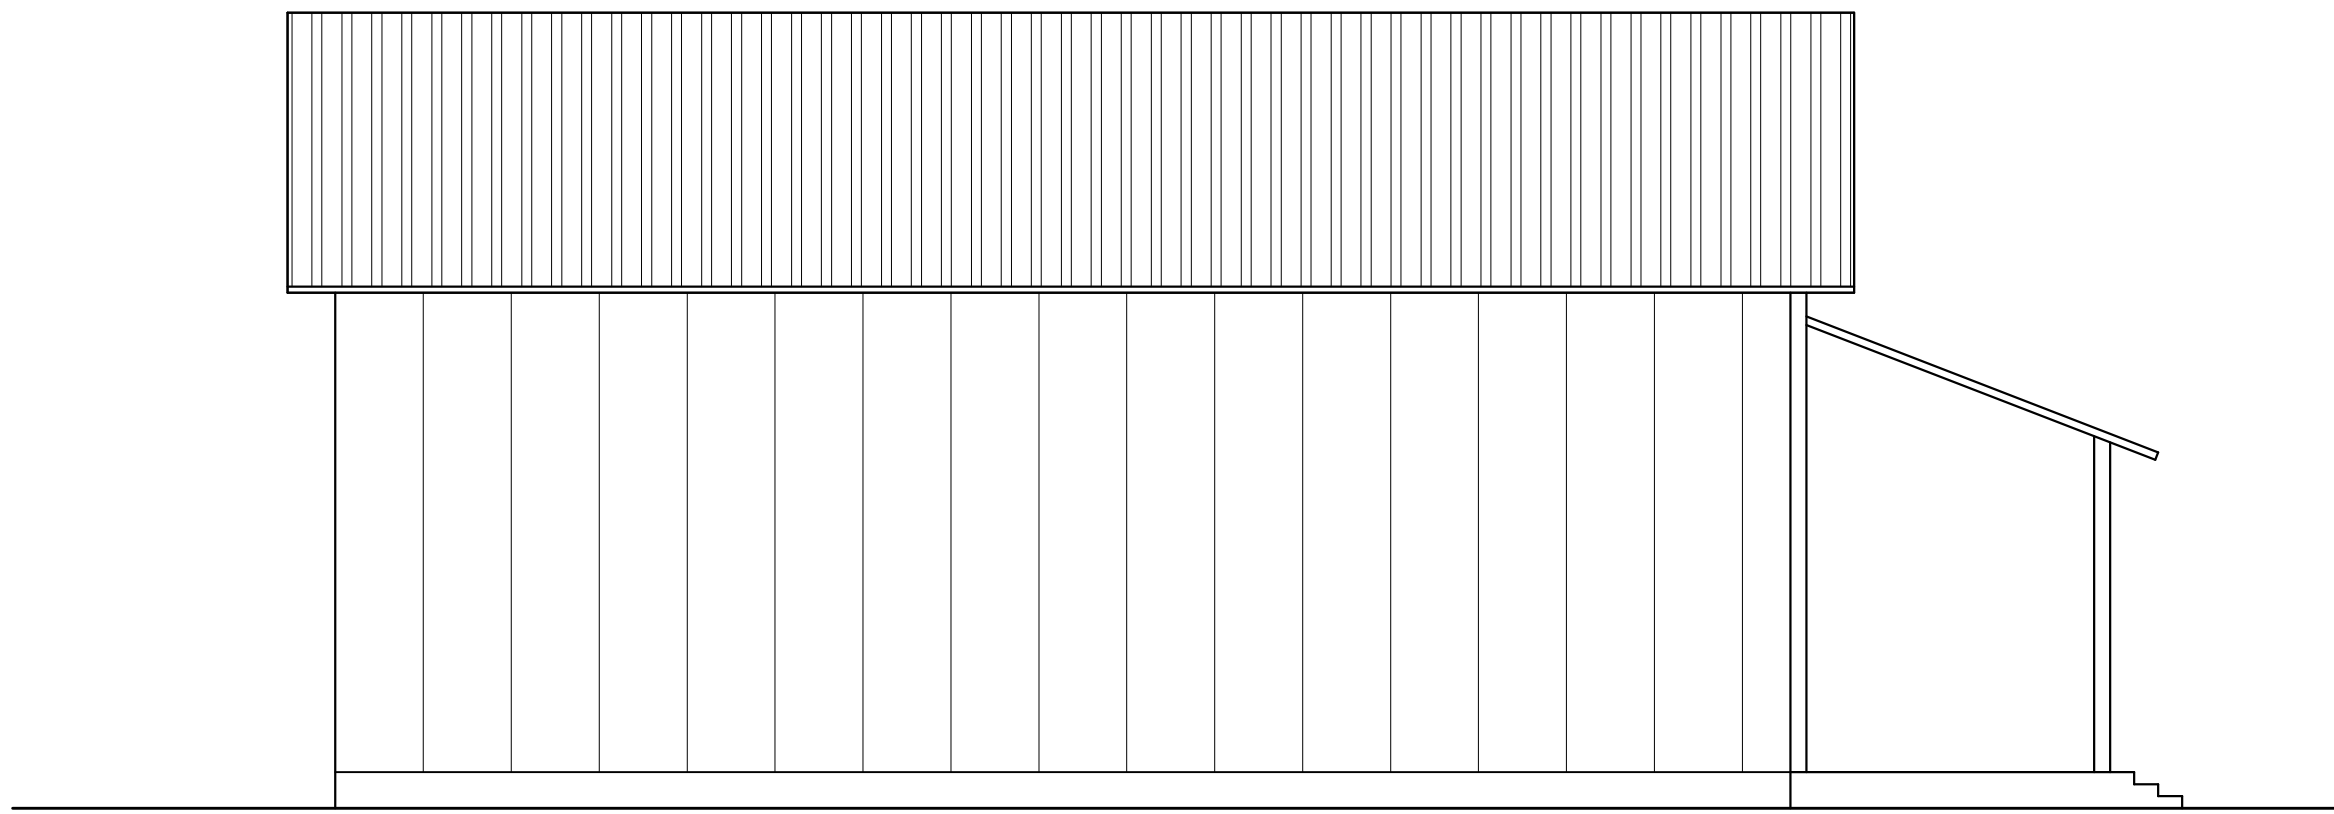


NORTH ELEVATION

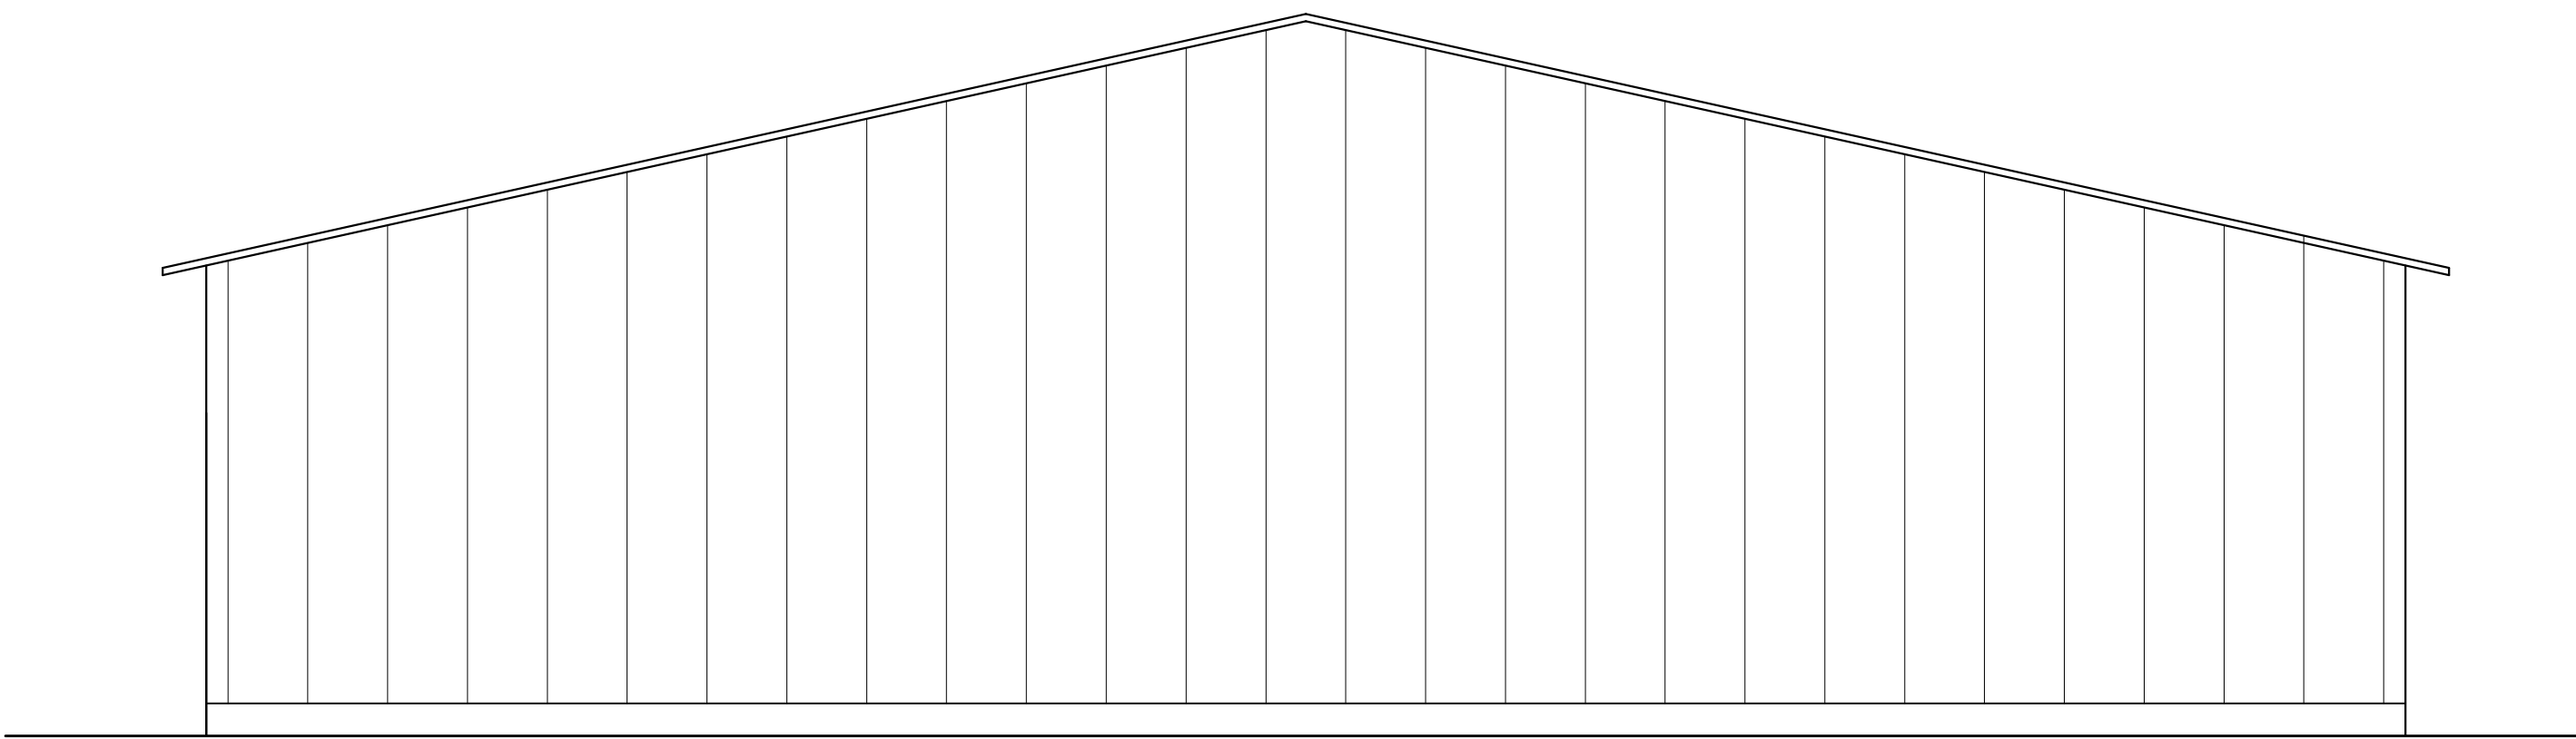

EAST ELEVATION

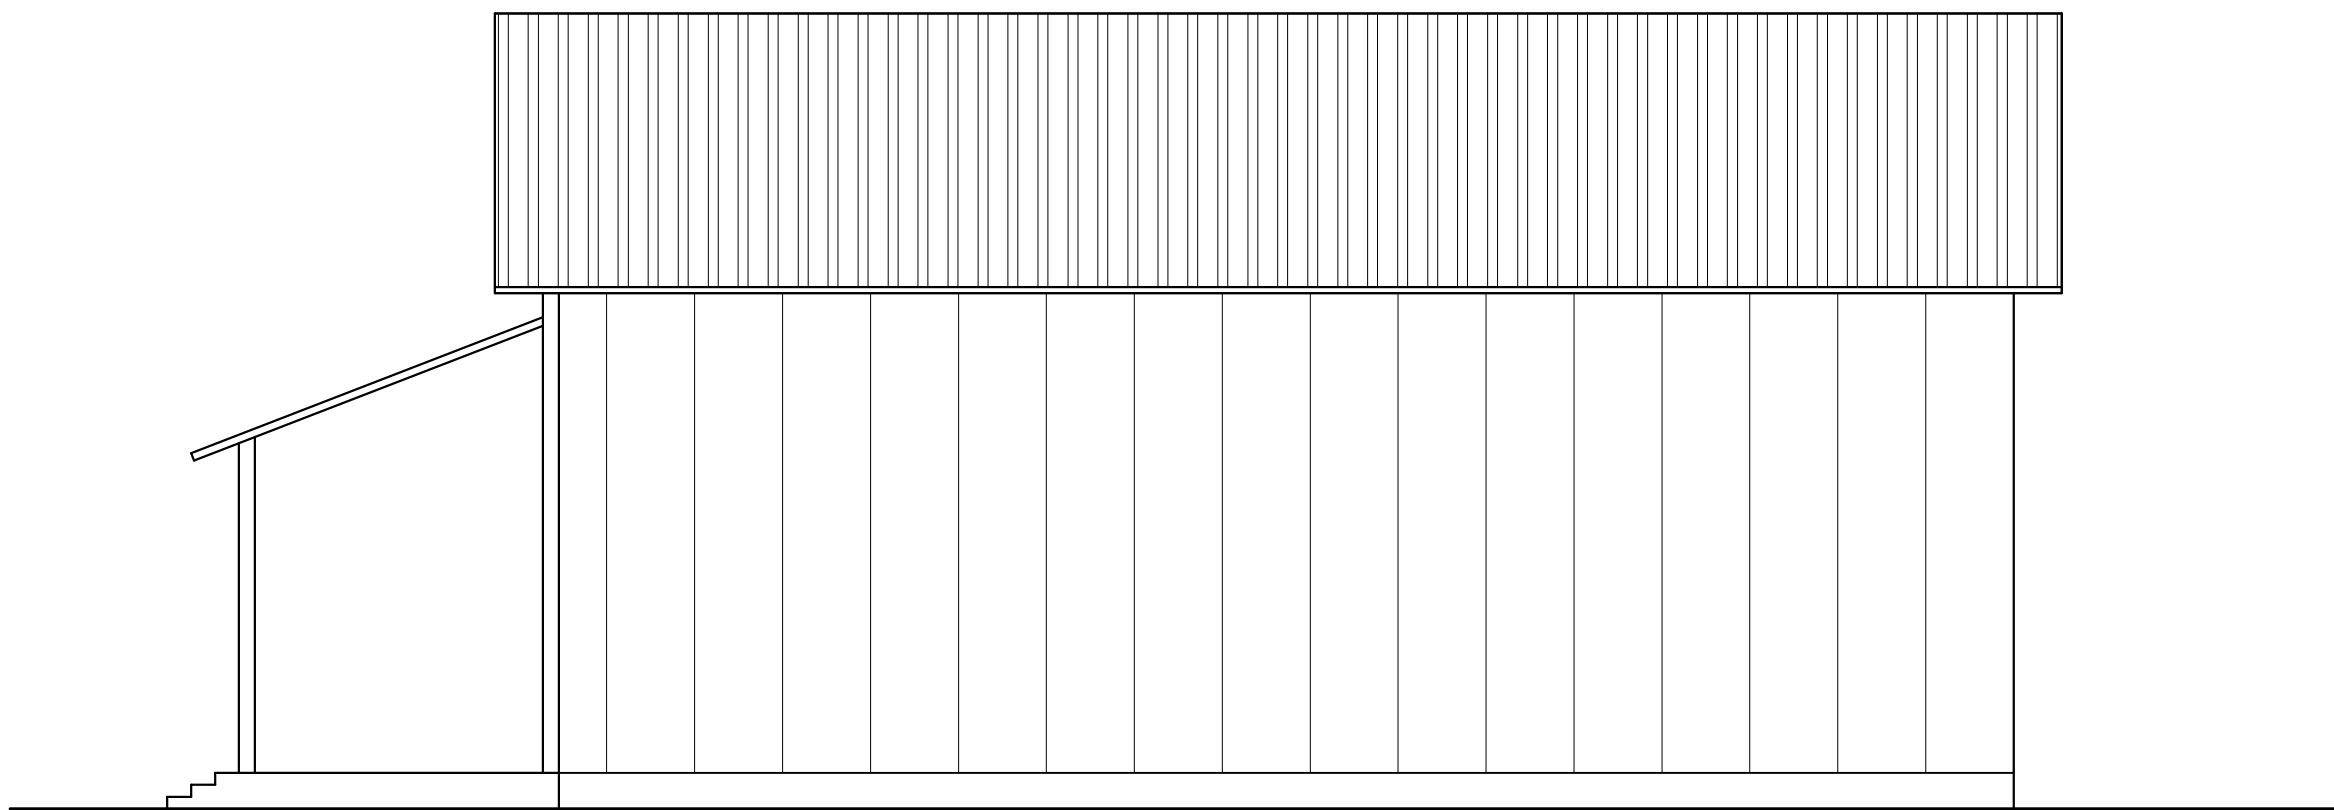


SOUTH ELEVATION

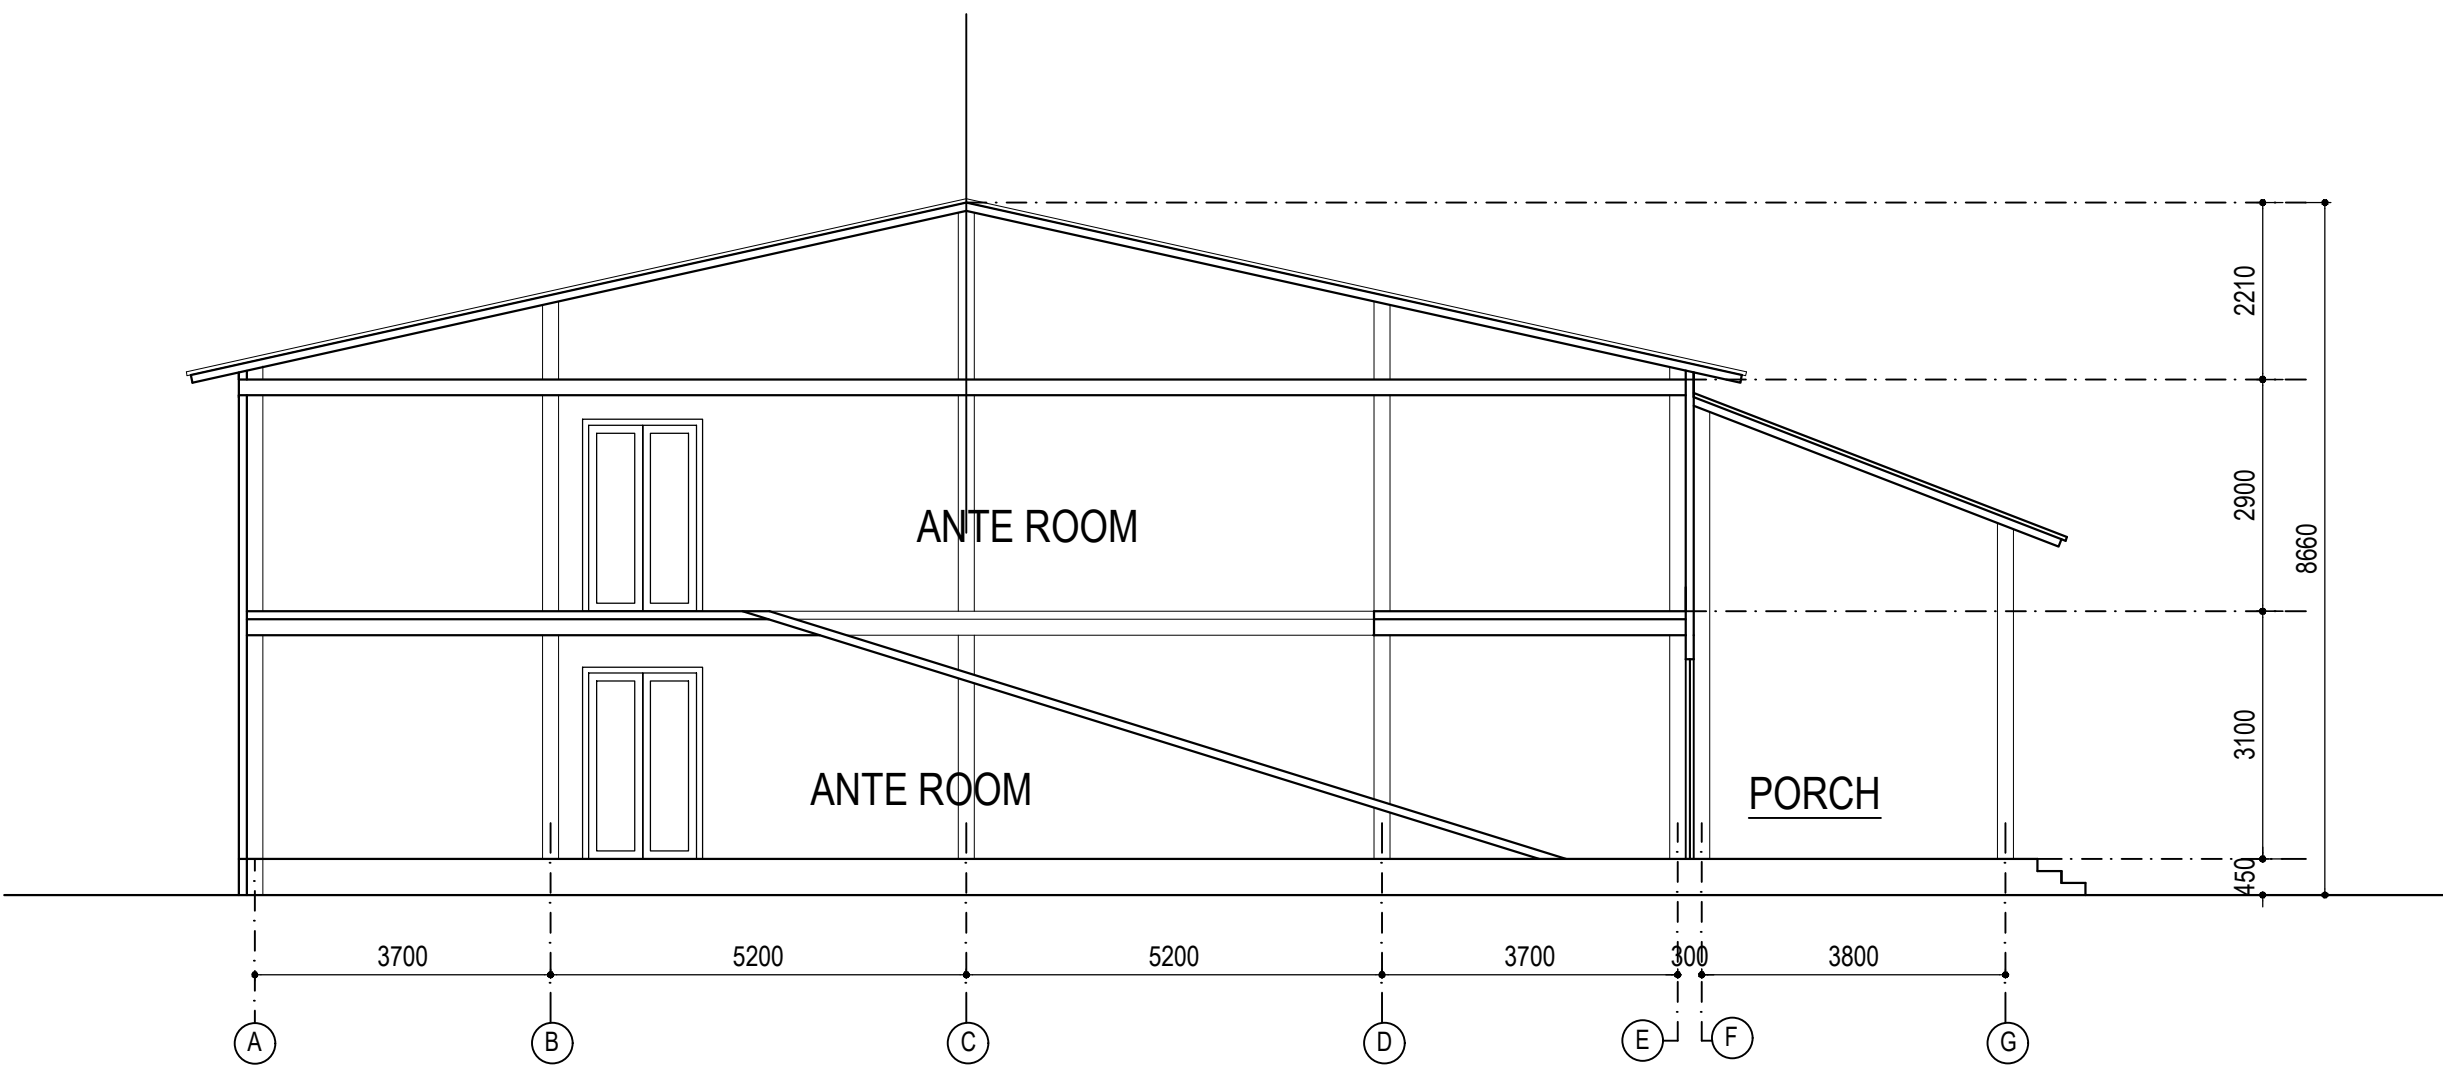

SECTION AT X-X

PROJECT: DPR OF 500MT COLD STORE AT JIRI, DOLAKHA		CONTENT: FLOOR PLAN	ARCHITECT :		CHECKED BY: APPROVED BY :	CONSULTANT: Sworaj Consultants Pvt. Ltd. Samkhushi, Kathmandu	Sheet No
CLIENT: Government of Province Ministry of Land Management, Agriculture and Cooperative Province No. 3, Hetauda		FINAL DRAWING	STR. ENGINEER:		SCALE : 1:200		AR 06
					DATE: REVISION:		

STRUCTURAL DRAWINGS

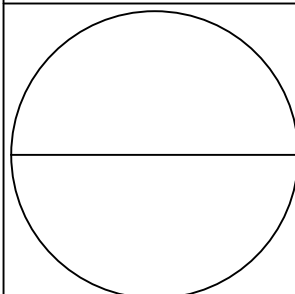PROJECT: DPR OF 500MT COLD STORE AT JIRI, DOLAKHA	CONTENT: STRUCTURAL DRAWINGS		CHECKED BY:	CONSULTANT: Sworaj Consultants Pvt. Ltd. Samakhushi, Kathmandu	Sheet No
CLIENT: Government of Province Ministry of Land Management, Agriculture and Cooperative Province No. 3, Hetauda	FINAL DRAWING		APPROVED BY :		
			SCALE :		
			DATE:	REVISION:	

GENERAL NOTES:-

A. General:

1. All works to be carried out in accordance with current best practice, Building Regulations, the project specification and relevant Indian Standards and Codes of Practice (IS 800:2007). Materials and components to be appropriate for their intended use.
2. The Contractor shall be responsible for verifying all dimensions on site and ensuring that all dimensions and levels shown on the drawings are correct and consistent with other relevant drawings. Any discrepancies are to be reported immediately to the Engineer.
3. During construction, the contractor shall be responsible for maintaining the structure in a stable condition and ensuring no part shall be damaged under construction activities.
4. Workmanship and materials are to be in accordance with the relevant current Indian Standards including all amendments and the local statutory authorities, except where varied by the contract document.
5. The Engineer shall accept no responsibility for the works unless they are inspected and approved by the Engineer during construction. At least 48 hours notice shall be provided for all engineering inspections..
6. Any damage to surface during erection/construction is to be made good.
7. The Contractor shall provide temporary scaffolding bracing and shoring against lateral forces and all construction loads throughout the work. The Contractor shall submit a method statement to the Engineer detailing the proposed means of the erecting the principal steelwork, including details of all temporary bracing and shoring required.
8. Before commencing structural steel works, the existing dimensions of the building shall be verified at the site.

B. Structural

Steel

1. Bolt should be of 4.6 grade.
2. Requirements of welds and weldings shall confirm to IS 816 and IS 9595, as appropriate.
3. The electrodes required for metal or welding shall be covered and shall confirm to IS 814 1991.
4. Metal surface shall be properly cleaned.
5. Welds and weldings shall be applied as per design/drawing/specifications.
6. Tensile Stress area of bolts shall be as followed:

Bolt size, d (mm)	Tensile Stress Area (mm ²)
16	157
20	245
24	353

7. Tensile properties of bolts in steel construction shall be as followed:

Grade / Classification	Properties		
	Yield stress fy MPa(min)	Ultimate Tensile Stress fub MPa (min)	Elongation % (min)
4.6	240	400	22
4.8	320	420	14

8. Minimum edge distance of the bolts shall be as followed:

Nominal diameter of bolt (d) (mm)	Diameter of hole (do) (mm)	Distance to sheared (mm)	Distance to rolled (e) (mm)
12	13	20	19
16	18	30	27
20	22	37	33
24	26	44	39

C. Units:

1. Do not scale drawings. Any missing dimensions shall be furnished upon request.
2. All dimensions are in millimeters unless otherwise stated.


D. Abbreviations:

1. CL = Centre line
2. C/C = Centre to centre
3. EL = Elevation
4. N.T.S. = Not to scale
5. RC = Reinforced concrete
6. ST = Stirrup(s)
7. G.I. = Galvanized Iron
8. N/A = Not applicable
9. BoQ = Bill of Quantities
10. SWG = Standard Wire Gauge

Note:


1. The Engineer may issue additional drawings for construction showing further details / clarifications etc whenever necessary.
2. The Contractor shall be deemed to have visited the site before submitting his tender and shall be wholly responsible for acquainting himself with the nature and the position of the site, service locations, groundwater levels, soil conditions, obstructions, the full extent of the works and all other information relevant to the execution of the Works.

PROJECT: DPR OF 500MT COLD STORE AT JIRI, DOLAKHA	CONTENT: STRUCTURAL DRAWINGS		CHECKED BY: APPROVED BY :	CONSULTANT: Sworaj Consultants Pvt. Ltd. Samkhushi, Kathmandu	Sheet No
CLIENT: Government of Province Ministry of Land Management, Agriculture and Cooperative Province No. 3, Hetauda	FINAL DRAWING		SCALE :		ST 01
		DATE:	REVISION:		

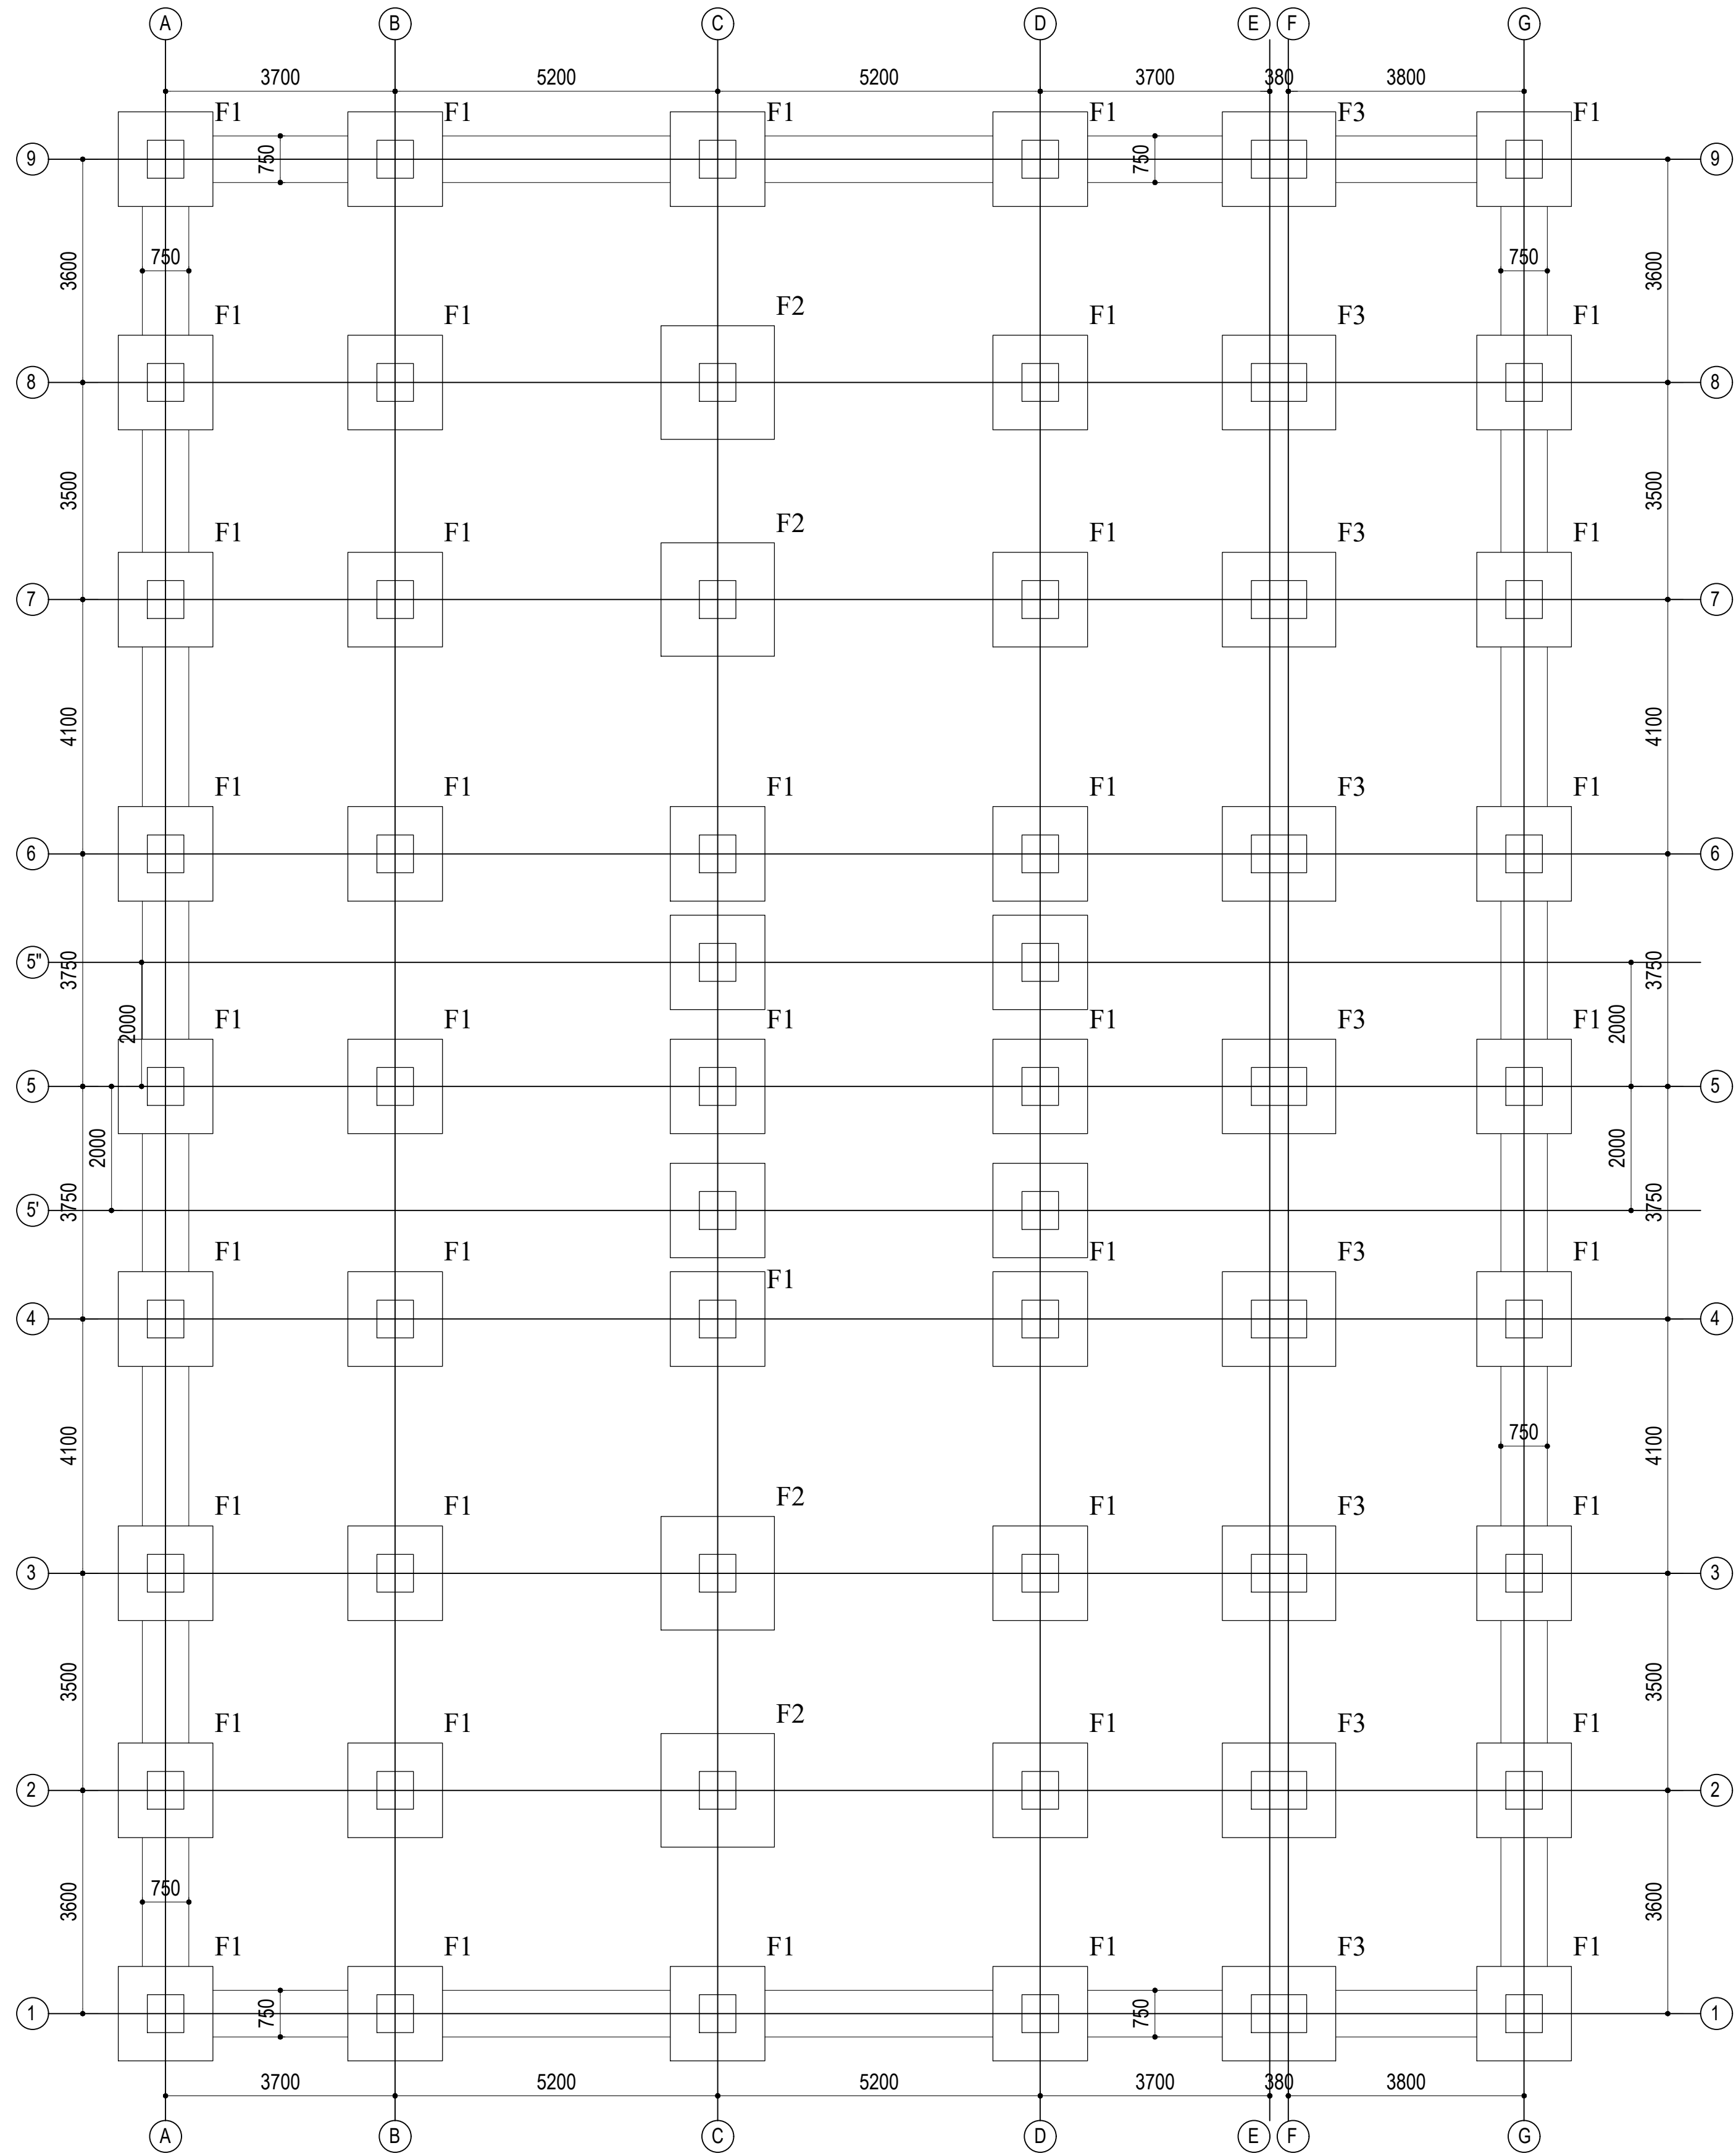


Footings Trench Plan


PROJECT: DPR OF 500MT COLD STORE AT JIRI, DOLAKHA		CONTENT: STRUCTURAL DRAWINGS		CHECKED BY: APPROVED BY :		CONSULTANT: Sworaj Consultants Pvt. Ltd. Samakhushi, Kathmandu		Sheet No	
CLIENT: Government of Province Ministry of Land Management, Agriculture and Cooperative Province No. 3, Hetauda		FINAL DRAWING		SCALE :				ST 02	
				DATE: REVISION:					

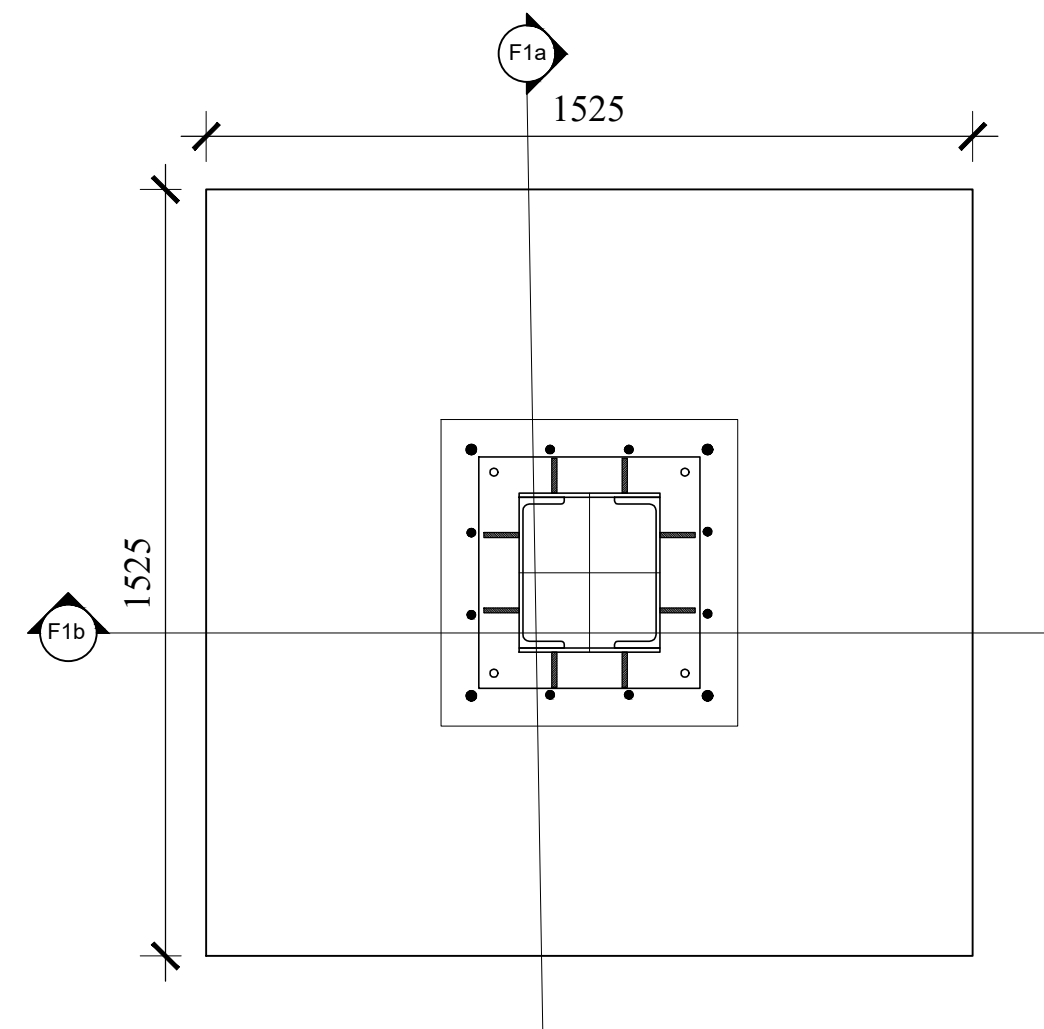


FOUNDATION-F1

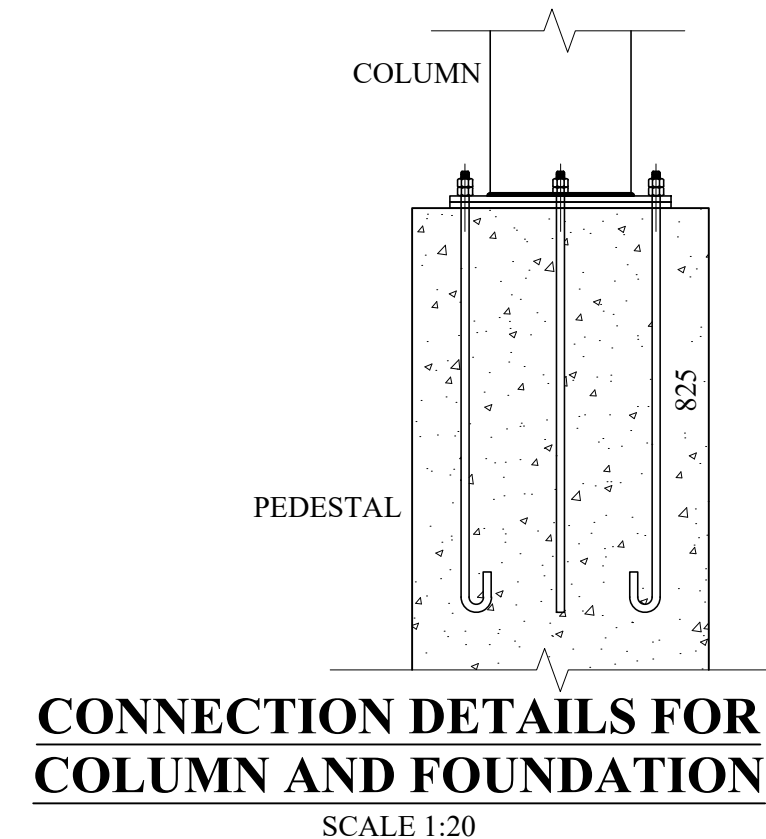


CONNECTION DETAILS FOR COLUMN AND FOUNDATION
SCALE 1:20

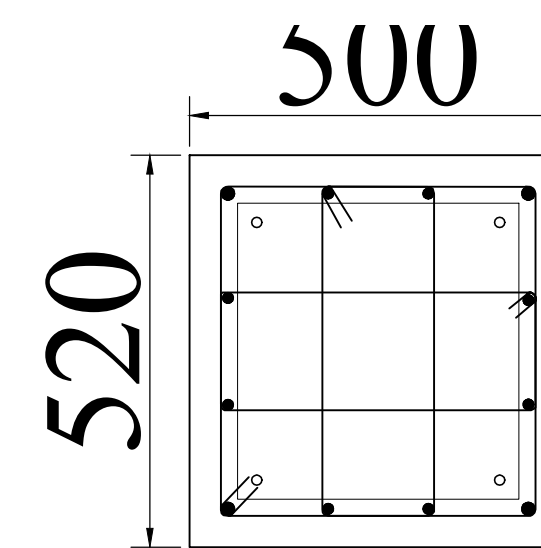


PEDESTAL DETAIL OF FOUNDATION-F1 and F2

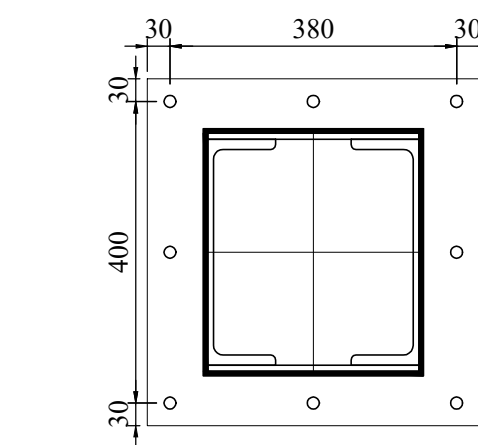


CONNECTION OF COLUMN & BASE PLATE

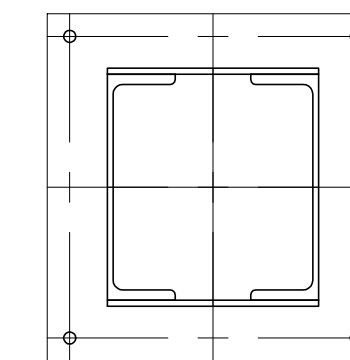


BASE PLATE DETAIL

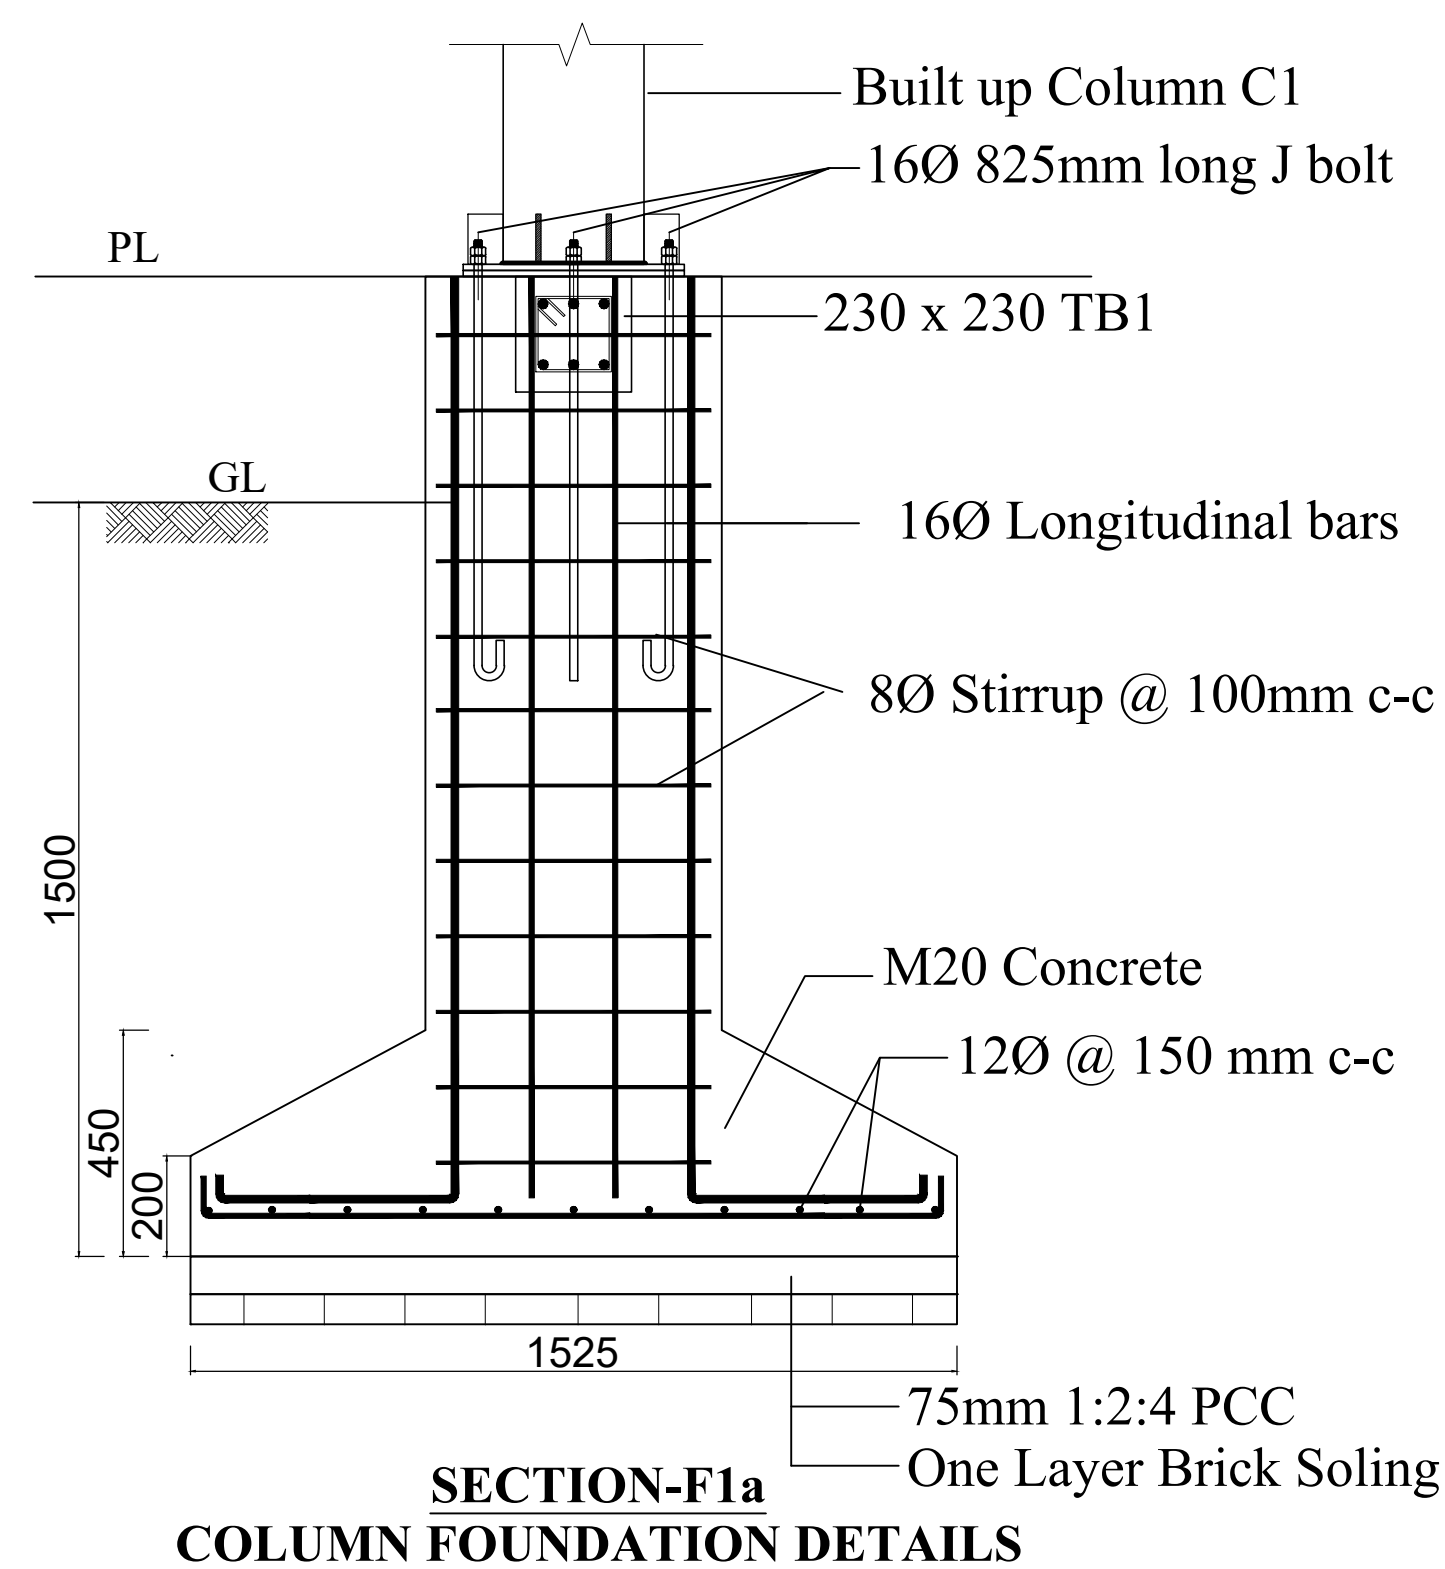


SECTION-F1a
COLUMN FOUNDATION DETAILS

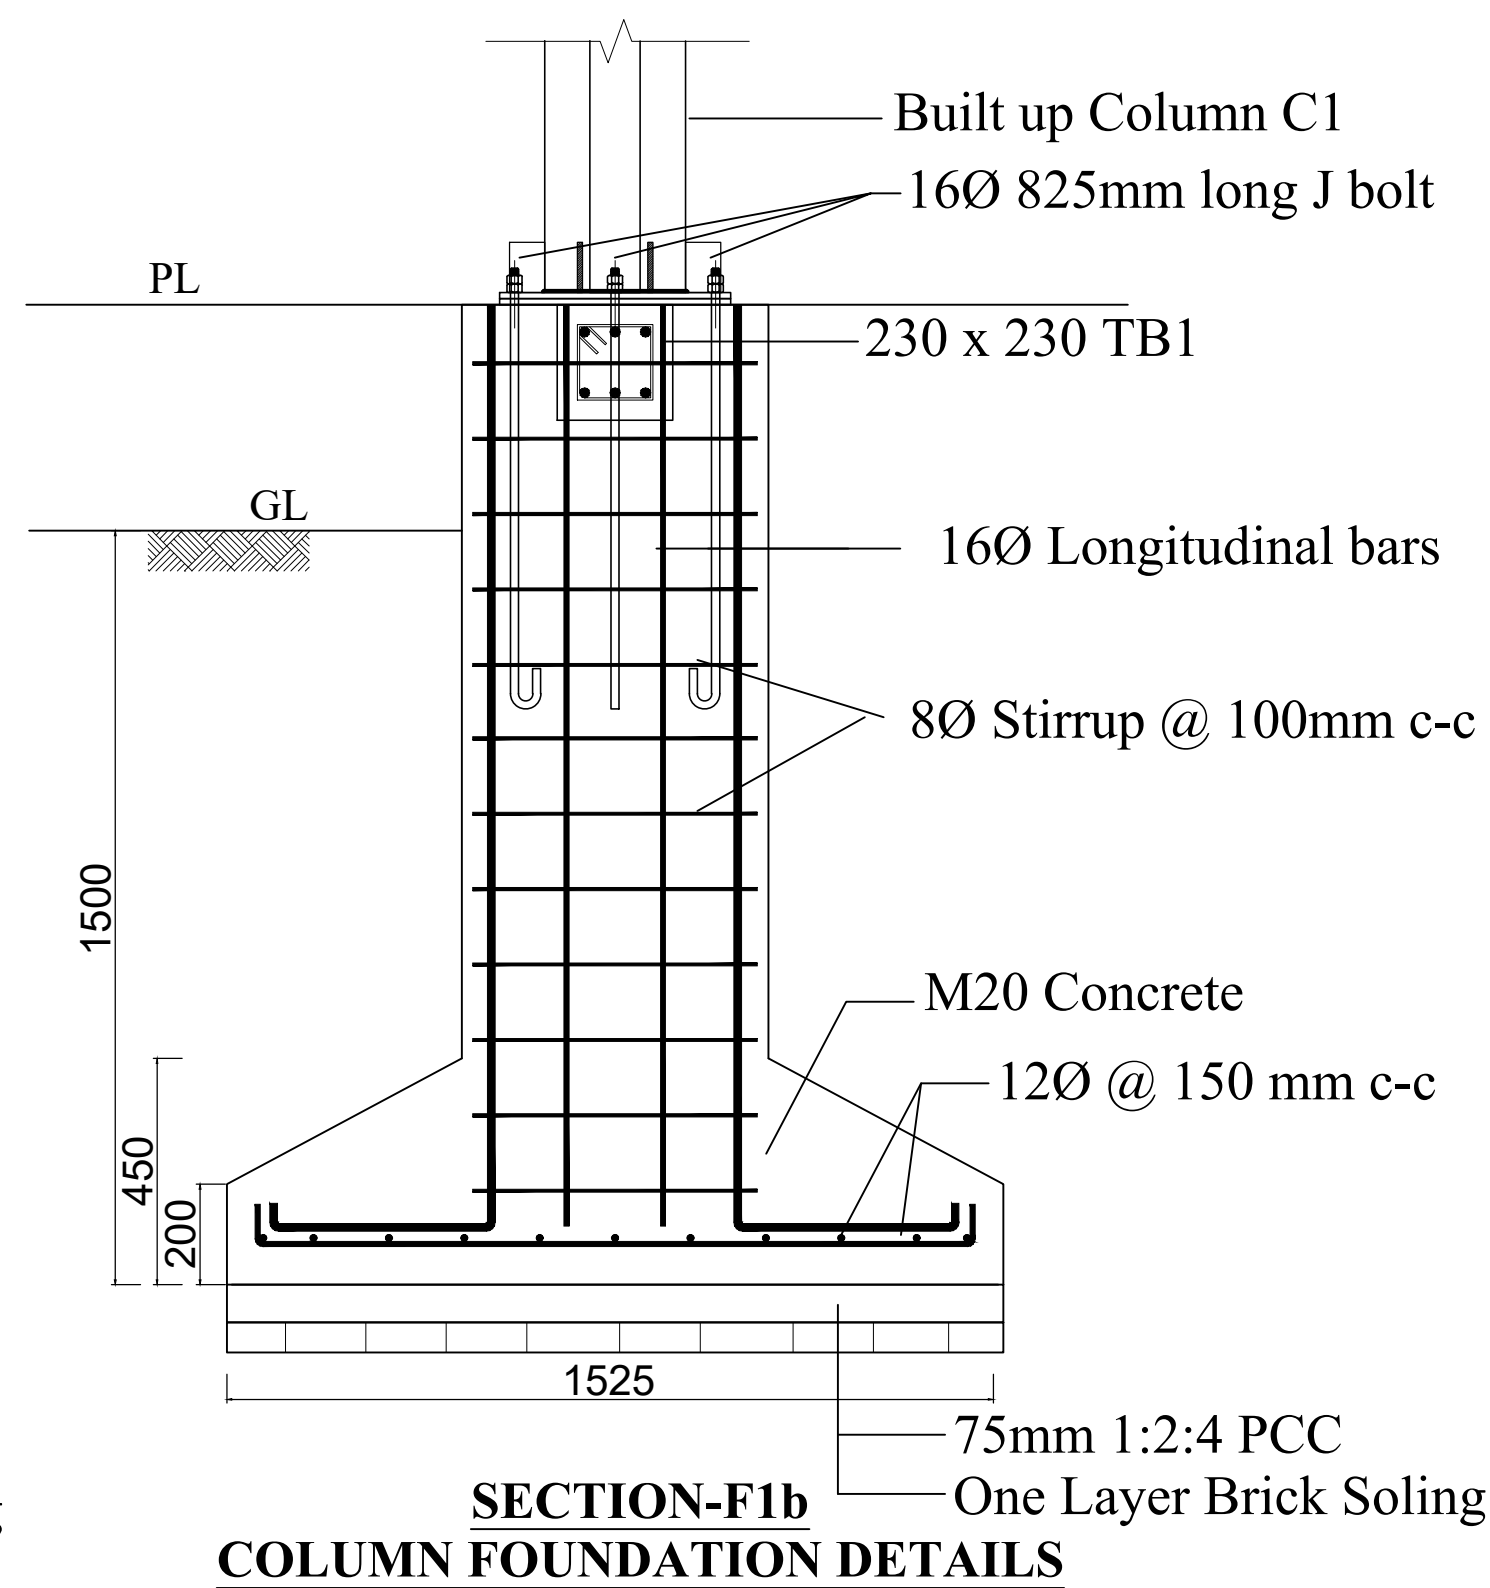


SECTION-F1b
COLUMN FOUNDATION DETAILS

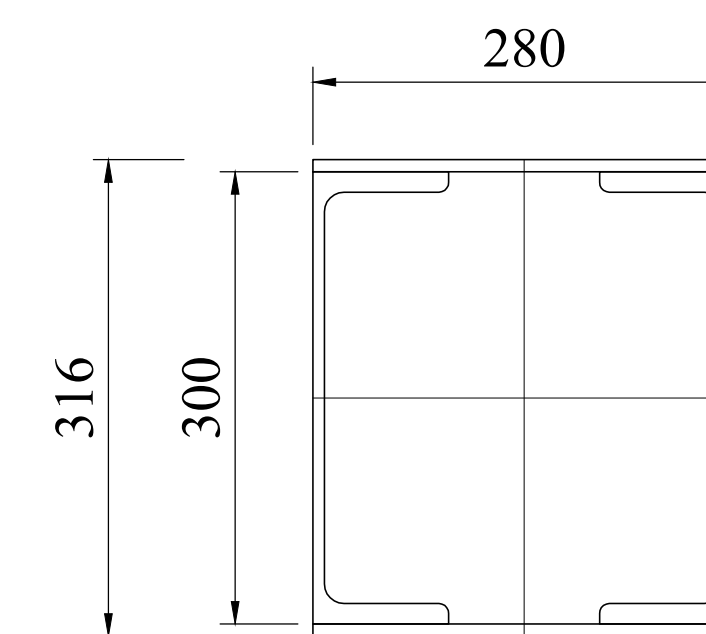

C1
ISMC 300

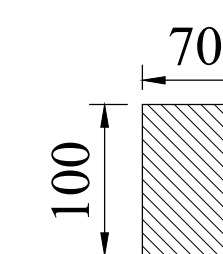


STIFFENER - S1
(10mm thick)

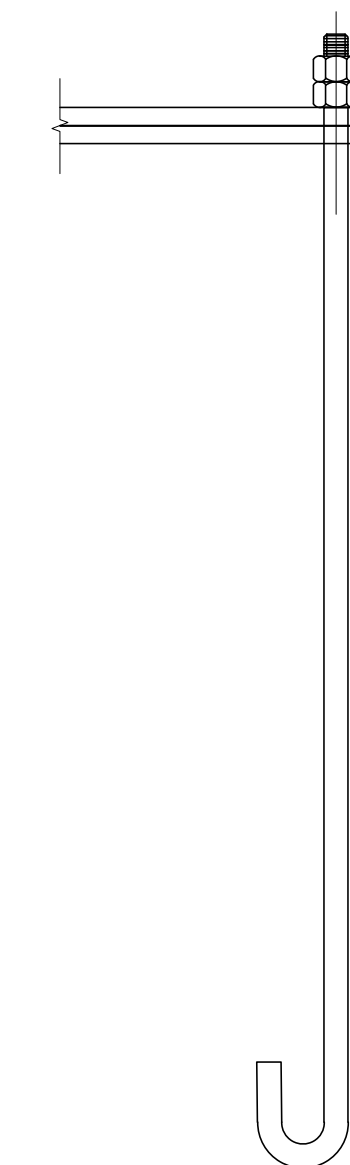


8-16Ø 825mm long
Anchor Bolts (J-Hooks)


PROJECT: DPR OF 500MT COLD STORE AT JIRI, DOLAKHA	CONTENT: STRUCTURAL DRAWINGS		CHECKED BY: APPROVED BY :	CONSULTANT: Sworaj Consultants Pvt. Ltd. Samkhushi, Kathmandu	Sheet No
CLIENT: Government of Province Ministry of Land Management, Agriculture and Cooperative Province No. 3, Hetauda	FINAL DRAWING		SCALE :		ST 03
			DATE: REVISION:		

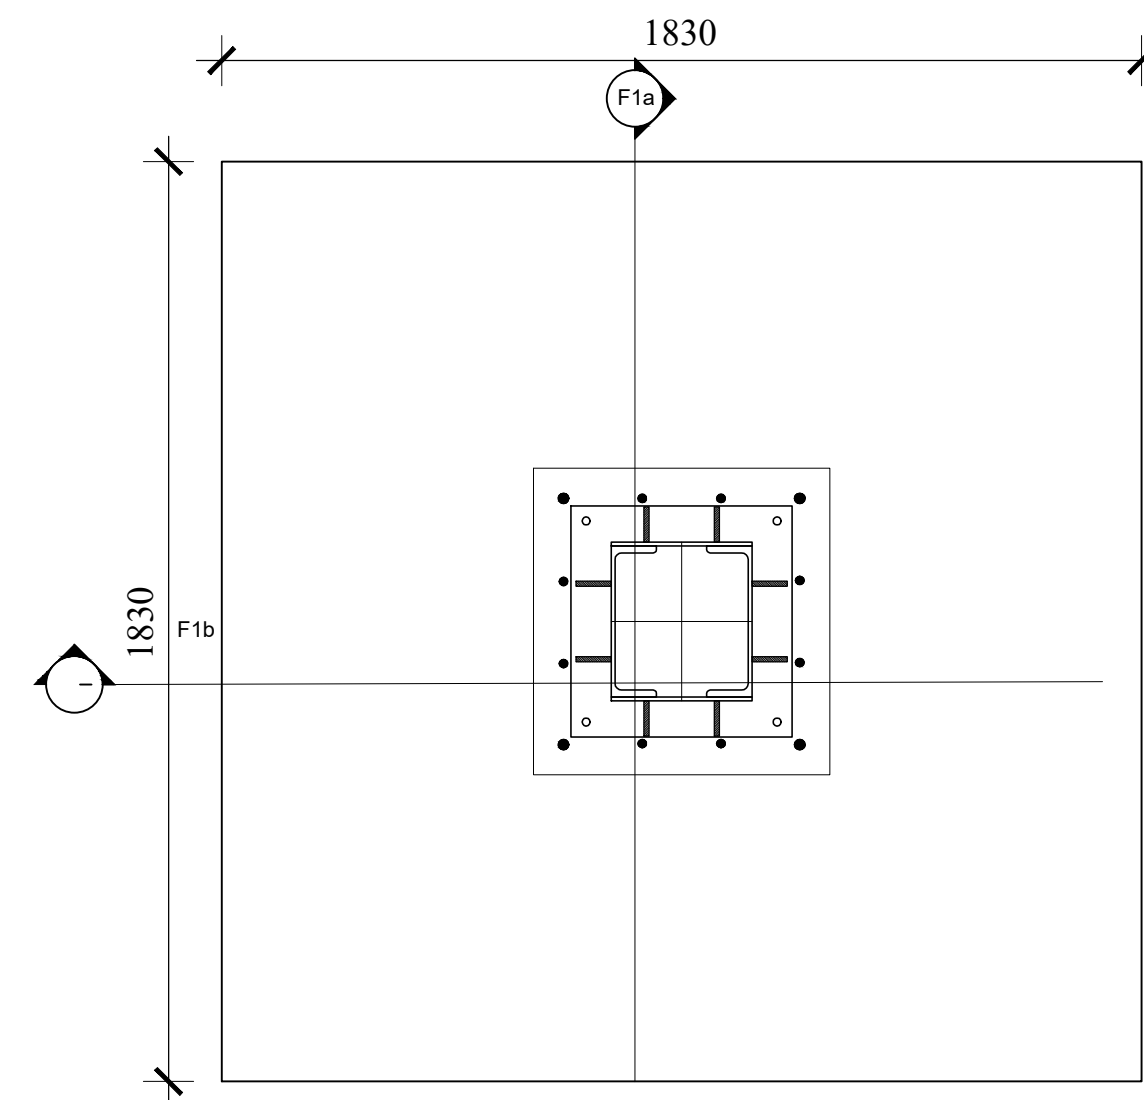


FOUNDATION-F2

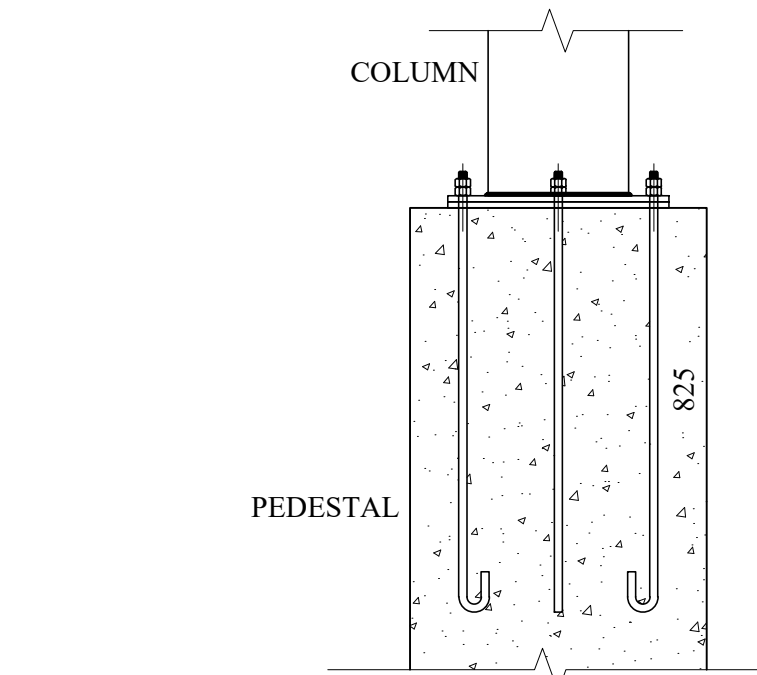


CONNECTION DETAILS FOR COLUMN AND FOUNDATION
SCALE 1:20

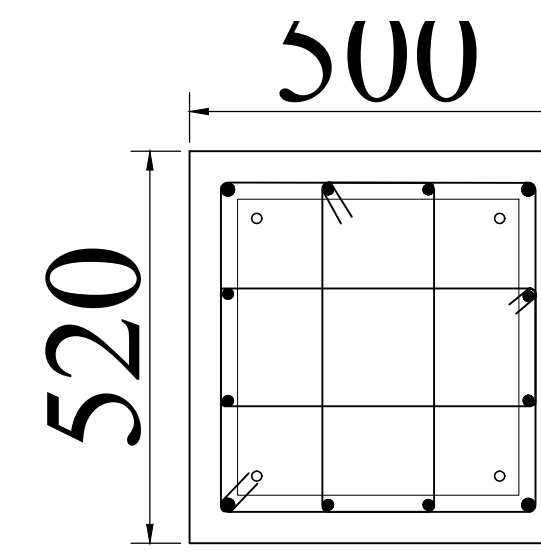


PEDESTAL DETAIL OF FOUNDATION-F1 and F2

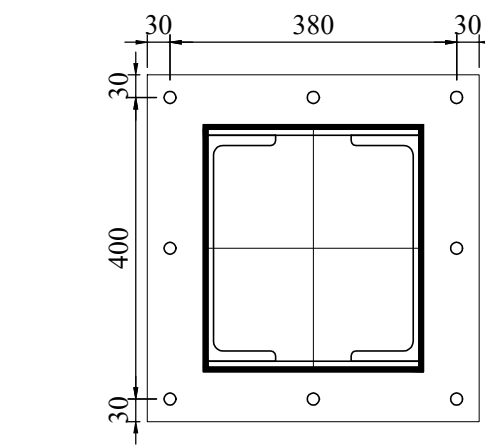


CONNECTION OF COLUMN & BASE PLATE

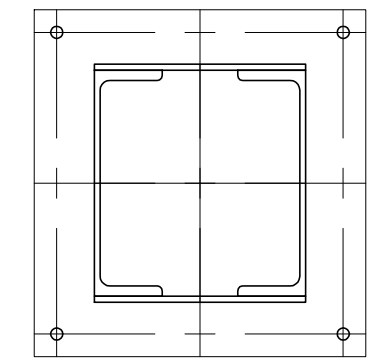


BASE PLATE DETAIL

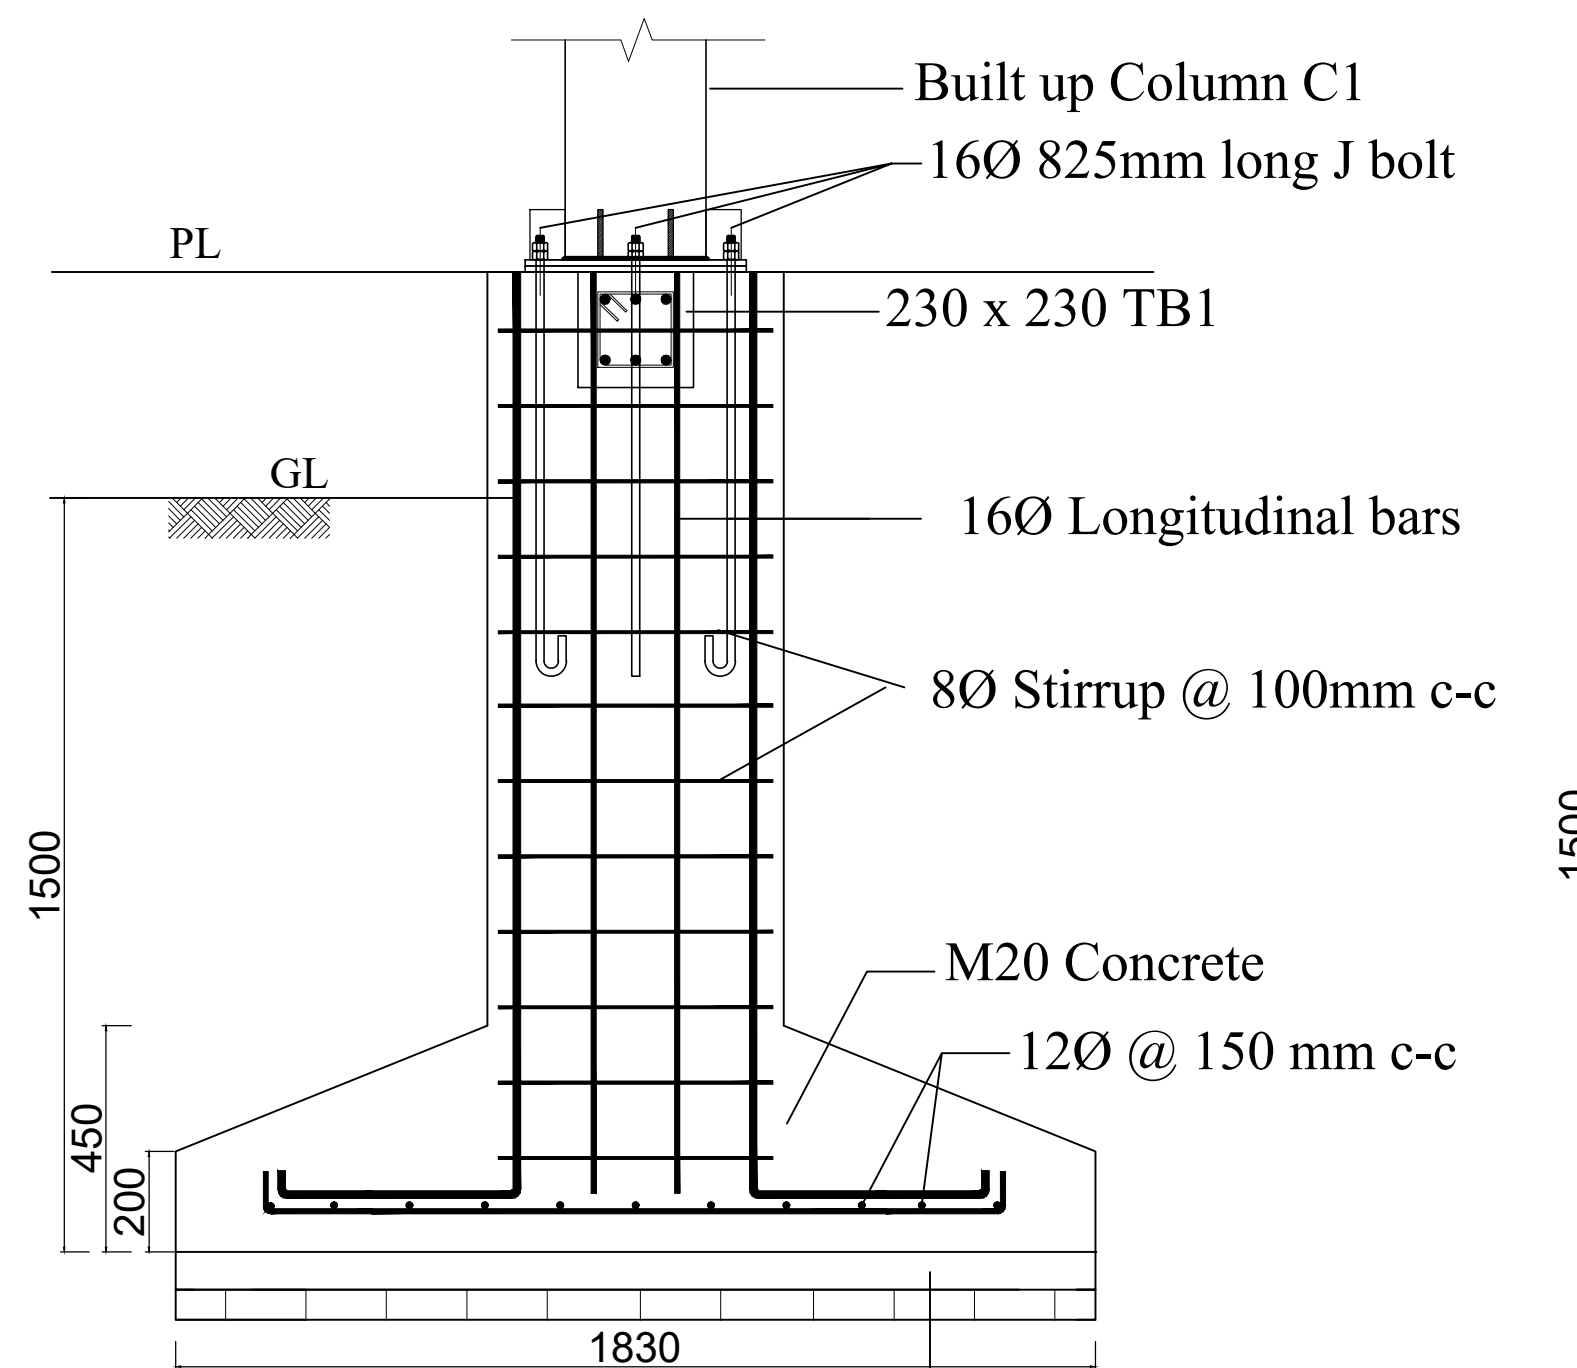


SECTION-F2a
COLUMN FOUNDATION DETAILS

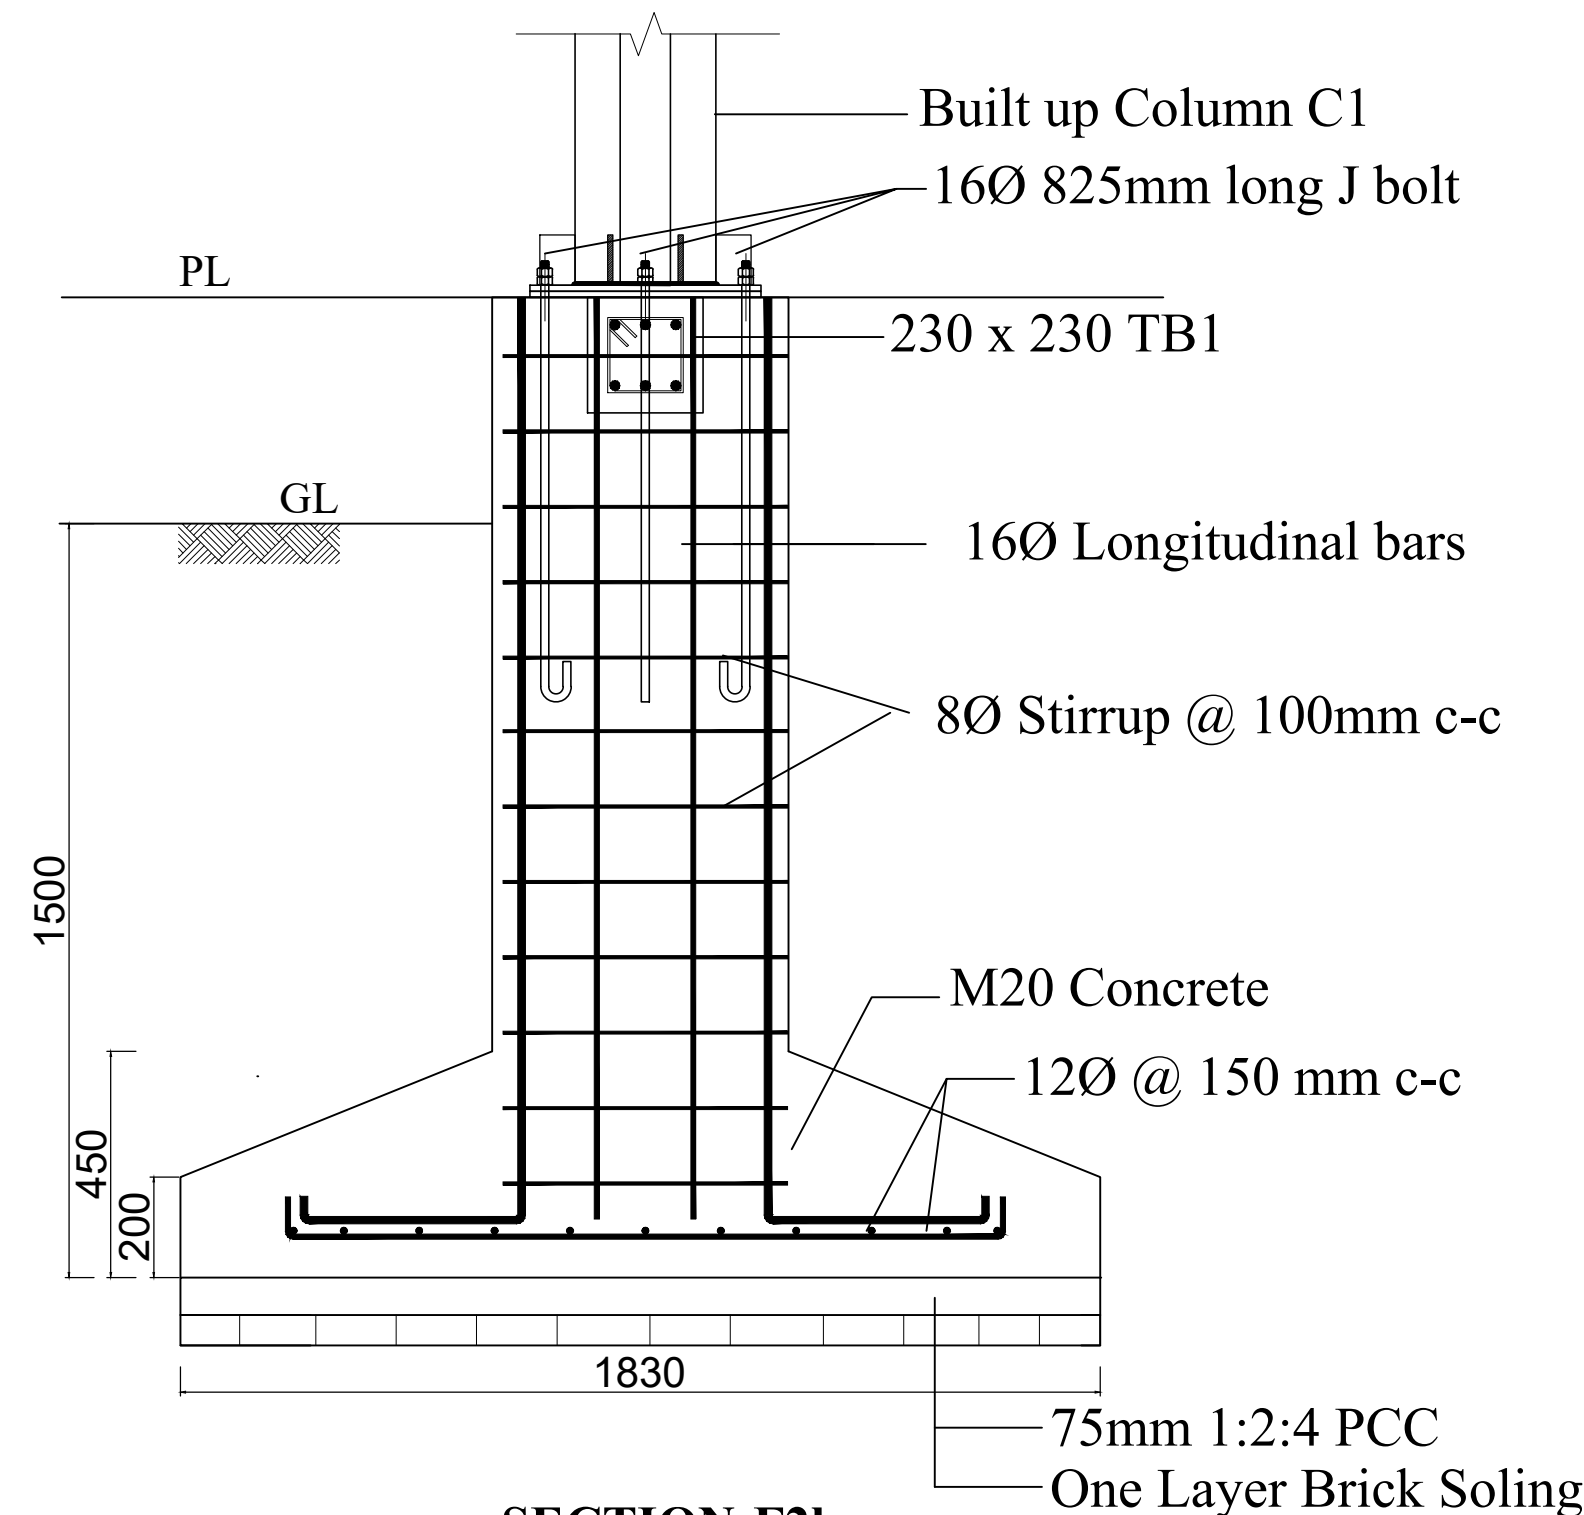


SECTION-F2b
COLUMN FOUNDATION DETAILS

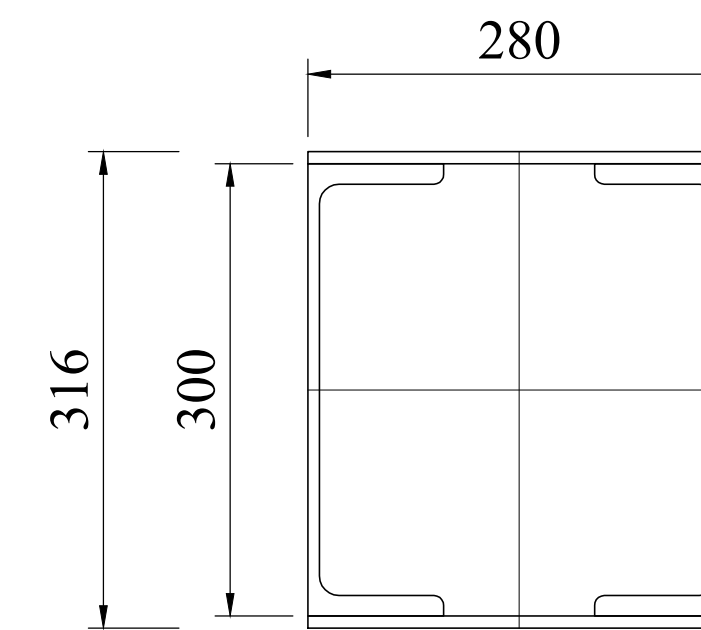

C1
ISMC 300

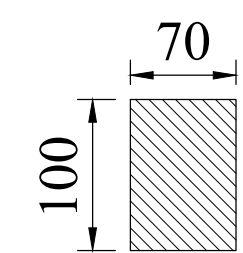


STIFFENER - S1
(10mm thick)

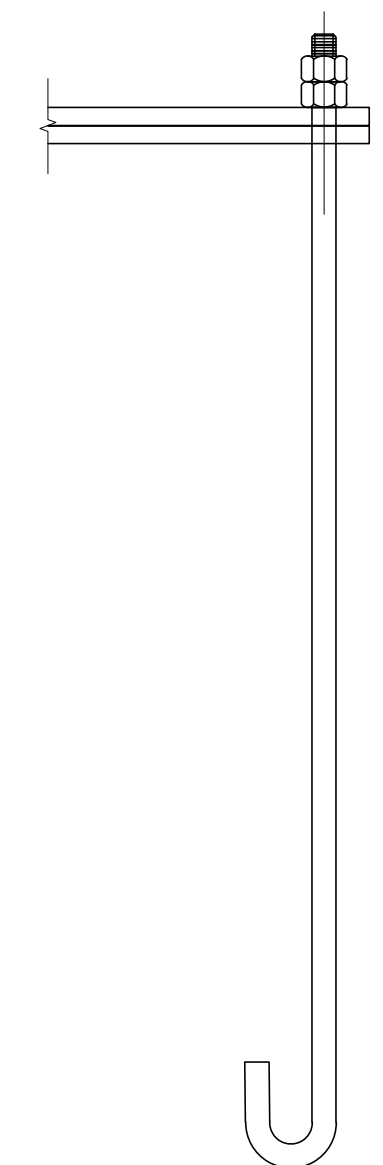


8-16Ø 825mm long
Anchor Bolts (J-Hooks)


PROJECT: DPR OF 500MT COLD STORE AT JIRI, DOLAKHA	CONTENT: STRUCTURAL DRAWINGS		CHECKED BY: APPROVED BY :	CONSULTANT: Sworaj Consultants Pvt. Ltd. Samkhushi, Kathmandu	Sheet No
CLIENT: Government of Province Ministry of Land Management, Agriculture and Cooperative Province No. 3, Hetauda	FINAL DRAWING		SCALE :		ST 04
			DATE: REVISION:		

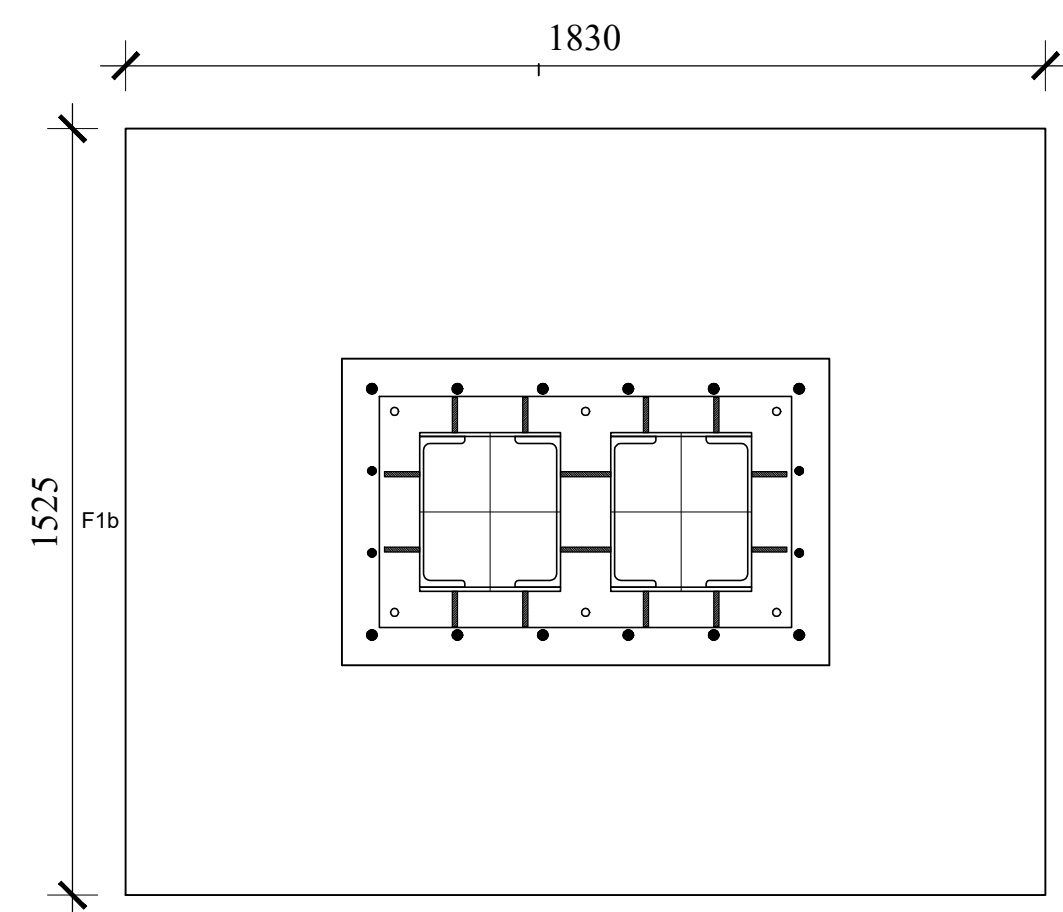


FOUNDATION-F3

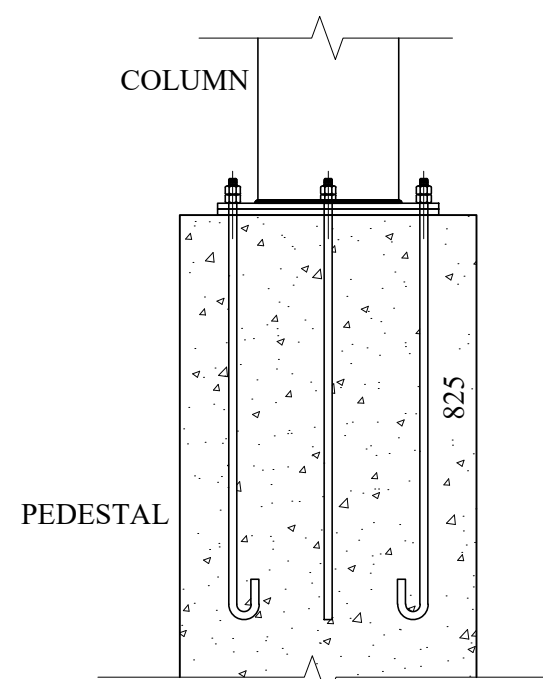


CONNECTION DETAILS FOR COLUMN AND FOUNDATION
SCALE 1:20

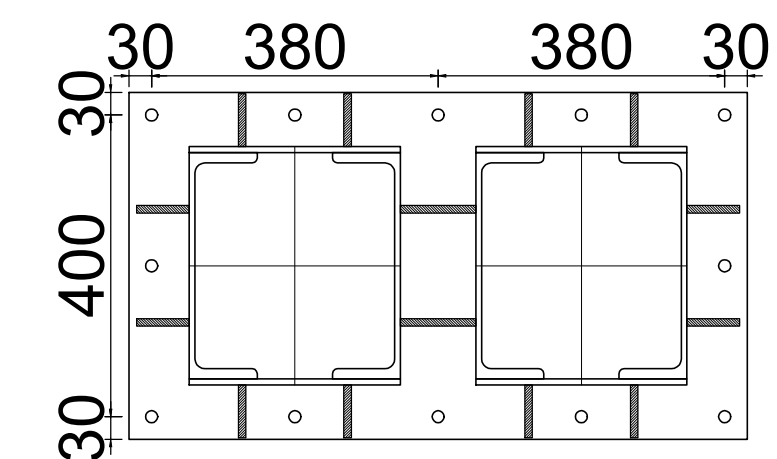


BASE PLATE DETAIL

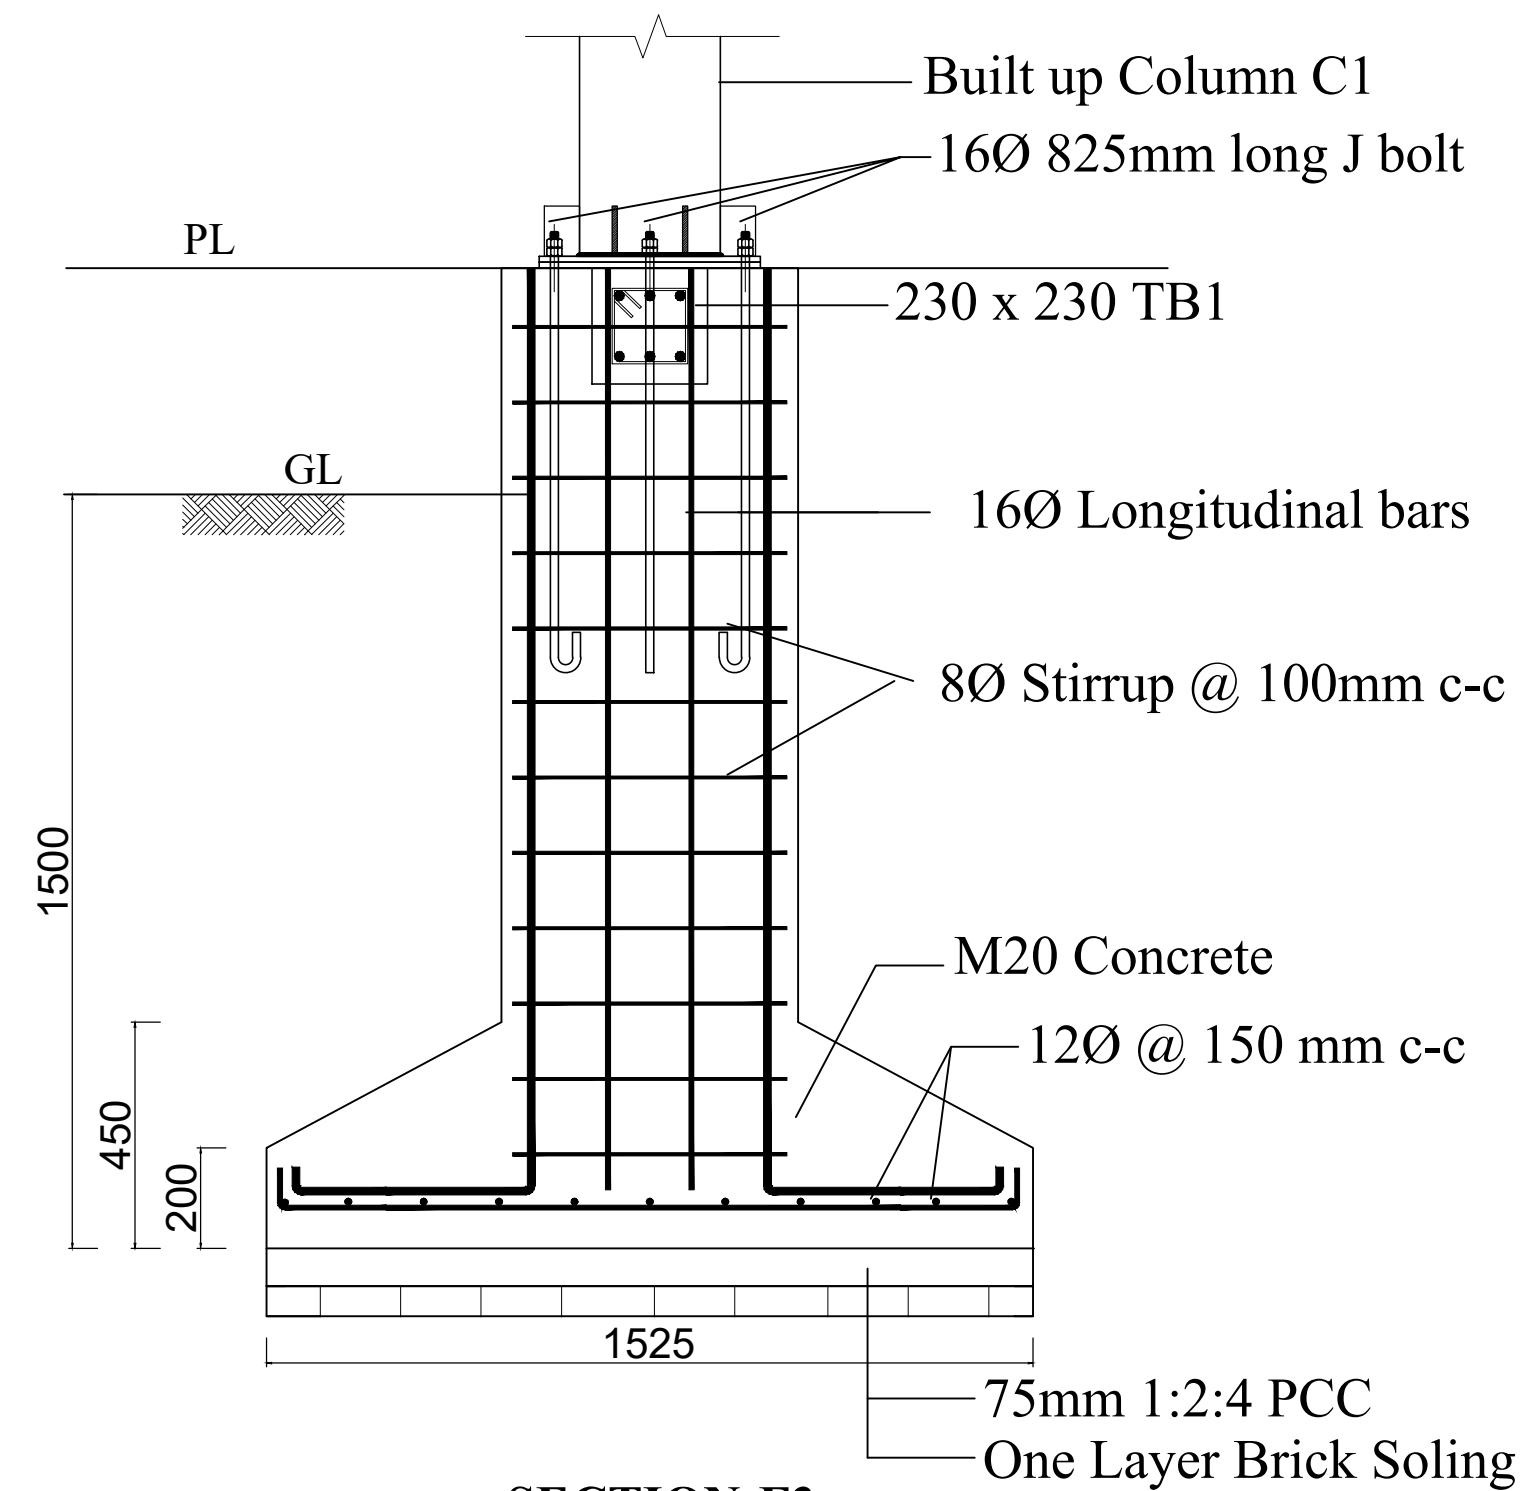


SECTION-F3a
COLUMN FOUNDATION DETAILS

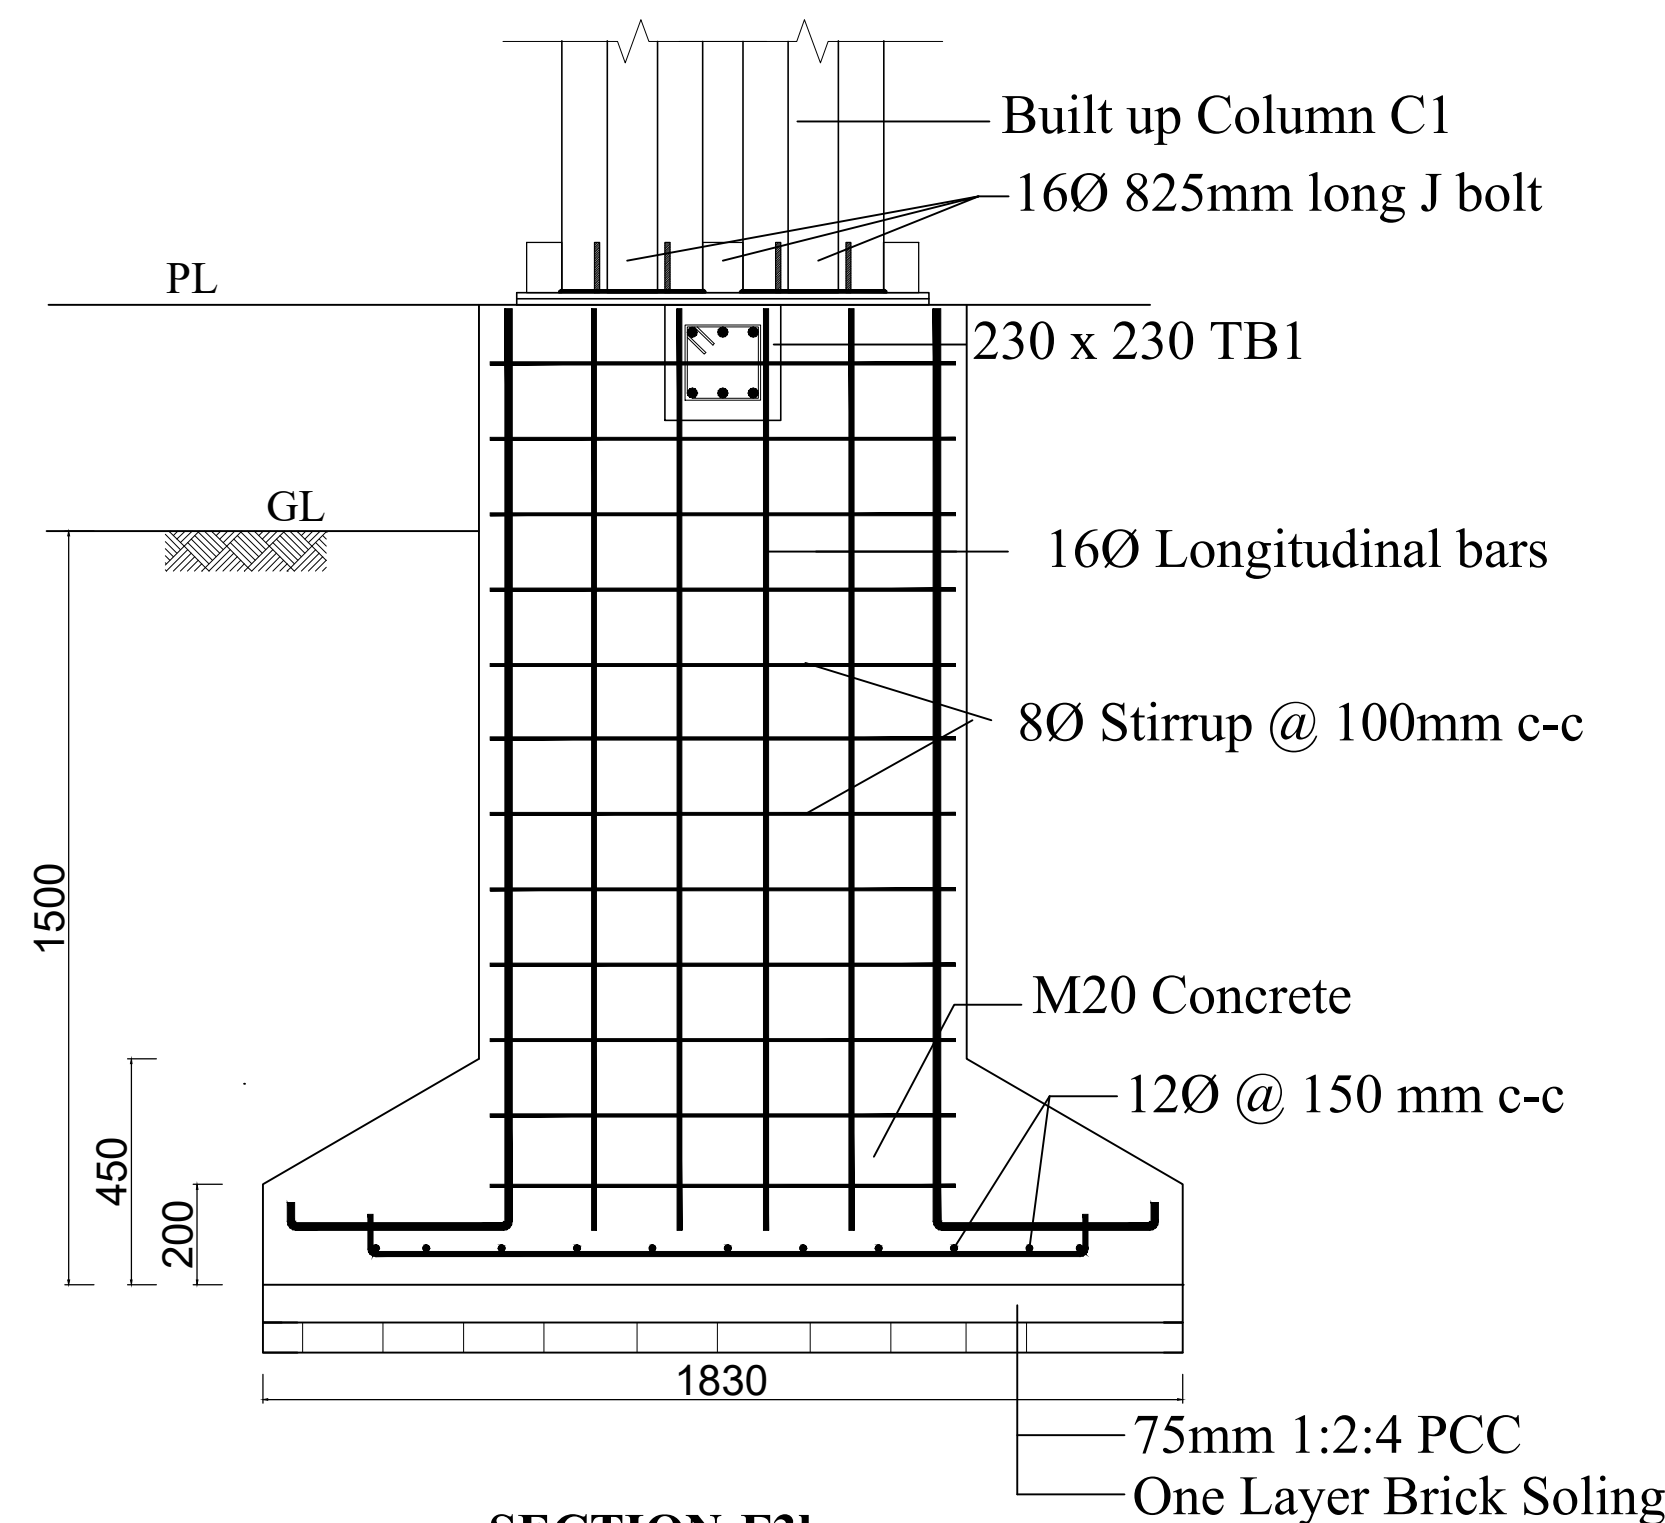

SECTION-F3b
COLUMN FOUNDATION DETAILS

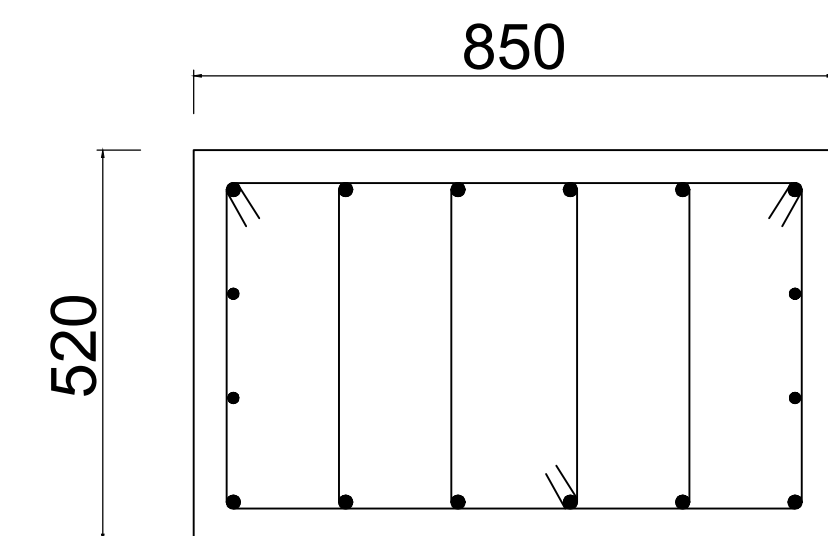


PEDESTAL DETAIL
OF FOUNDATION-F3

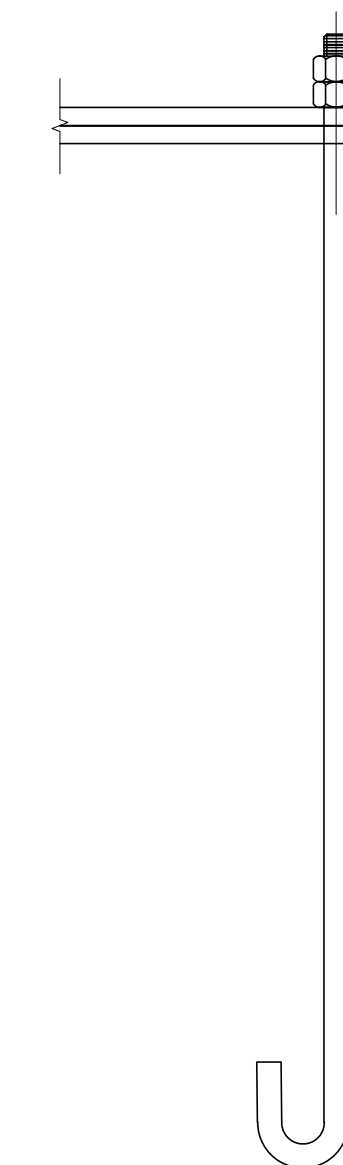


8-16Ø 825mm long
Anchor Bolts (J-Hooks)

PROJECT: DPR OF 500MT COLD STORE AT JIRI, DOLAKHA	CONTENT: STRUCTURAL DRAWINGS		CHECKED BY: APPROVED BY :	CONSULTANT: Sworaj Consultants Pvt. Ltd. Samkhushi, Kathmandu	Sheet No
CLIENT: Government of Province Ministry of Land Management, Agriculture and Cooperative Province No. 3, Hetauda	FINAL DRAWING		SCALE :		ST 05
			DATE: REVISION:		

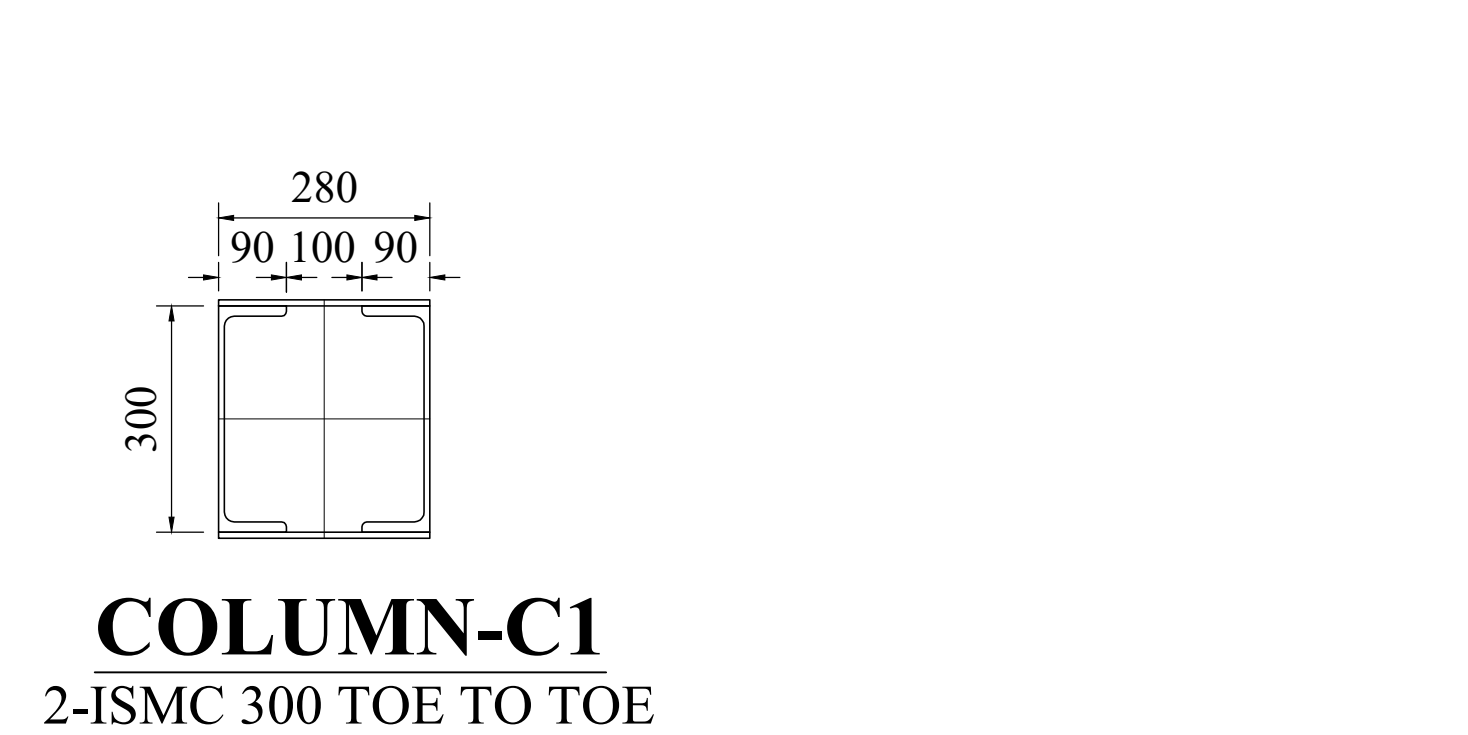

L-SECTION ALONG TIE BEAM AT MID PORTIONS OF BUILDING

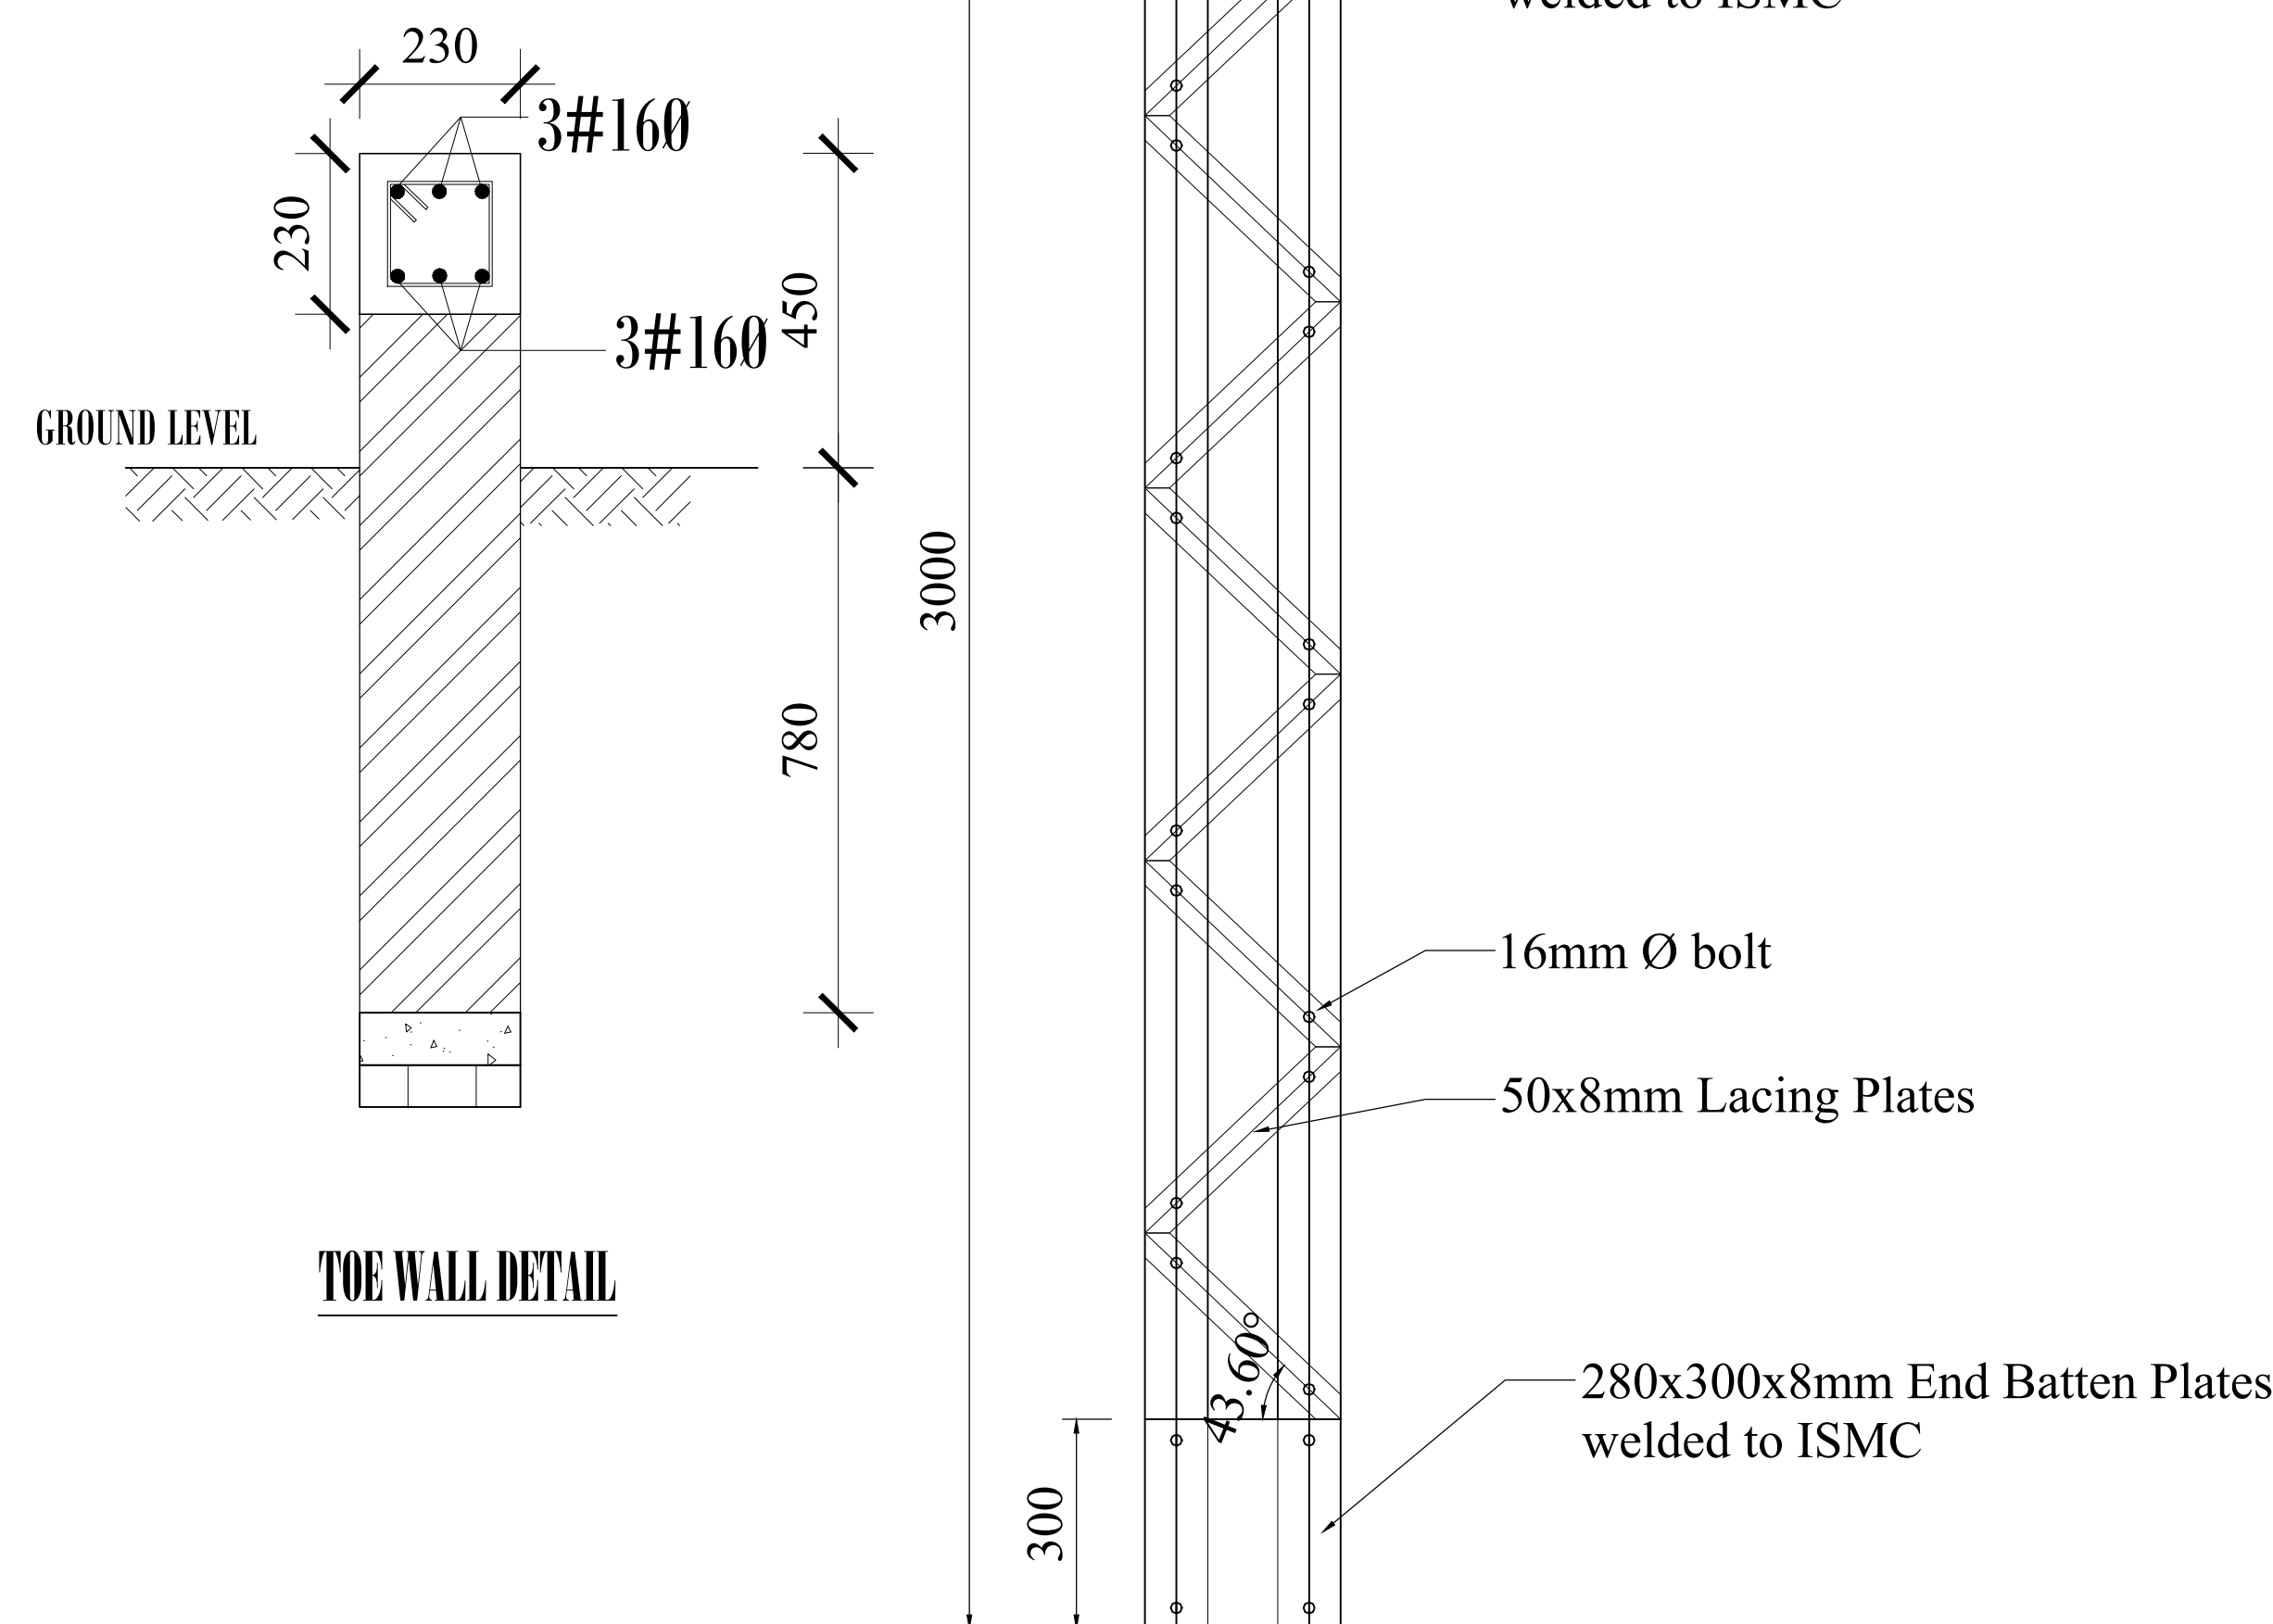


L-SECTION ALONG THE BEAM & TOE WALL AT PERIMETER OF BUILDING

ELEVATION OF COLUMNS C1


SCALE 1:20

PROJECT: DPR OF 500MT COLD STORE AT JIRI, DOLAKHA	CONTENT: STRUCTURAL DRAWINGS	CHECKED BY: APPROVED BY :	CONSULTANT: Sworaj Consultants Pvt. Ltd. Samkhushi, Kathmandu	Sheet No
CLIENT: Government of Province Ministry of Land Management, Agriculture and Cooperative Province No. 3, Hetauda	FINAL DRAWING	SCALE :		ST 06
		DATE: REVISION:		

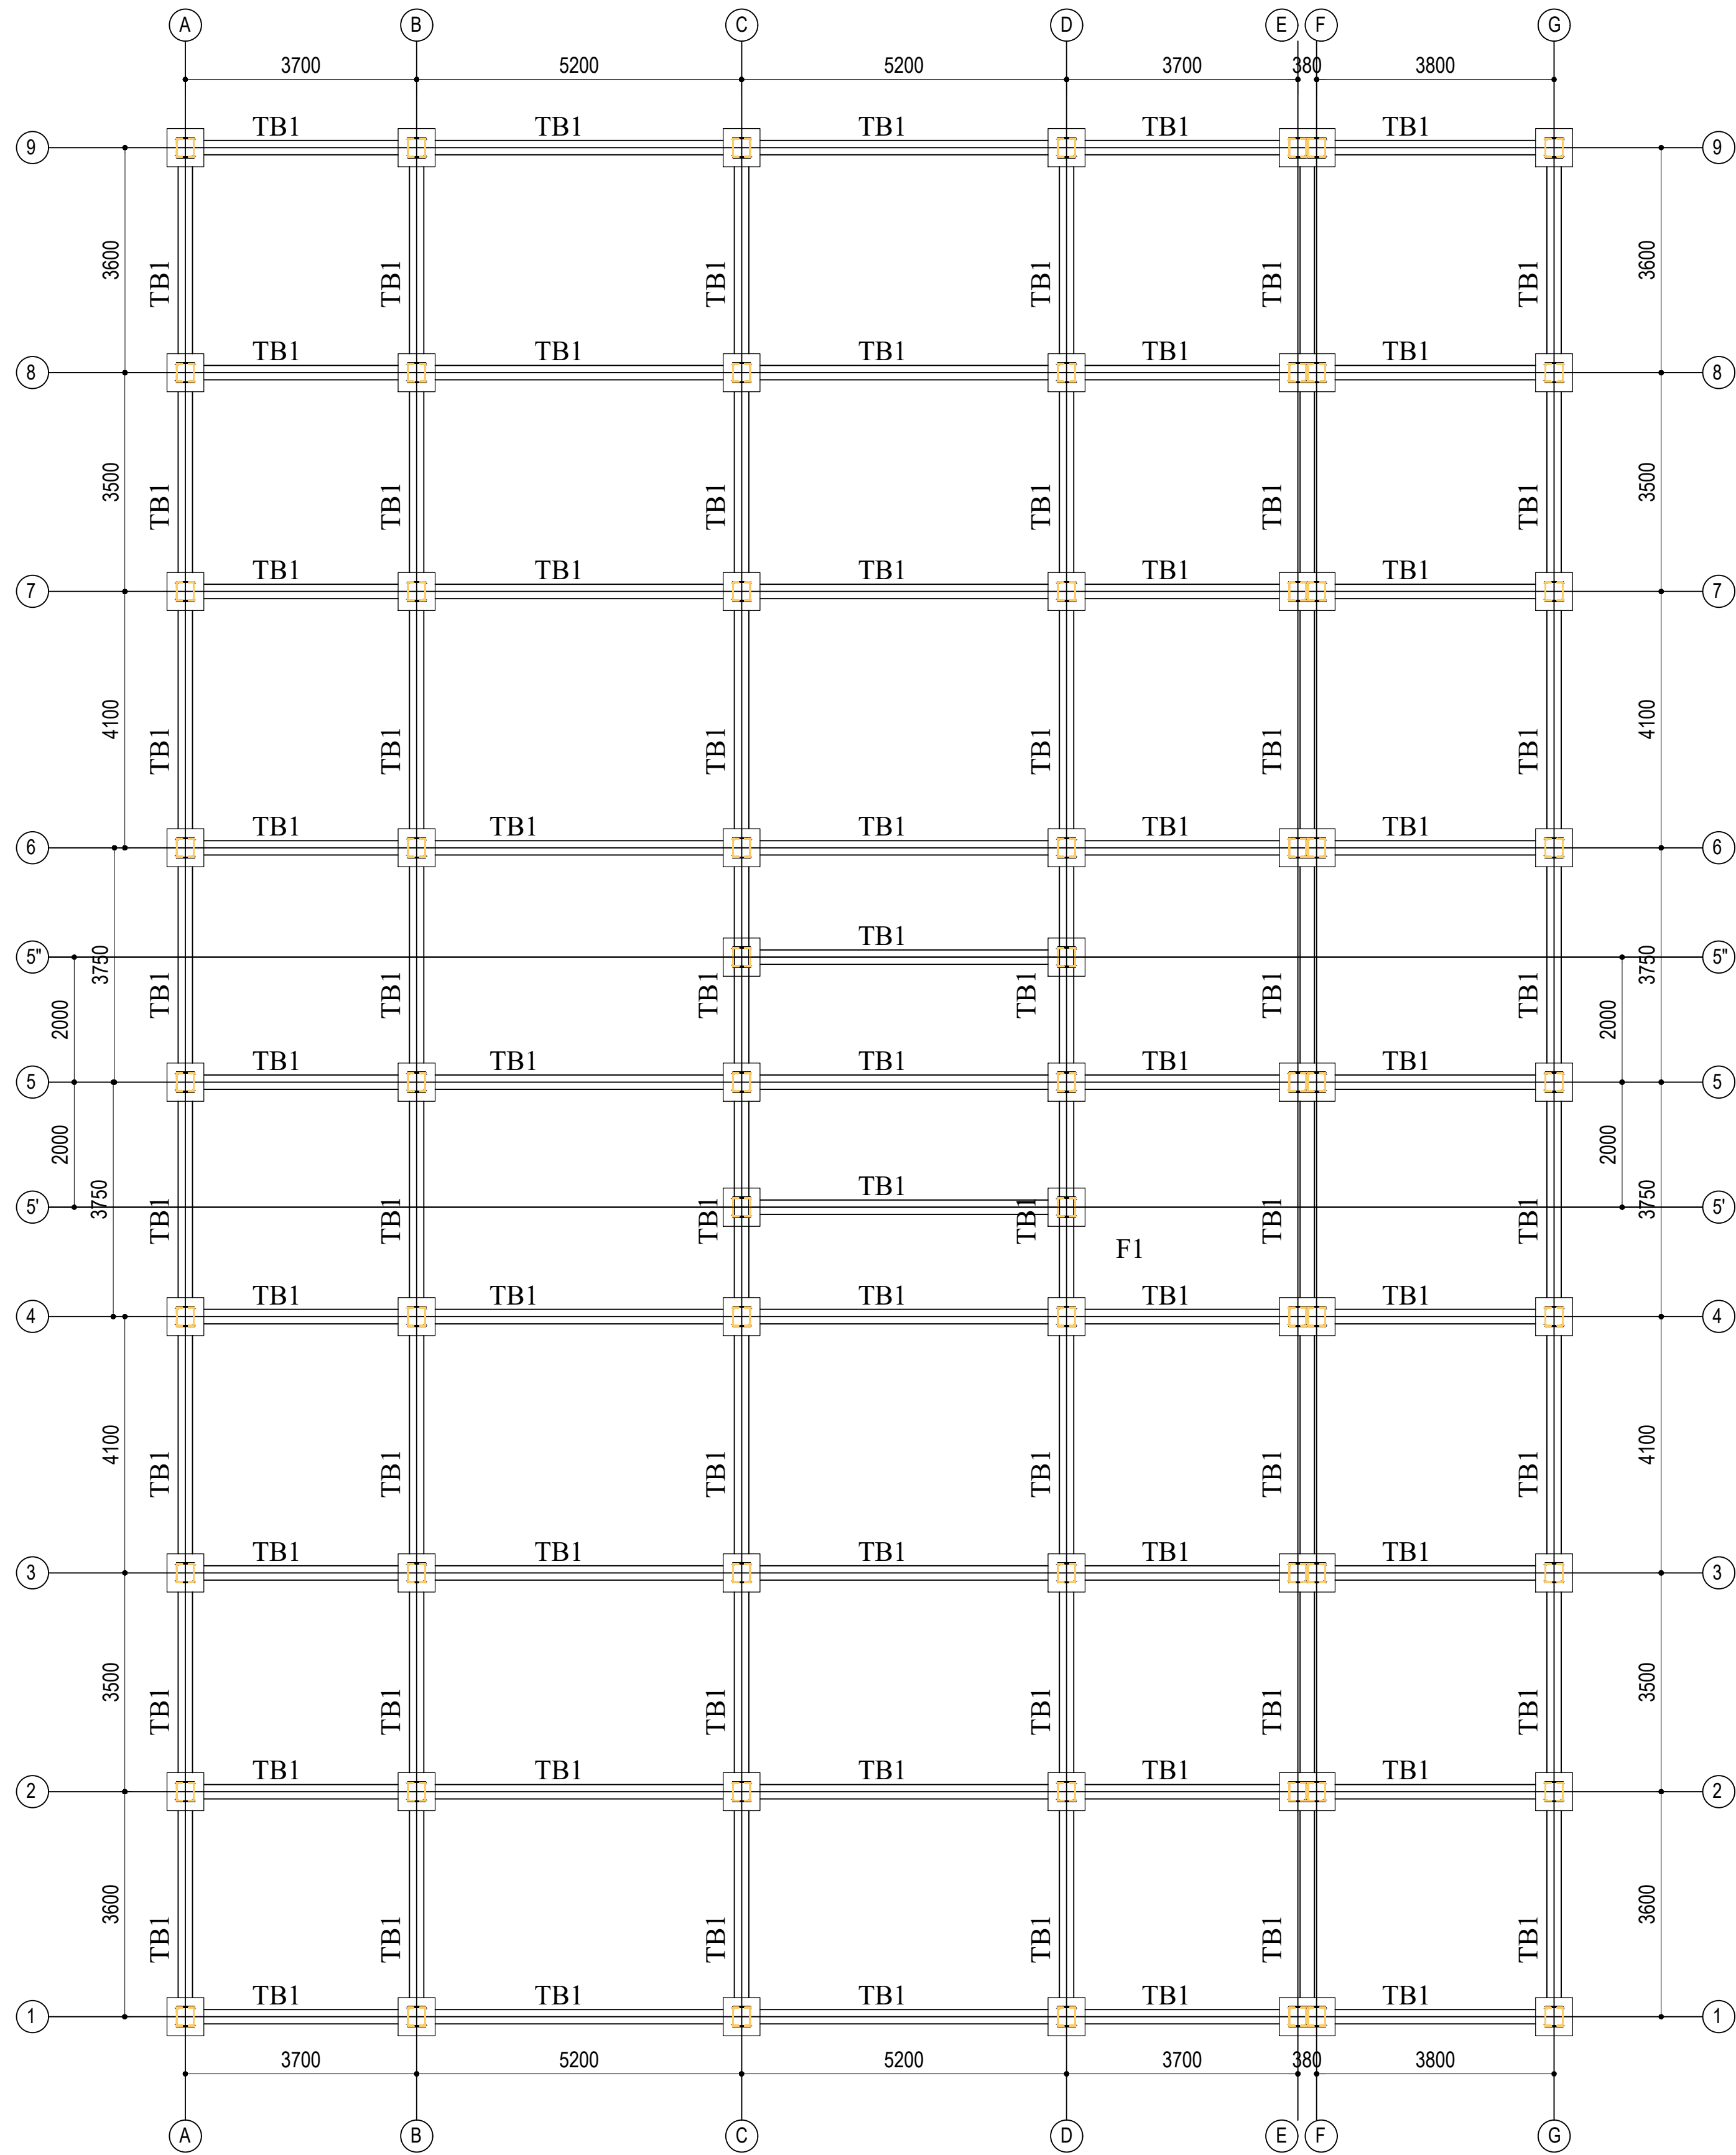


Tie Beam Layout Plan

PROJECT: DPR OF 500MT COLD STORE AT JIRI, DOLAKHA		CONTENT: STRUCTURAL DRAWINGS		CHECKED BY: APPROVED BY :		CONSULTANT: Sworaj Consultants Pvt. Ltd. Samakhushi, Kathmandu		Sheet No	
CLIENT: Government of Province Ministry of Land Management, Agriculture and Cooperative Province No. 3, Hetauda		FINAL DRAWING		SCALE :				ST 07	
				DATE: REVISION:					

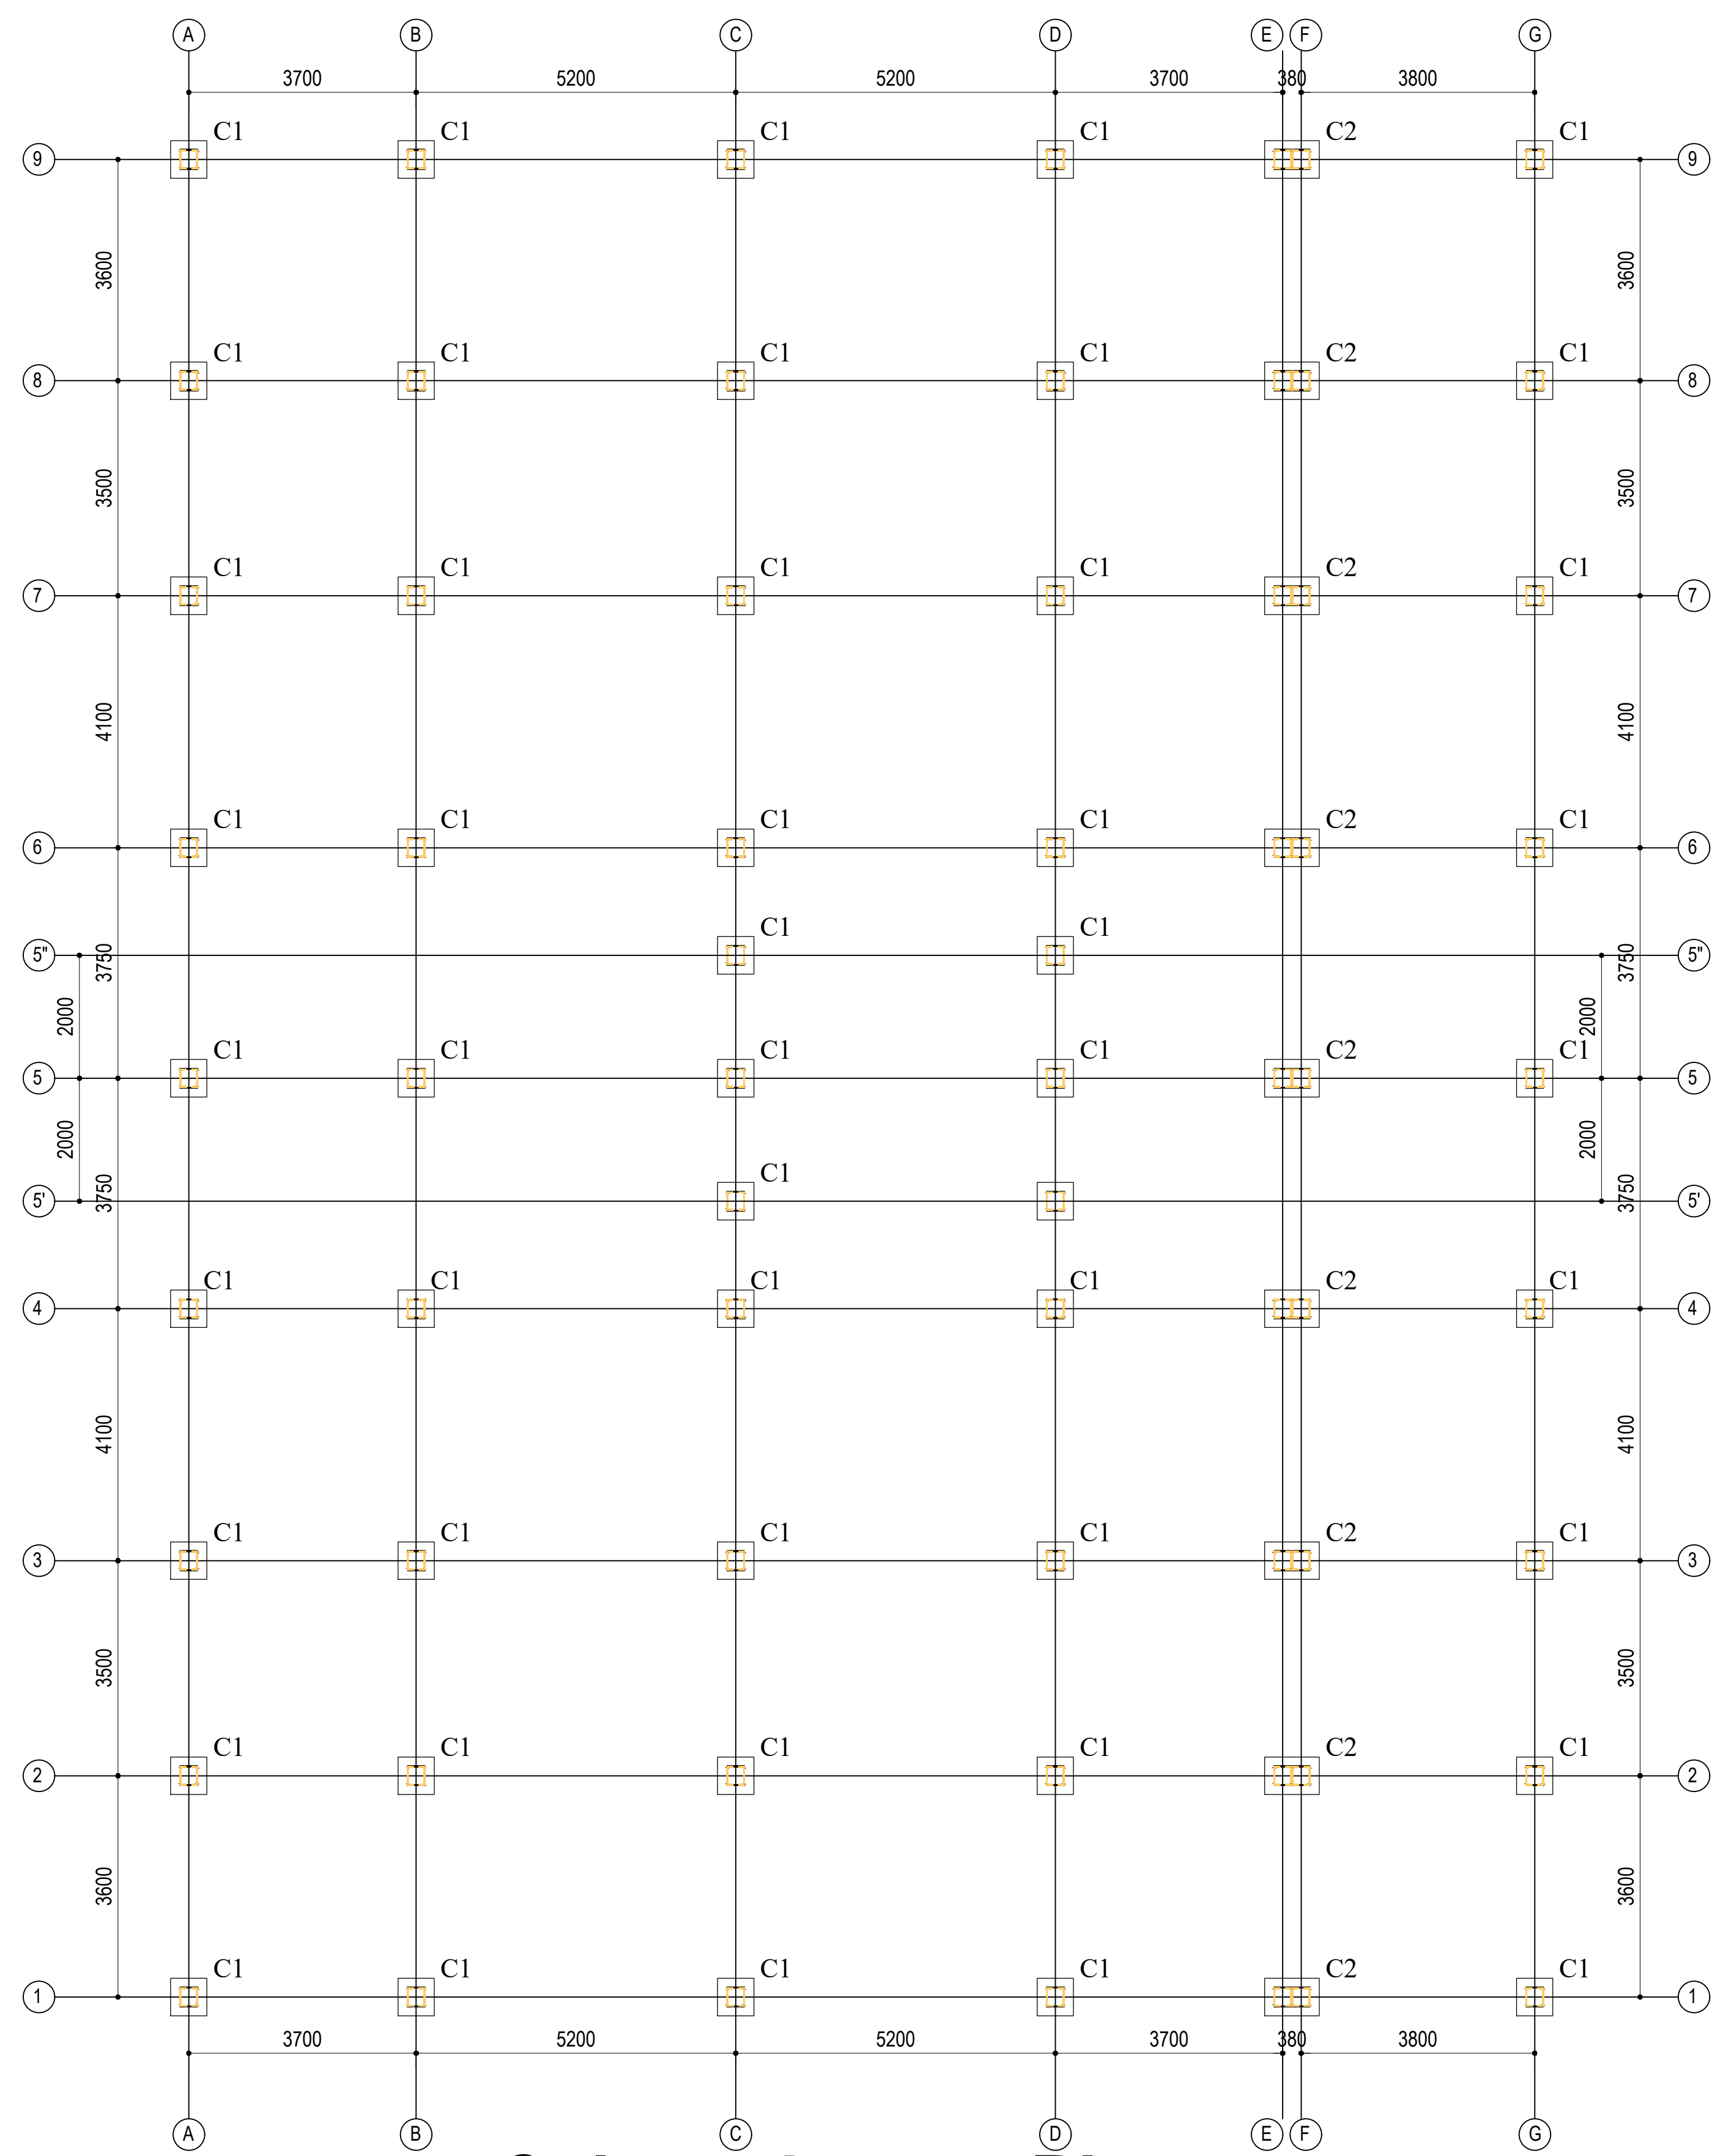


Column Layout Plan

PROJECT: DPR OF 500MT COLD STORE AT JIRI, DOLAKHA		CONTENT: STRUCTURAL DRAWINGS		CHECKED BY: APPROVED BY :		CONSULTANT: Sworaj Consultants Pvt. Ltd. Samakhushi, Kathmandu		Sheet No	
CLIENT: Government of Province Ministry of Land Management, Agriculture and Cooperative Province No. 3, Hetauda		FINAL DRAWING		SCALE :				ST 08	
				DATE: REVISION:					

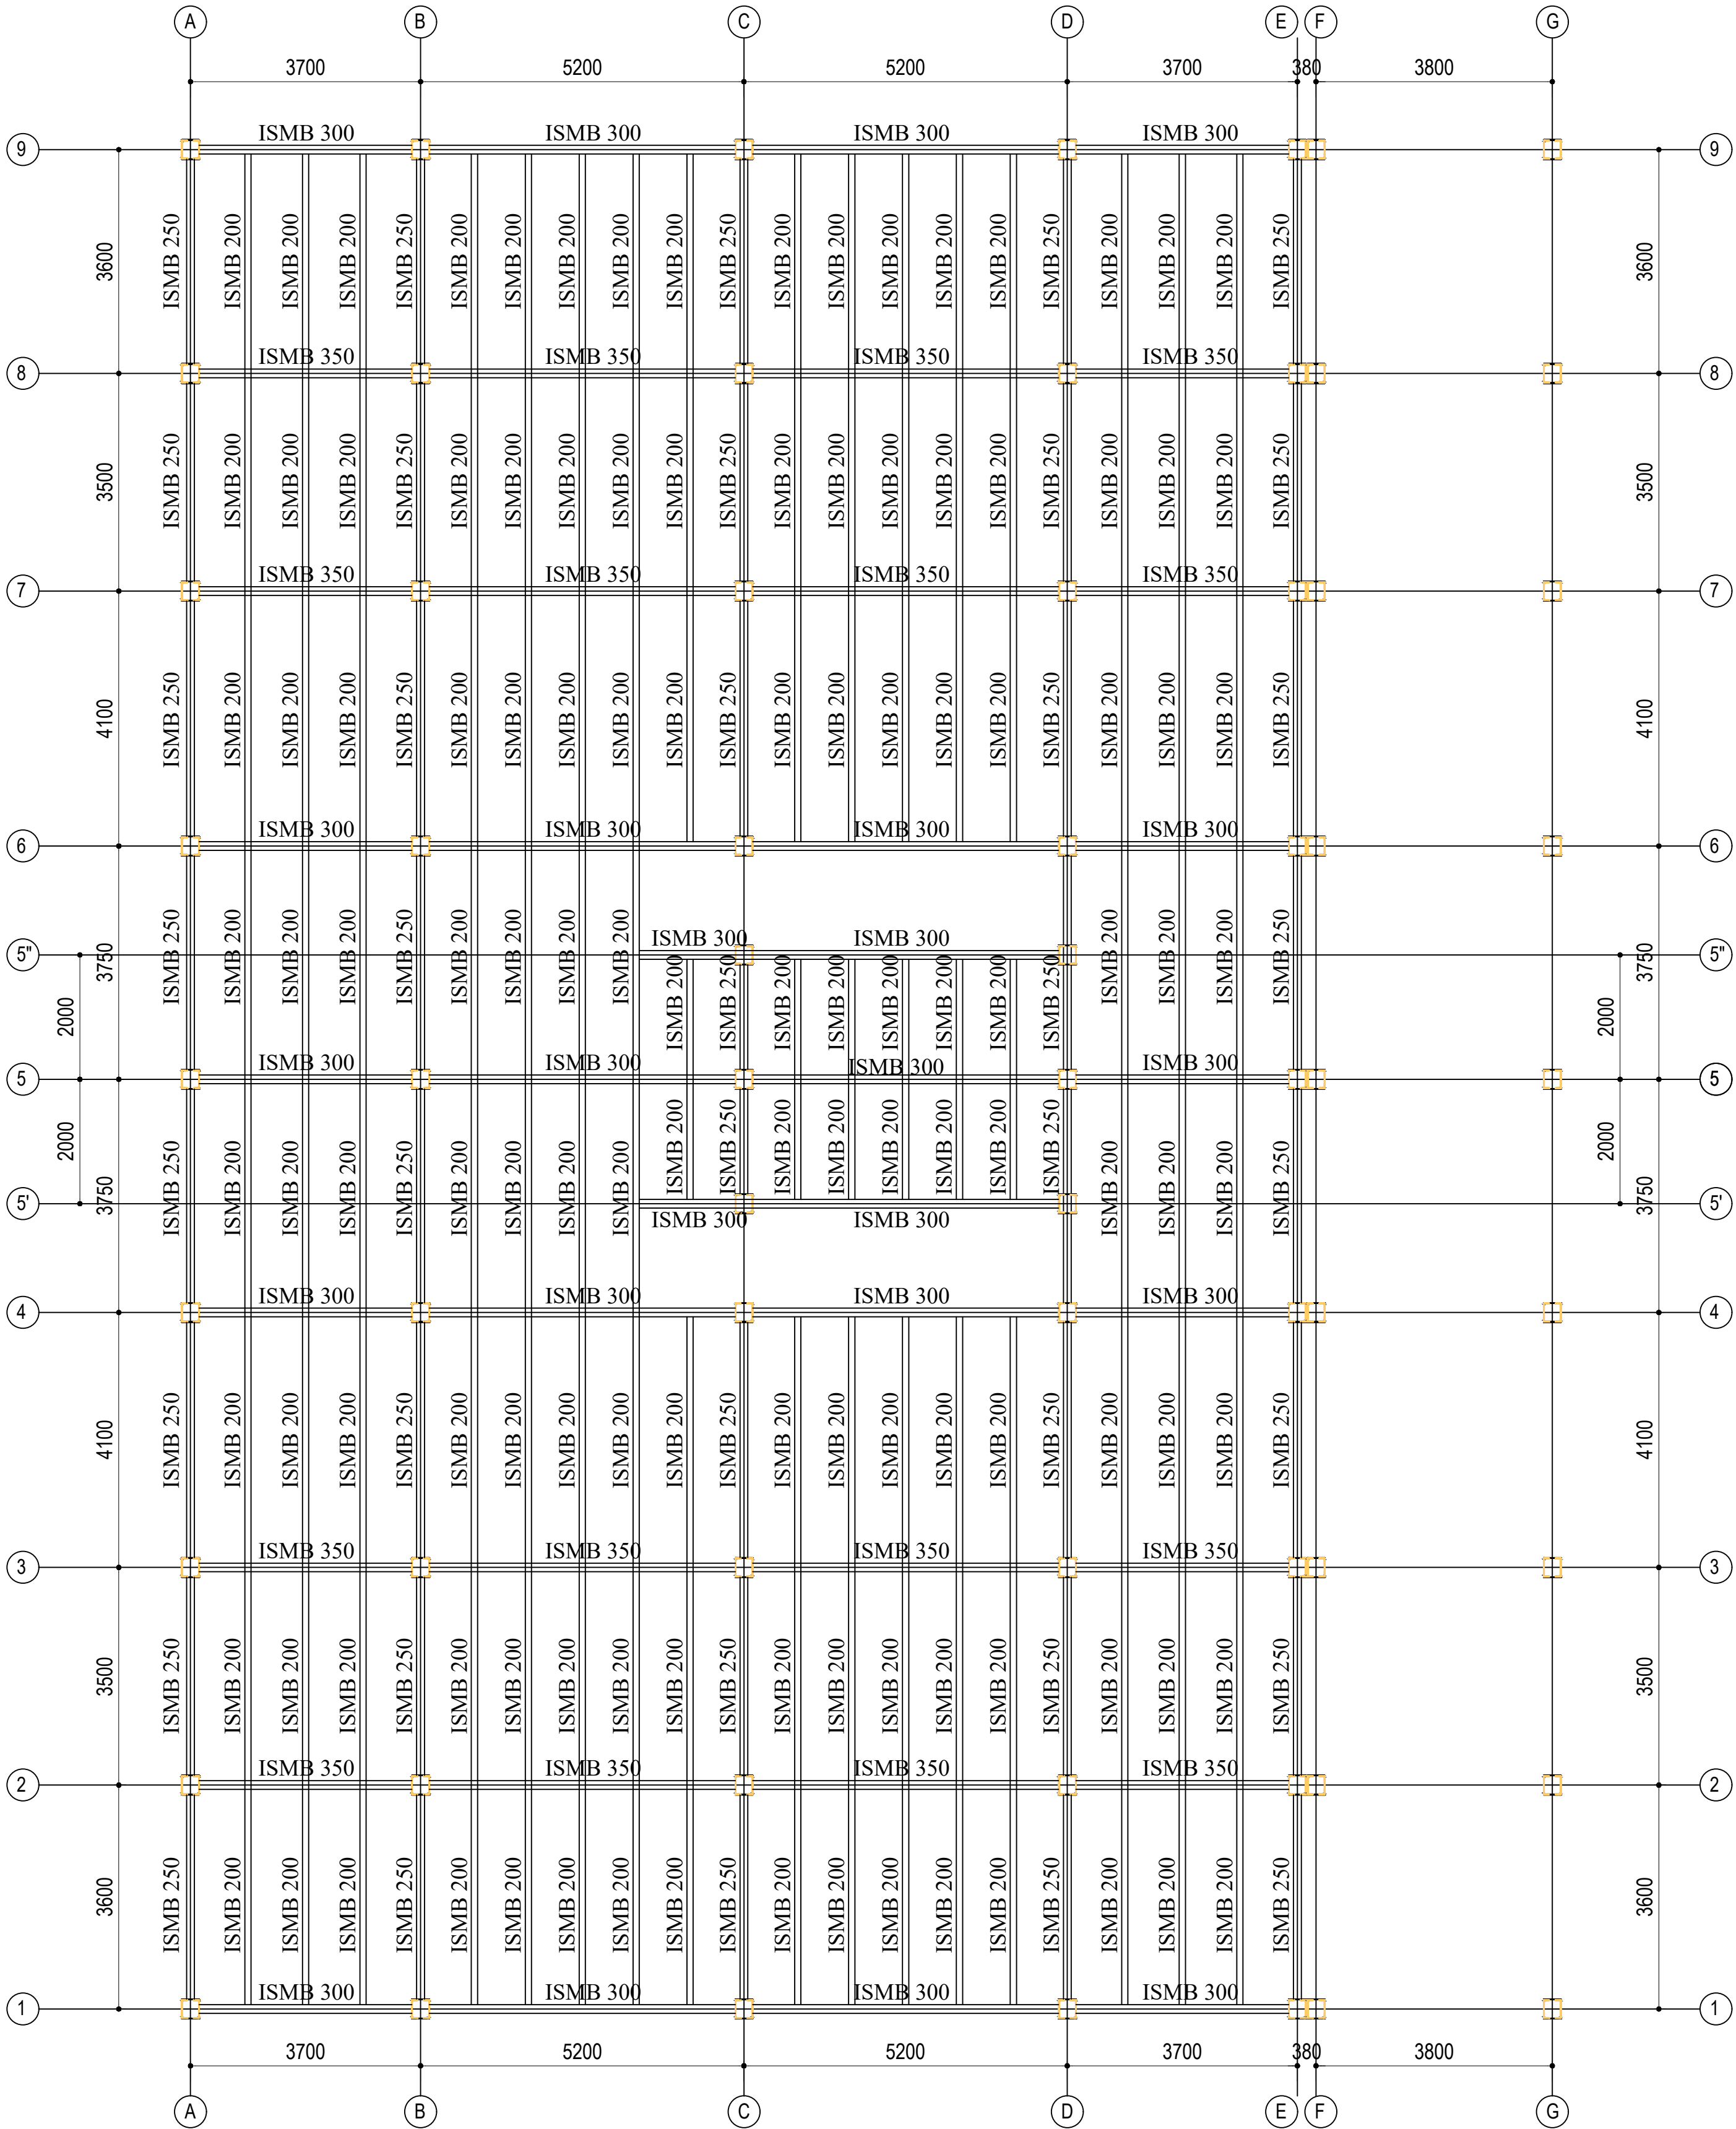


First Floor Beam Layout Plan


PROJECT: DPR OF 500MT COLD STORE AT JIRI, DOLAKHA		CONTENT: STRUCTURAL DRAWINGS	CHECKED BY:		CONSULTANT: Sworaj Consultants Pvt. Ltd. Samakhushi, Kathmandu	Sheet No ST 09
CLIENT: Government of Province Ministry of Land Management, Agriculture and Cooperative Province No. 3, Hetauda			APPROVED BY :			
			SCALE :			
			DATE:	REVISION:		

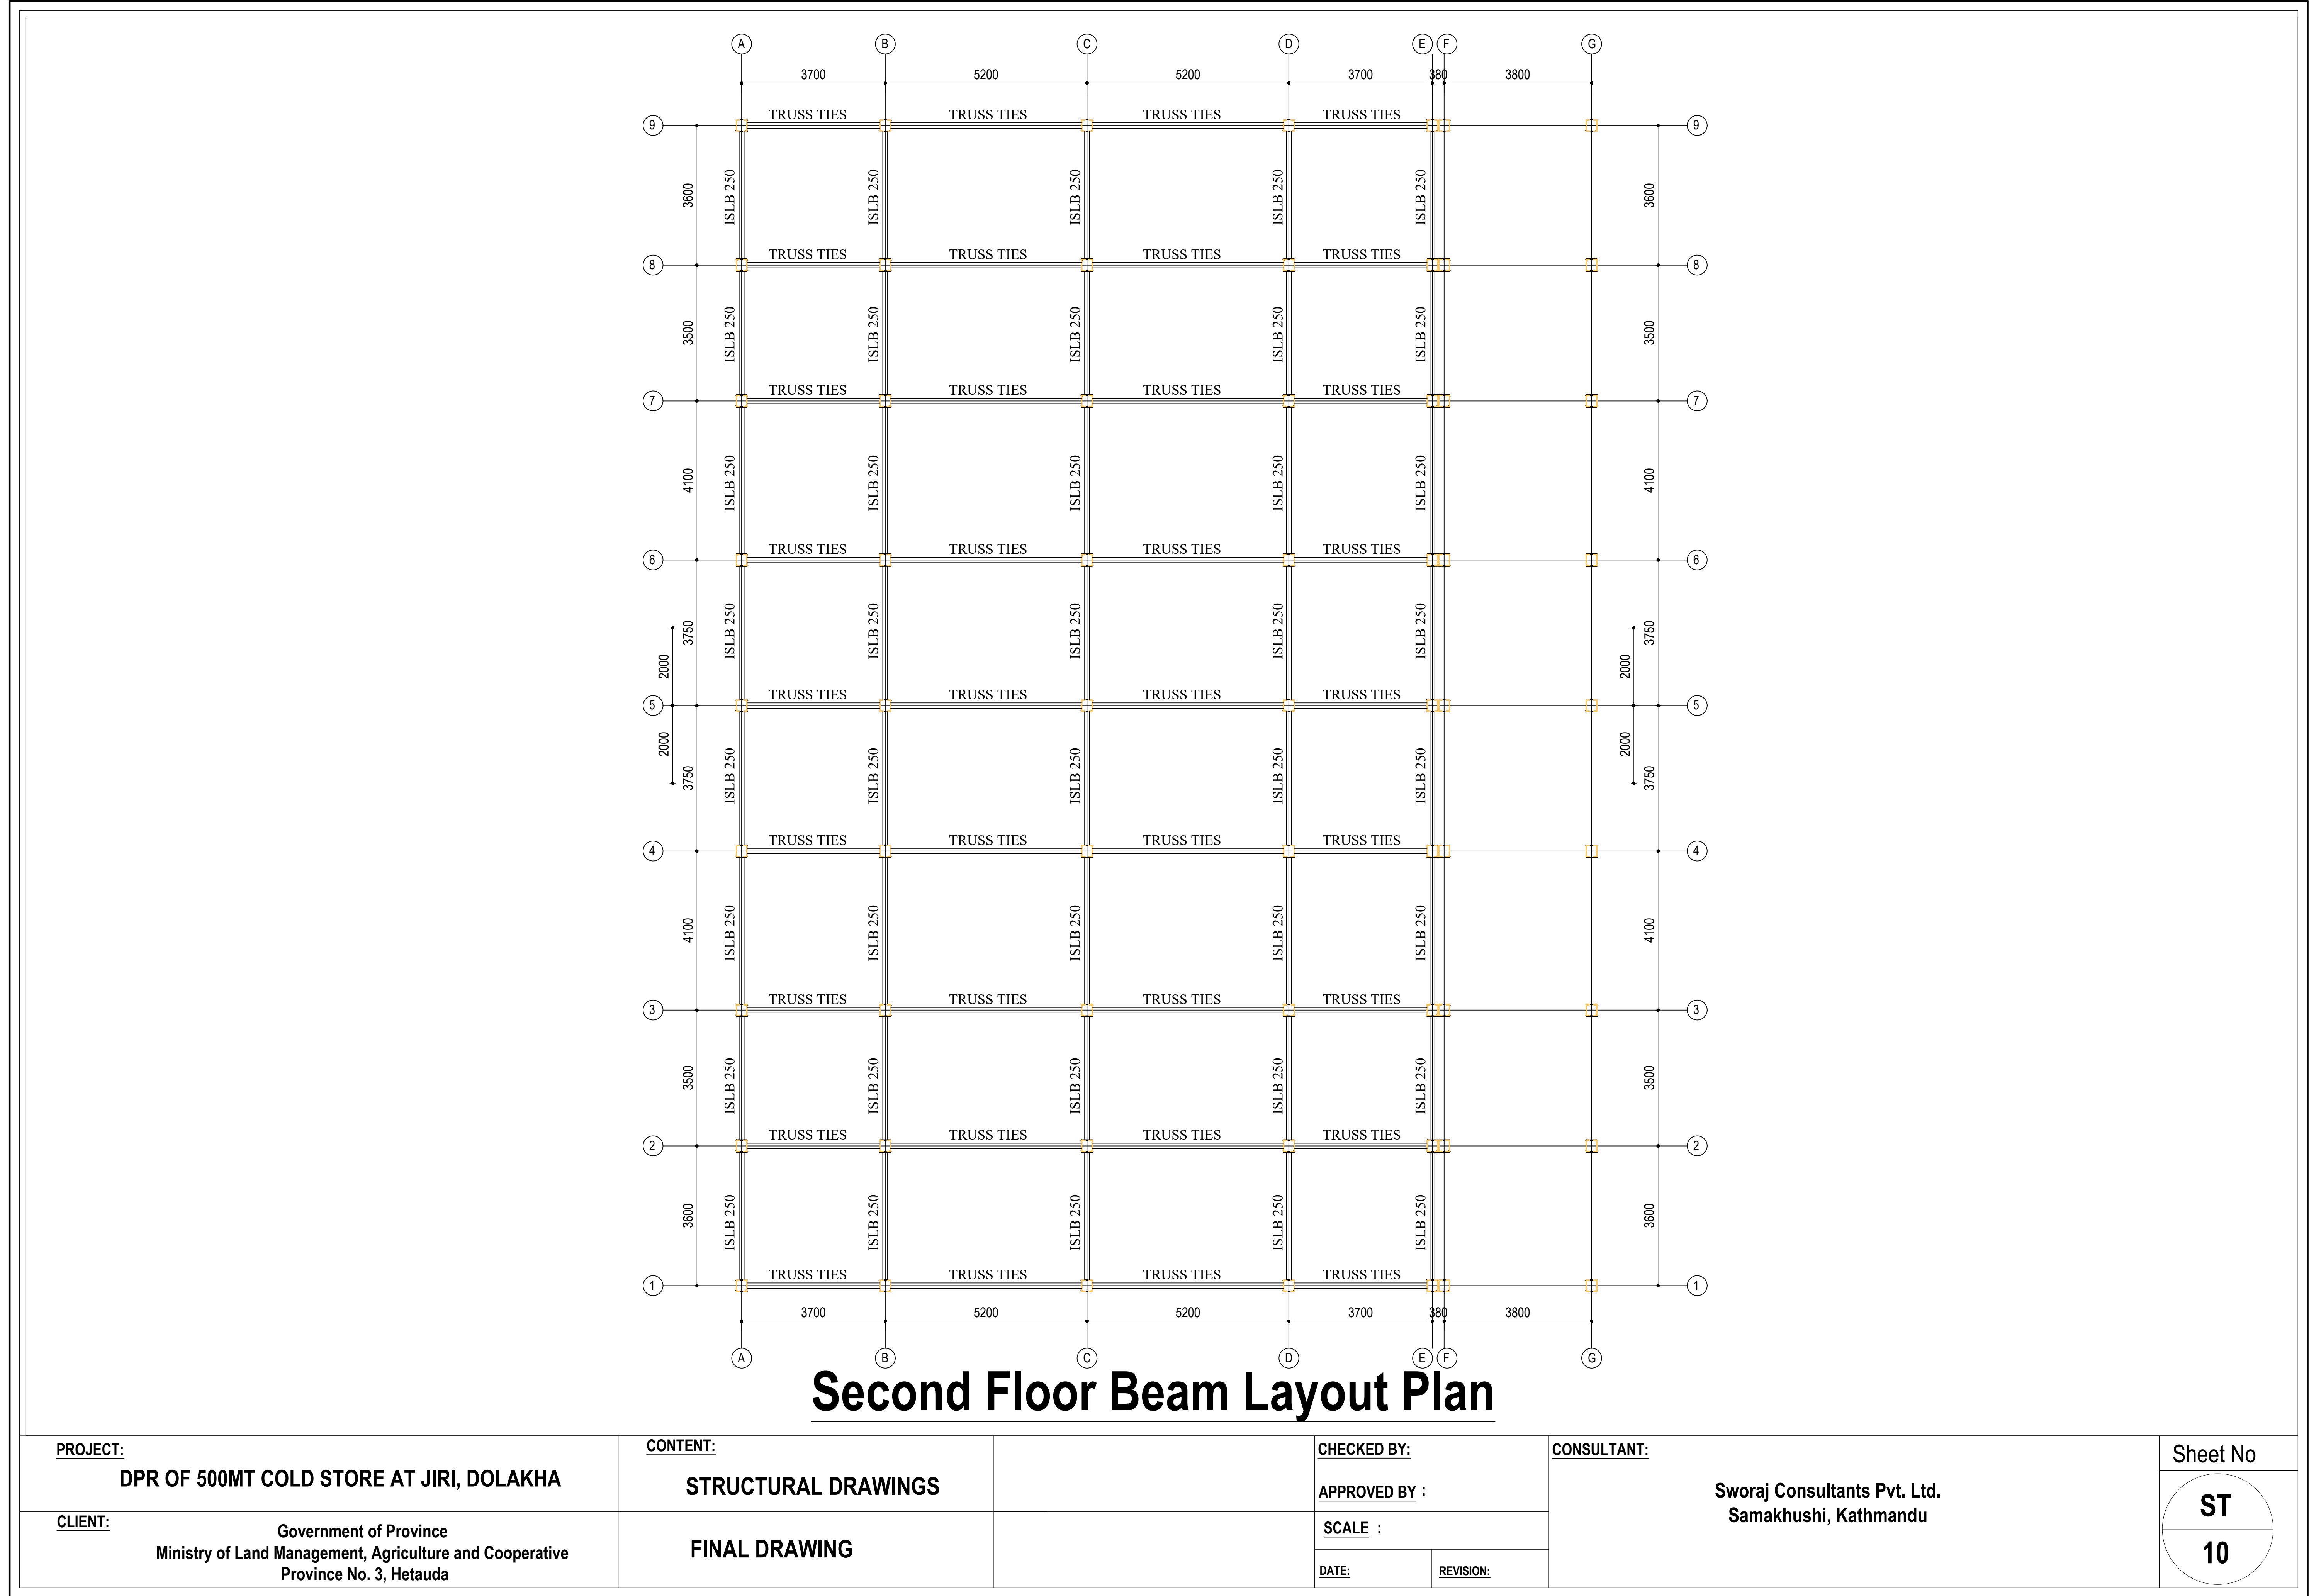


PROJECT: DPR OF 500MT COLD STORE AT JIRI, DOLAKHA	CONTENT: STRUCTURAL DRAWINGS		CHECKED BY: APPROVED BY :	CONSULTANT: Sworaj Consultants Pvt. Ltd. Samakhushi, Kathmandu	Sheet No
CLIENT: Government of Province Ministry of Land Management, Agriculture and Cooperative Province No. 3, Hetauda	FINAL DRAWING		SCALE :		ST 10
		DATE:	REVISION:		

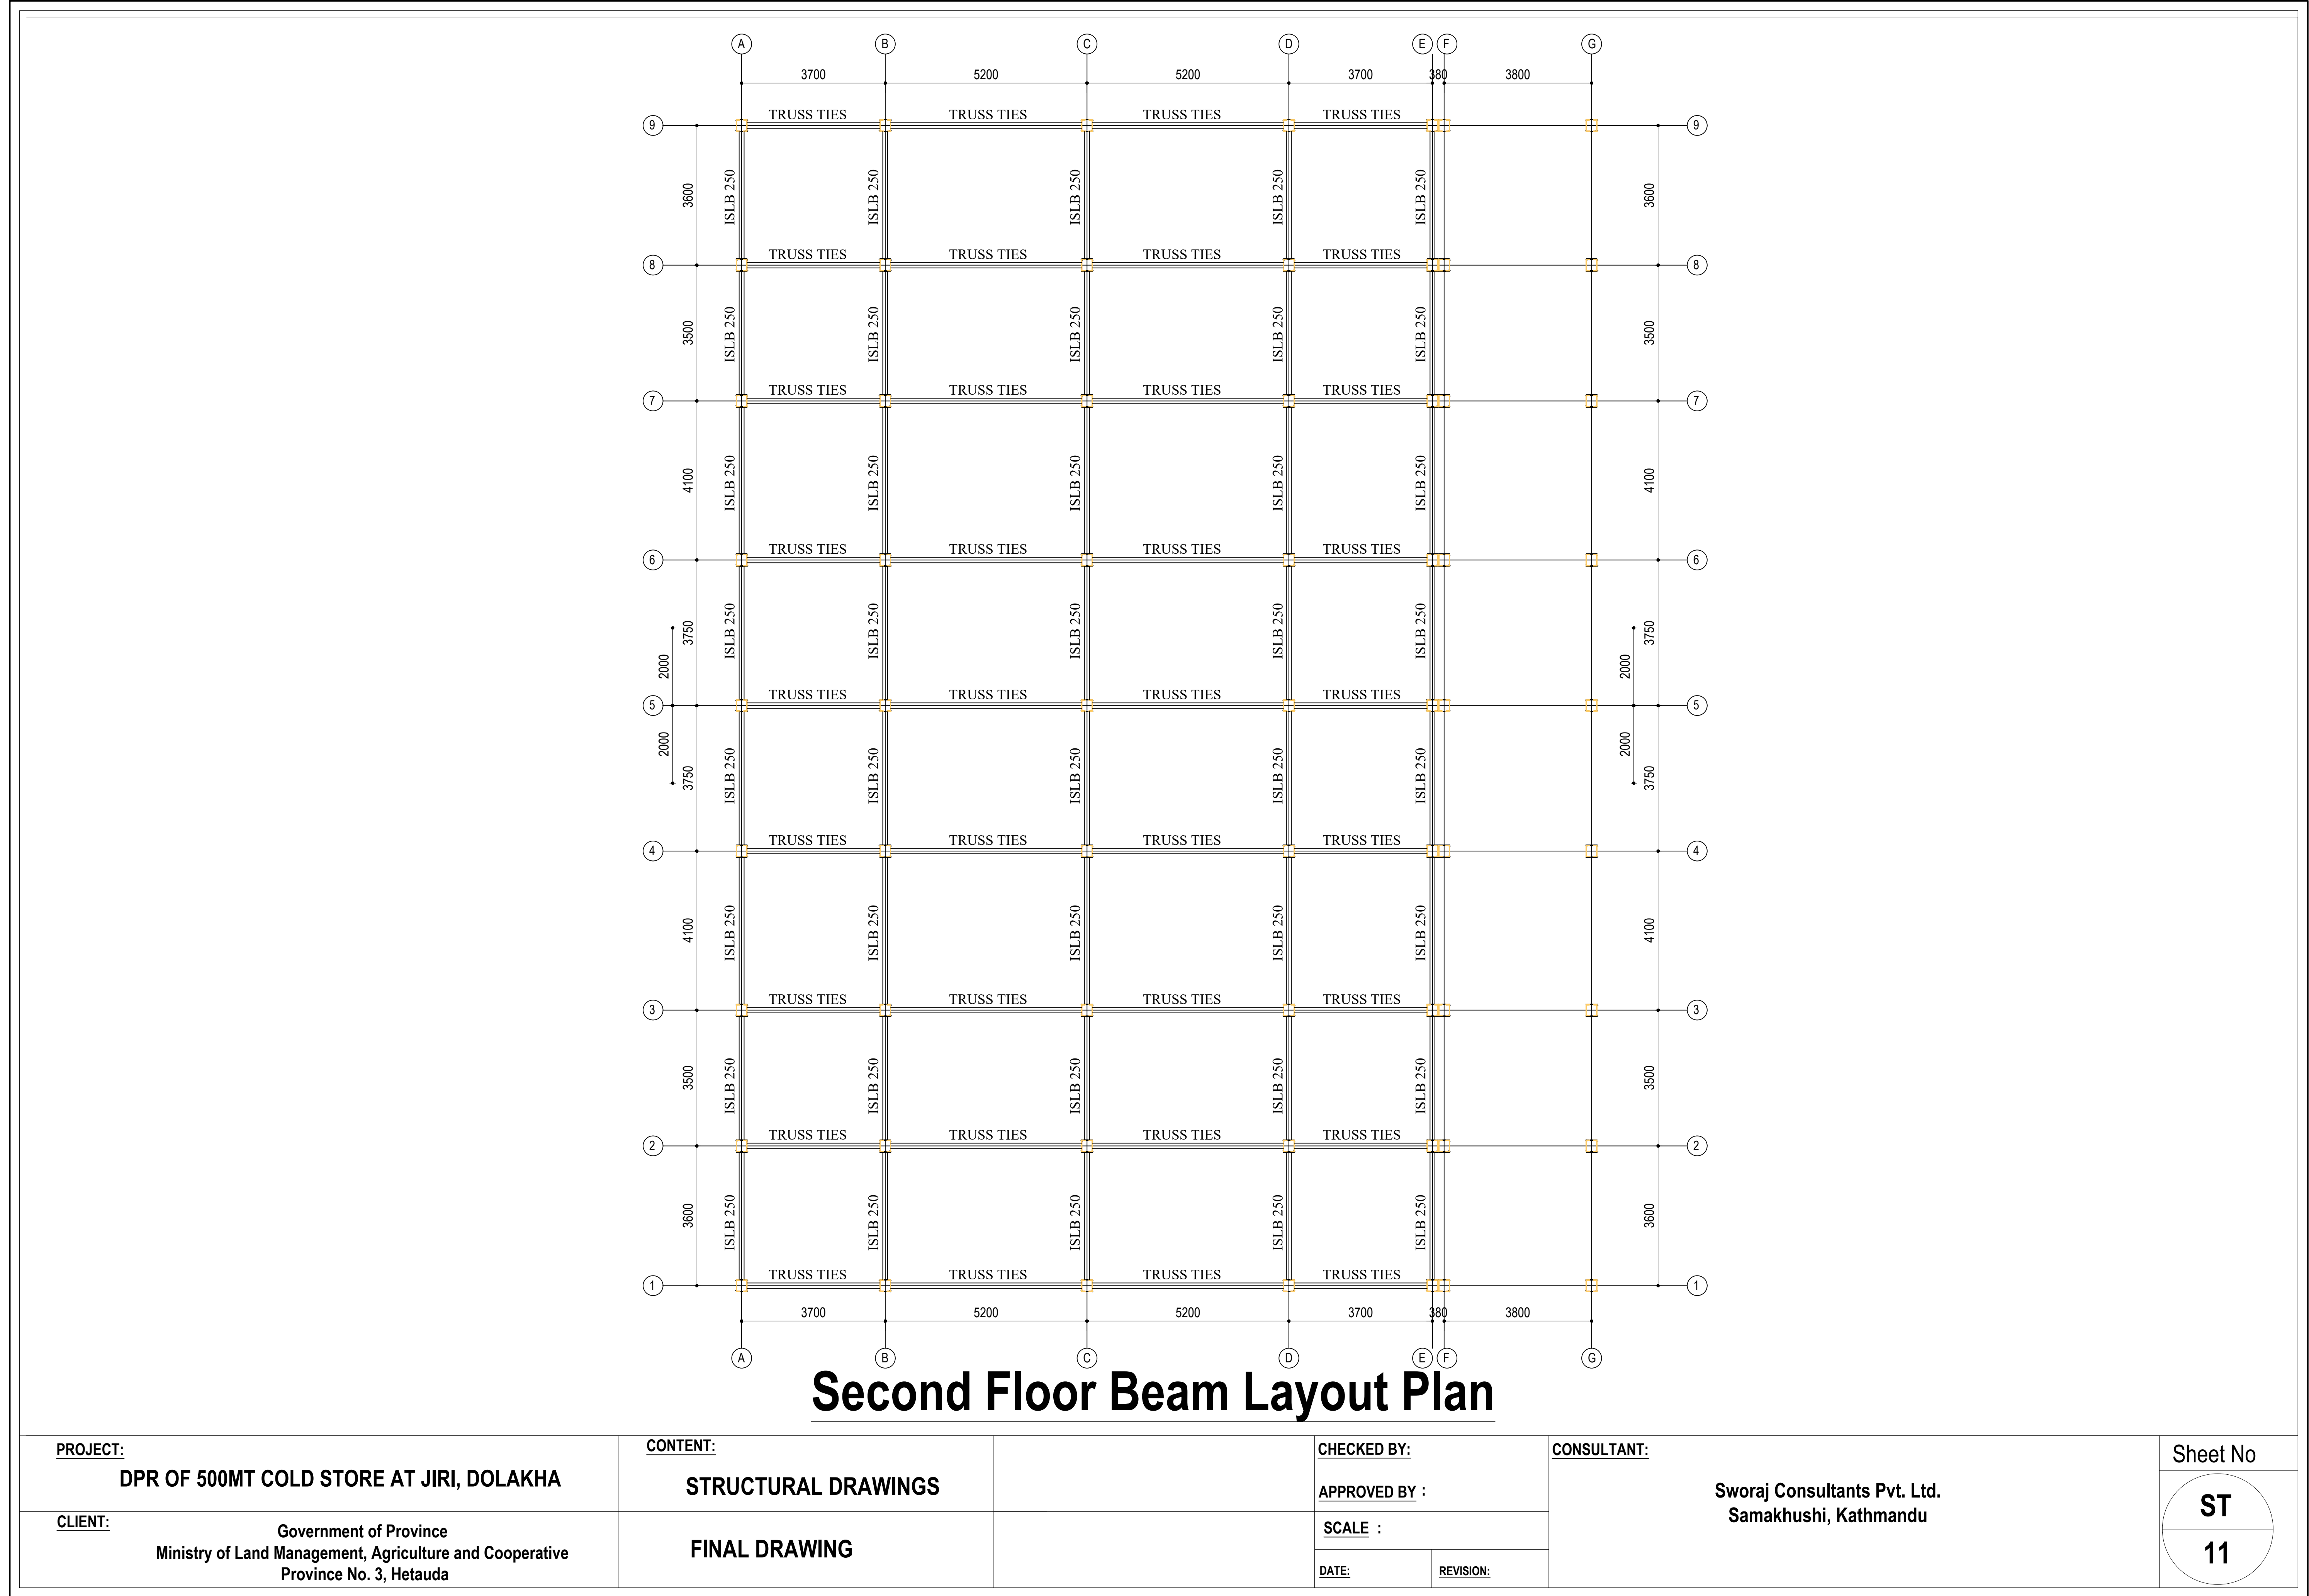

PROJECT: DPR OF 500MT COLD STORE AT JIRI, DOLAKHA	CONTENT: STRUCTURAL DRAWINGS		CHECKED BY: APPROVED BY :	CONSULTANT: Sworaj Consultants Pvt. Ltd. Samakhushi, Kathmandu	Sheet No ST 11
CLIENT: Government of Province Ministry of Land Management, Agriculture and Cooperative Province No. 3, Hetauda	FINAL DRAWING	SCALE :			
		DATE: REVISION:			

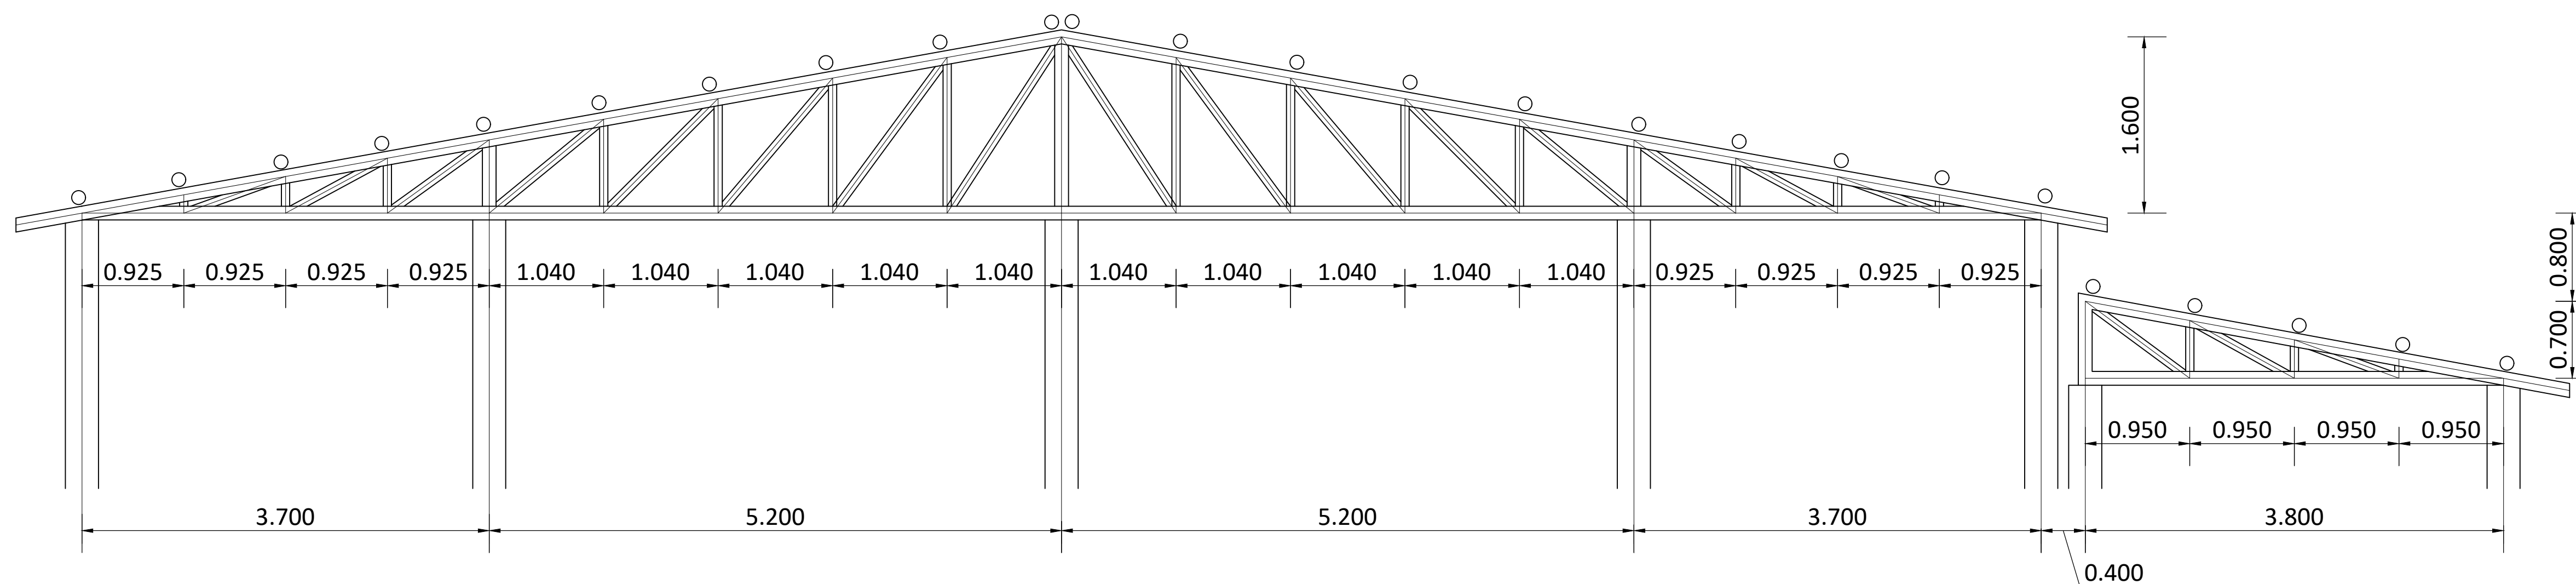



TRUSS ROOF ARRANGEMENT

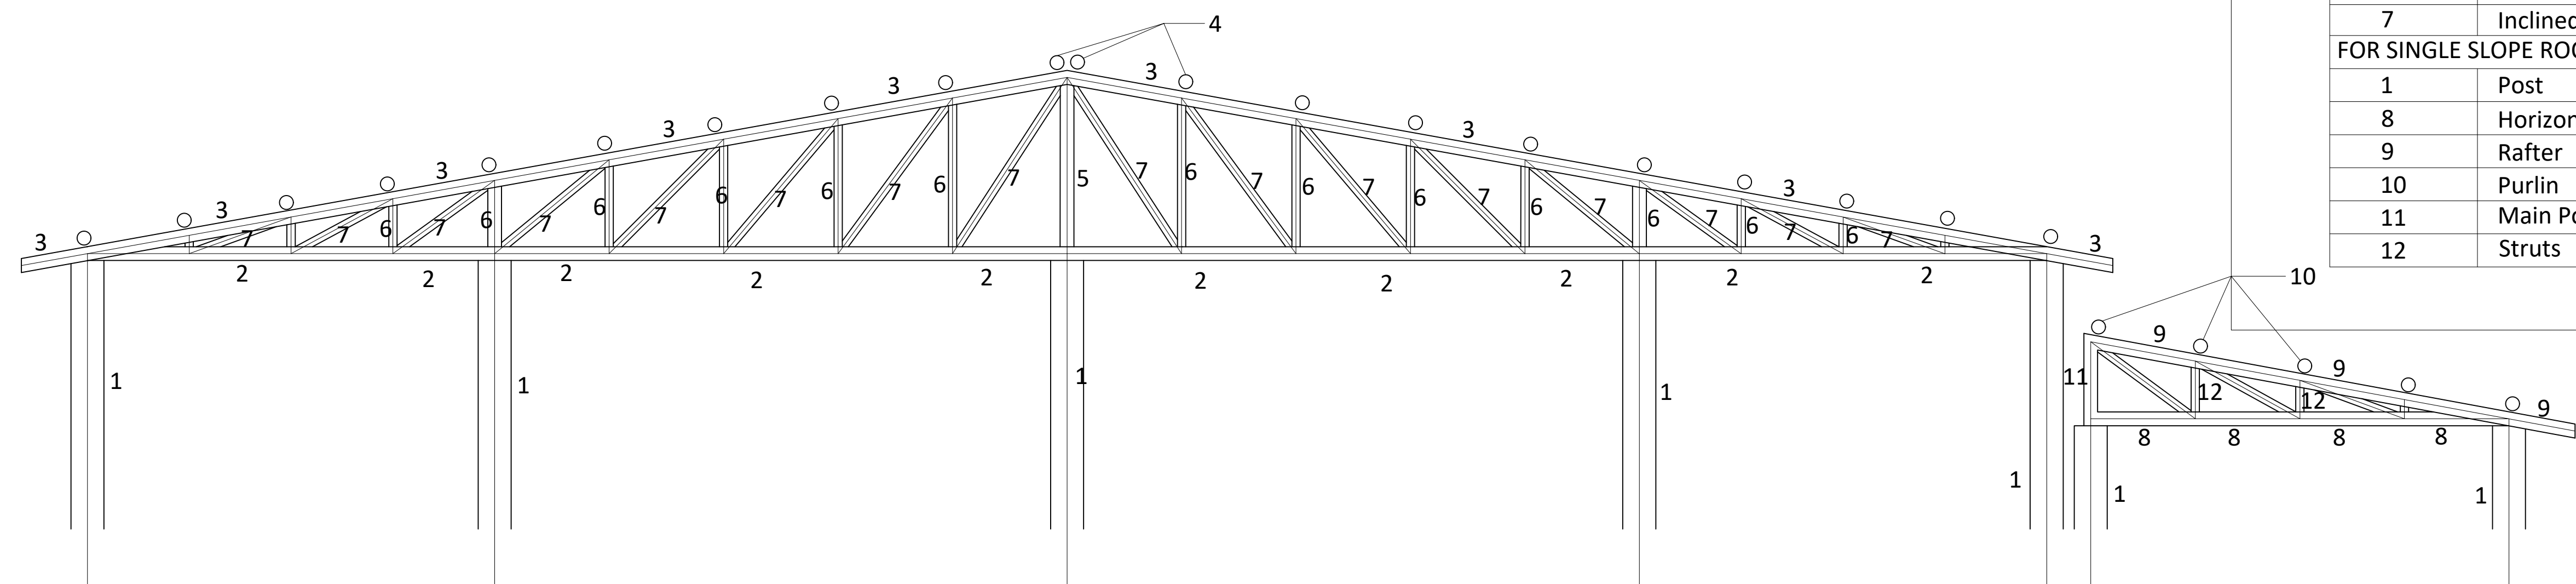


MONO SLOPE ROOF MEMBER DETAIL

FOR DOUBLE SLOPE ROOF		
Member No.	Member Identification	Member Specifiaction
1	Post	BUILT UP COLUMN C1
2	Horizontal ties of truss	ISNB 100M
3	Rafter	ISNB 100M
4	Purlin	ISNB 80M
5	King Post	ISNB 125M
6	Vertical struts	ISNB 65M
7	Inclined struts	ISNB 65M
FOR SINGLE SLOPE ROOF		
1	Post	BUILT UP COLUMN C1
8	Horizontal ties of truss	ISNB 80M
9	Rafter	ISNB 80M
10	Purlin	ISNB 80M
11	Main Post	ISNB 80M
12	Struts	ISNB 65M


<u>PROJECT:</u> DPR OF 500MT COLD STORE AT JIRI, DOLAKHA		<u>CONTENT:</u> STRUCTURAL DRAWINGS	<u>CHECKED BY:</u>		<u>CONSULTANT:</u> Sworaj Consultants Pvt. Ltd. Samakhushi, Kathmandu	Sheet No
<u>CLIENT:</u> Government of Province Ministry of Land Management, Agriculture and Cooperative Province No. 3, Hetauda			<u>APPROVED BY :</u>			ST 12
			<u>SCALE :</u>			
			<u>DATE:</u>	<u>REVISION:</u>		

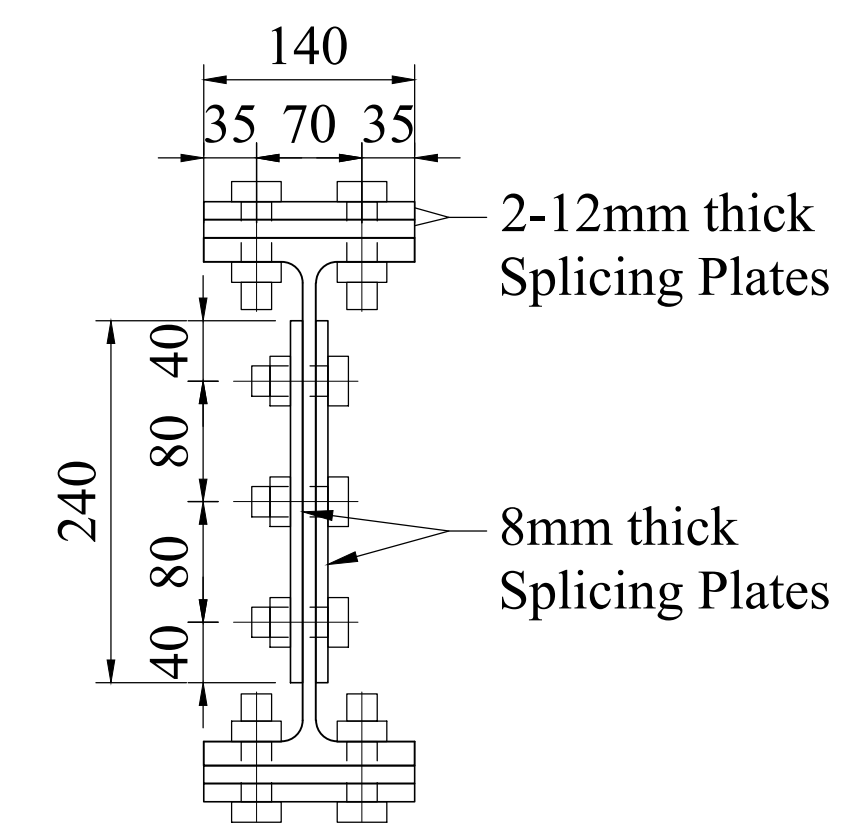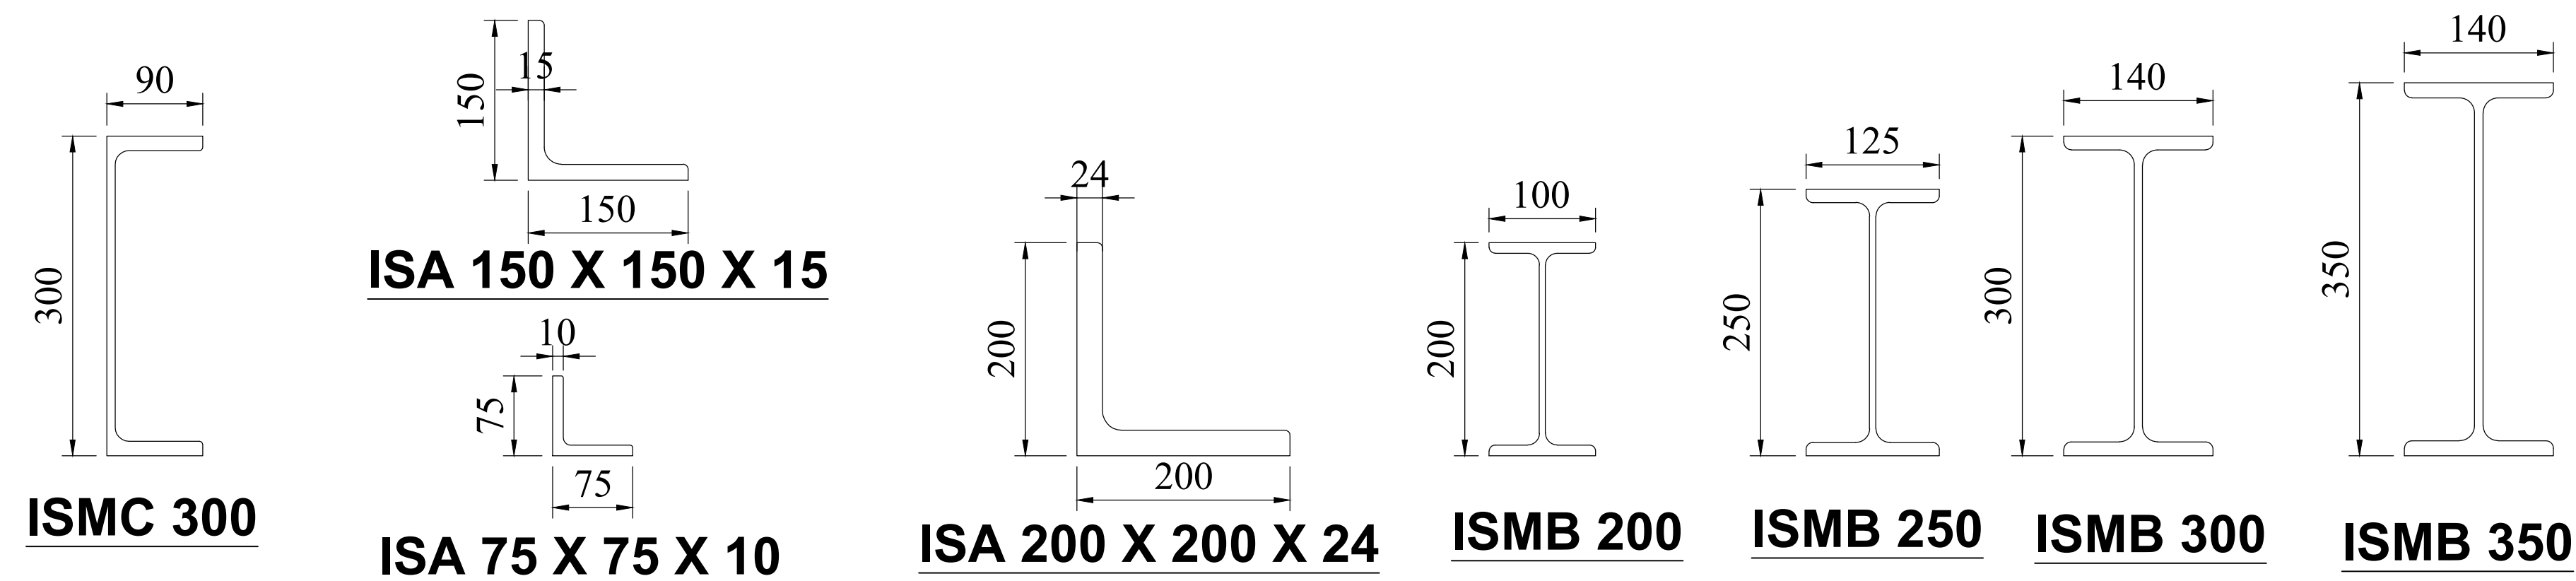


VIEW BS-A

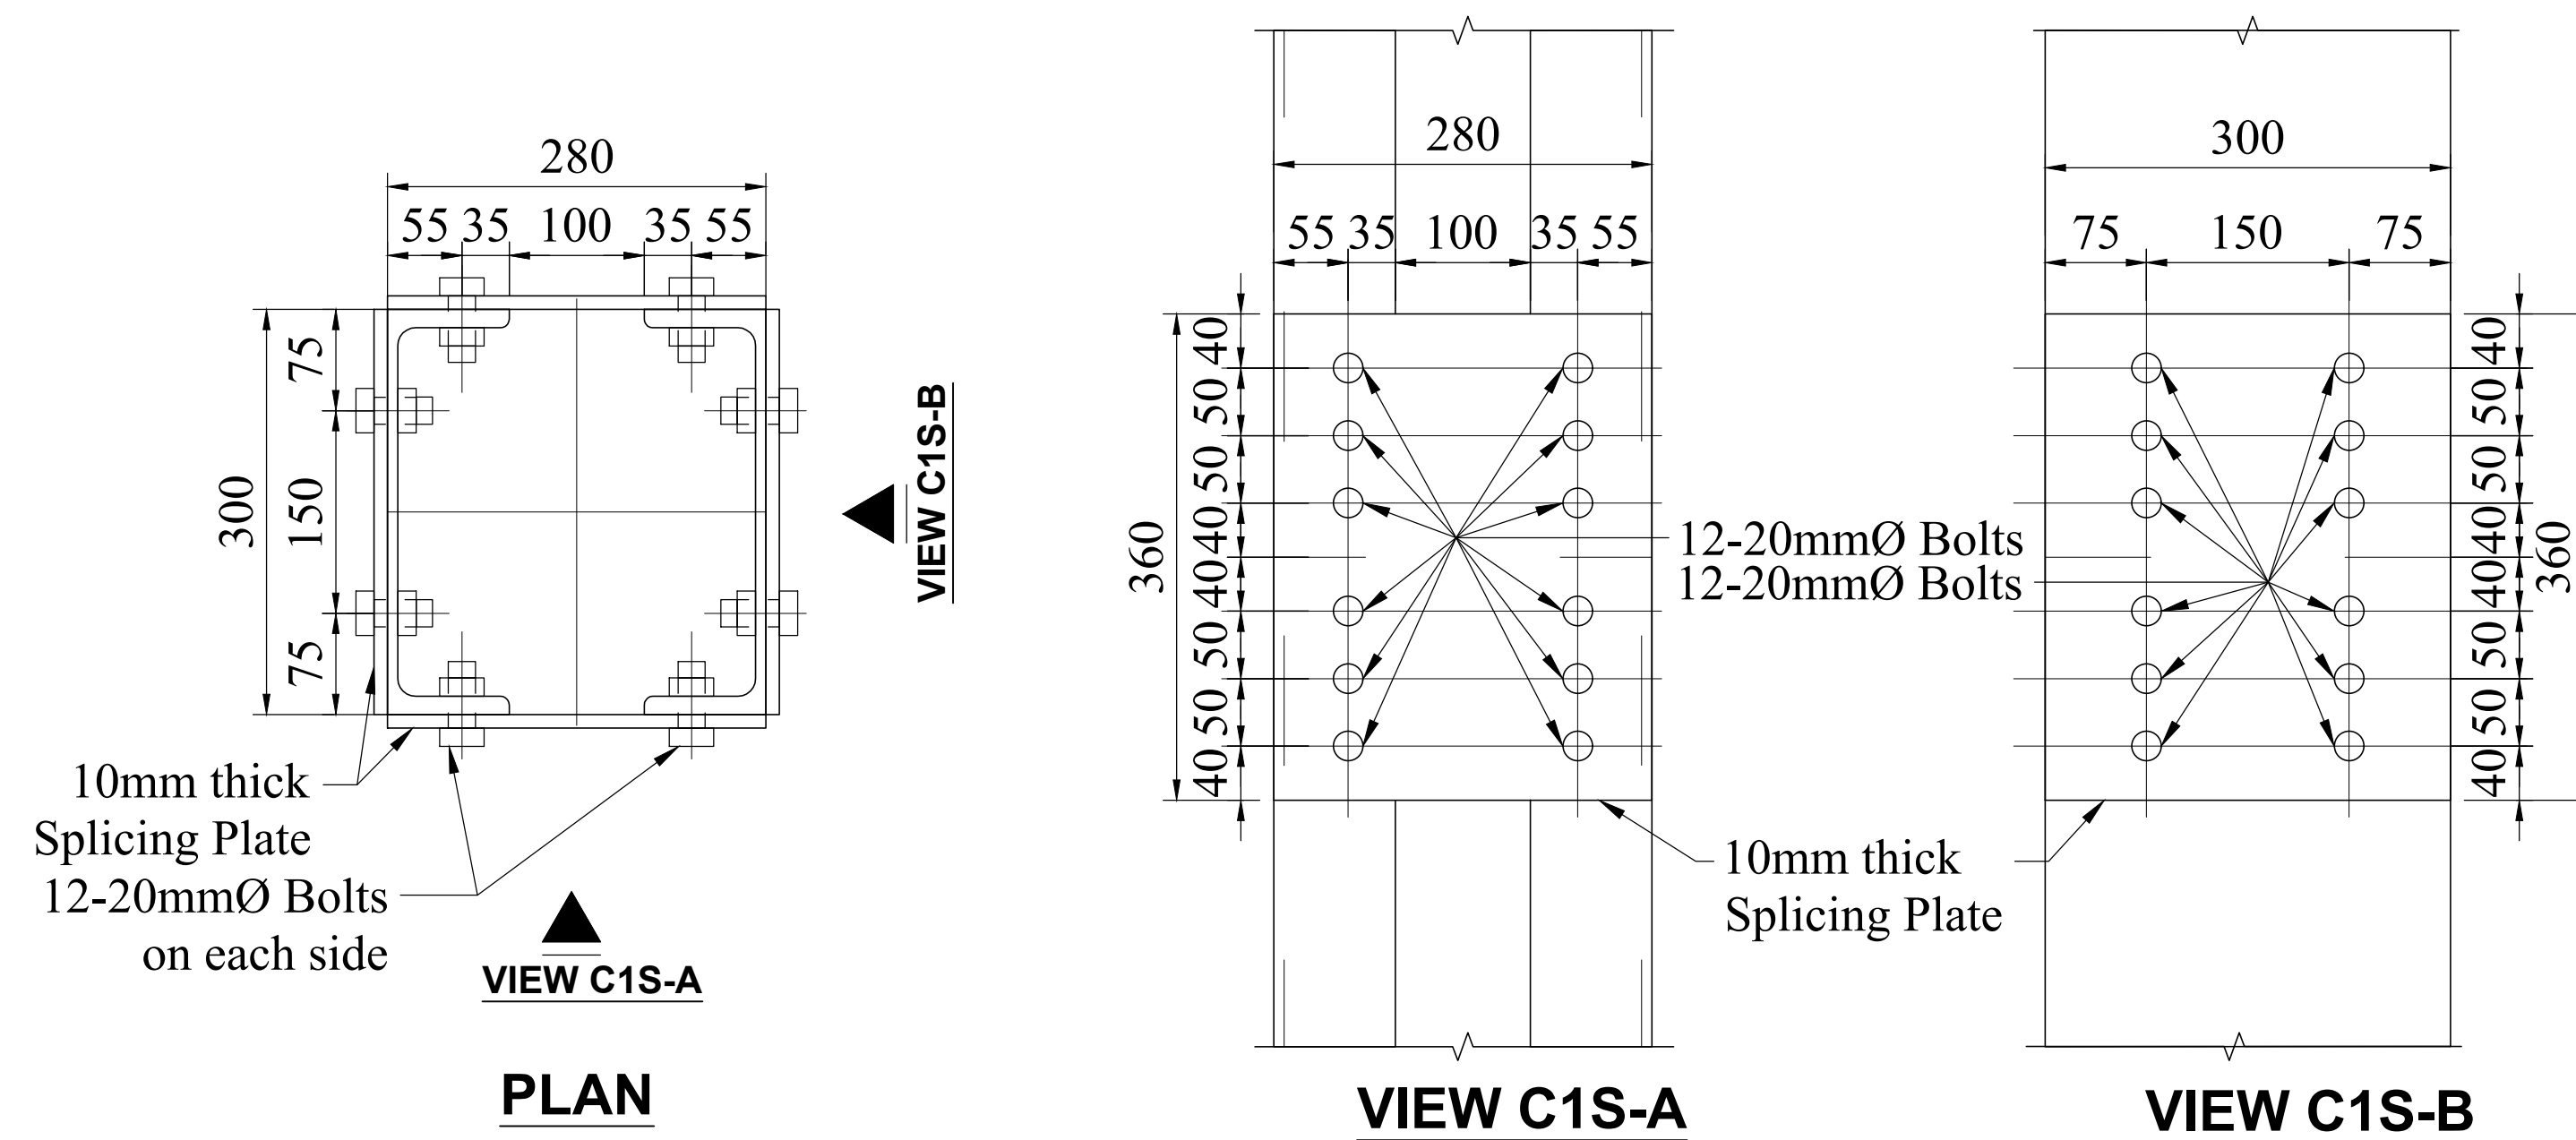

SPLICE FOR COLUMN-C1

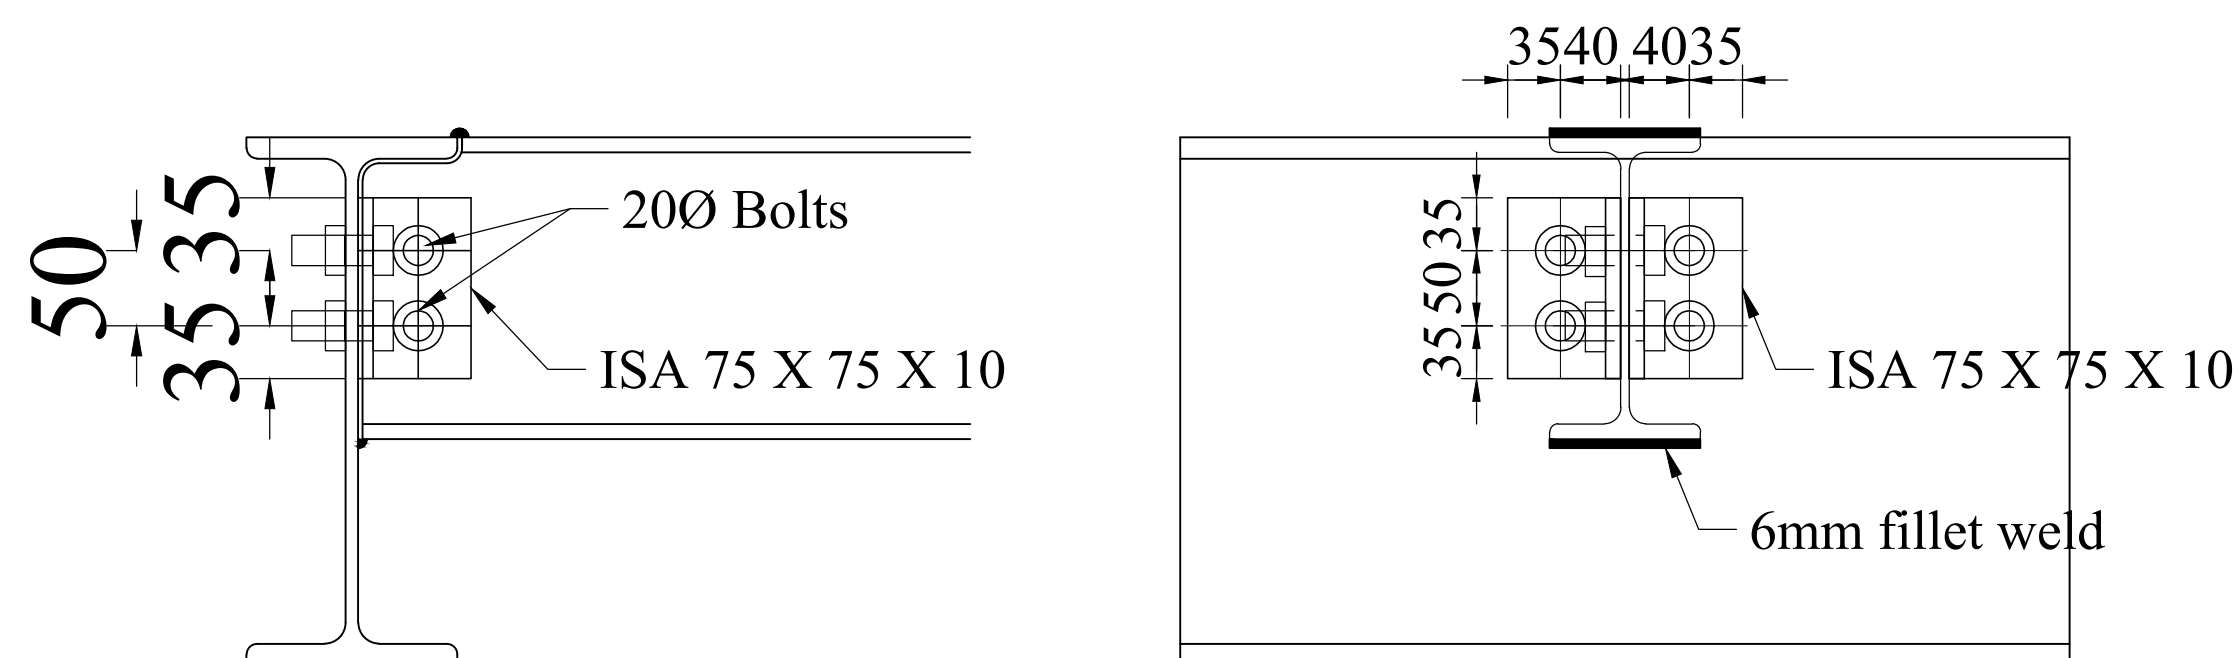


Beam - Beam Connection

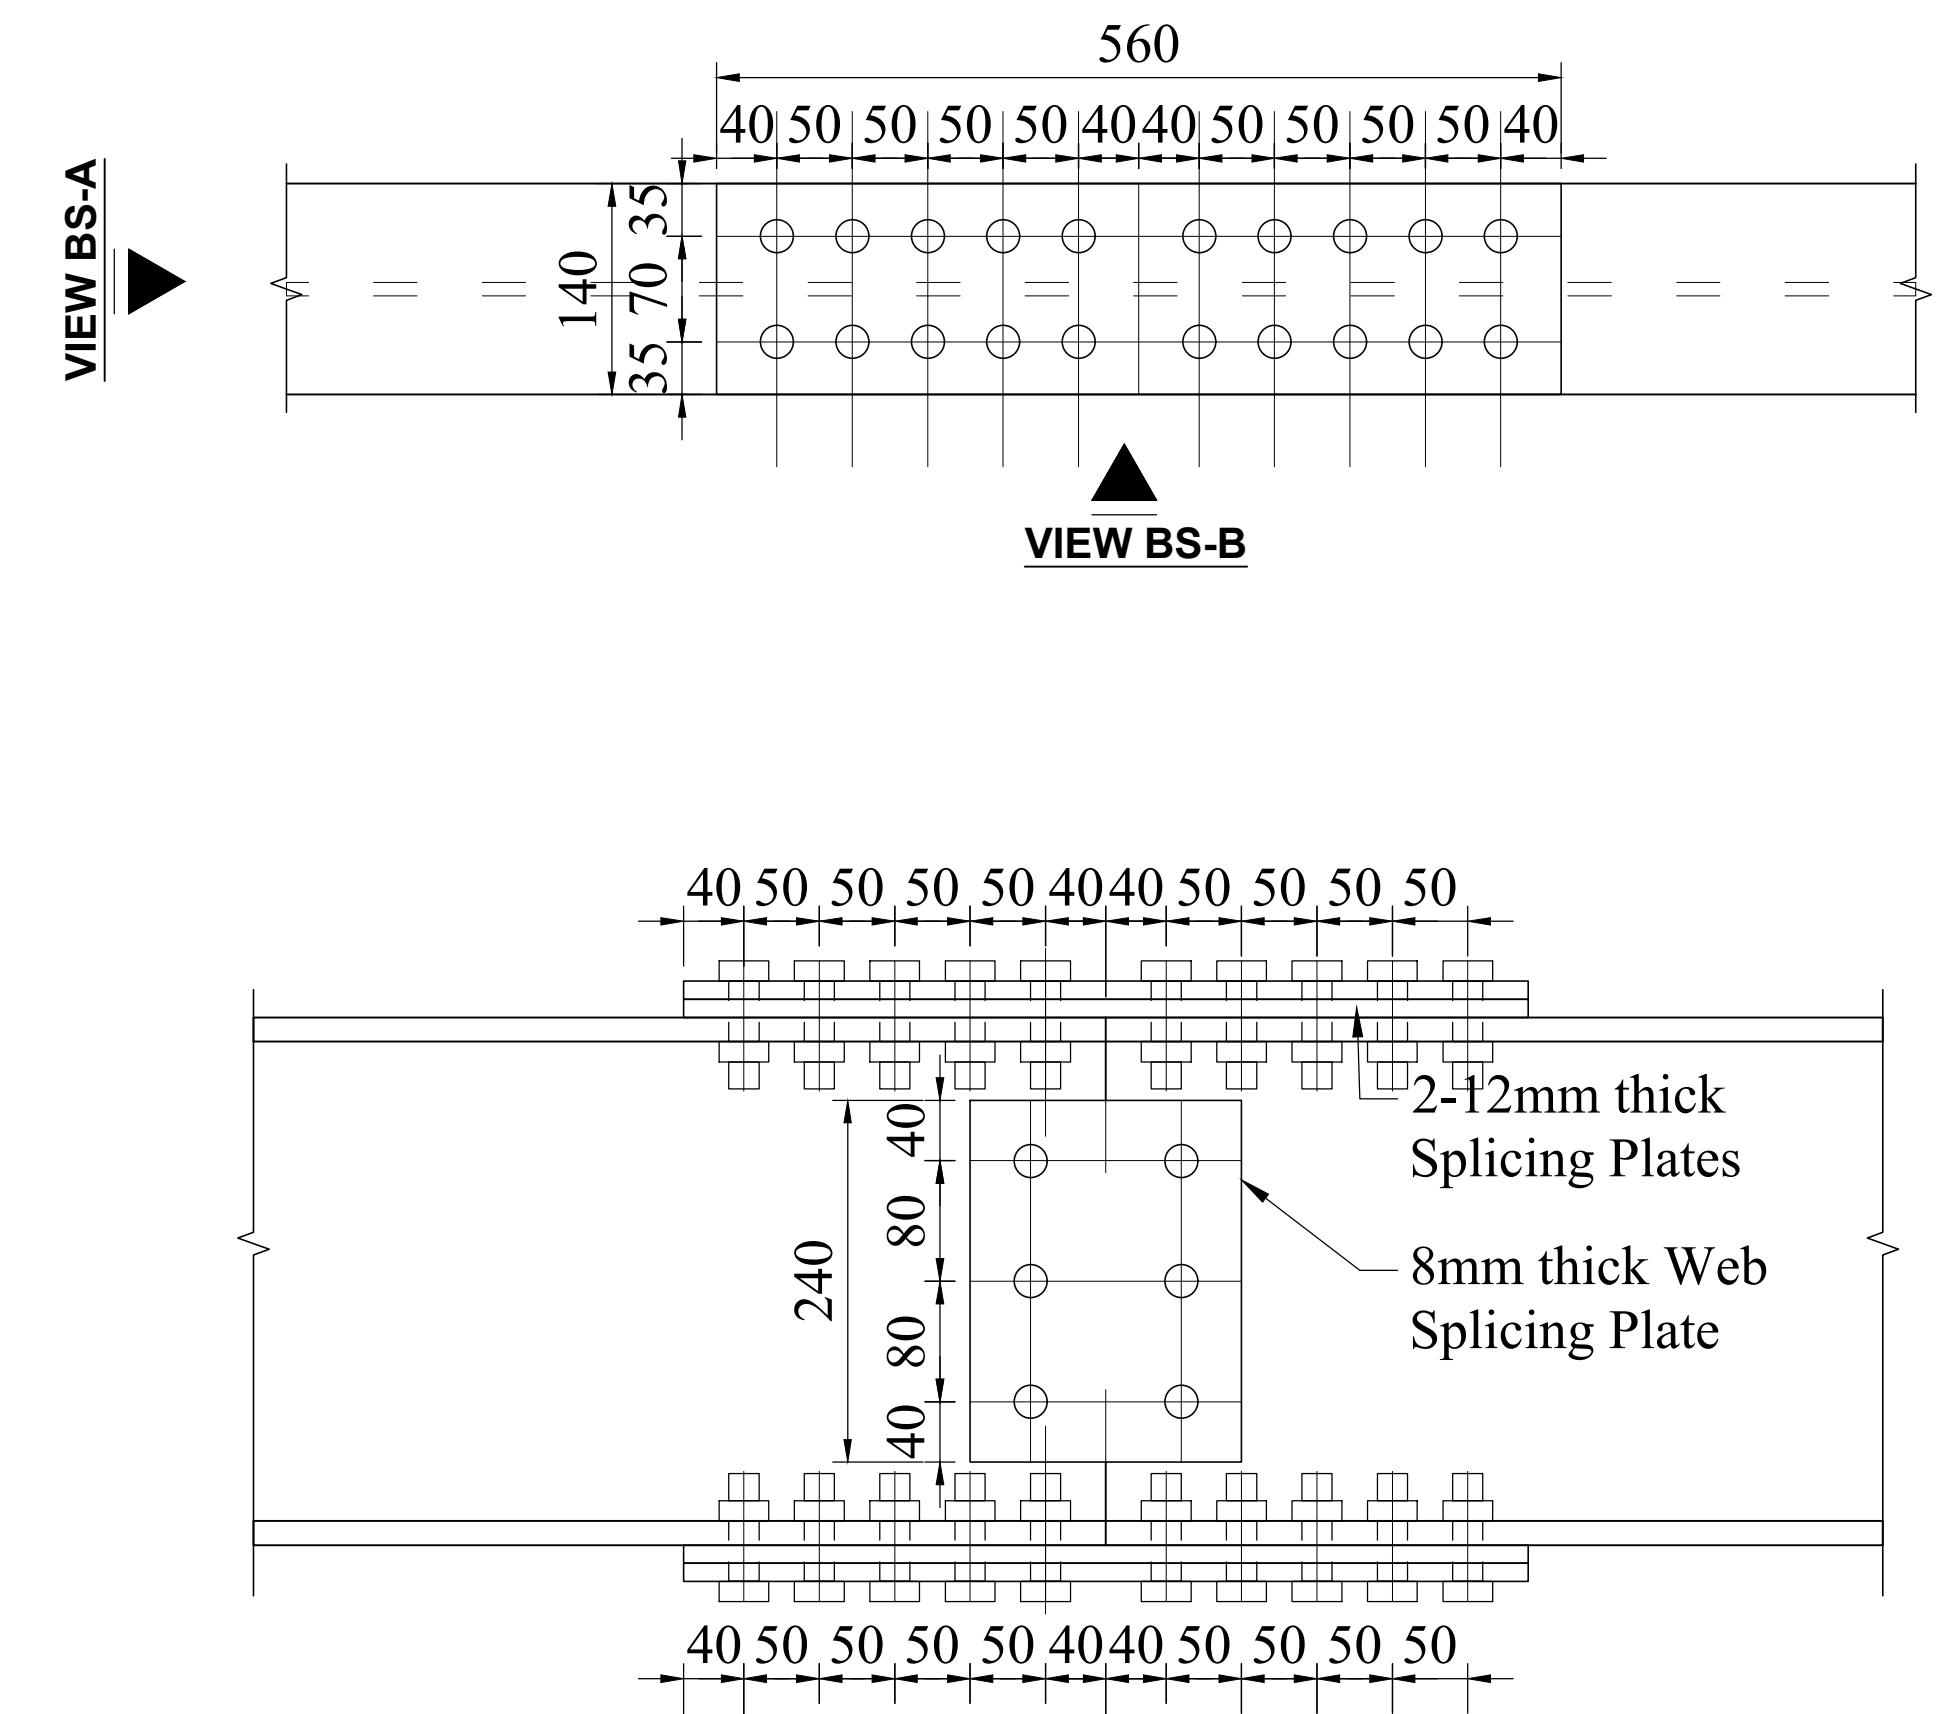


SPLICE FOR ISMB 350
SCALE 1:10

PROJECT: DPR OF 500MT COLD STORE AT JIRI, DOLAKHA	CONTENT: STRUCTURAL DRAWINGS		CHECKED BY: APPROVED BY :	CONSULTANT: Sworaj Consultants Pvt. Ltd. Samkhushi, Kathmandu	Sheet No
CLIENT: Government of Province Ministry of Land Management, Agriculture and Cooperative Province No. 3, Hetauda	FINAL DRAWING		SCALE :		ST 13
			DATE: REVISION:		

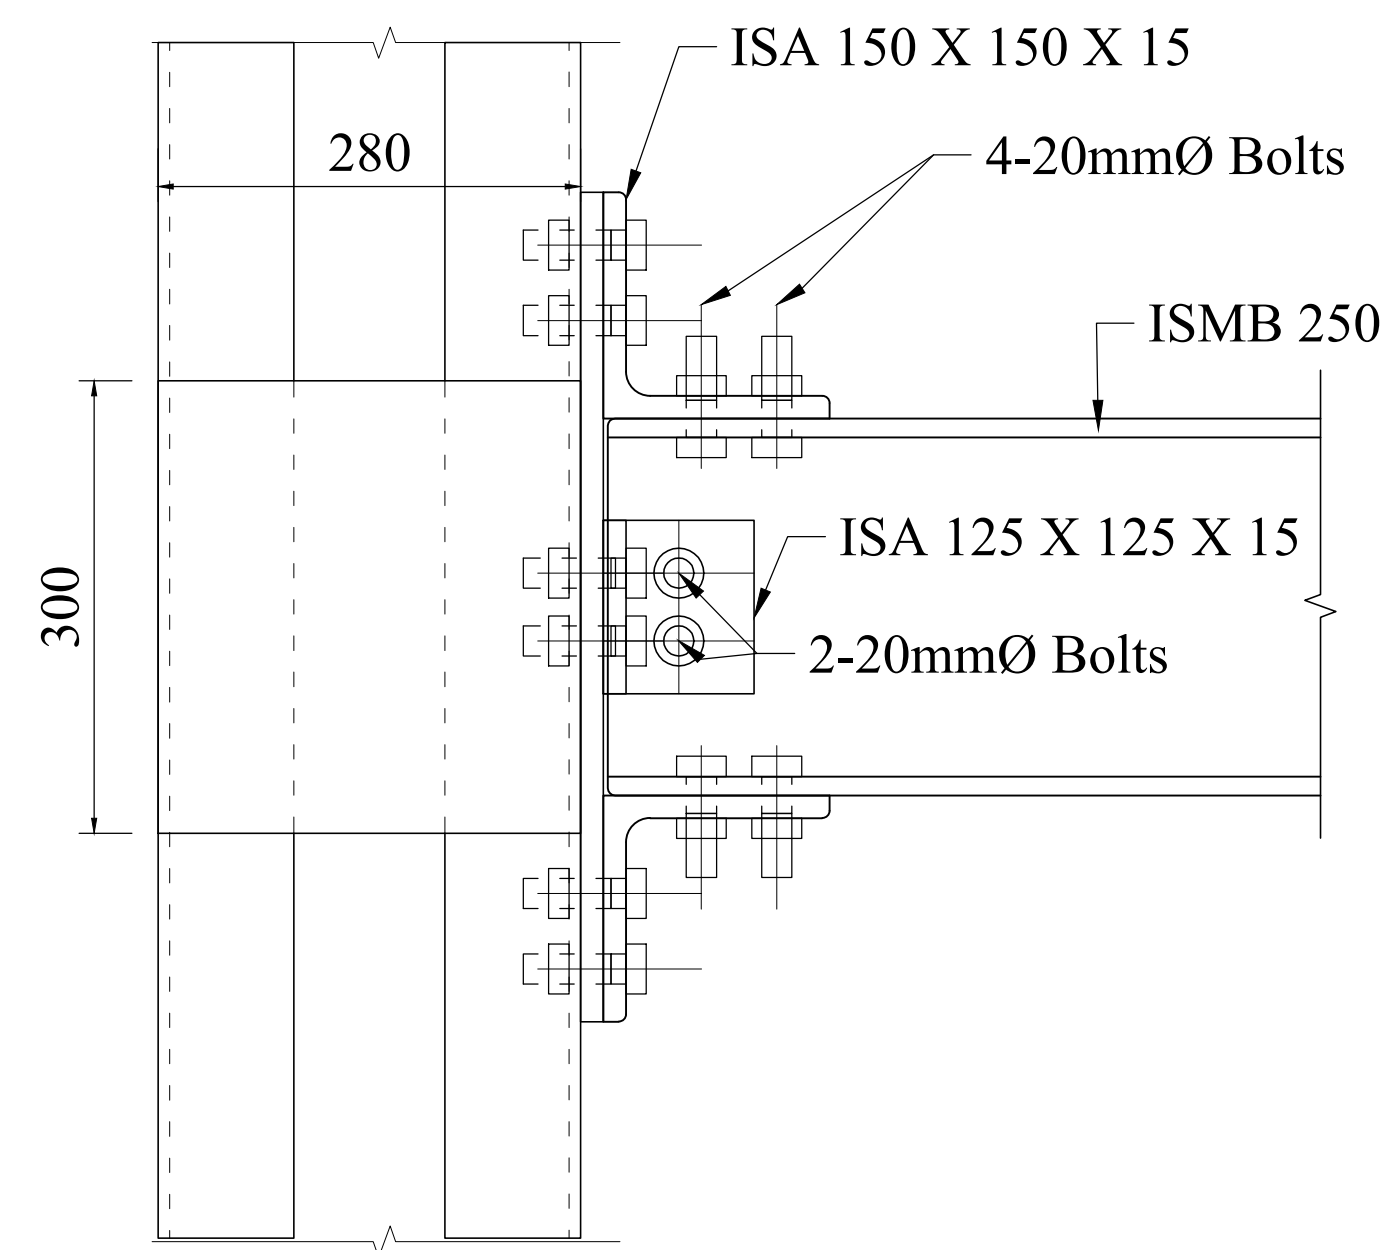


VIEW 1A-1

BEAM-COLUMN CONNECTION BC-1A

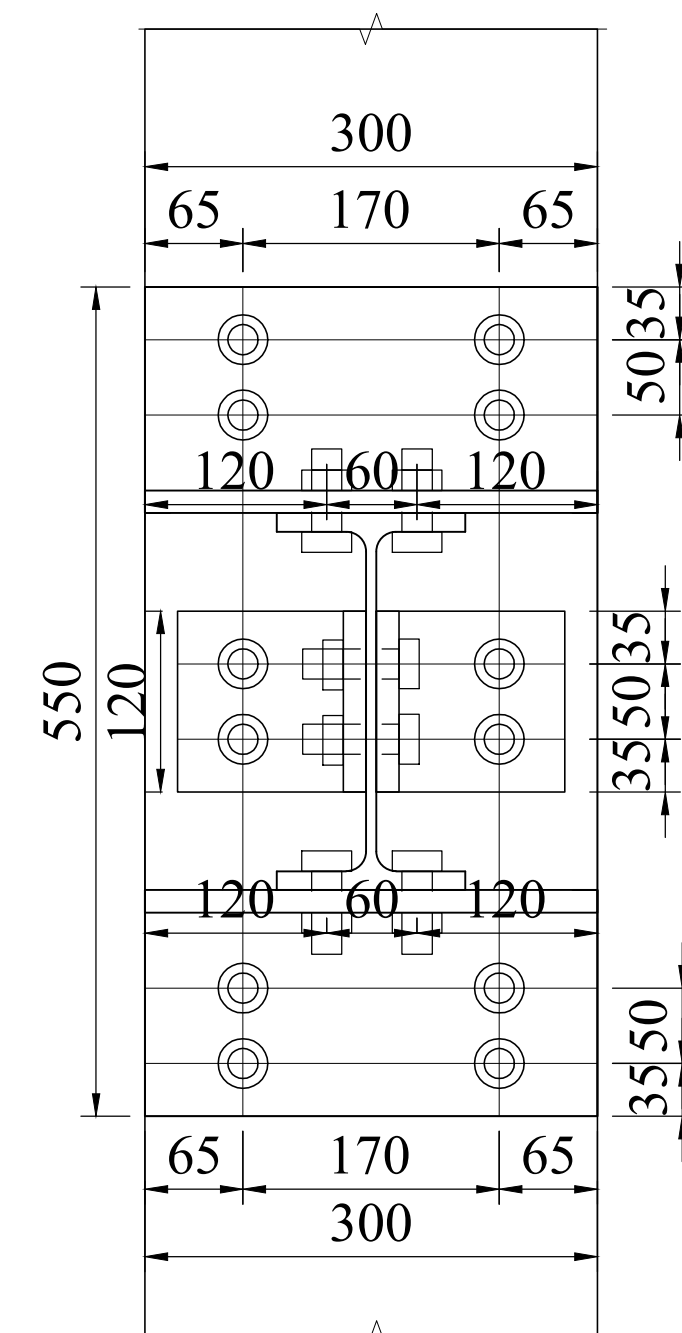


VIEW 1A-2

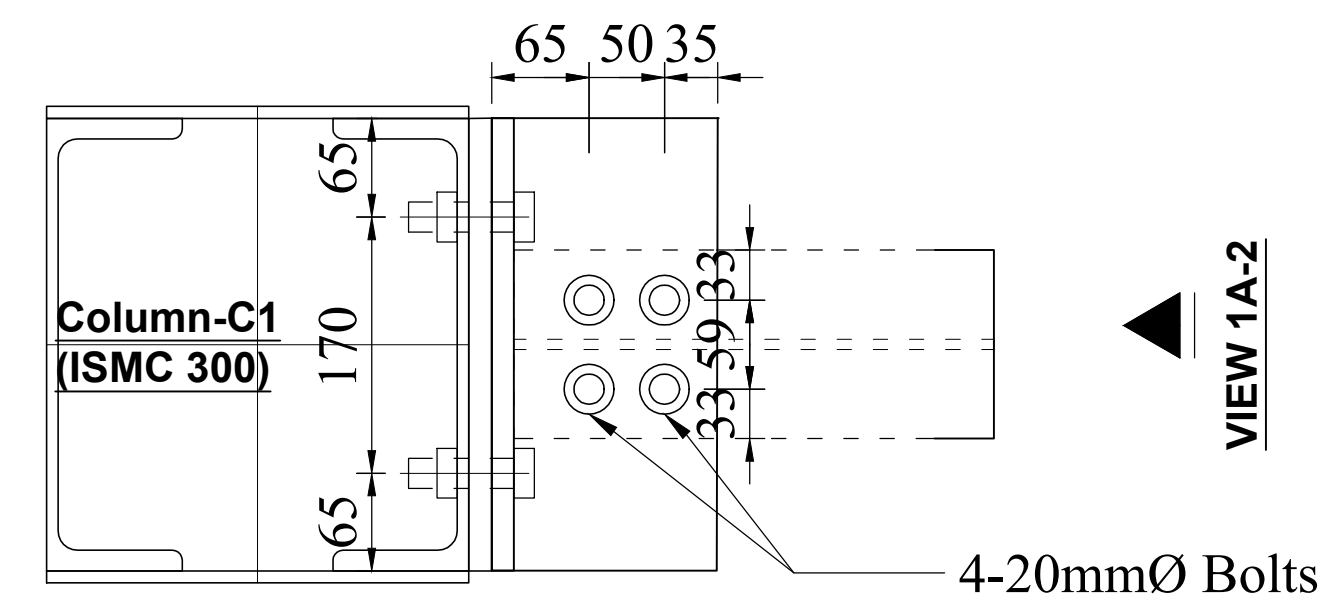


VIEW 1A-1

CONNECTION DETAIL PLAN

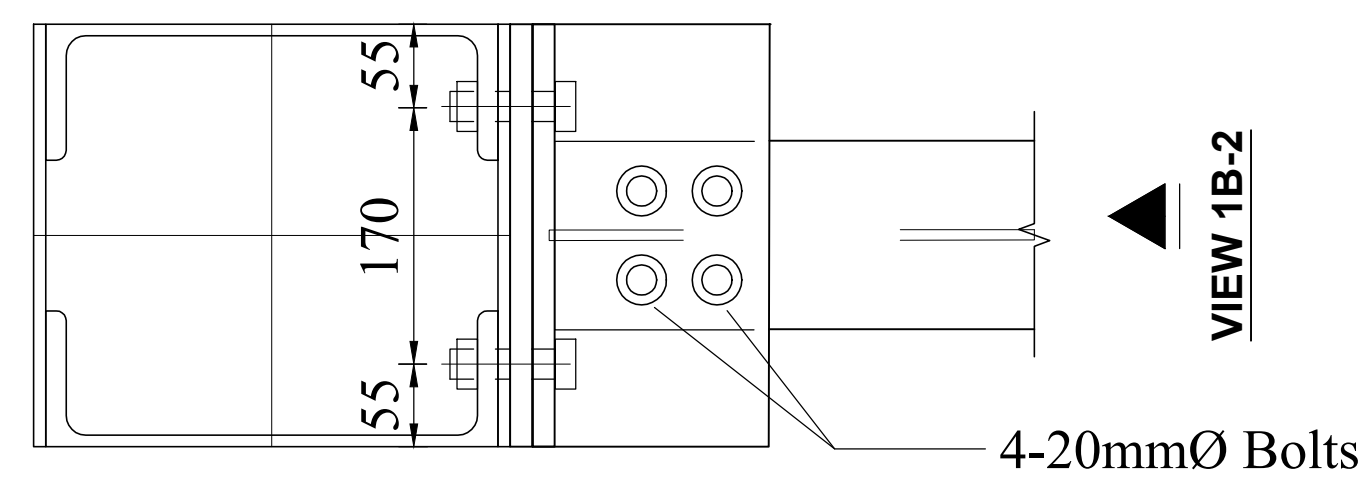


VIEW 1B-1

CONNECTION DETAIL PLAN

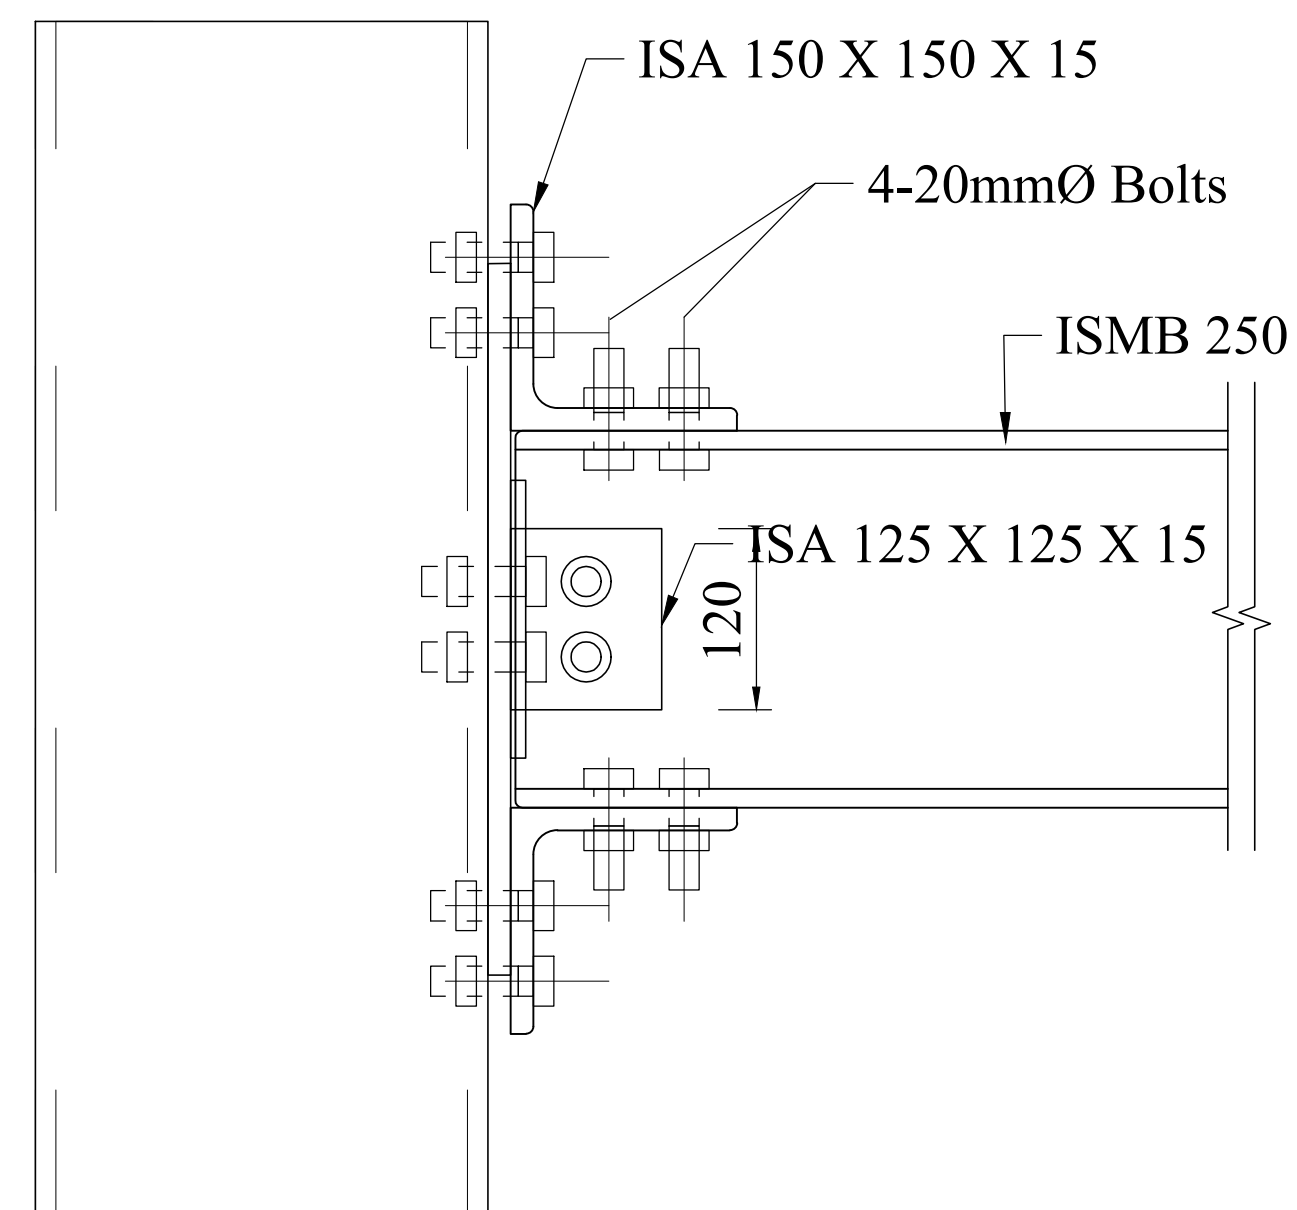


VIEW 1B-1

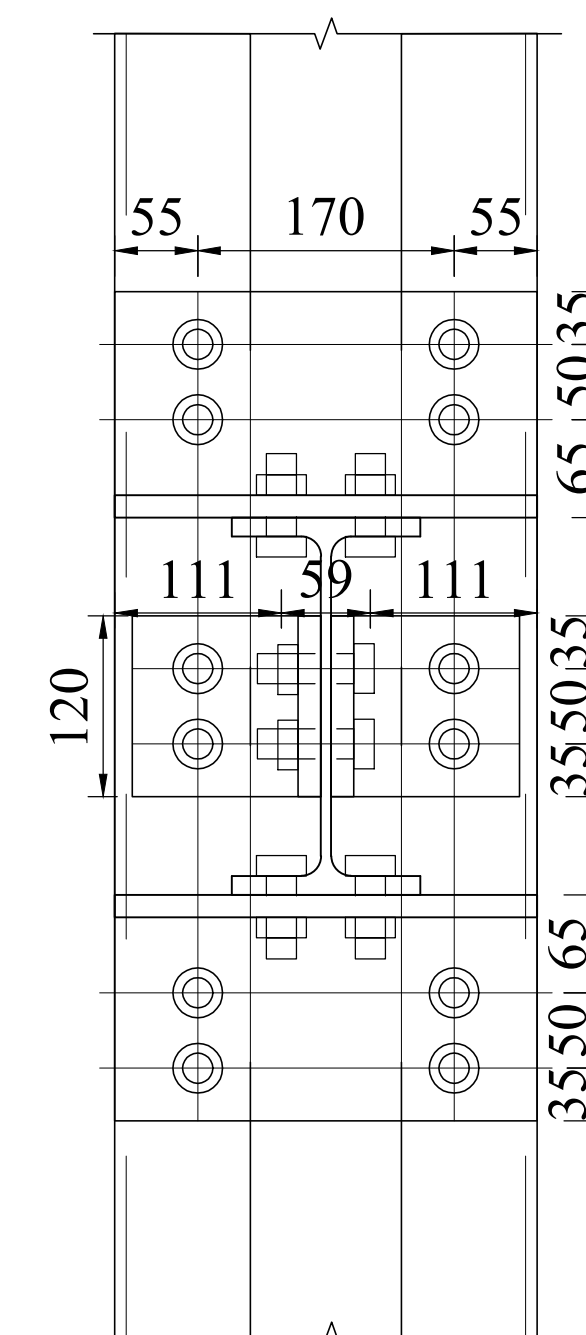


VIEW 1B-2

BEAM-COLUMN CONNECTION BC-1B


PROJECT: DPR OF 500MT COLD STORE AT JIRI, DOLAKHA	CONTENT: STRUCTURAL DRAWINGS		CHECKED BY: APPROVED BY :	CONSULTANT: Sworaj Consultants Pvt. Ltd. Samkhushi, Kathmandu	Sheet No
CLIENT: Government of Province Ministry of Land Management, Agriculture and Cooperative Province No. 3, Hetauda	FINAL DRAWING		SCALE :		ST 14
			DATE: REVISION:		

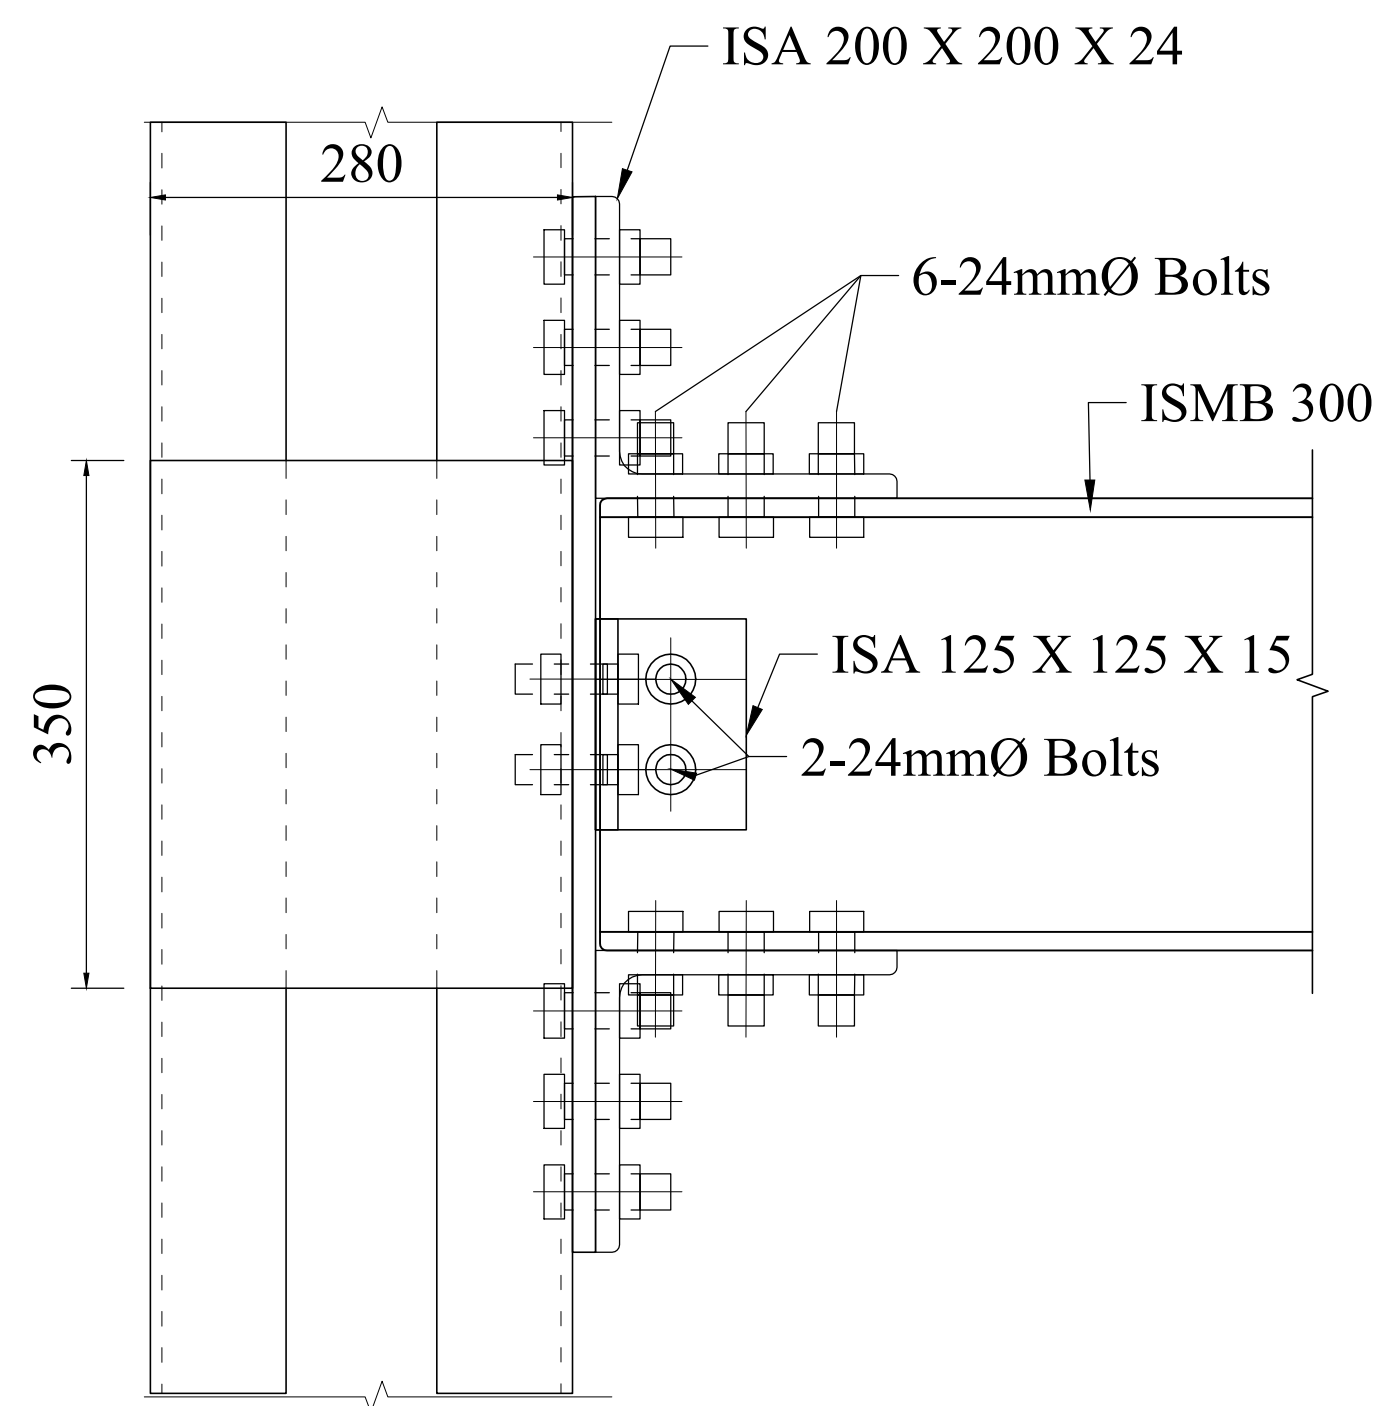

VIEW 2A-1

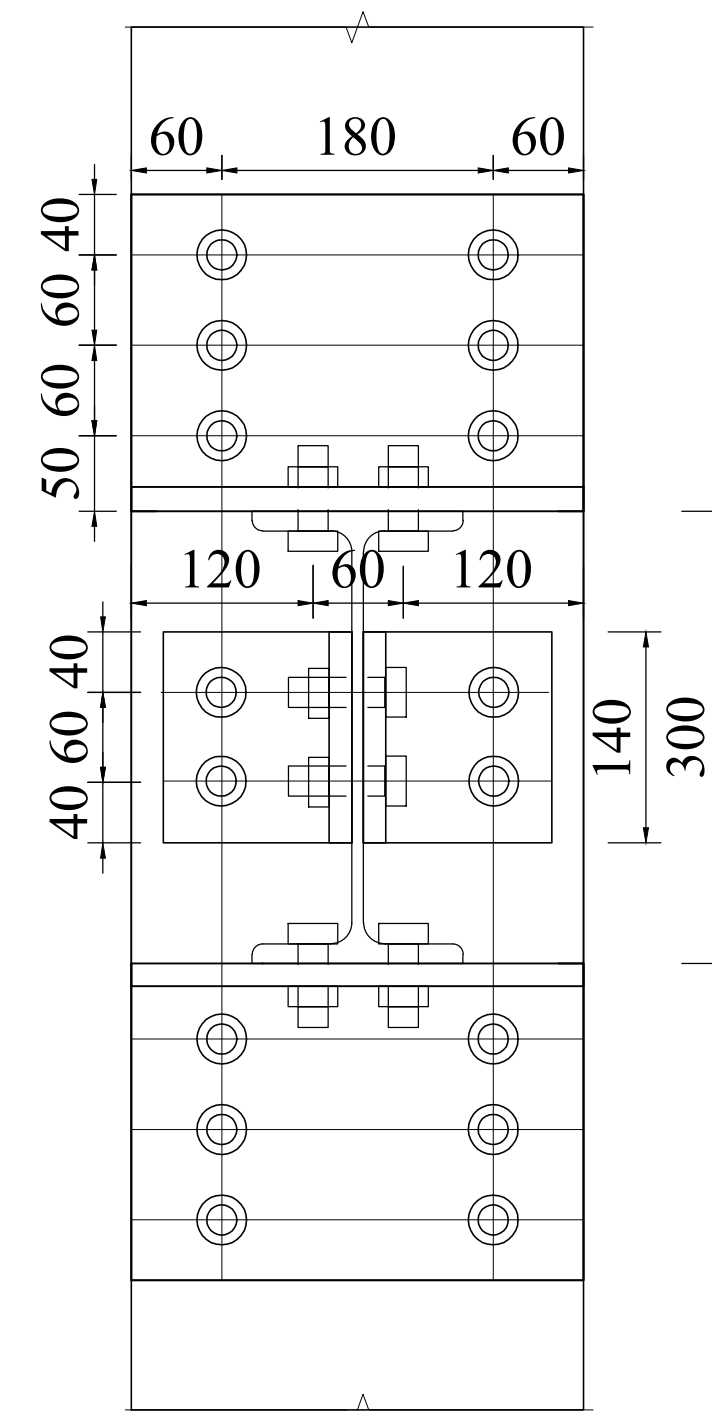


VIEW 2A-2

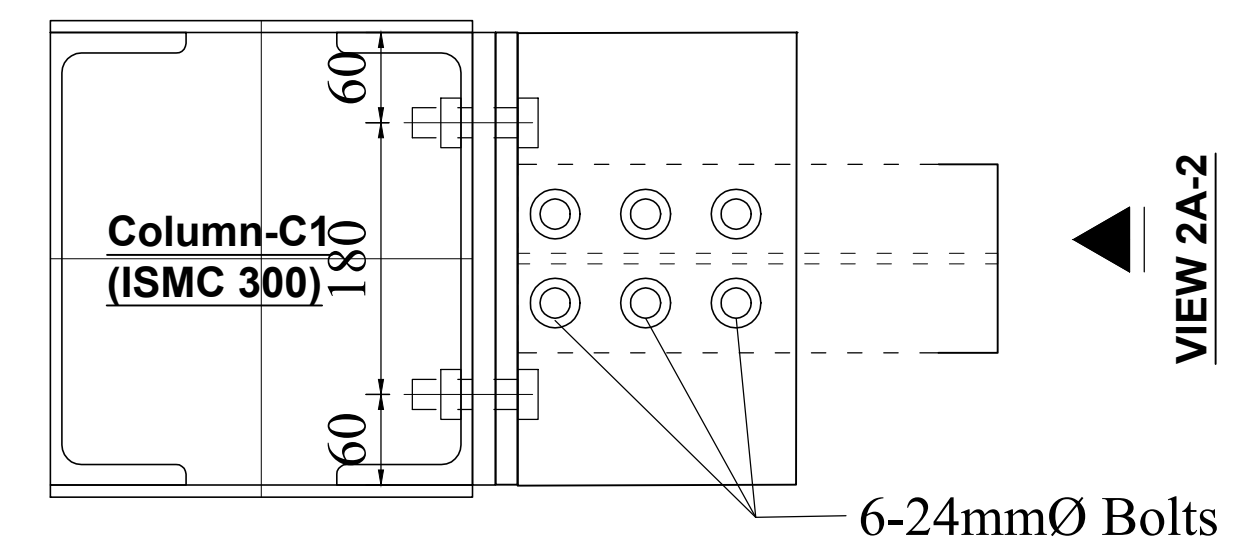


VIEW 2A-1

CONNECTION DETAIL PLAN


BEAM-COLUMN CONNECTION BC-2A

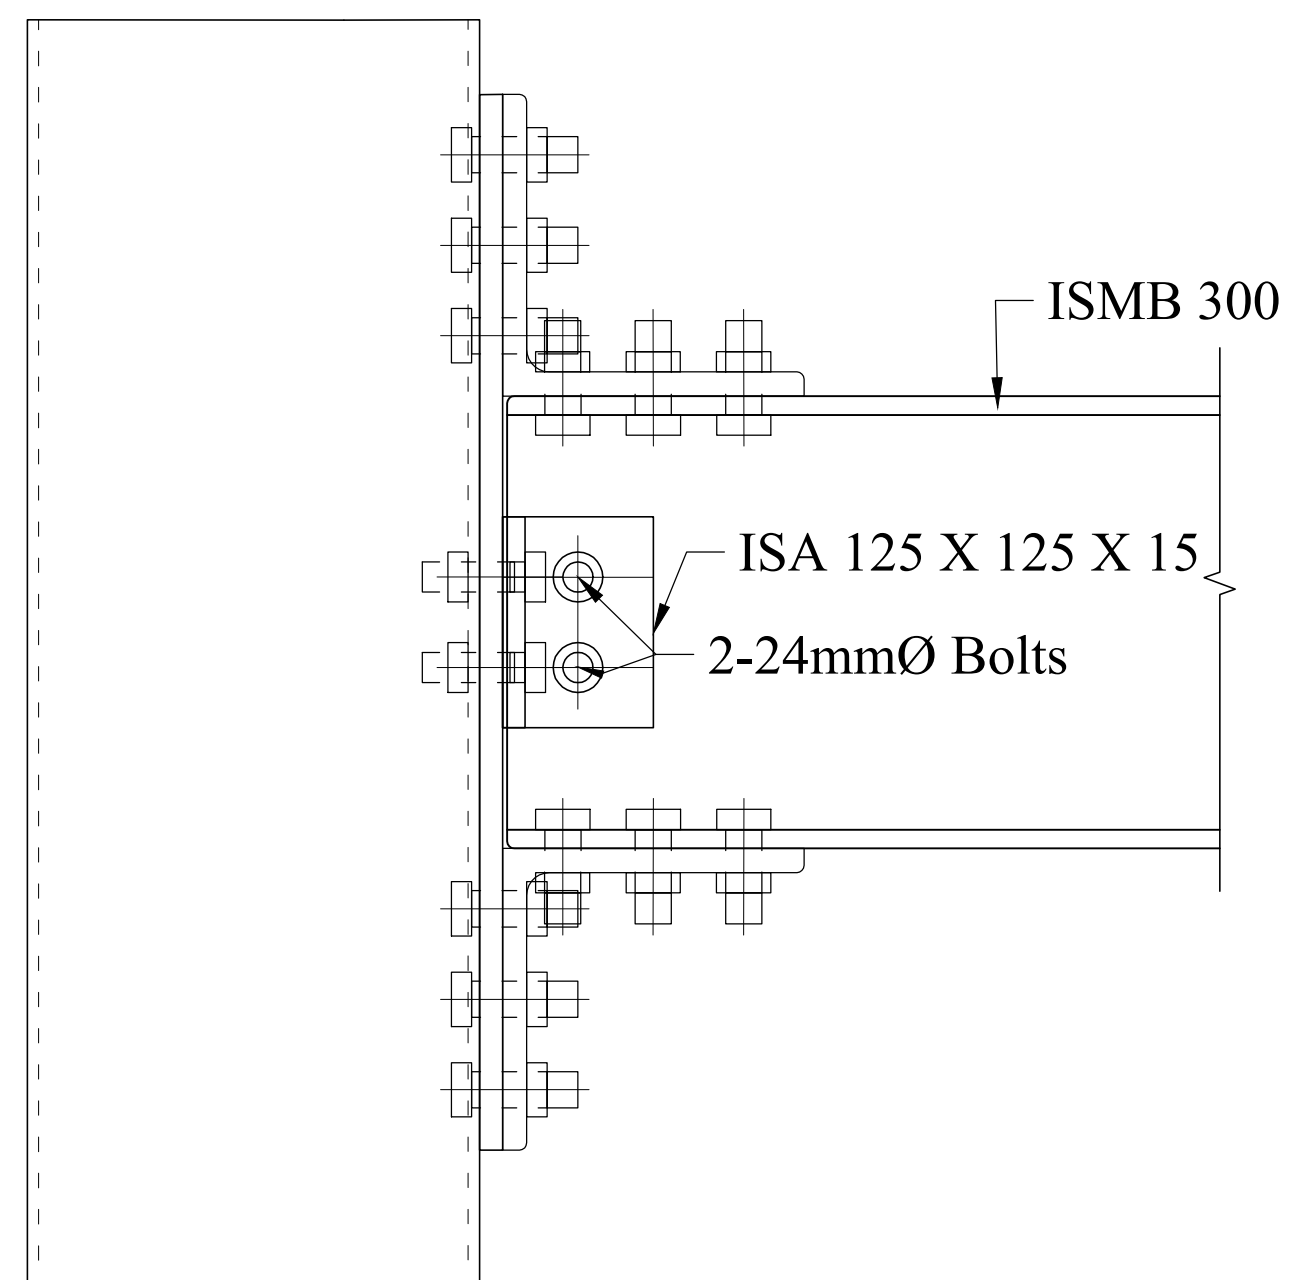

VIEW 2B-1

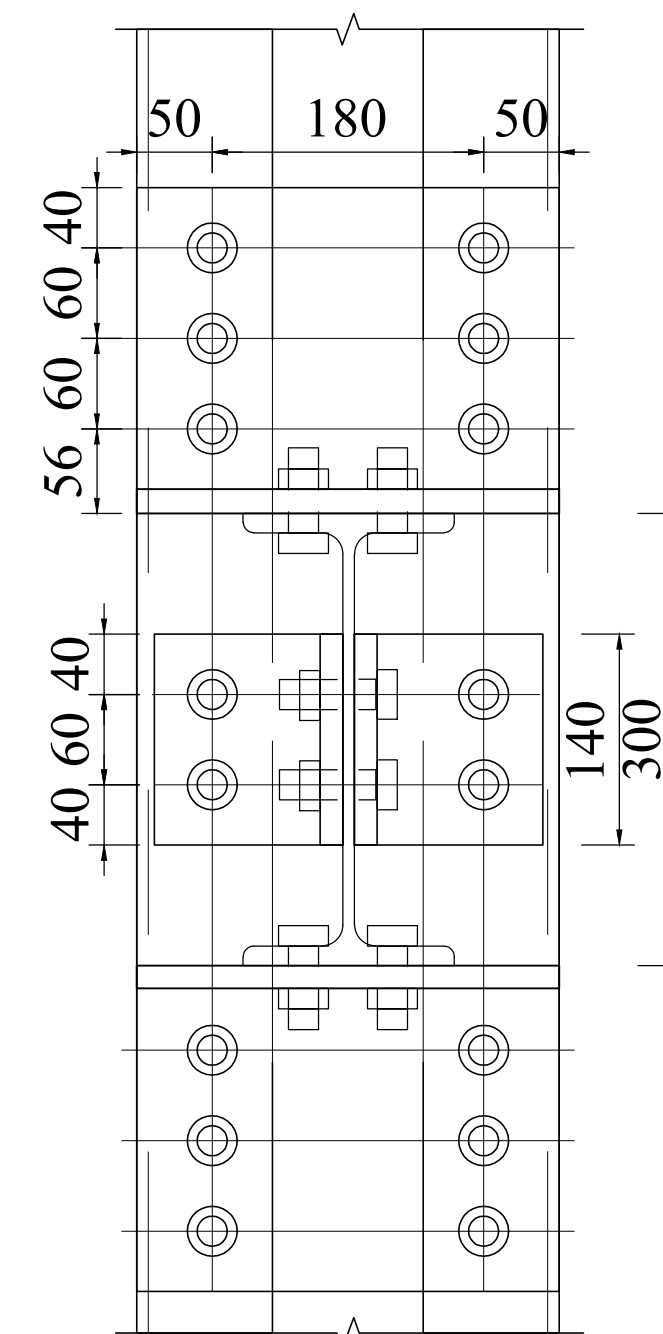

VIEW 2B-2

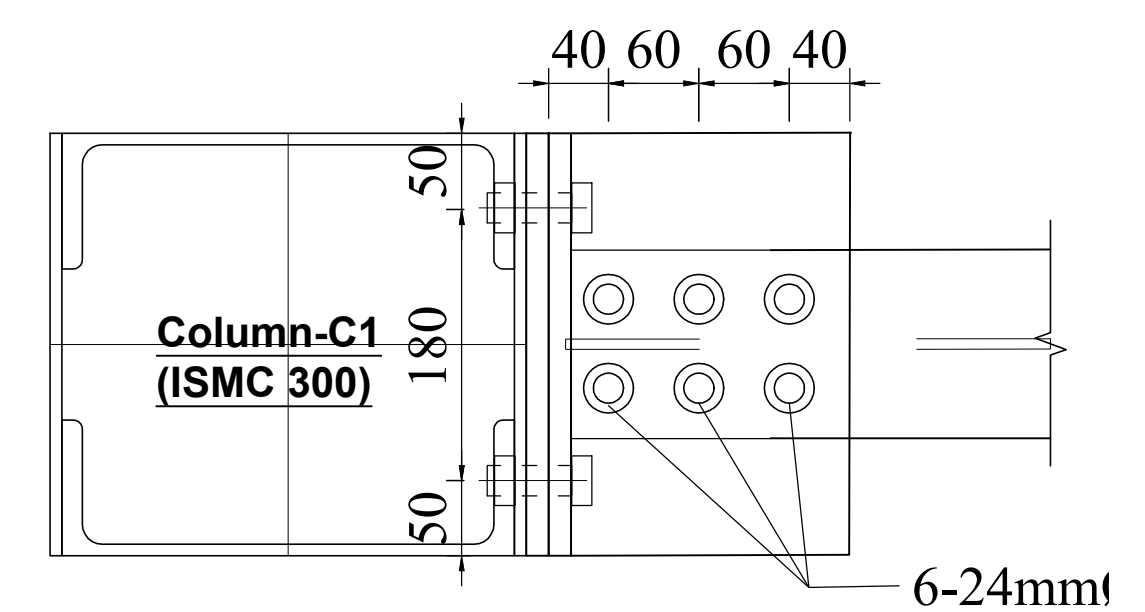


VIEW 2B-1


CONNECTION DETAIL PLAN

BEAM-COLUMN CONNECTION BC-2B


PROJECT: DPR OF 500MT COLD STORE AT JIRI, DOLAKHA	CONTENT: STRUCTURAL DRAWINGS		CHECKED BY: APPROVED BY :	CONSULTANT: Sworaj Consultants Pvt. Ltd. Samkhushi, Kathmandu	Sheet No
CLIENT: Government of Province Ministry of Land Management, Agriculture and Cooperative Province No. 3, Hetauda	FINAL DRAWING		SCALE :		ST 15
			DATE: REVISION:		

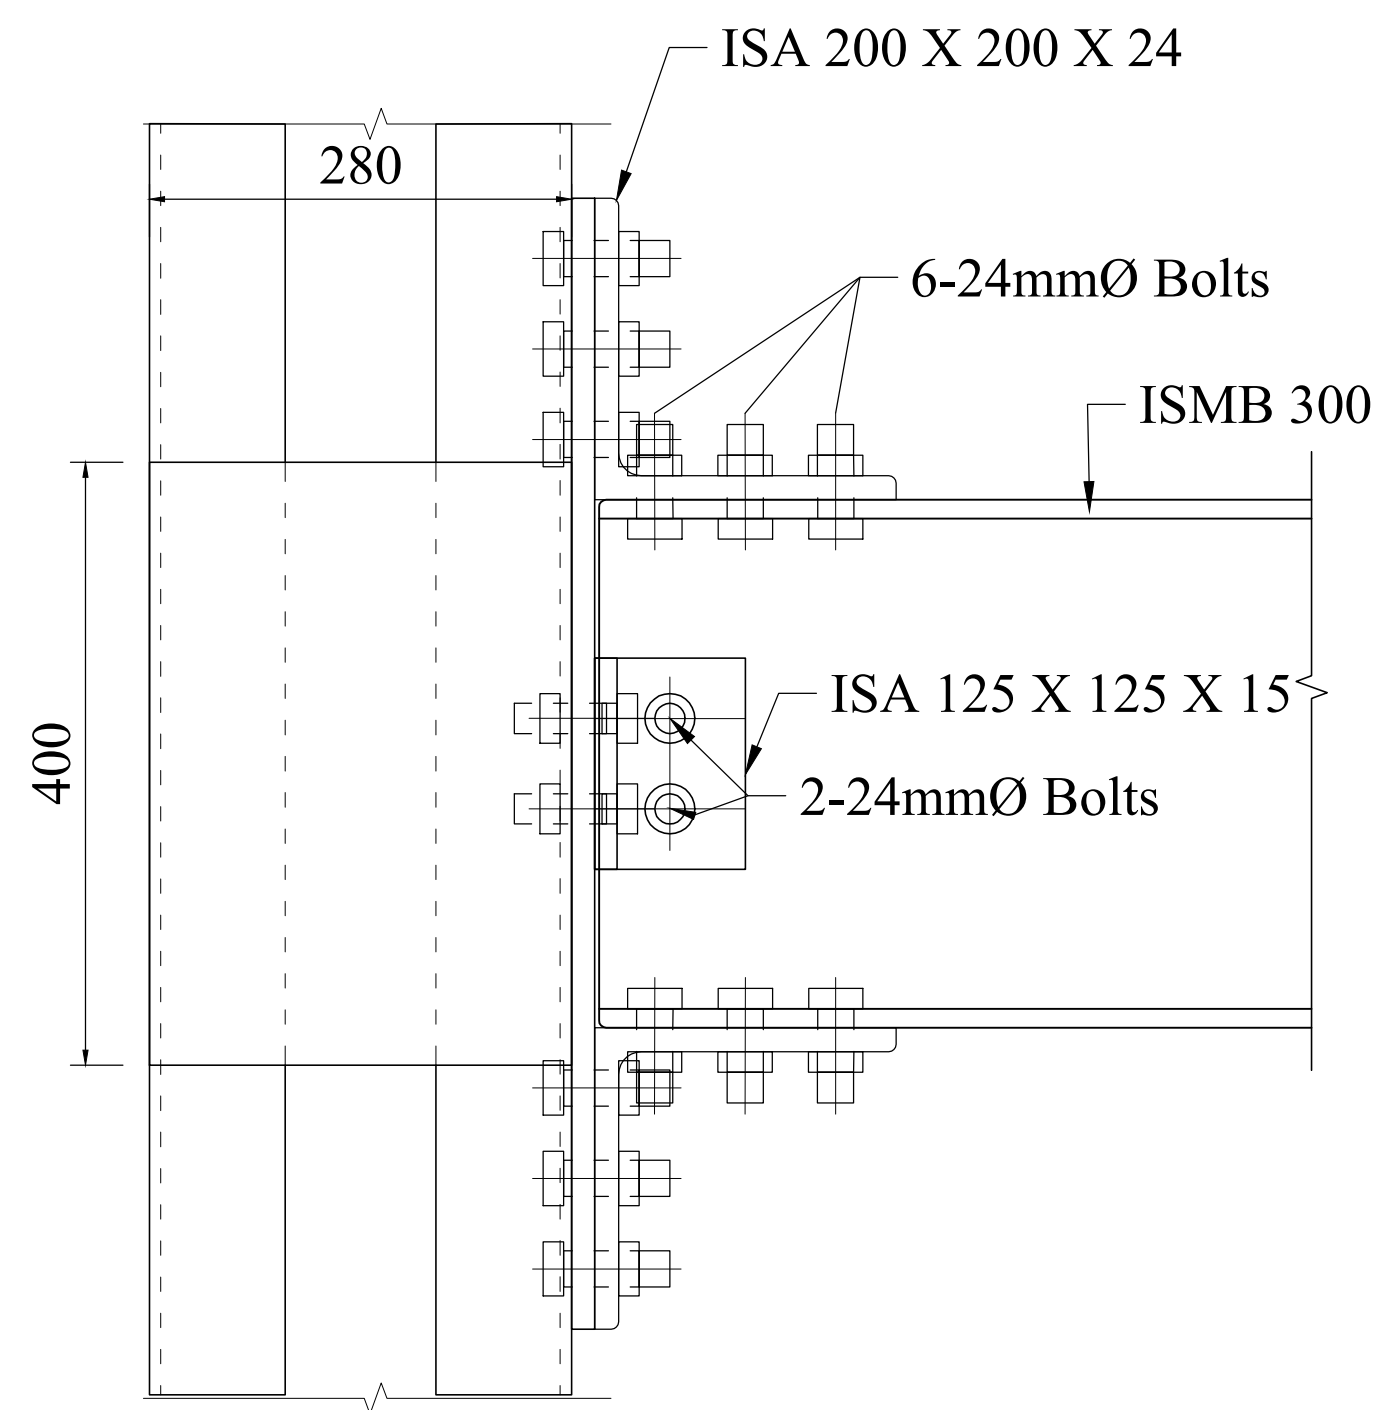

VIEW 3A-1

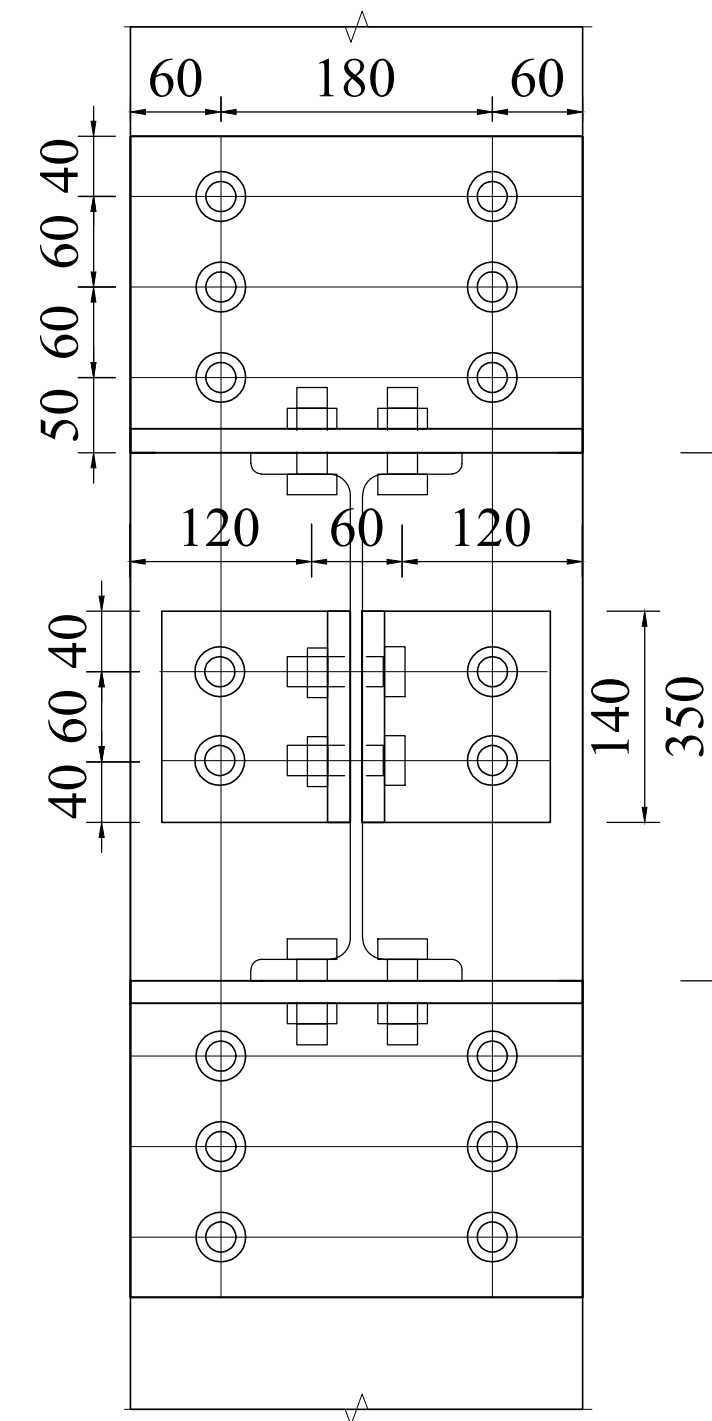

VIEW 3A-2

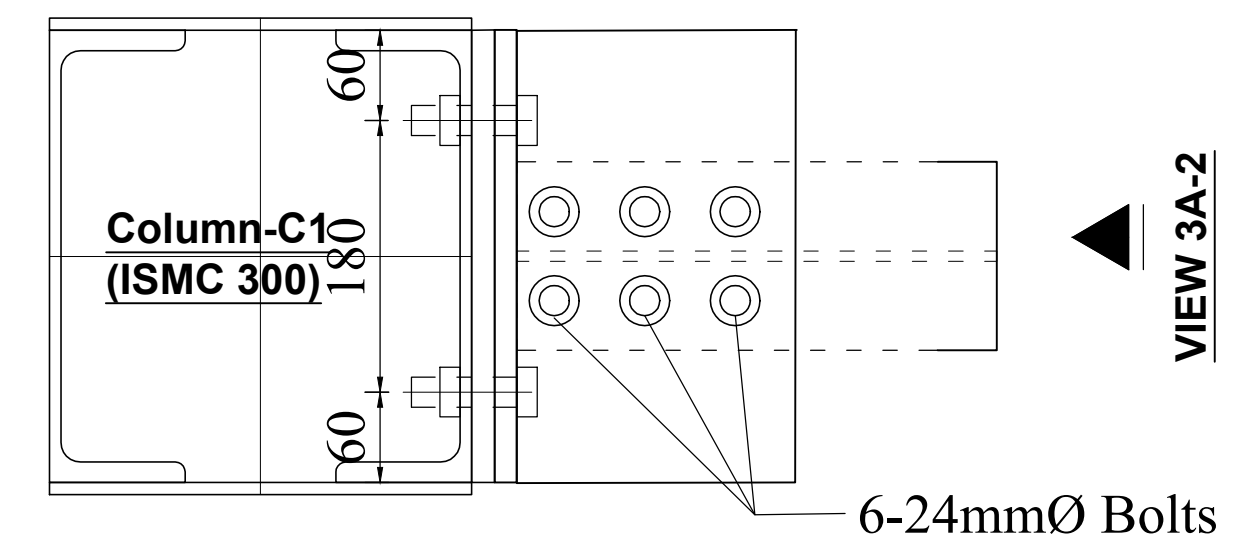


VIEW 3A-2


VIEW 3A-1

CONNECTION DETAIL PLAN


BEAM-COLUMN CONNECTION BC-3A

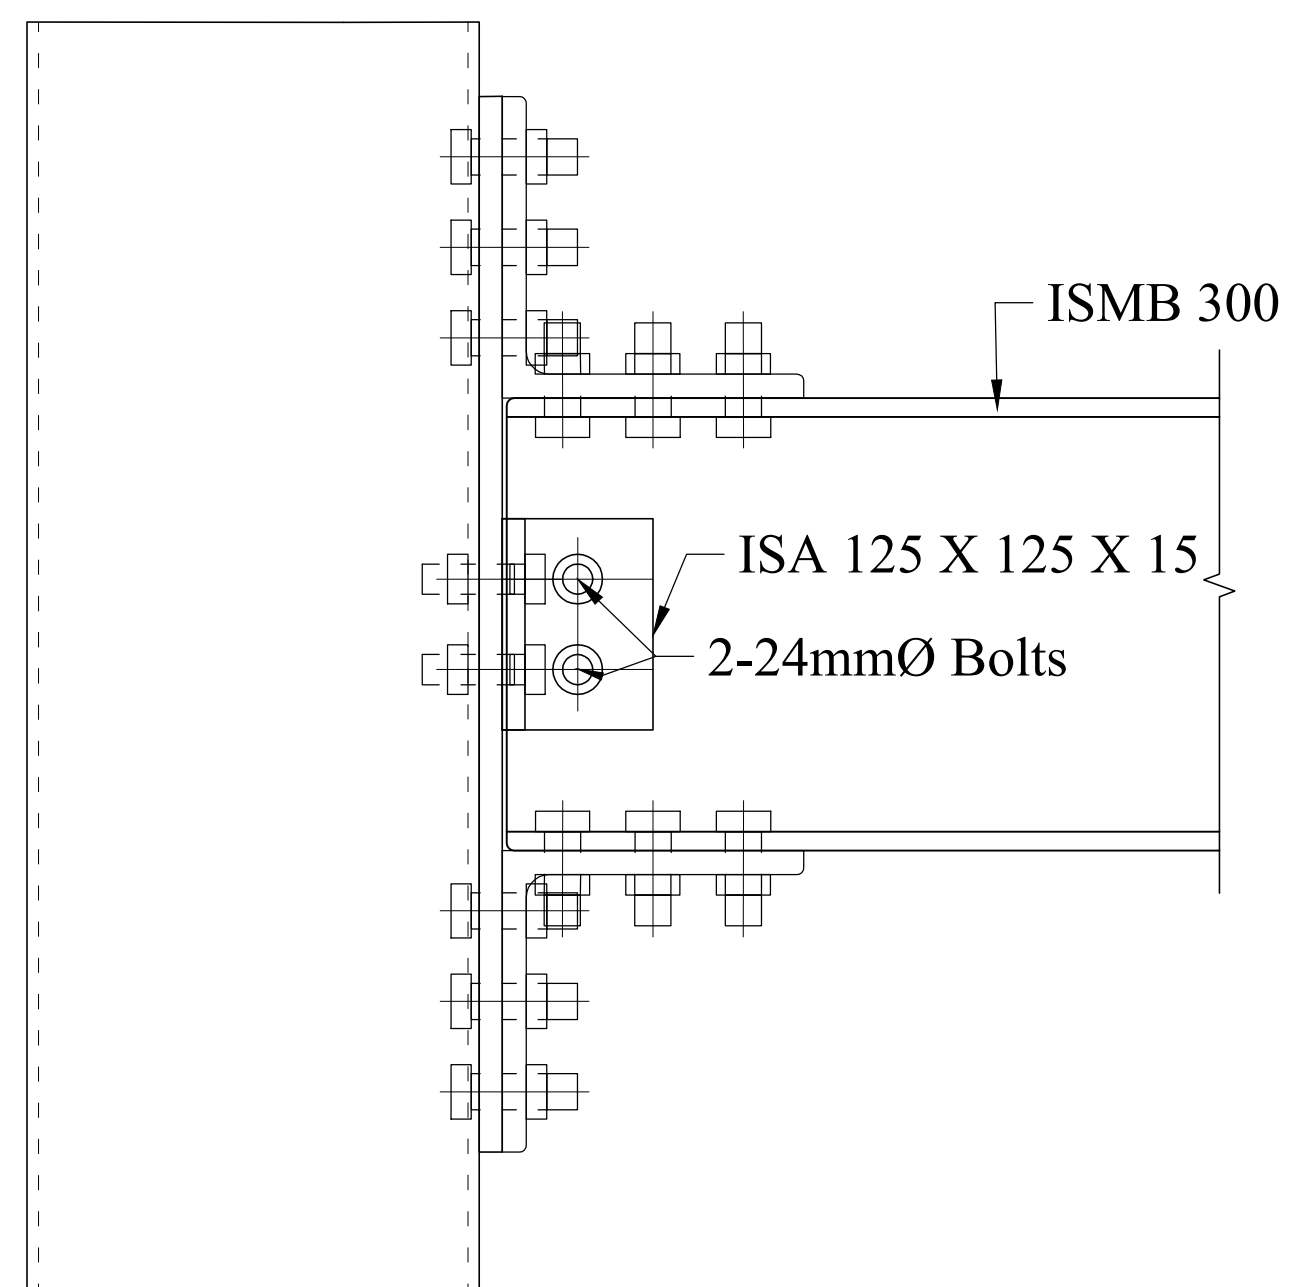

VIEW 3B-1

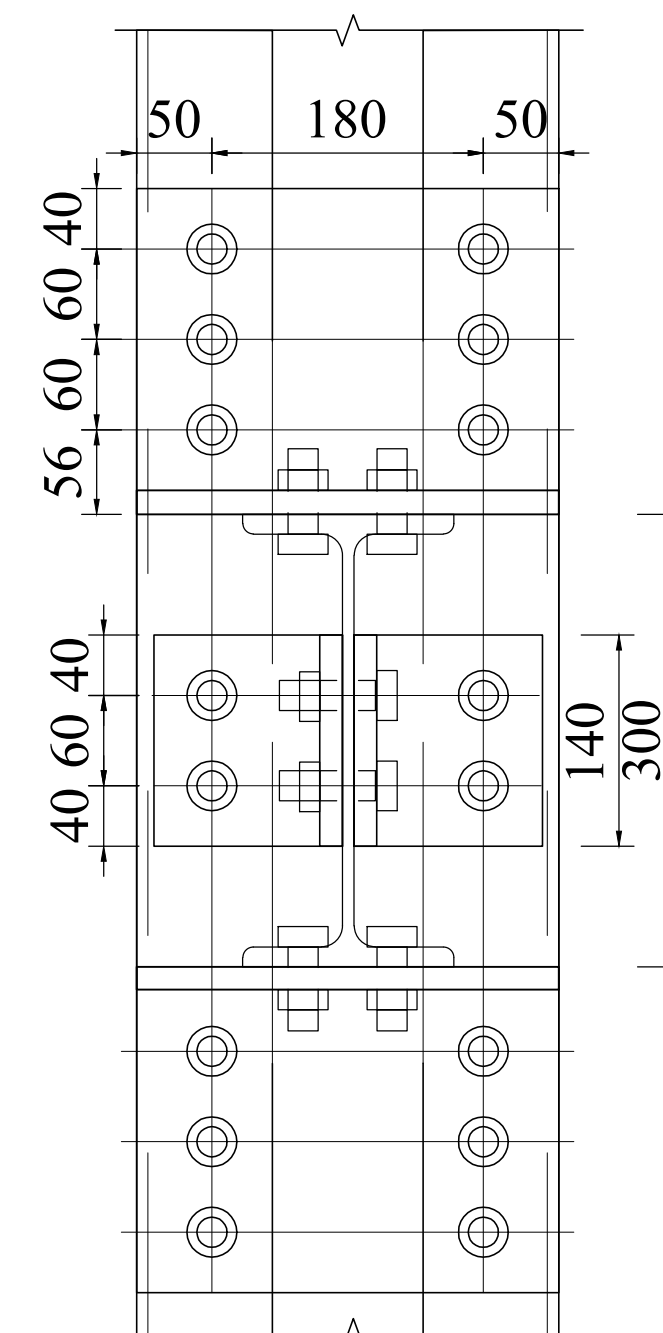

VIEW 3B-2

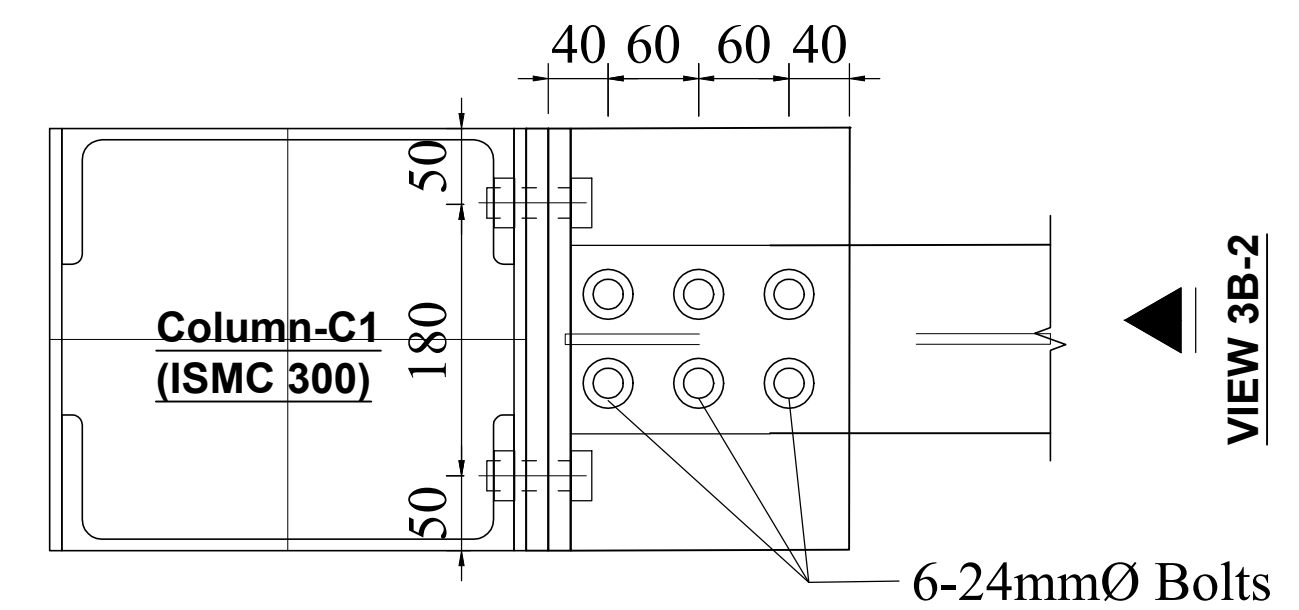



VIEW 3B-2

VIEW 3B-1


CONNECTION DETAIL PLAN

BEAM-COLUMN CONNECTION BC-3B


PROJECT: DPR OF 500MT COLD STORE AT JIRI, DOLAKHA	CONTENT: STRUCTURAL DRAWINGS		CHECKED BY: 	CONSULTANT: Sworaj Consultants Pvt. Ltd. Samkhushi, Kathmandu	Sheet No
CLIENT: Government of Province Ministry of Land Management, Agriculture and Cooperative Province No. 3, Hetauda	FINAL DRAWING		APPROVED BY :		ST
			SCALE : 		
			DATE:		16

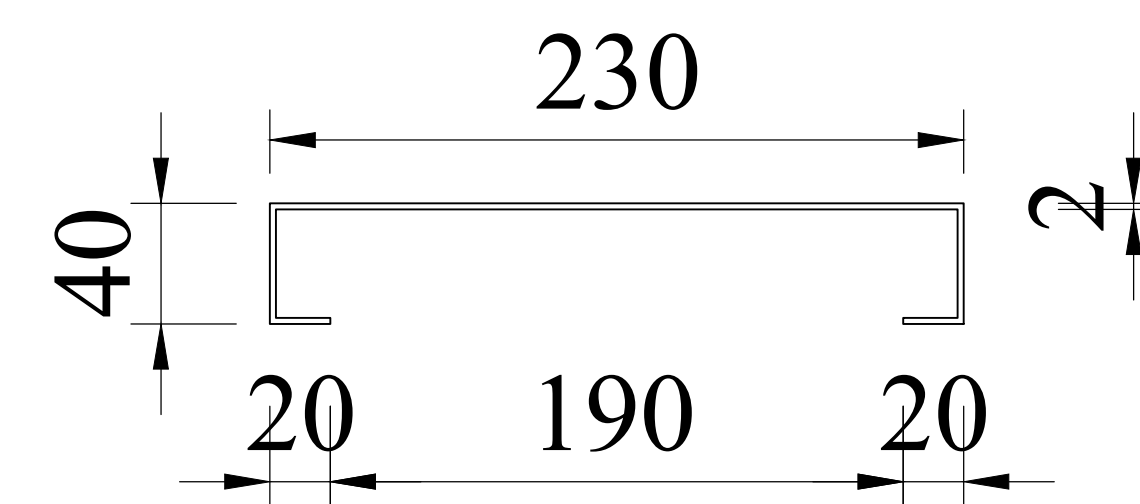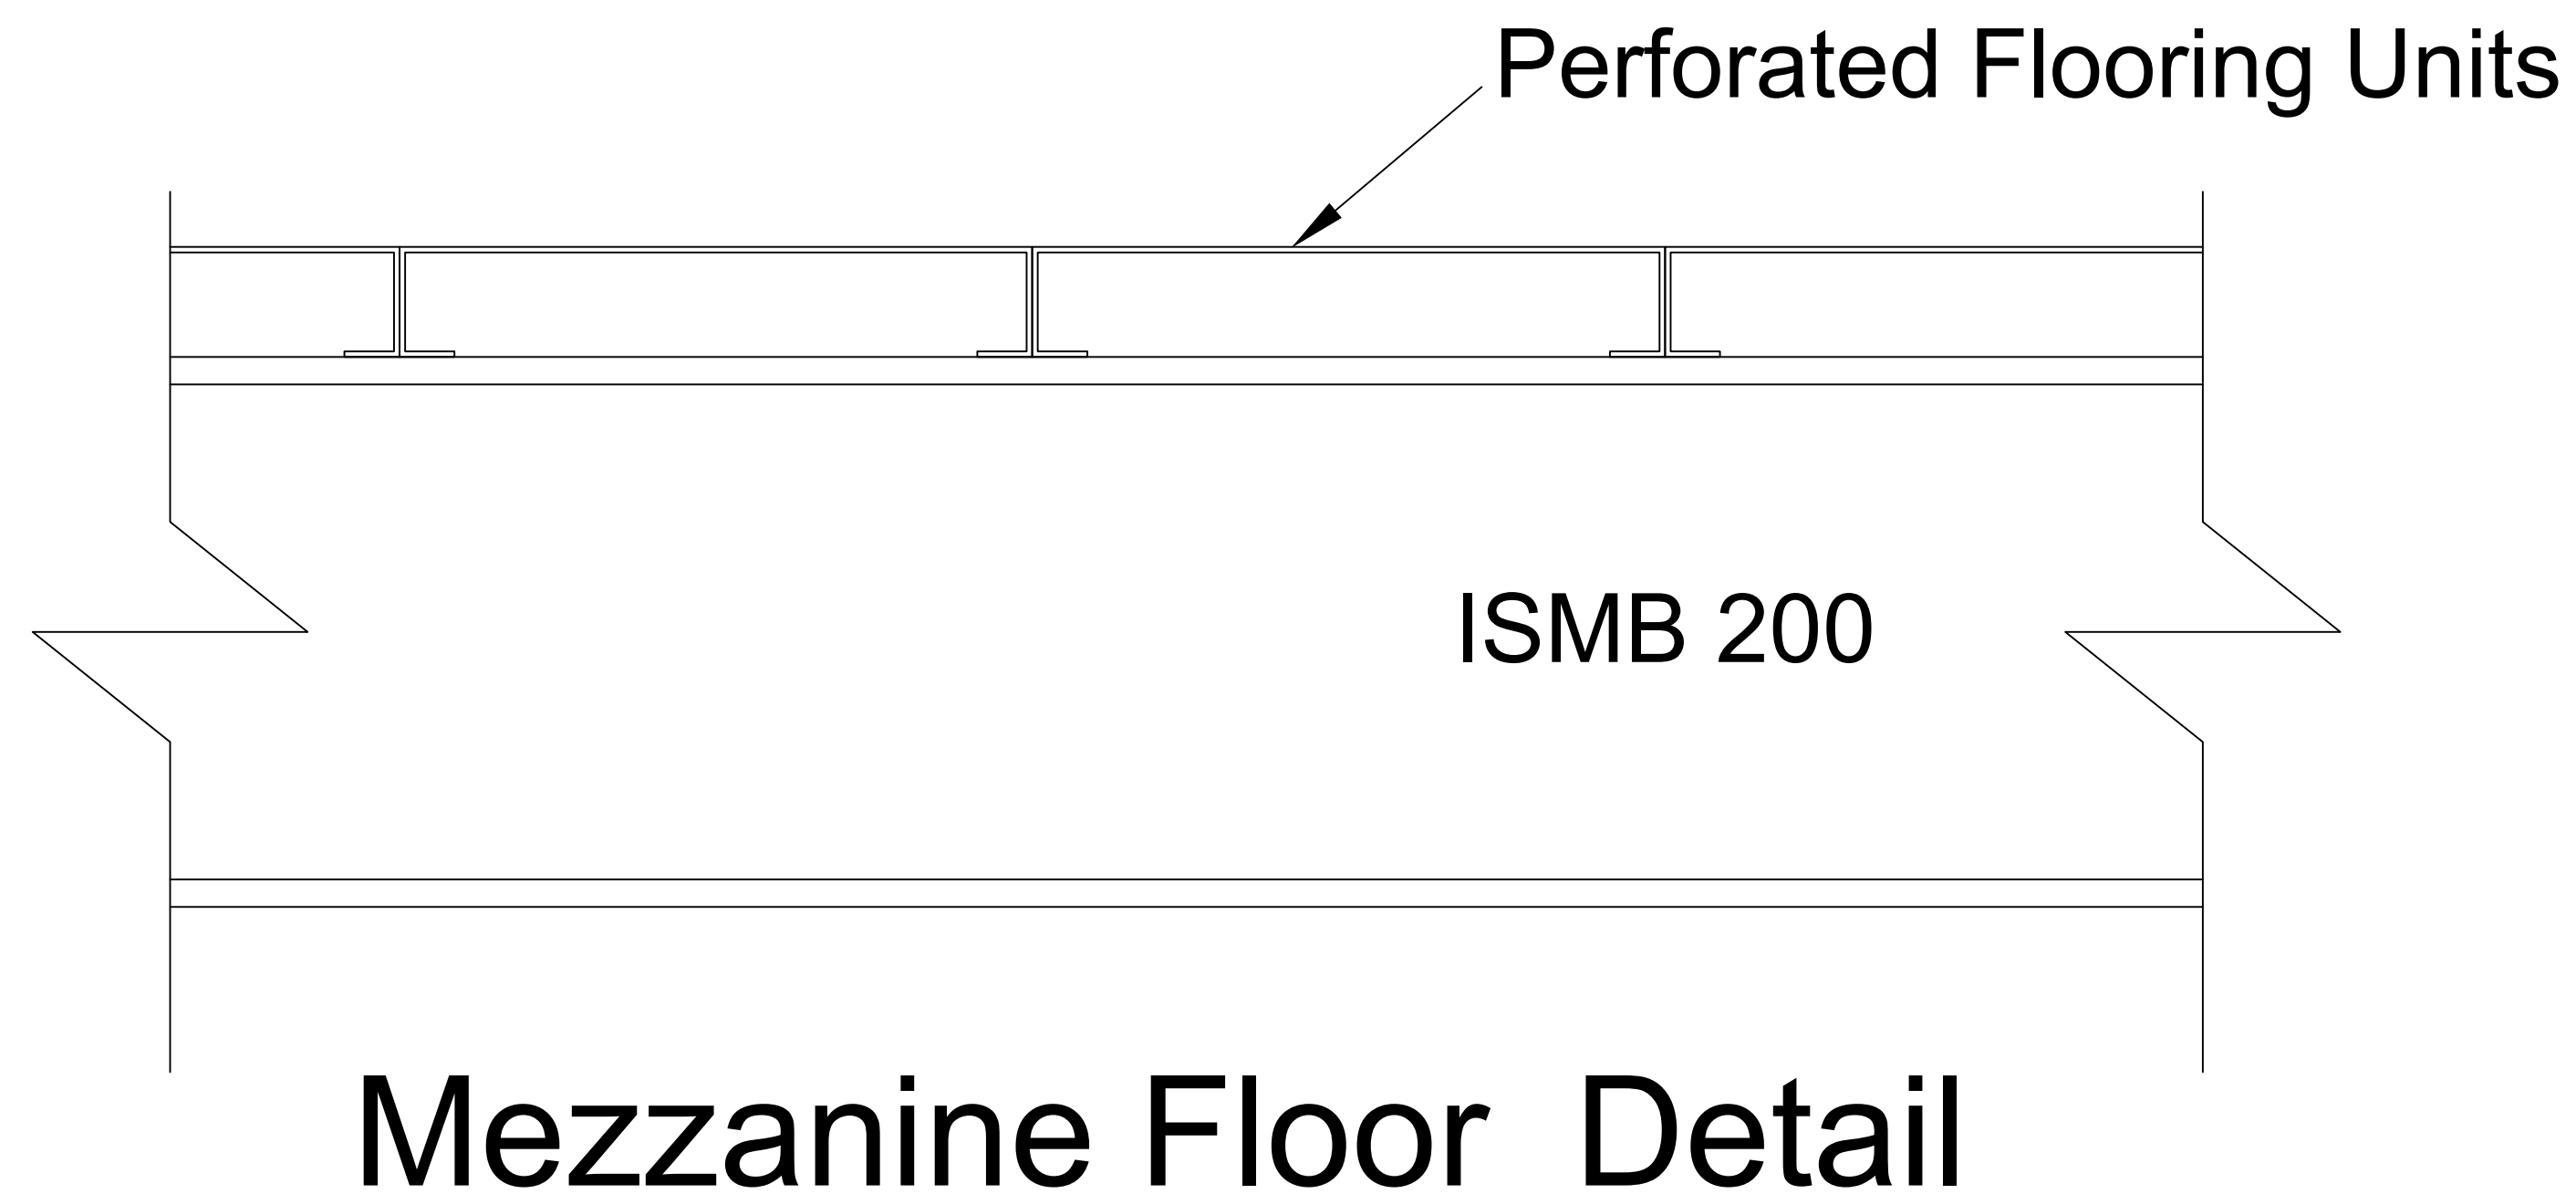


Mezzanine Perforated
Flooring Unit Detail

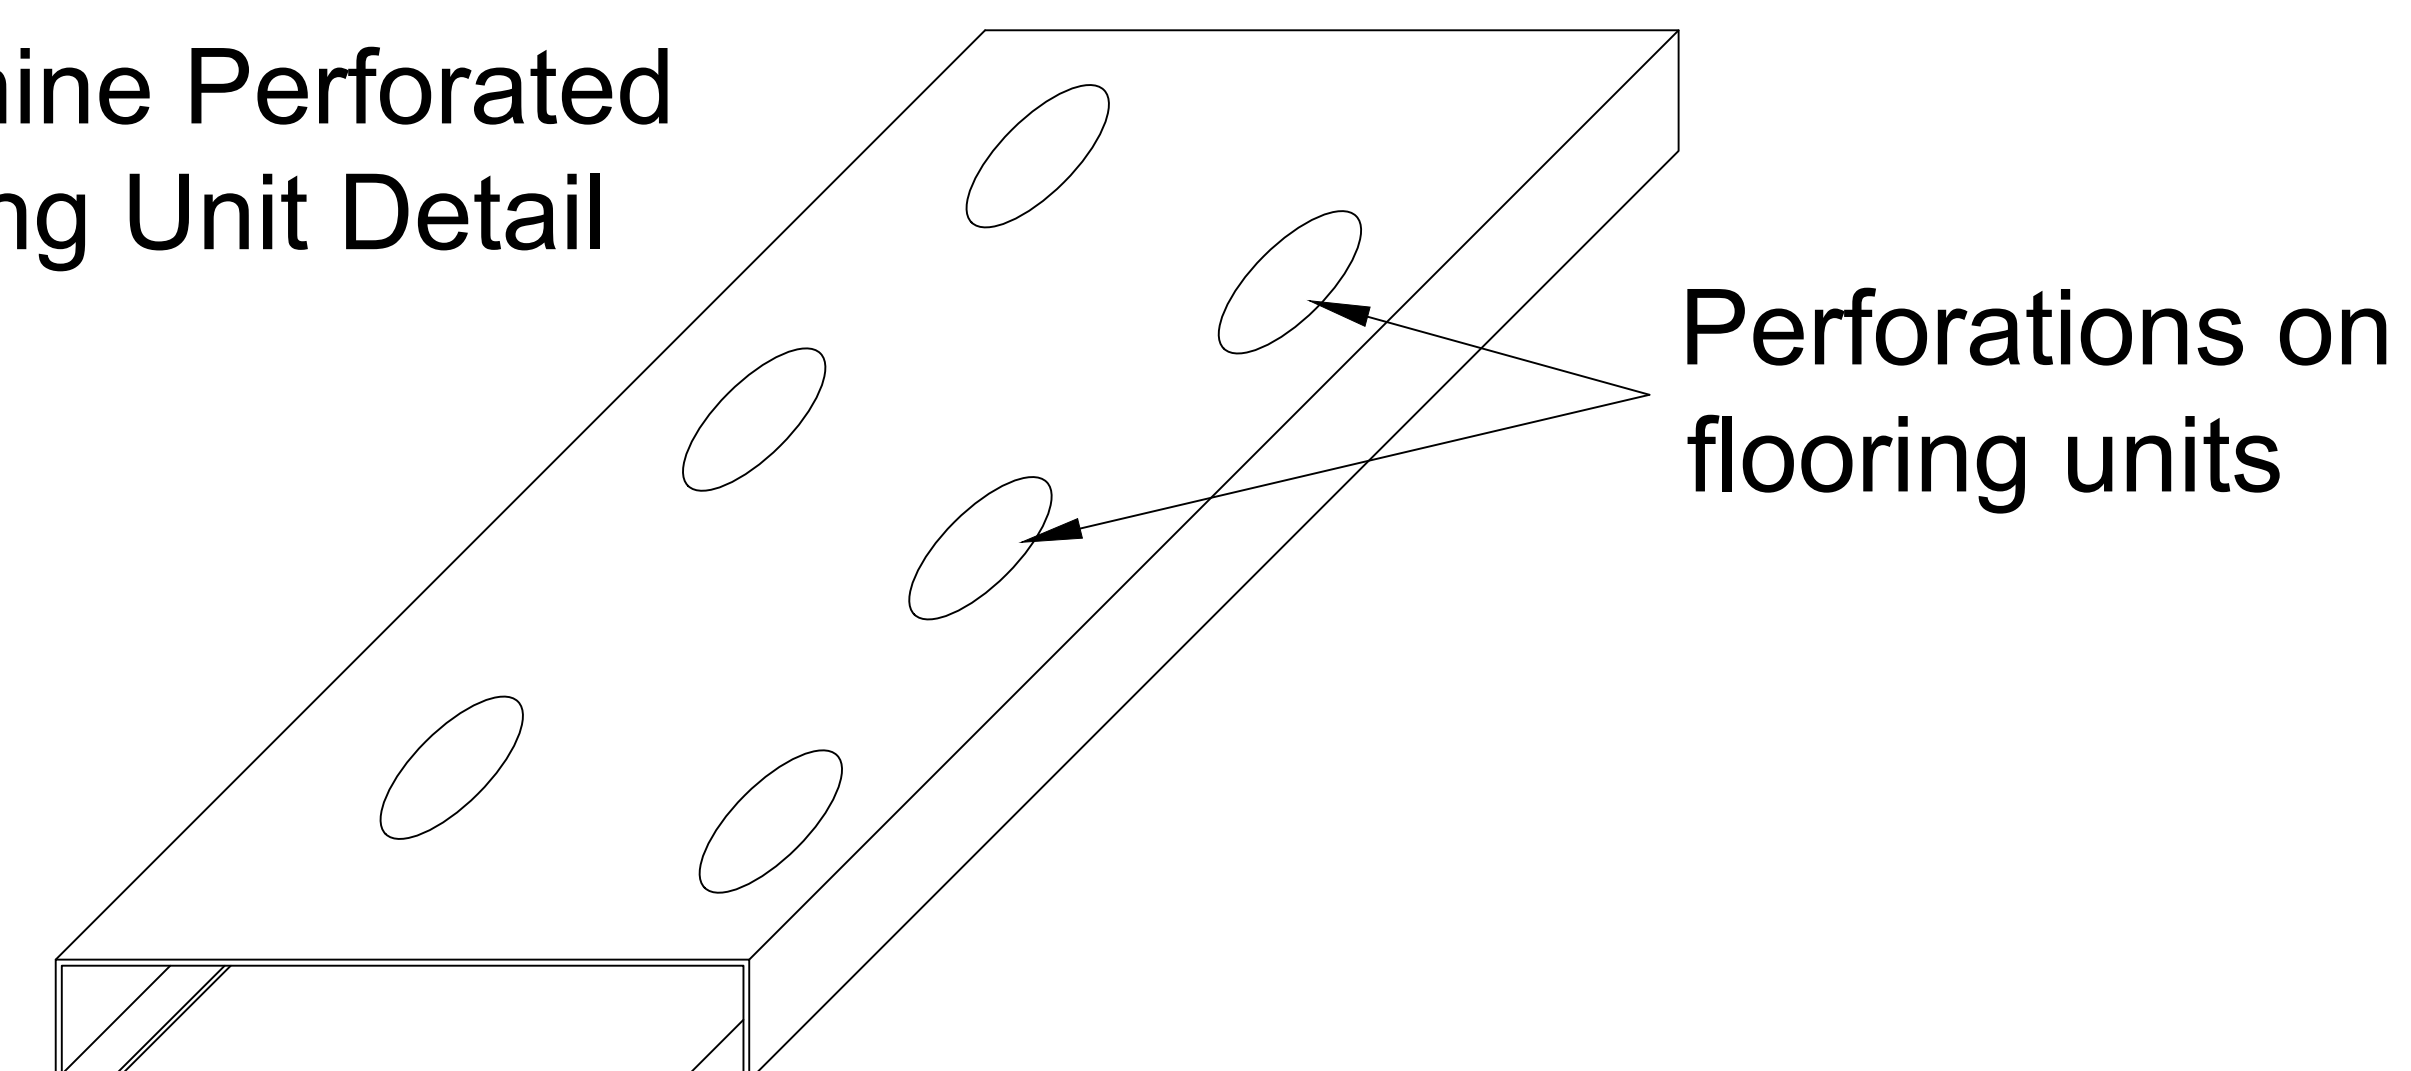

Note: For 75 mm RCC on Ground Floor Use 8mmØ bars @150 mm spacing both ways at bottom only.

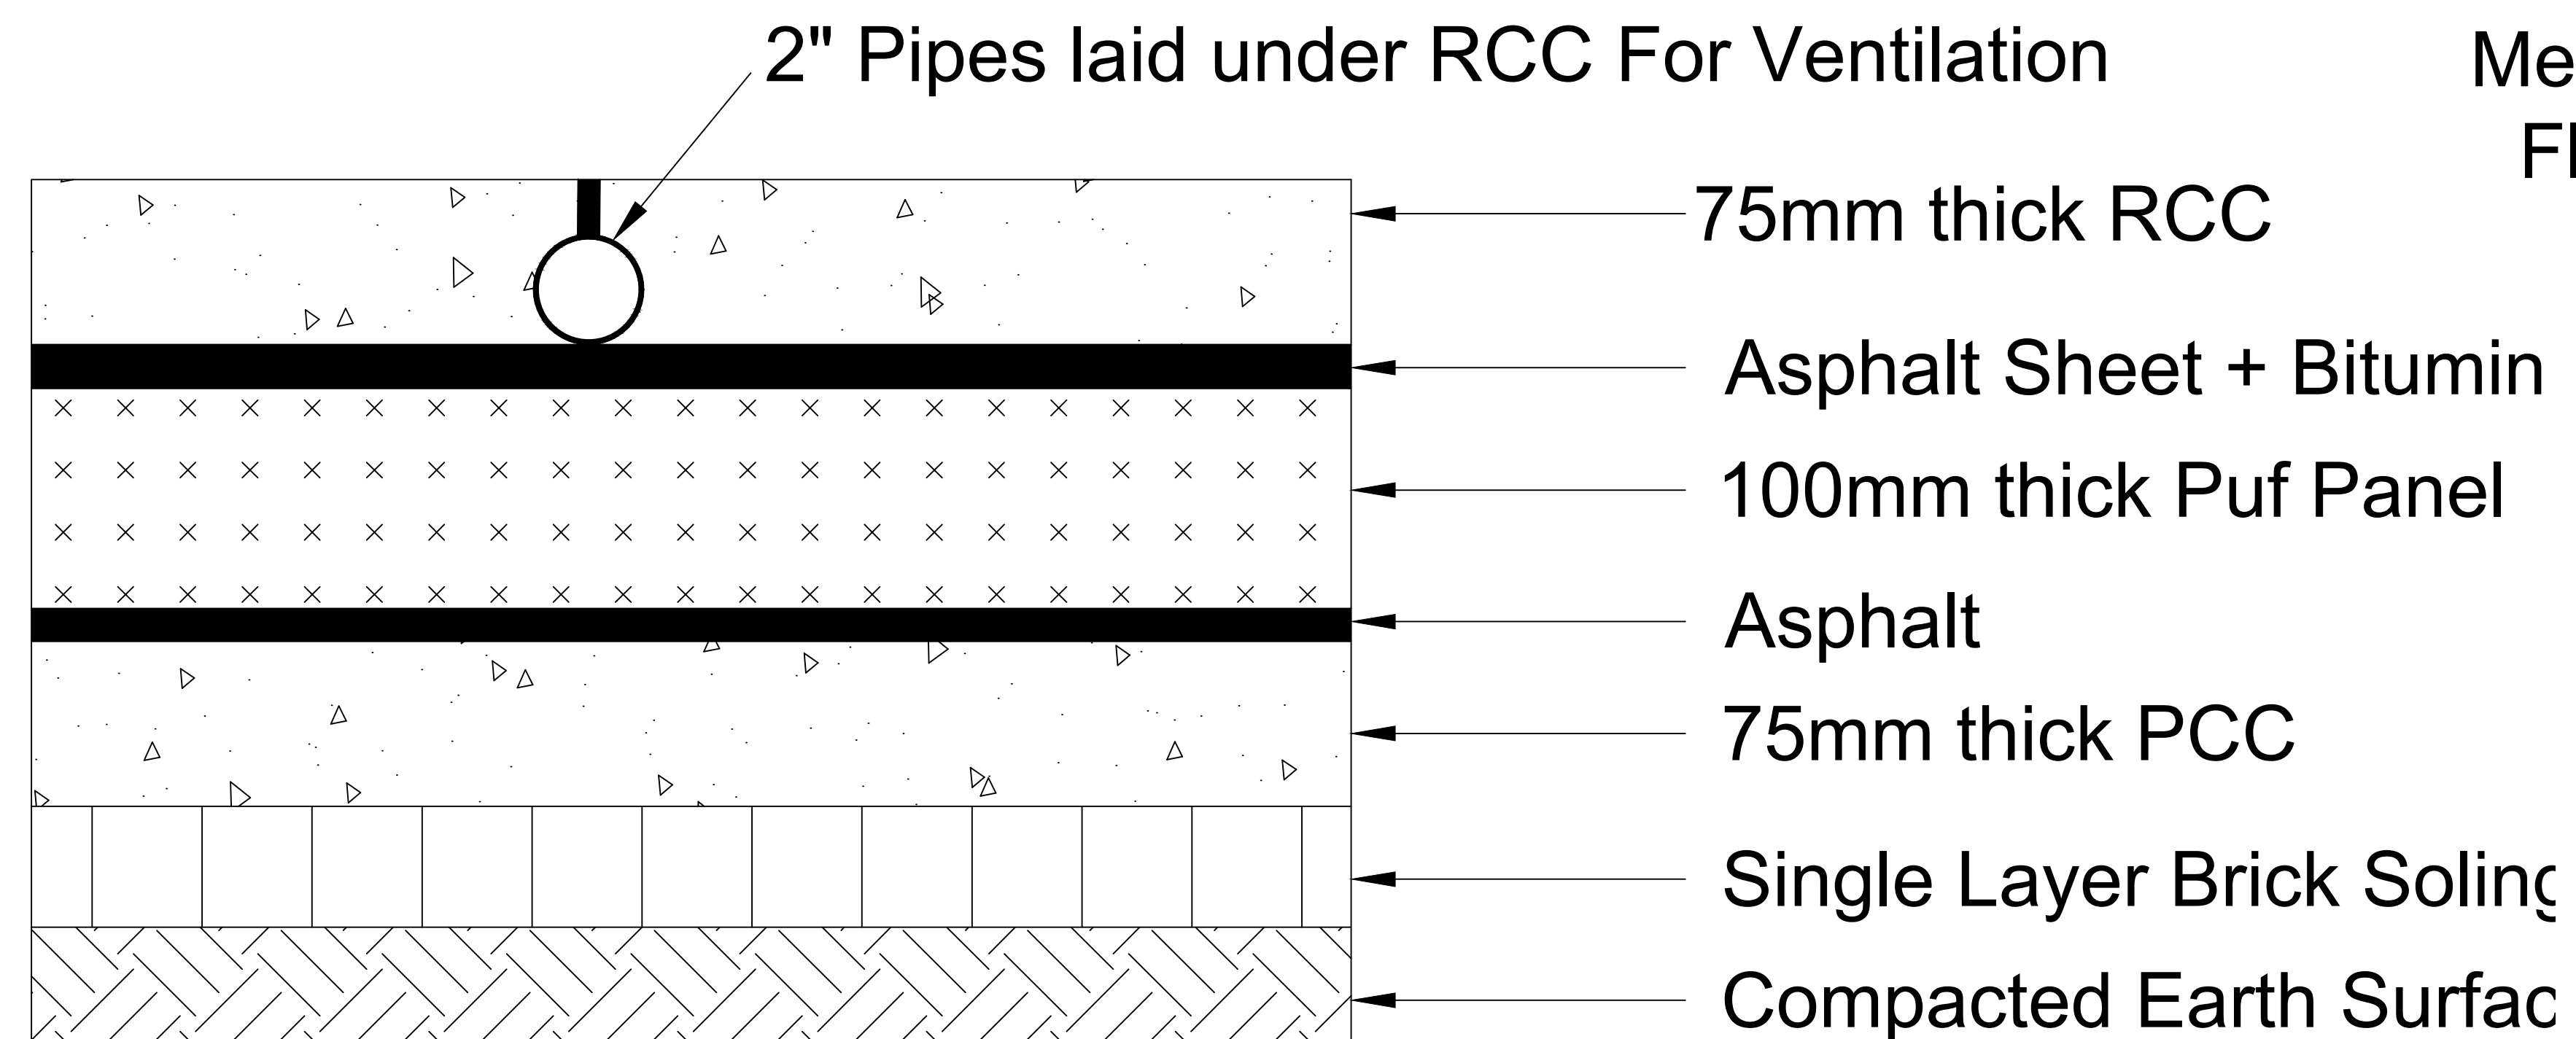

Mezzanine Perforated
Flooring Unit Detail

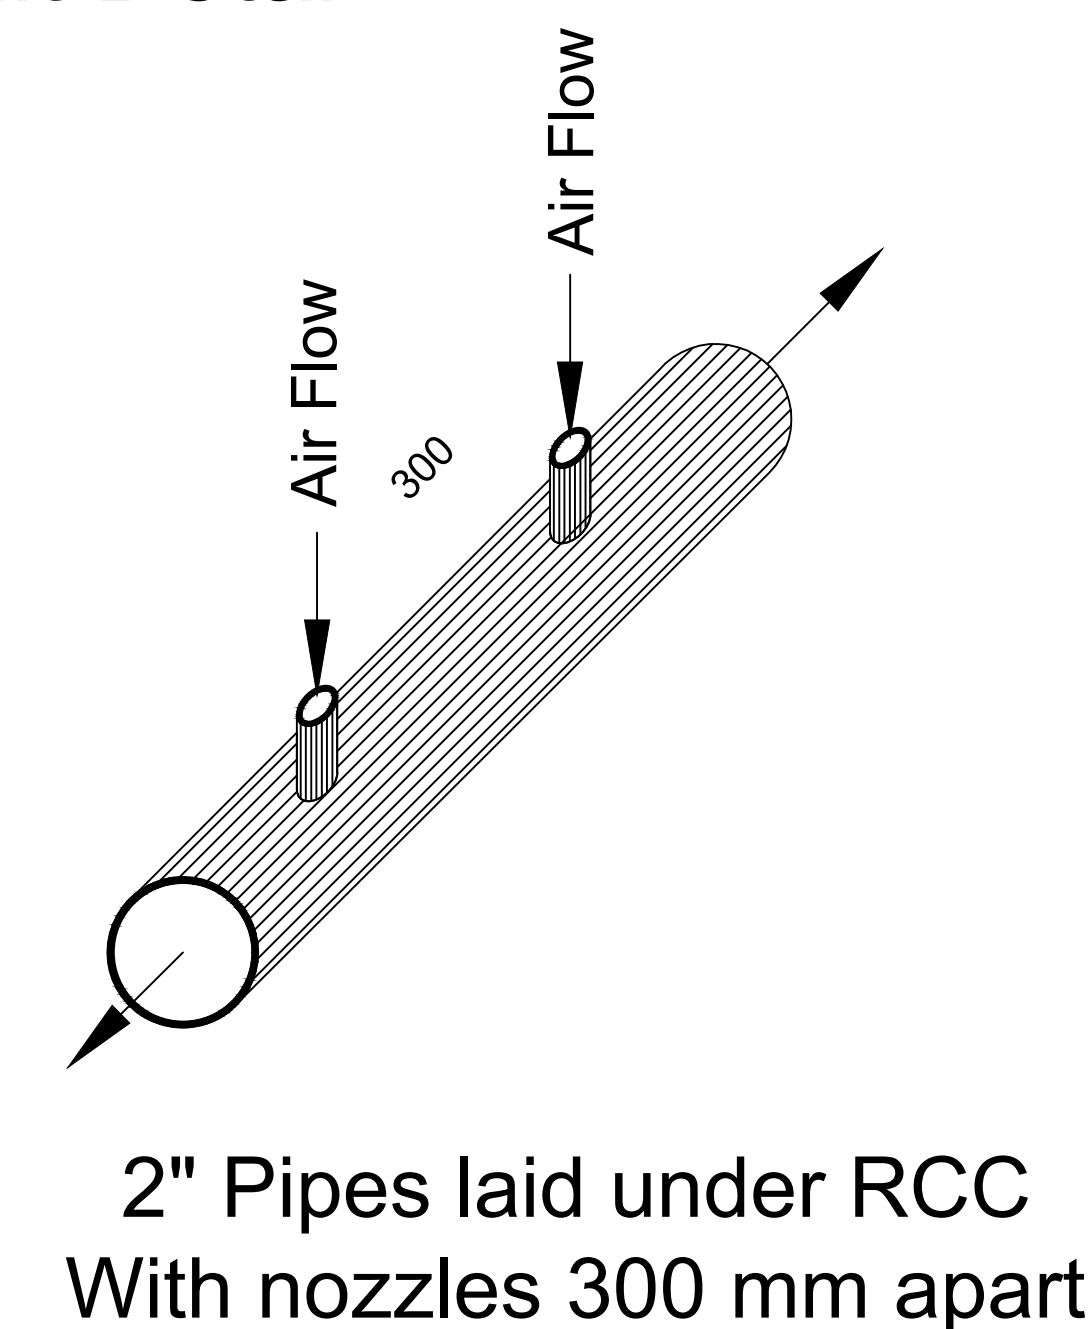



Ground Floor Detail

PROJECT: DPR OF 500MT COLD STORE AT JIRI, DOLAKHA	CONTENT: STRUCTURAL DRAWINGS		CHECKED BY: APPROVED BY :	CONSULTANT: Sworaj Consultants Pvt. Ltd. Samkhushi, Kathmandu	Sheet No
CLIENT: Government of Province Ministry of Land Management, Agriculture and Cooperative Province No. 3, Hetauda	FINAL DRAWING		SCALE :		ST 17
			DATE: REVISION:		


ADMINISTRATION

BLOCK

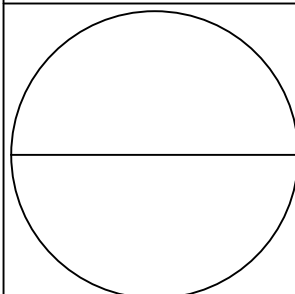
PROJECT: DPR OF 500MT COLD STORE AT JIRI, DOLAKHA	CONTENT: ADMIN BLOCK		CHECKED BY:	CONSULTANT: Sworaj Consultants Pvt. Ltd. Samakhushi, Kathmandu	Sheet No
CLIENT: Government of Province Ministry of Land Management, Agriculture and Cooperative Province No. 3, Hetauda	FINAL DRAWING		APPROVED BY :		
			SCALE :		
			DATE:	REVISION:	

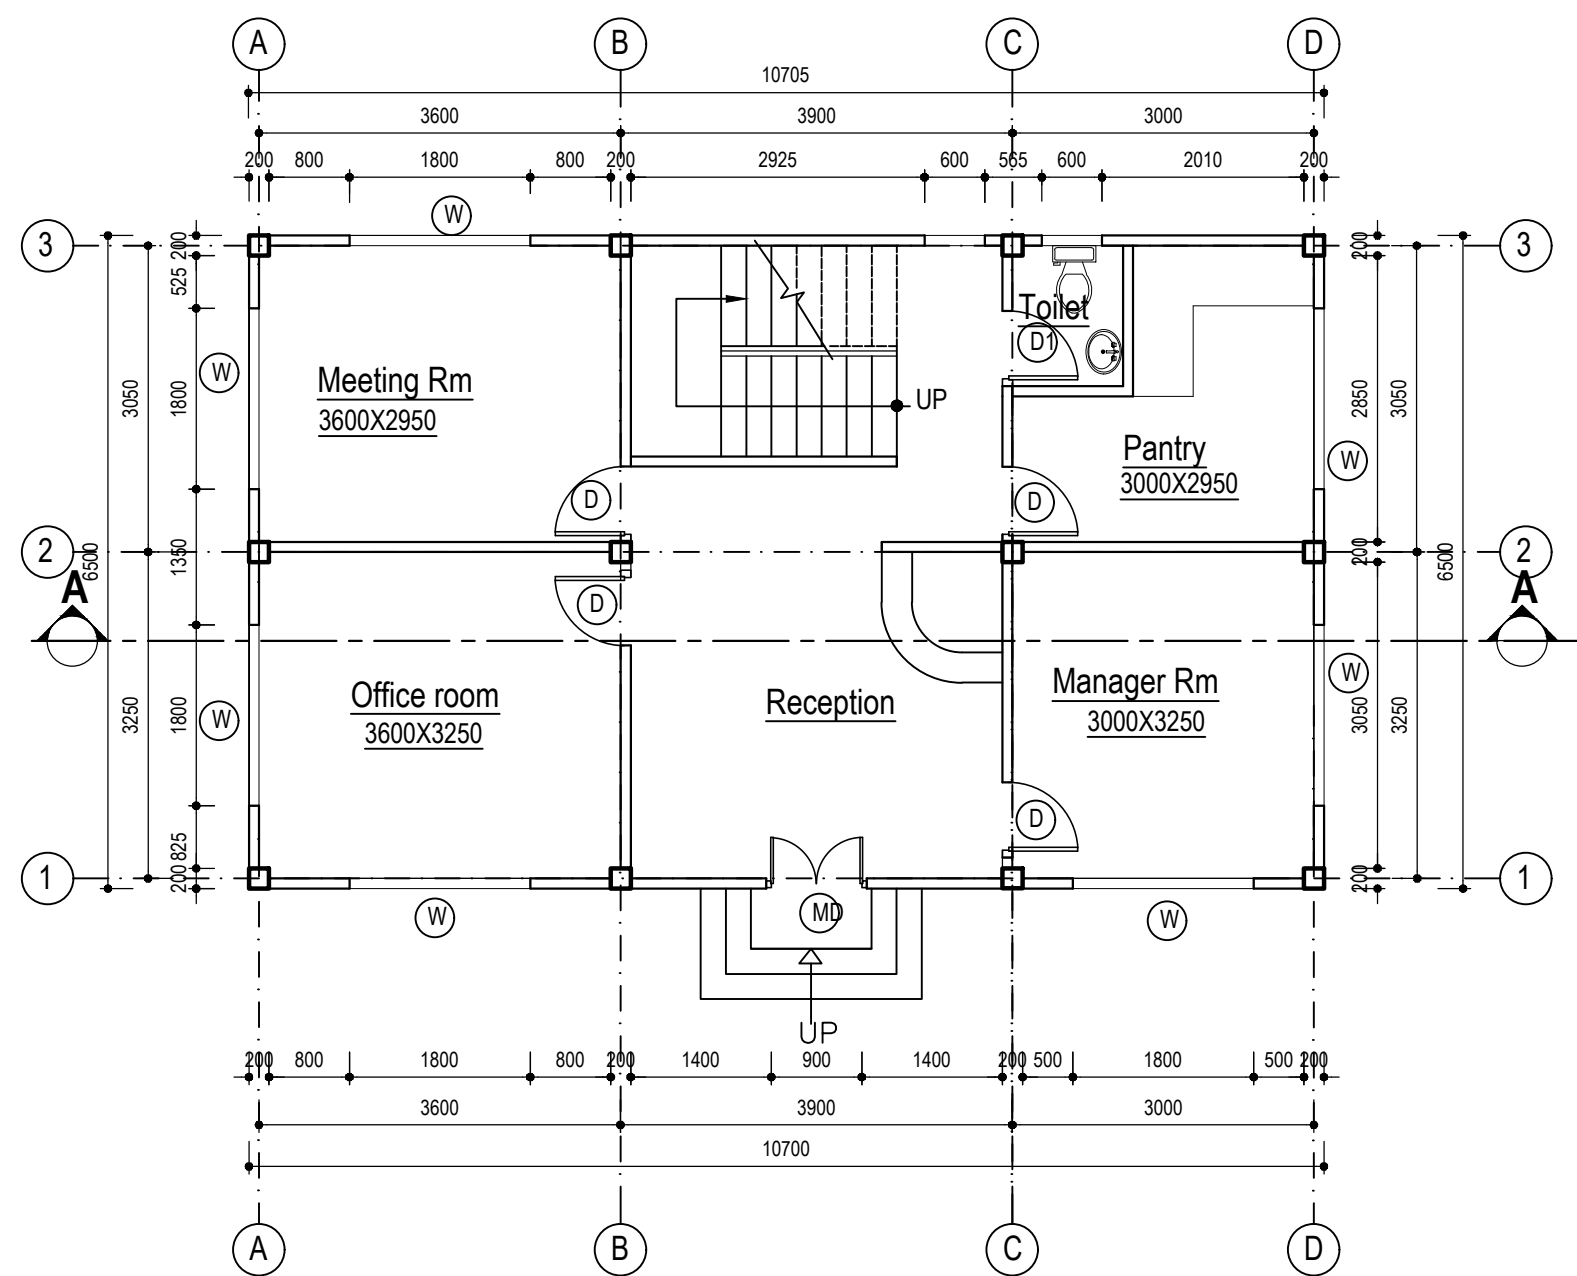

Ground Floor Plan
Floor Area:69.550 Sq.m

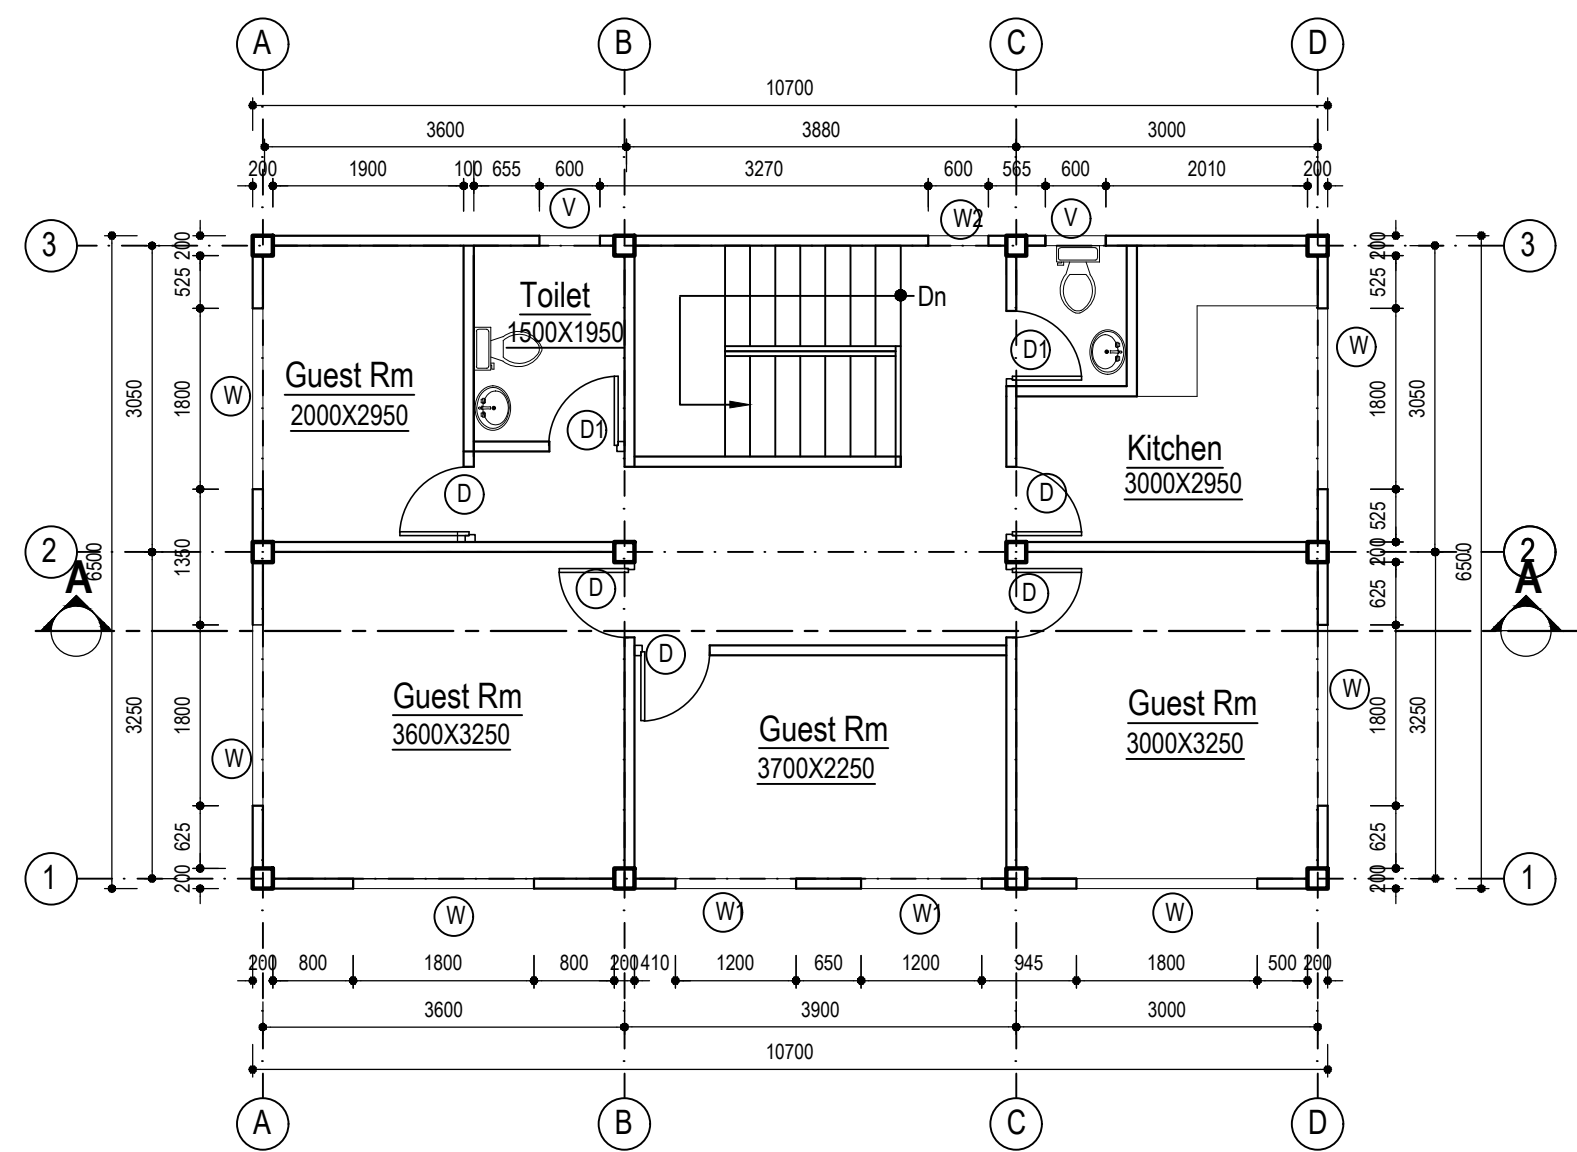


FIRST Floor Plan
Floor Area:69.550 Sq.m

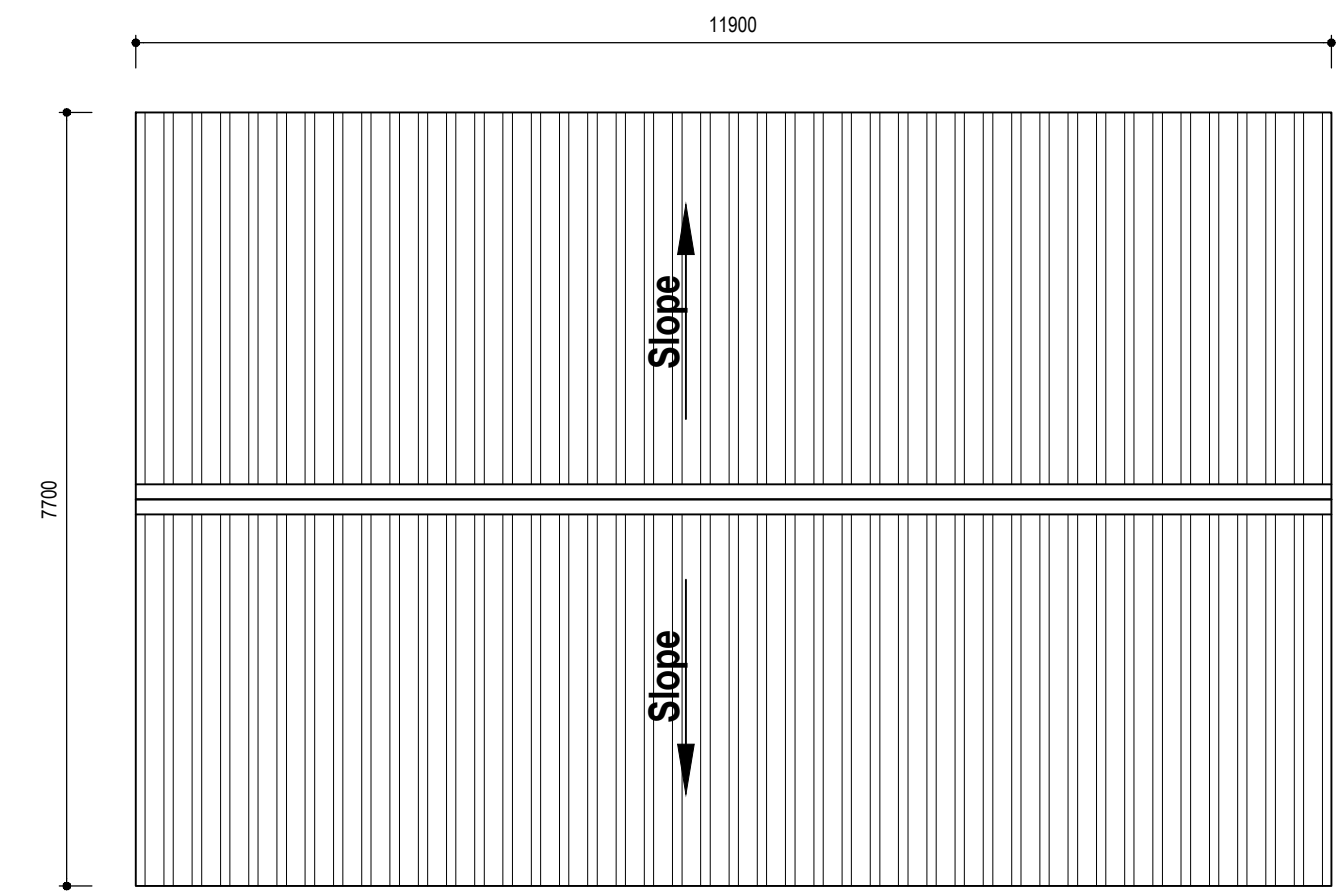


Roof Plan




South Elevation

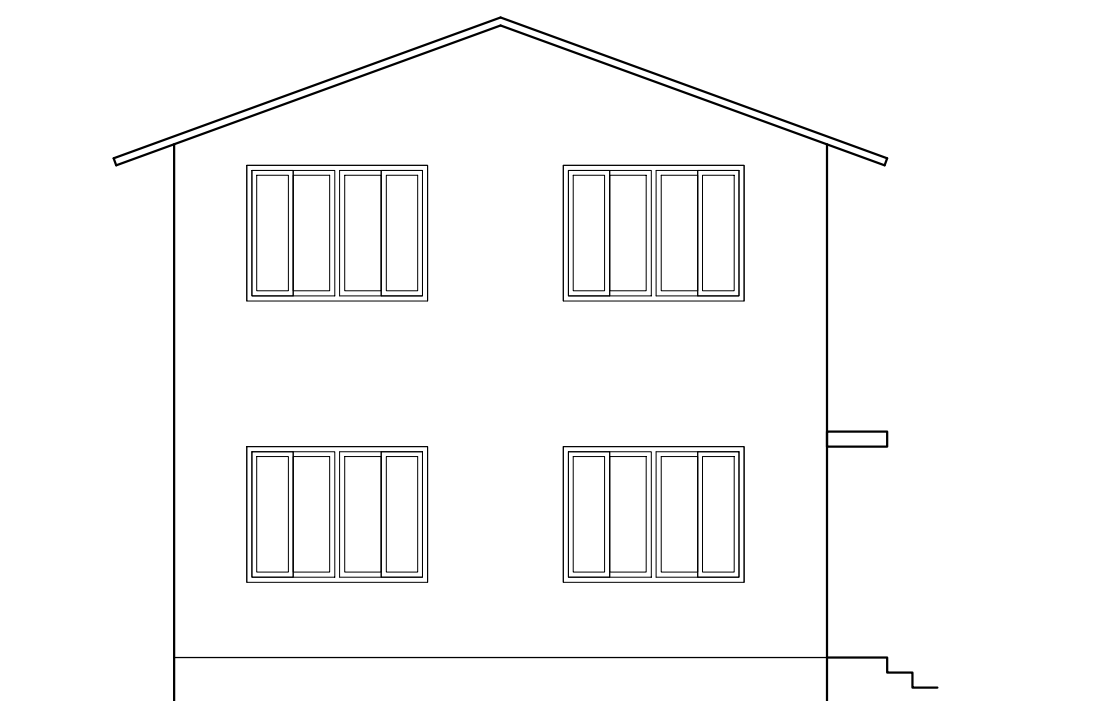


West Elevation

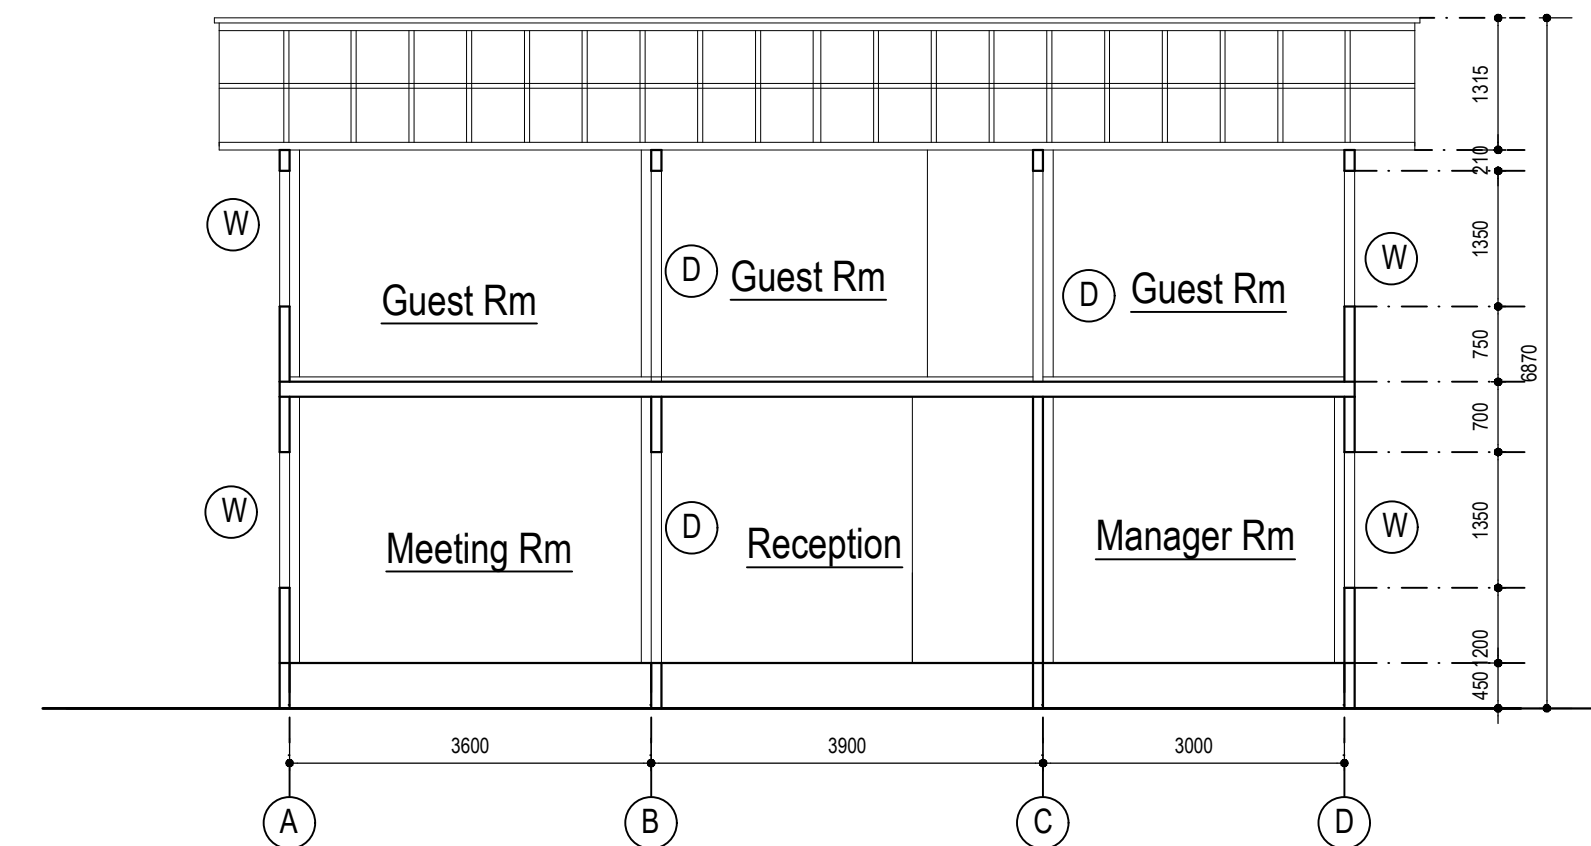


Section At A-A

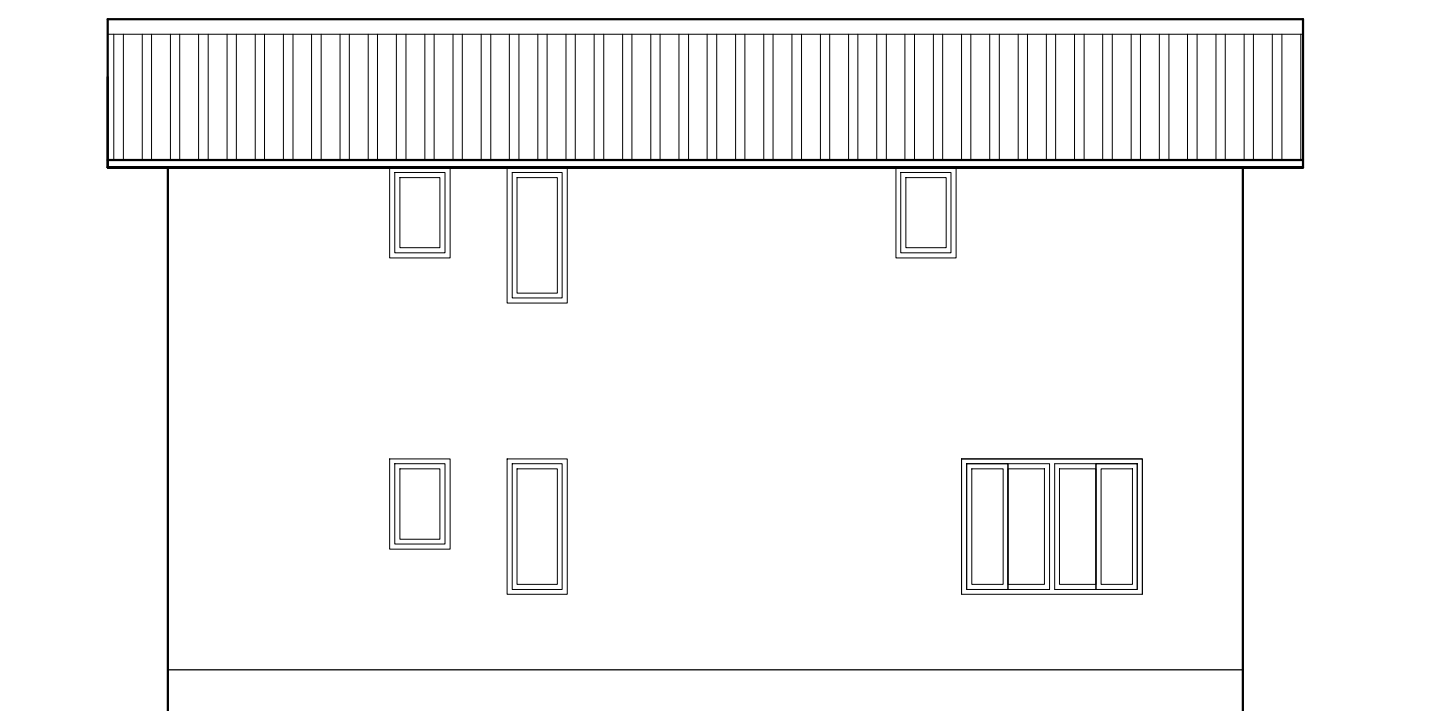

North Elevation

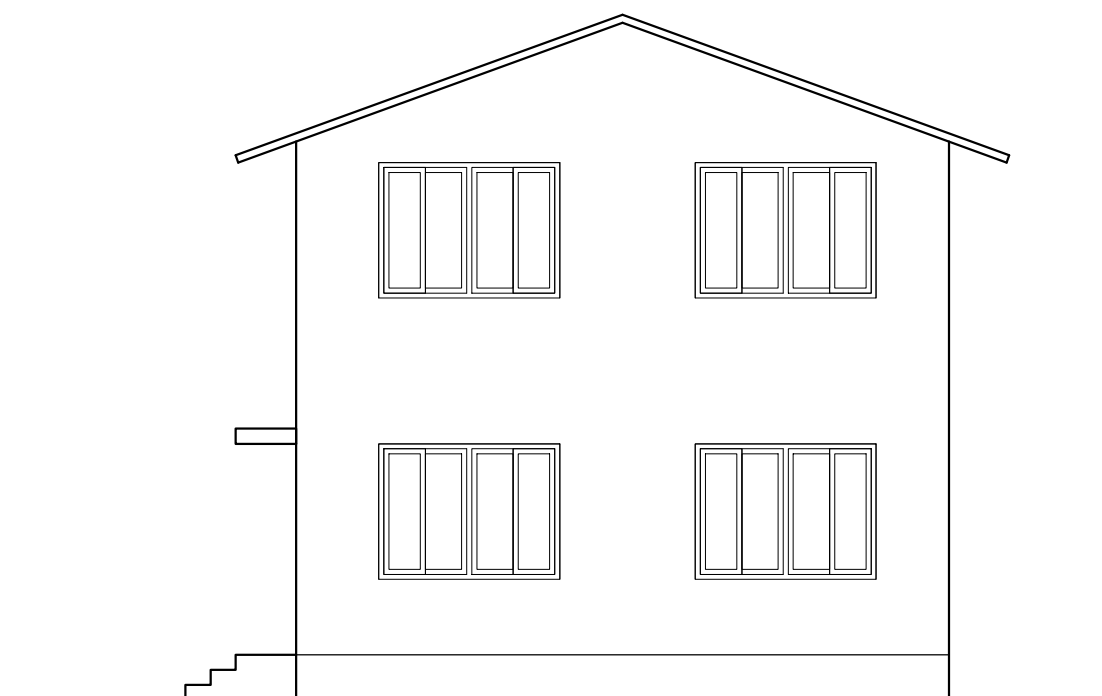

East Elevation

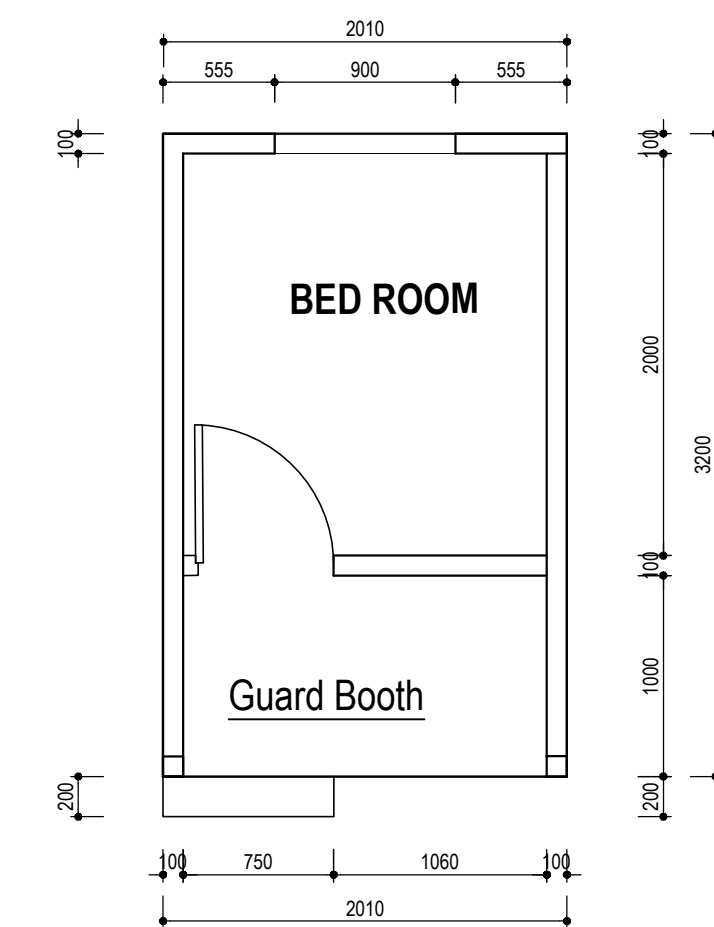

Guard Booth Plan
Floor Area:26.00 Sq.m

PROJECT:
DPR OF 500MT COLD STORE AT JIRI, DOLAKHA

CLIENT:
Government of Province
Ministry of Land Management, Agriculture and Cooperative
Province No. 3, Hetauda

CONTENT:
ADMINISTRATION BLOCK

FINAL DRAWING

ARCHITECT :

STR. ENGINEER:

CHECKED BY:

APPROVED BY :

SCALE :

DATE:


REVISION:

CONSULTANT:


Sworaj Consultants Pvt. Ltd.
Samkhushi, Kathmandu

Sheet No



AR
07

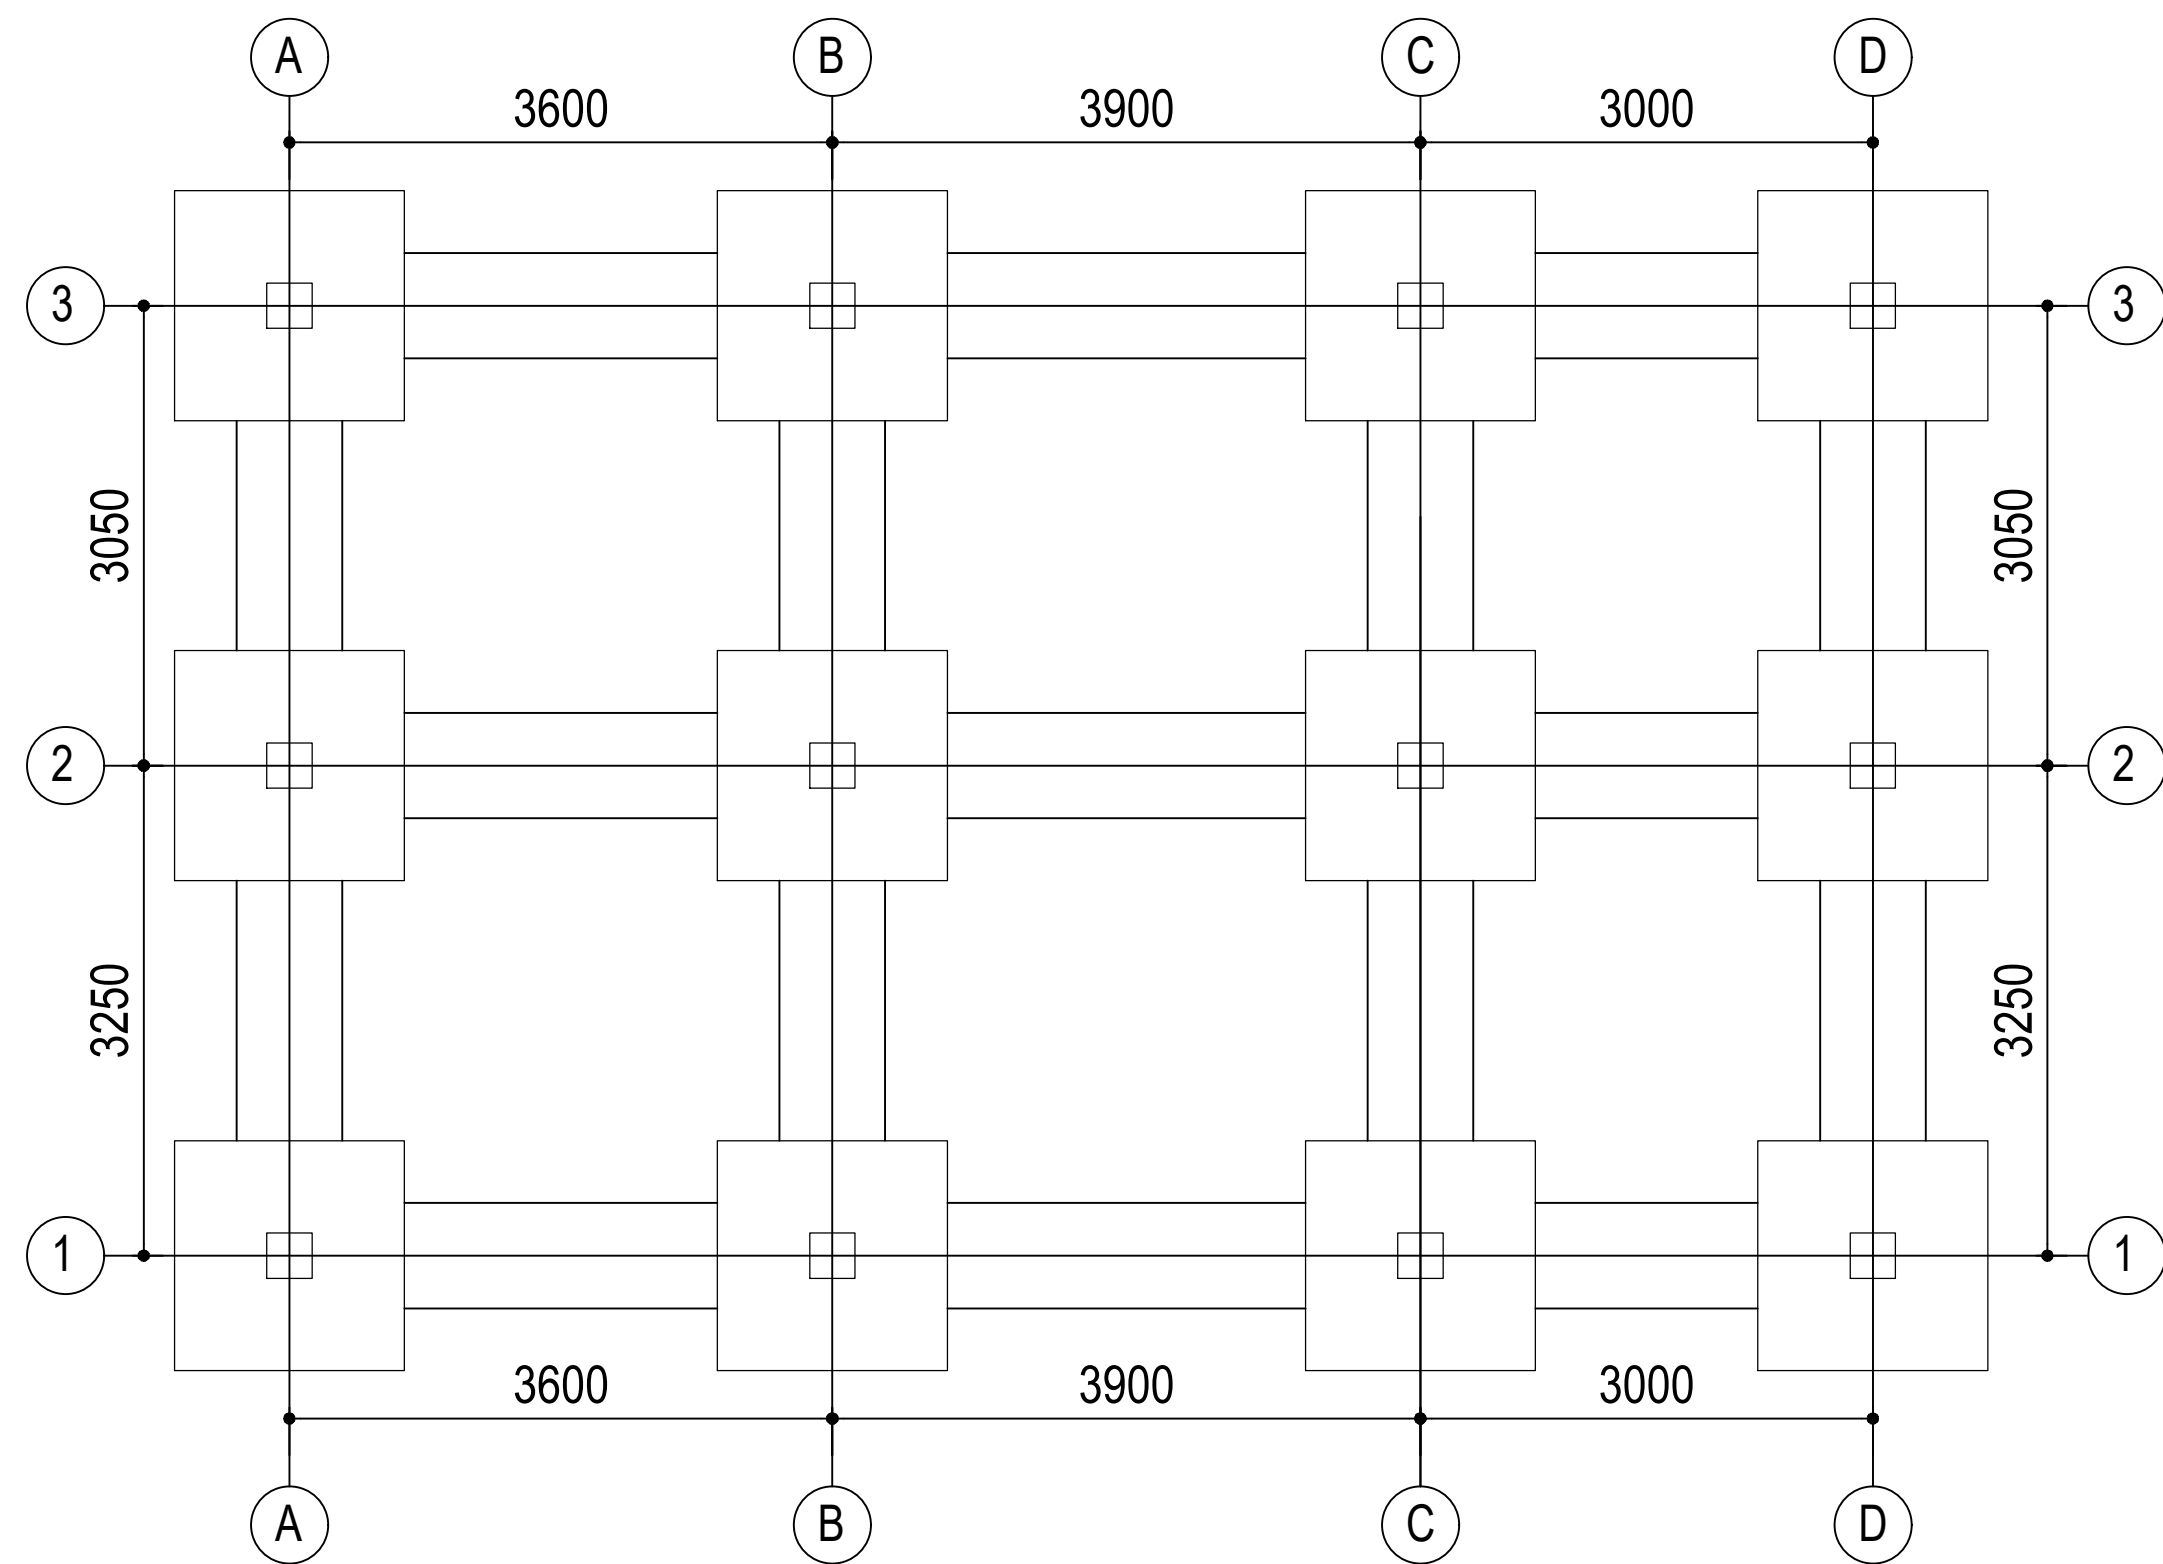

FOOTING TRENCH PLAN

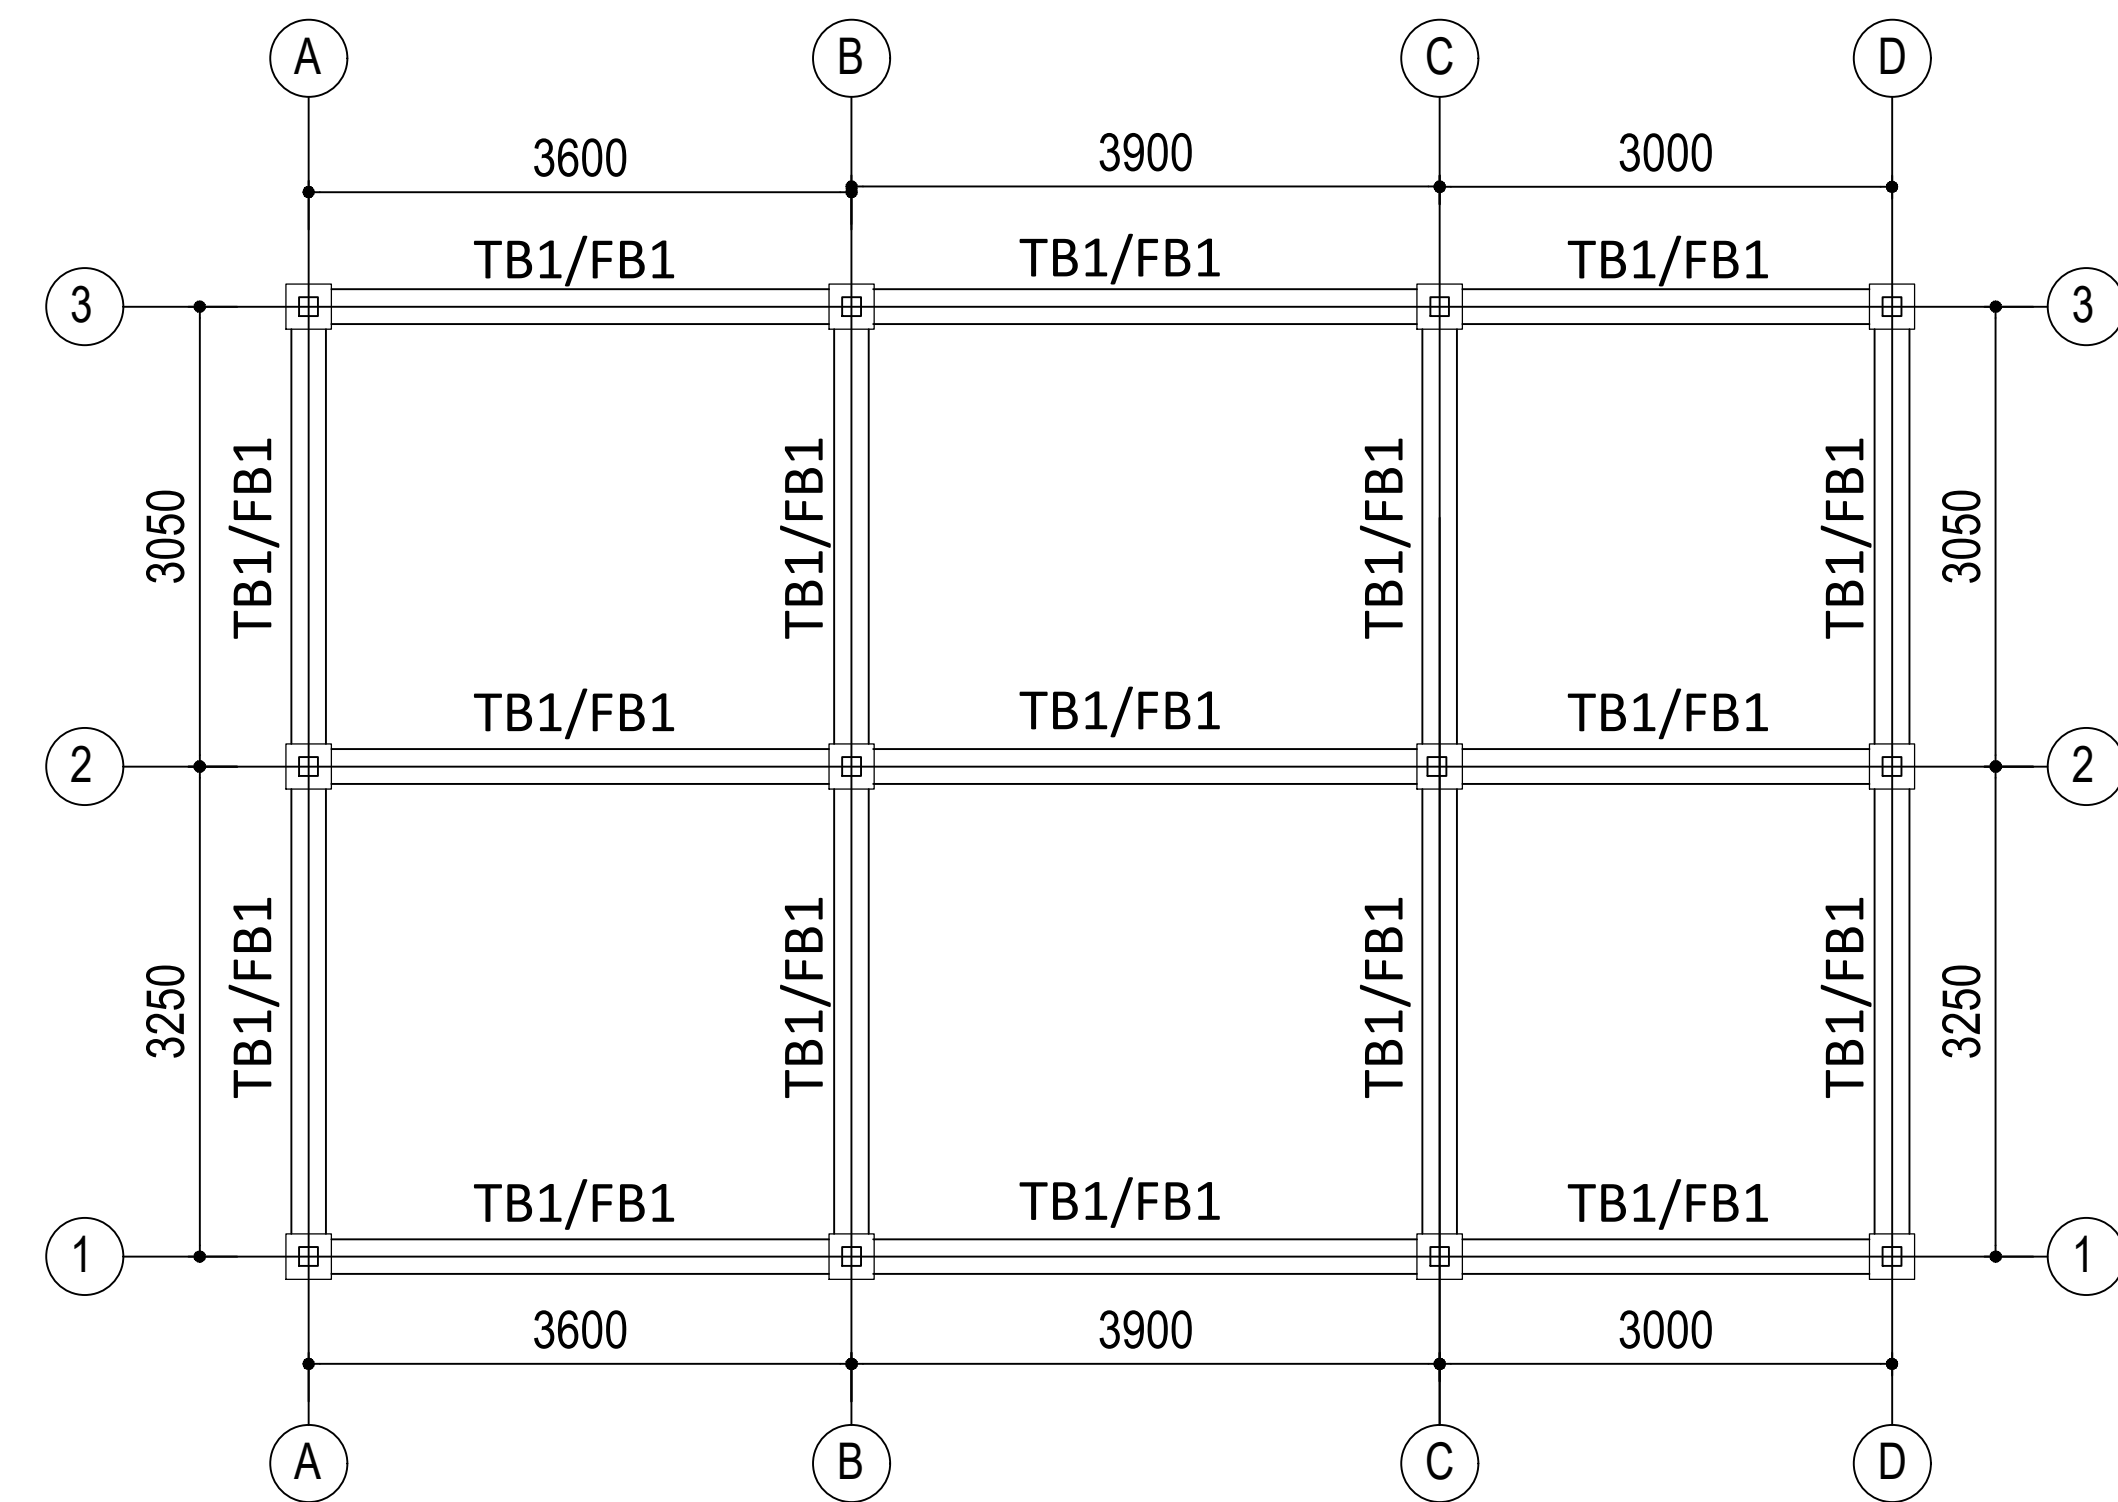


TIE BEAM LAYOUT PLAN

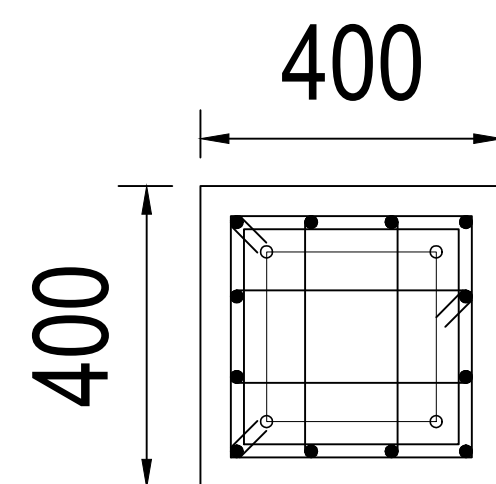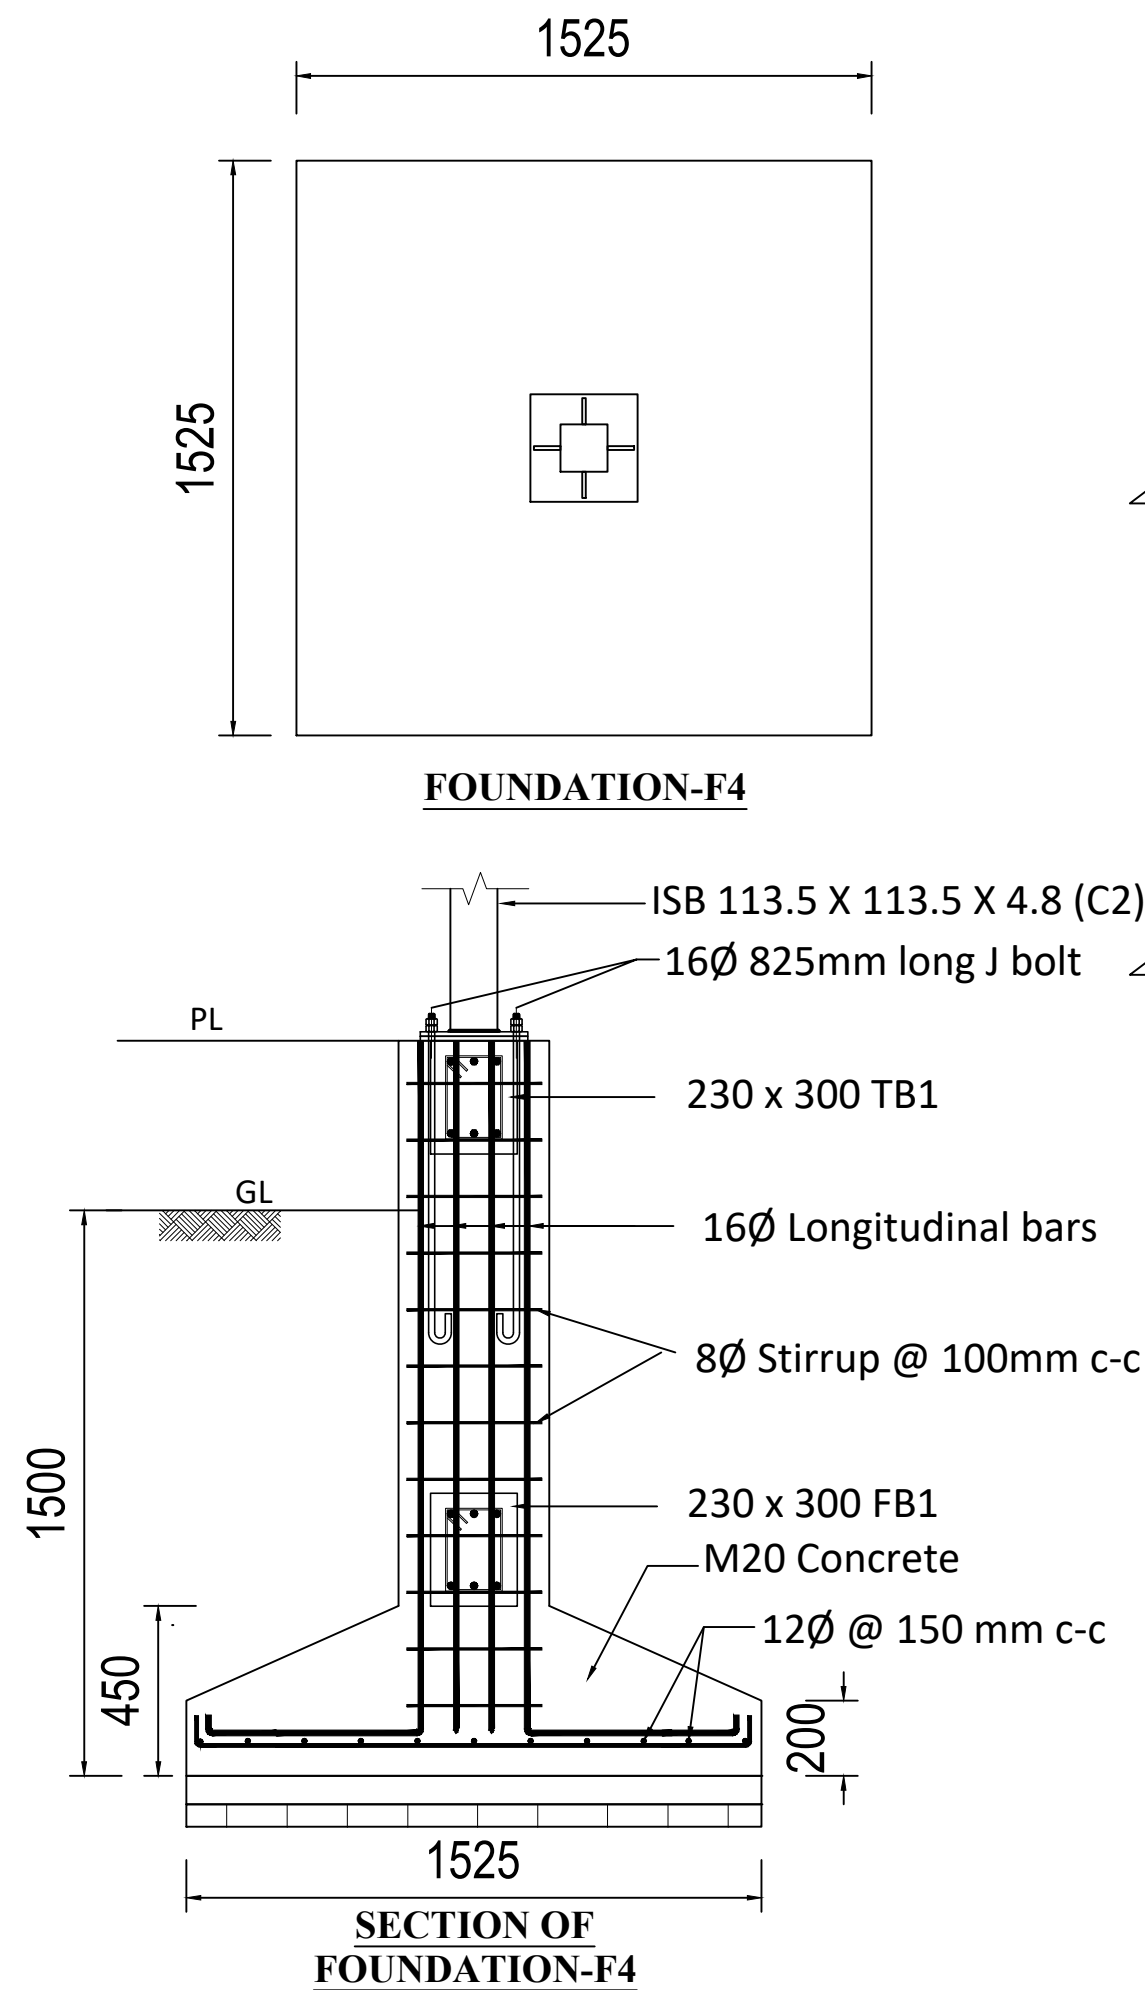


PEDESTAL DETAIL OF FOUNDATION-F1


STIFFENER - S1
(10mm thick)

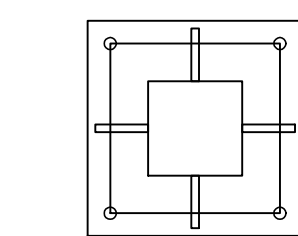


BASE PLATE DETAIL
(285x285x12)
(For Vertical Post - C2)

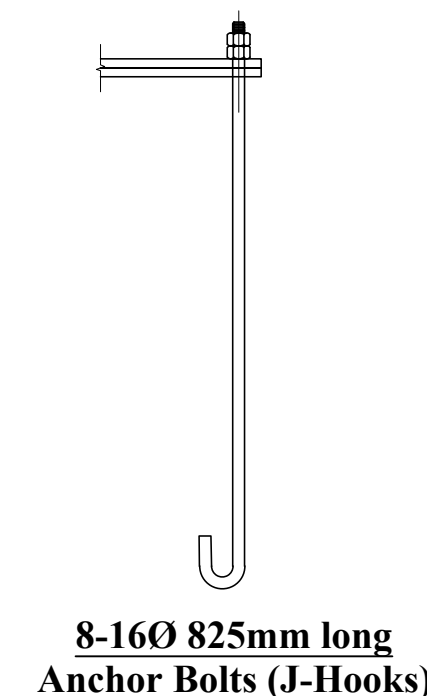


8-16Ø 825mm long
Anchor Bolts (J-Hooks)

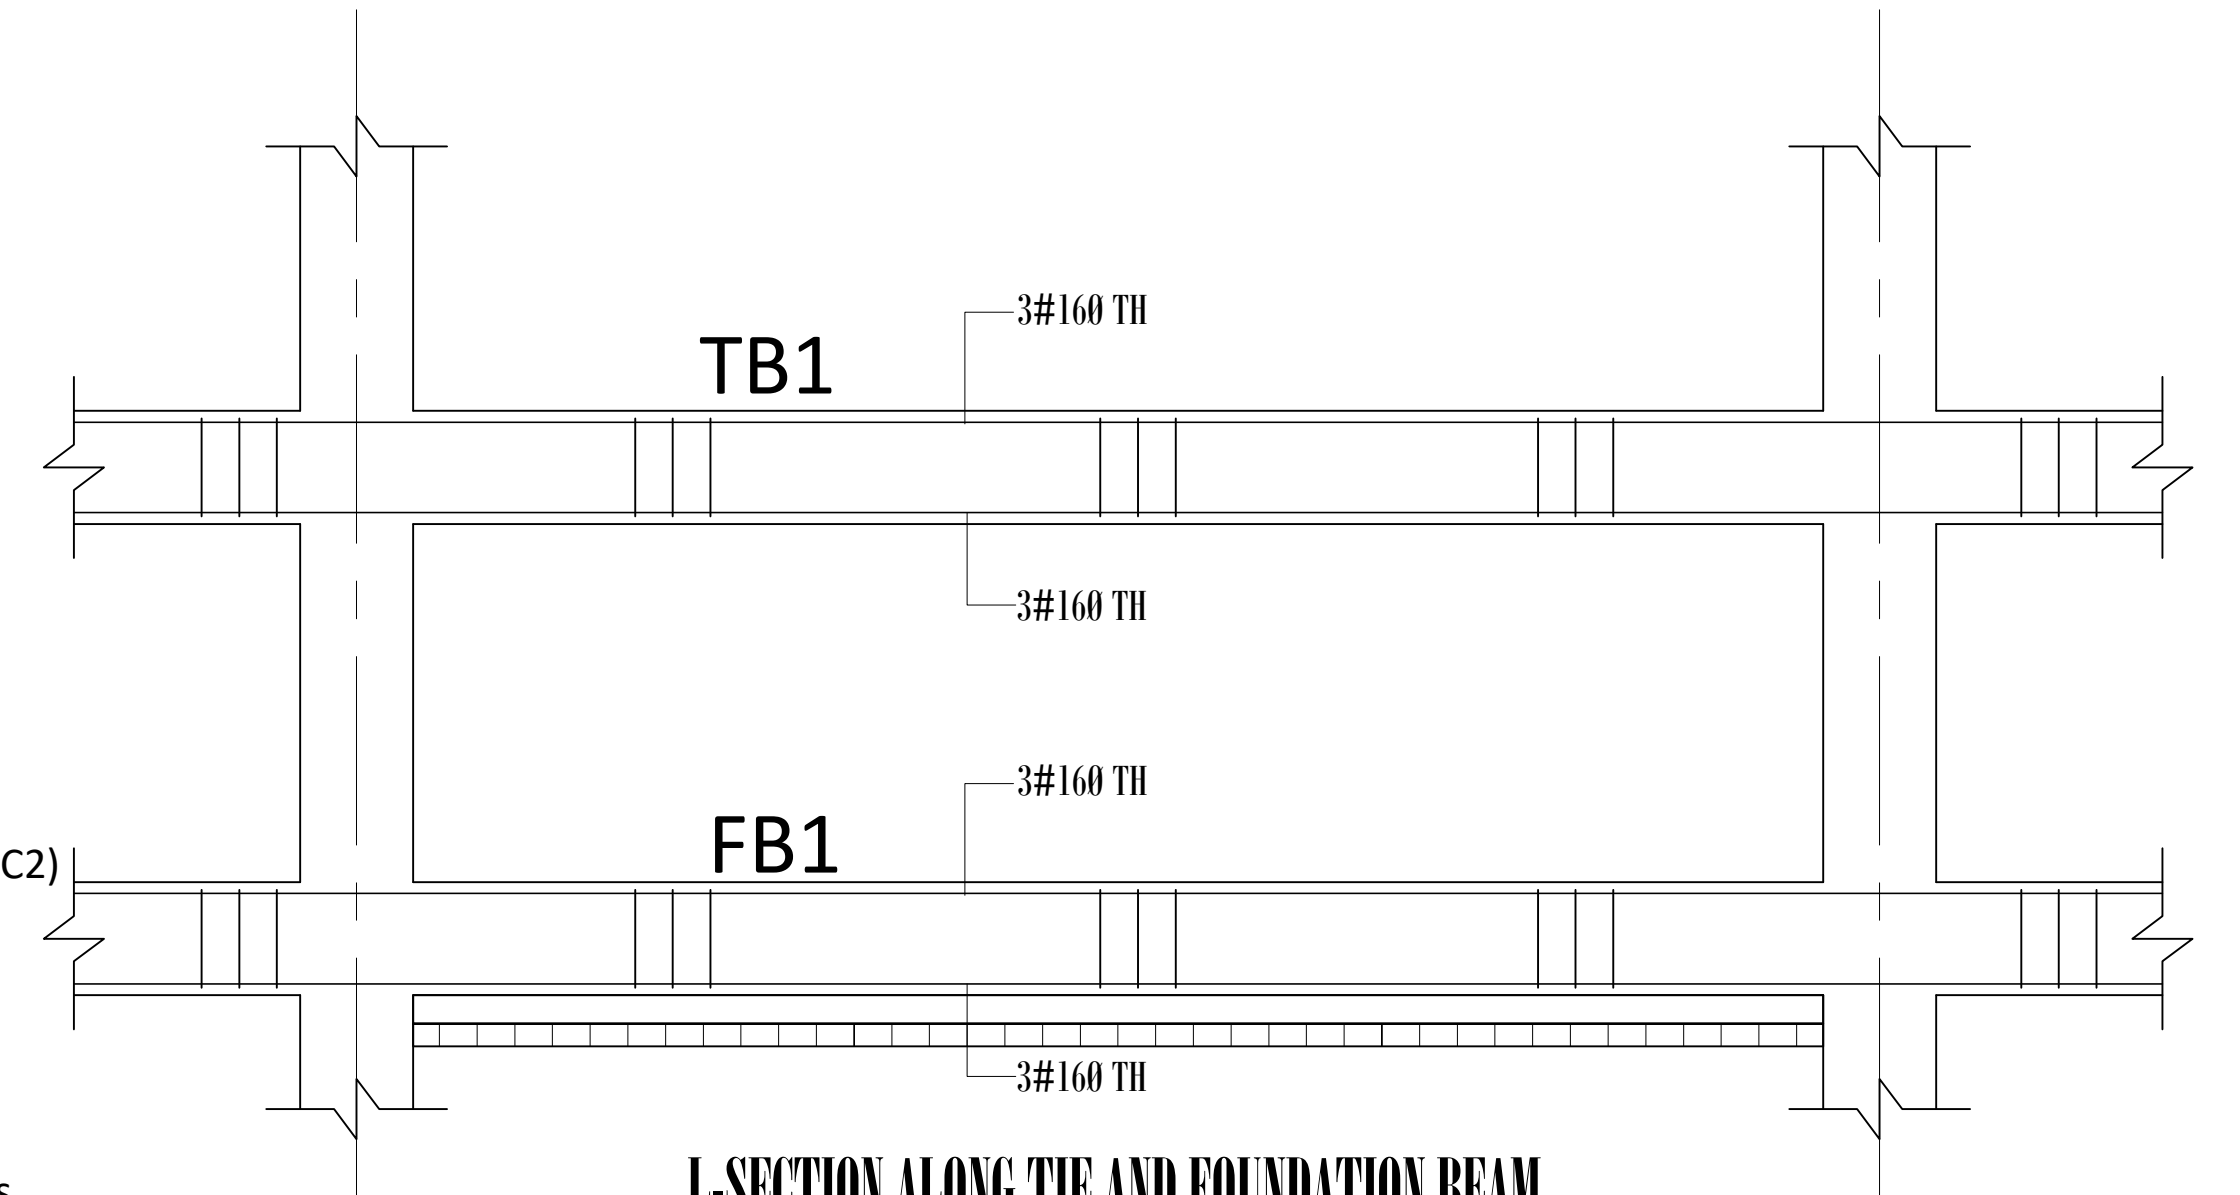


L-SECTION ALONG TIE AND FOUNDATION BEAM

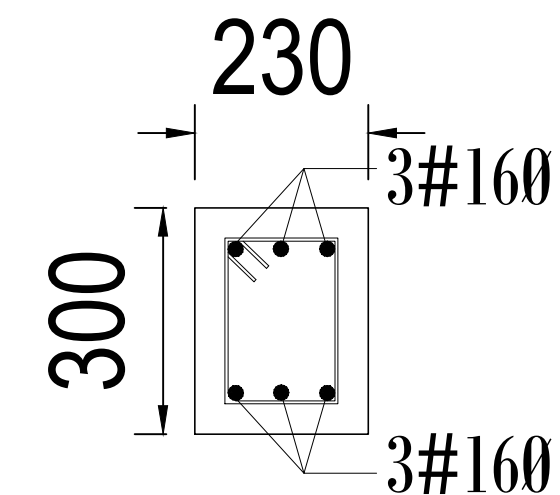

SECTION OF TIE BEAM (TB1)

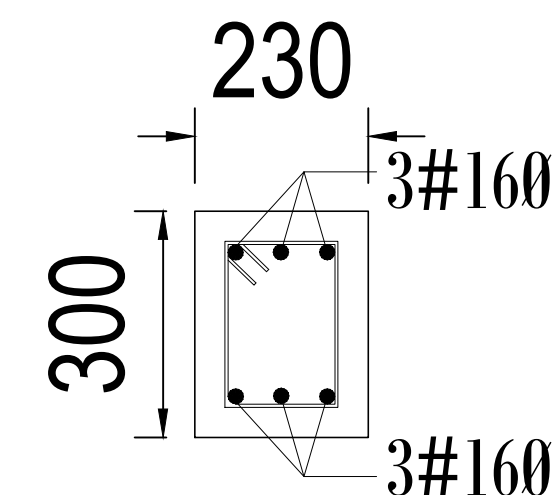


SECTION OF FOUNDATION BEAM (FB1)

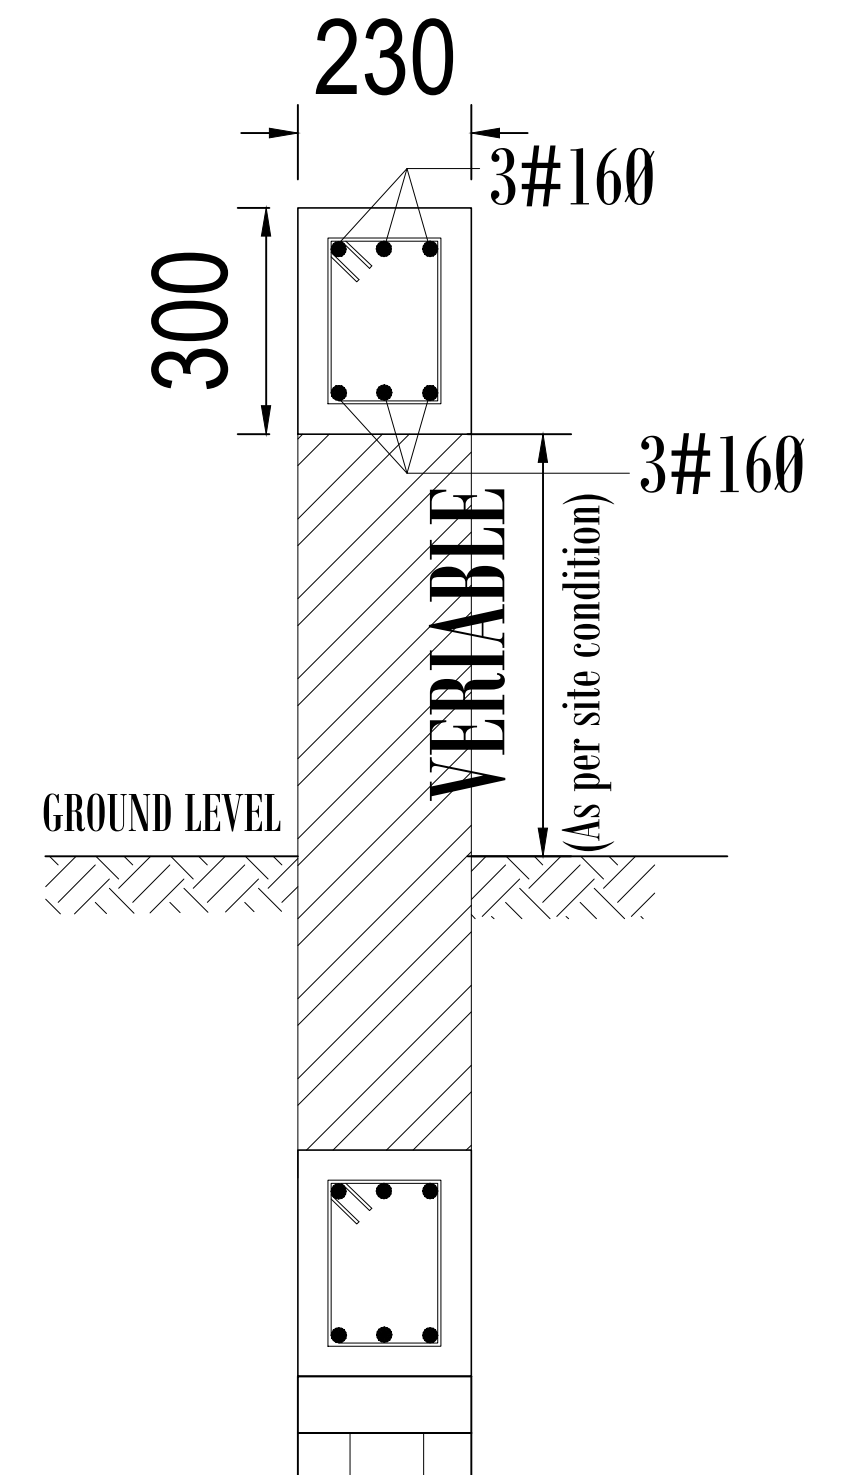


TOE WALL DETAIL


PROJECT: DPR OF 500MT COLD STORE AT JIRI, DOLAKHA	CONTENT: ADMIN BLOCK		CHECKED BY: 	CONSULTANT: Sworaj Consultants Pvt. Ltd. Samakhushi, Kathmandu	Sheet No
CLIENT: Government of Province Ministry of Land Management, Agriculture and Cooperative Province No. 3, Hetauda	FINAL DRAWING		APPROVED BY :		AD 02
			SCALE : DATE: REVISION:		

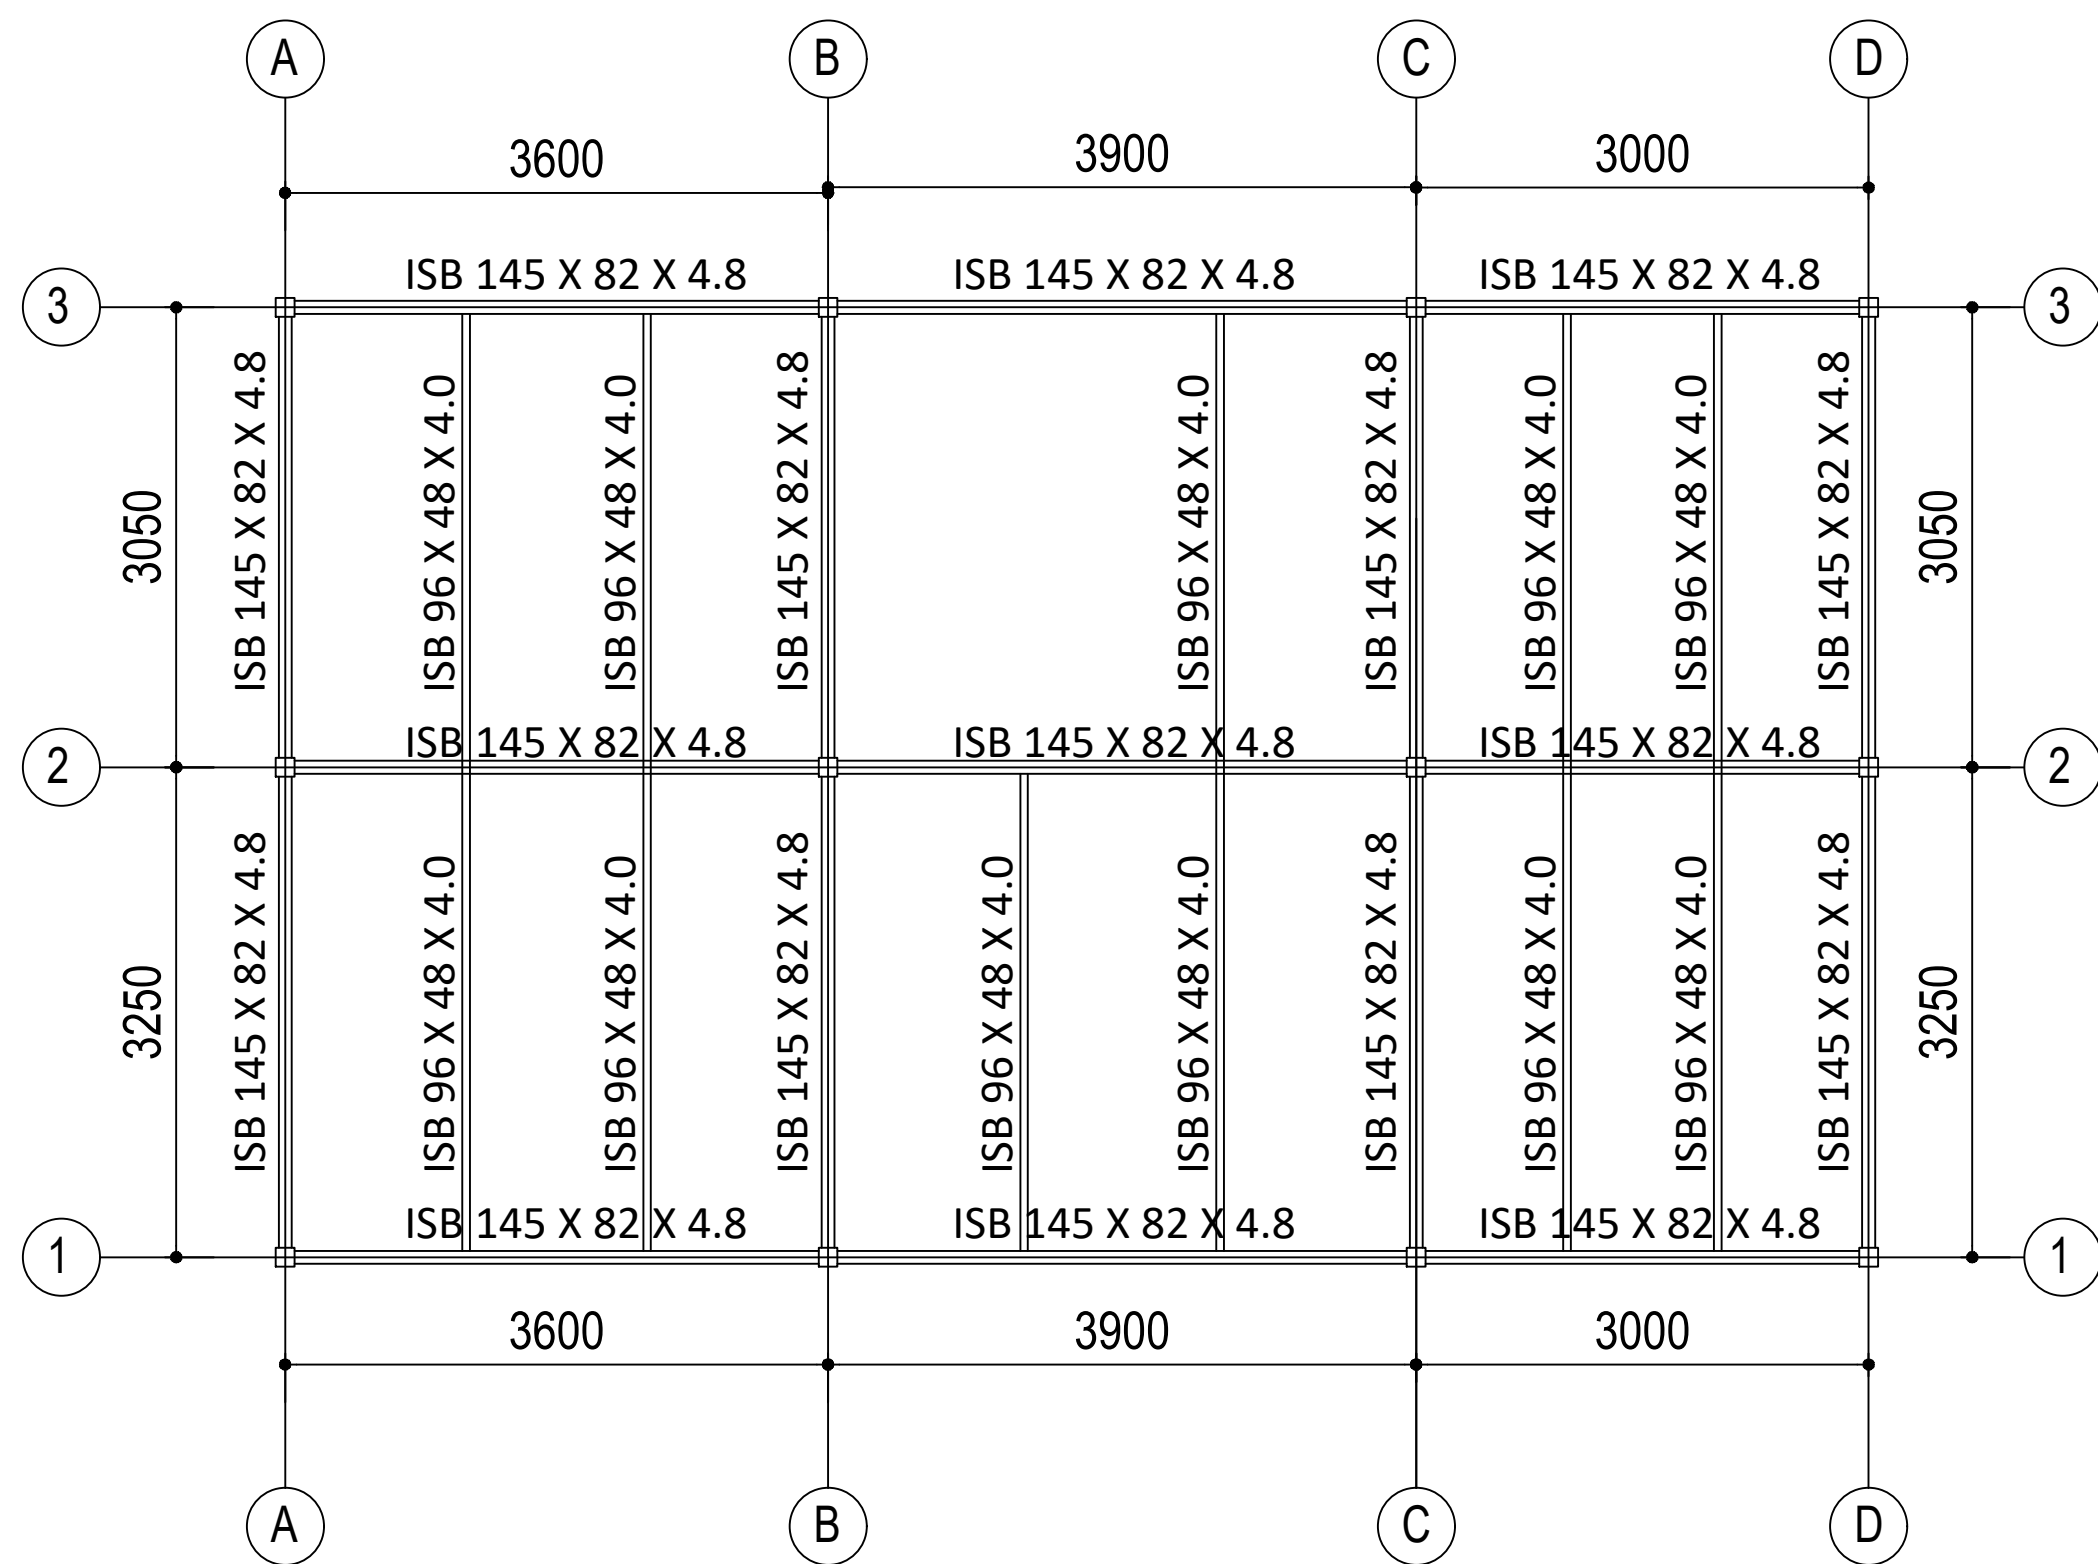


FIRST FLOOR BEAM LAYOUT PLAN

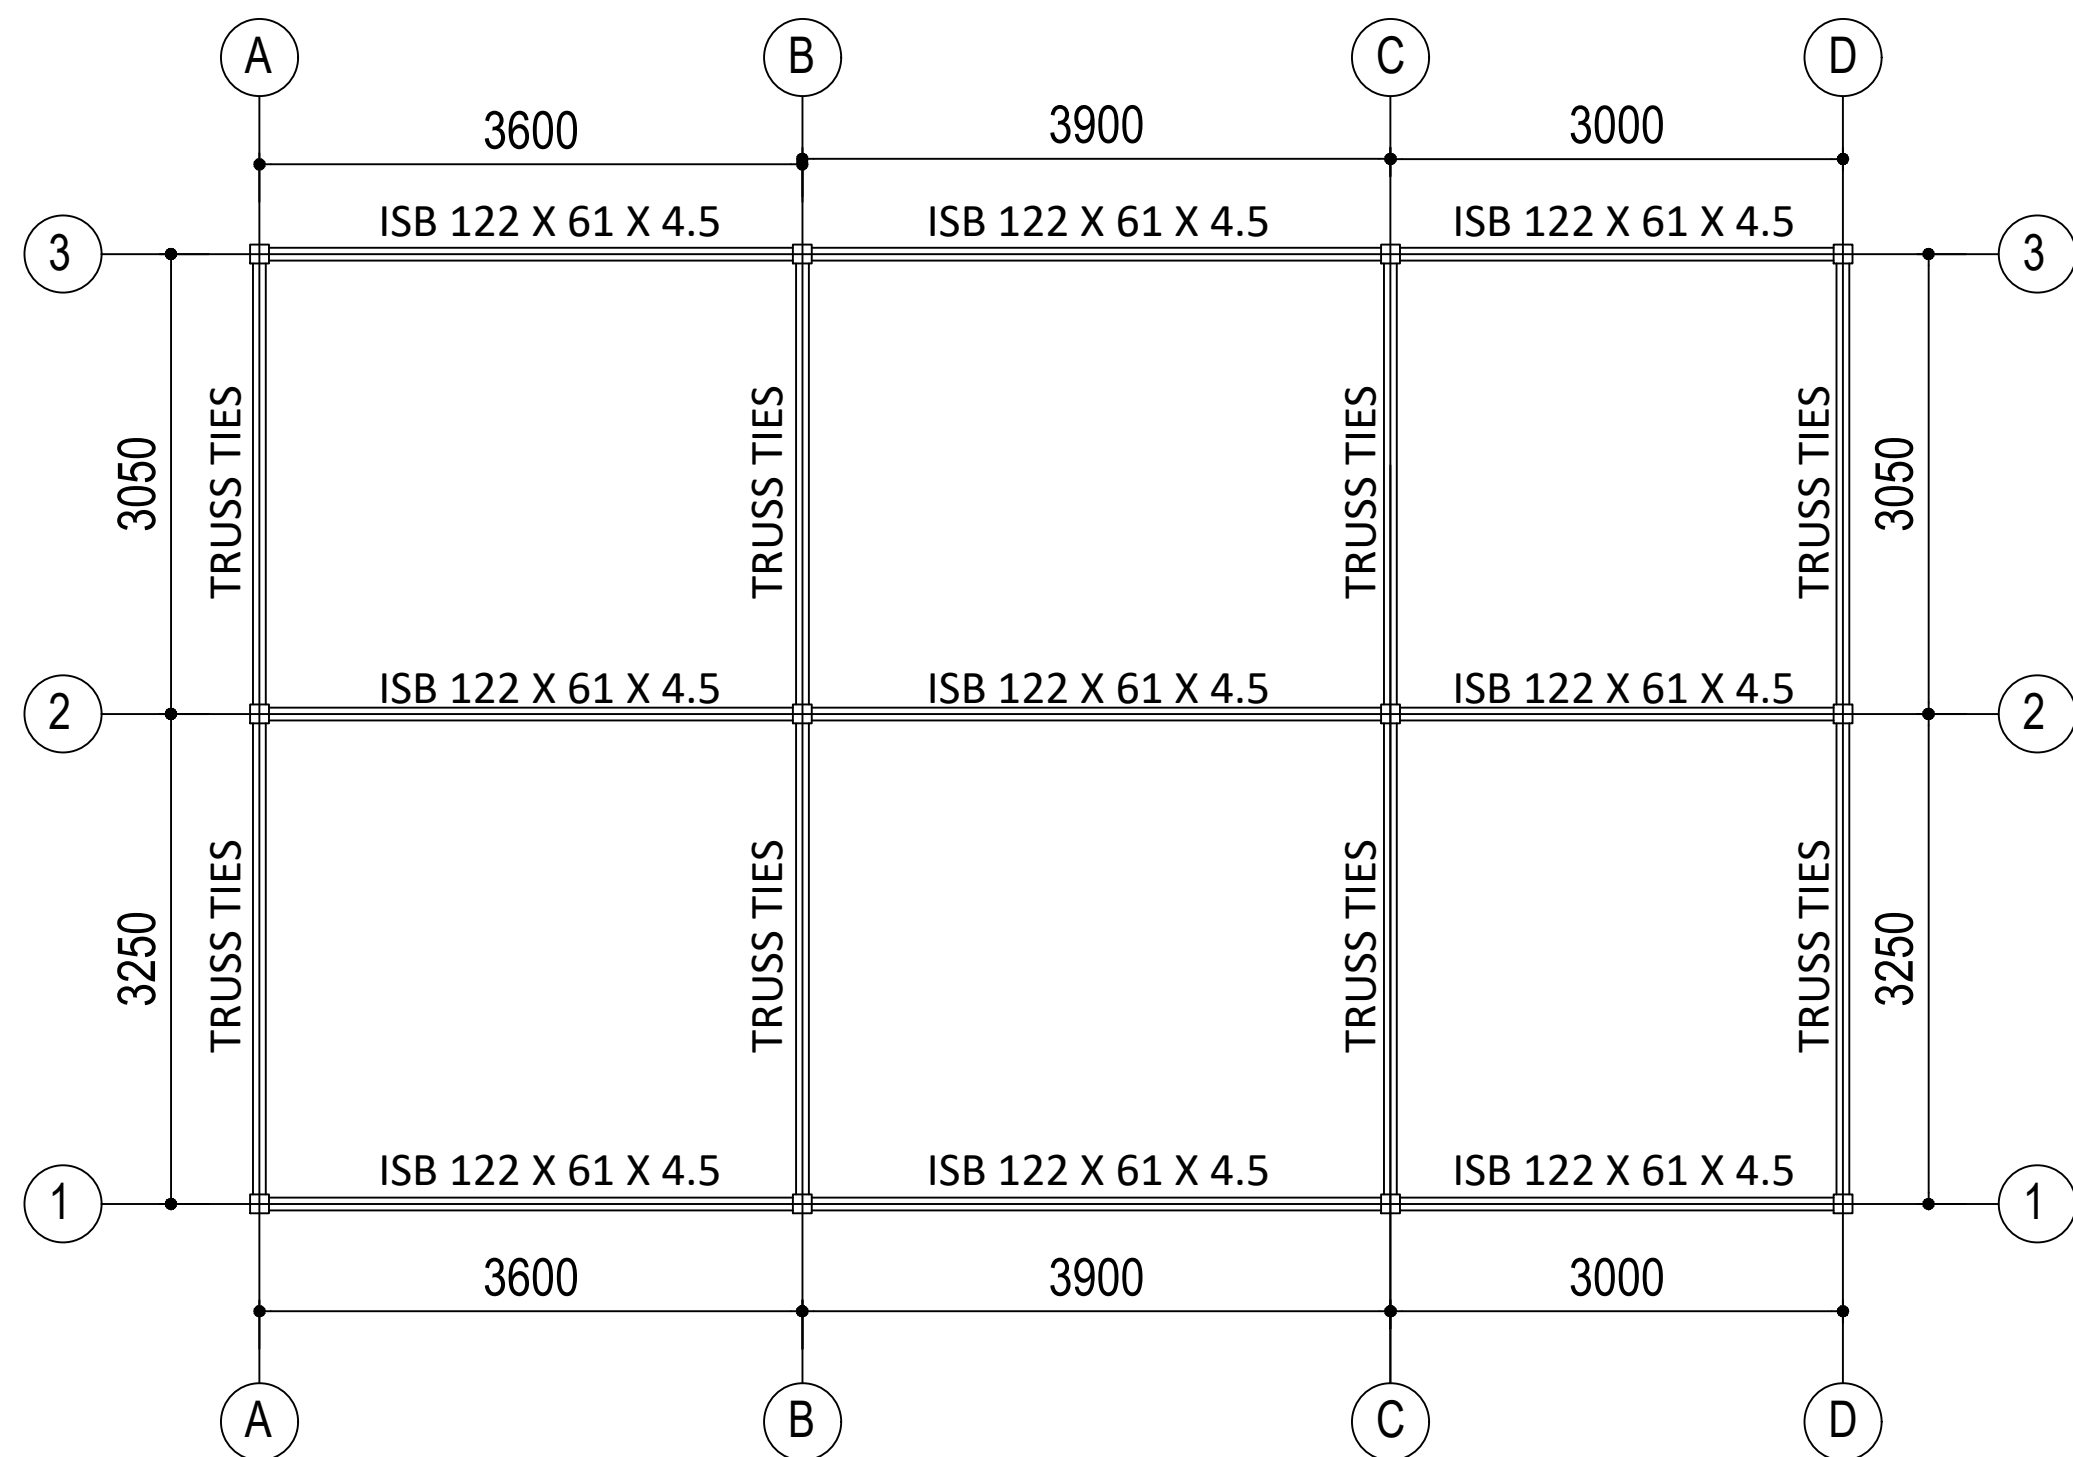

SECOND FLOOR BEAM LAYOUT PLAN

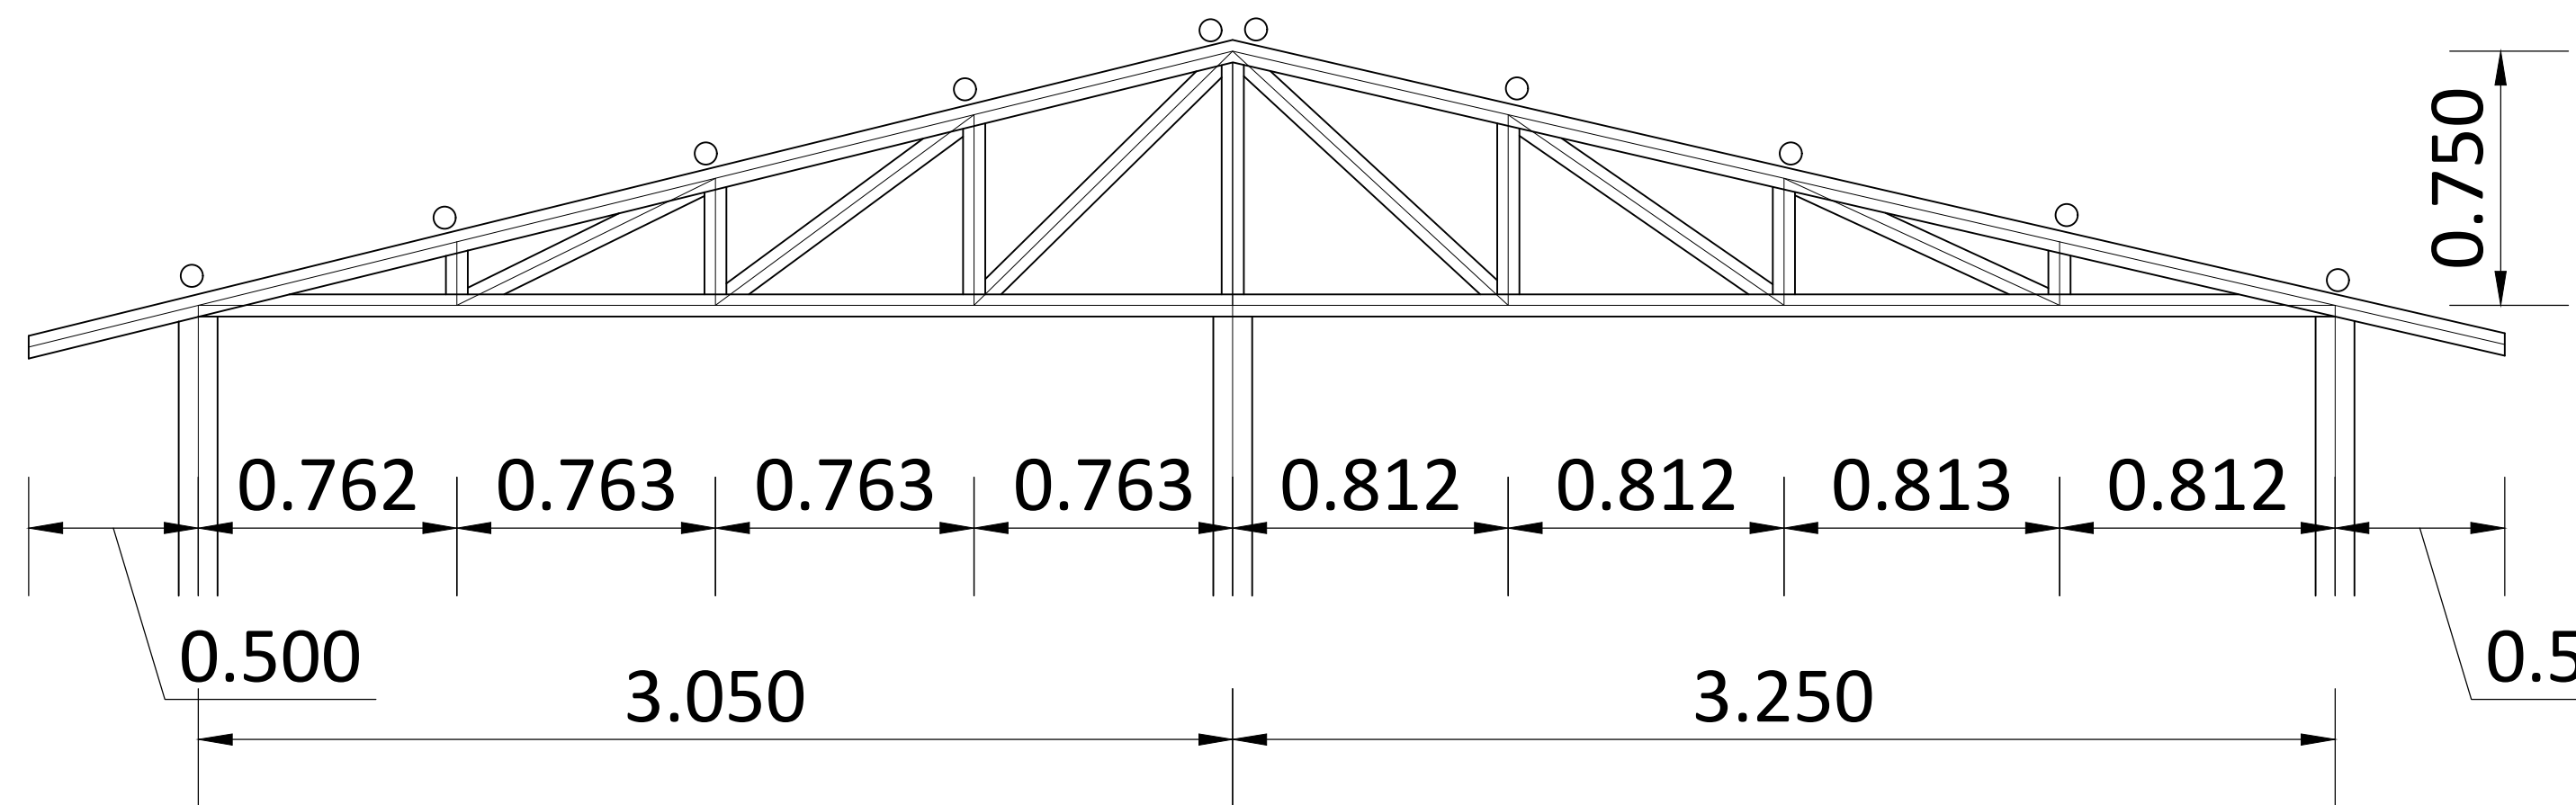

TRUSS MEMBER SIZES

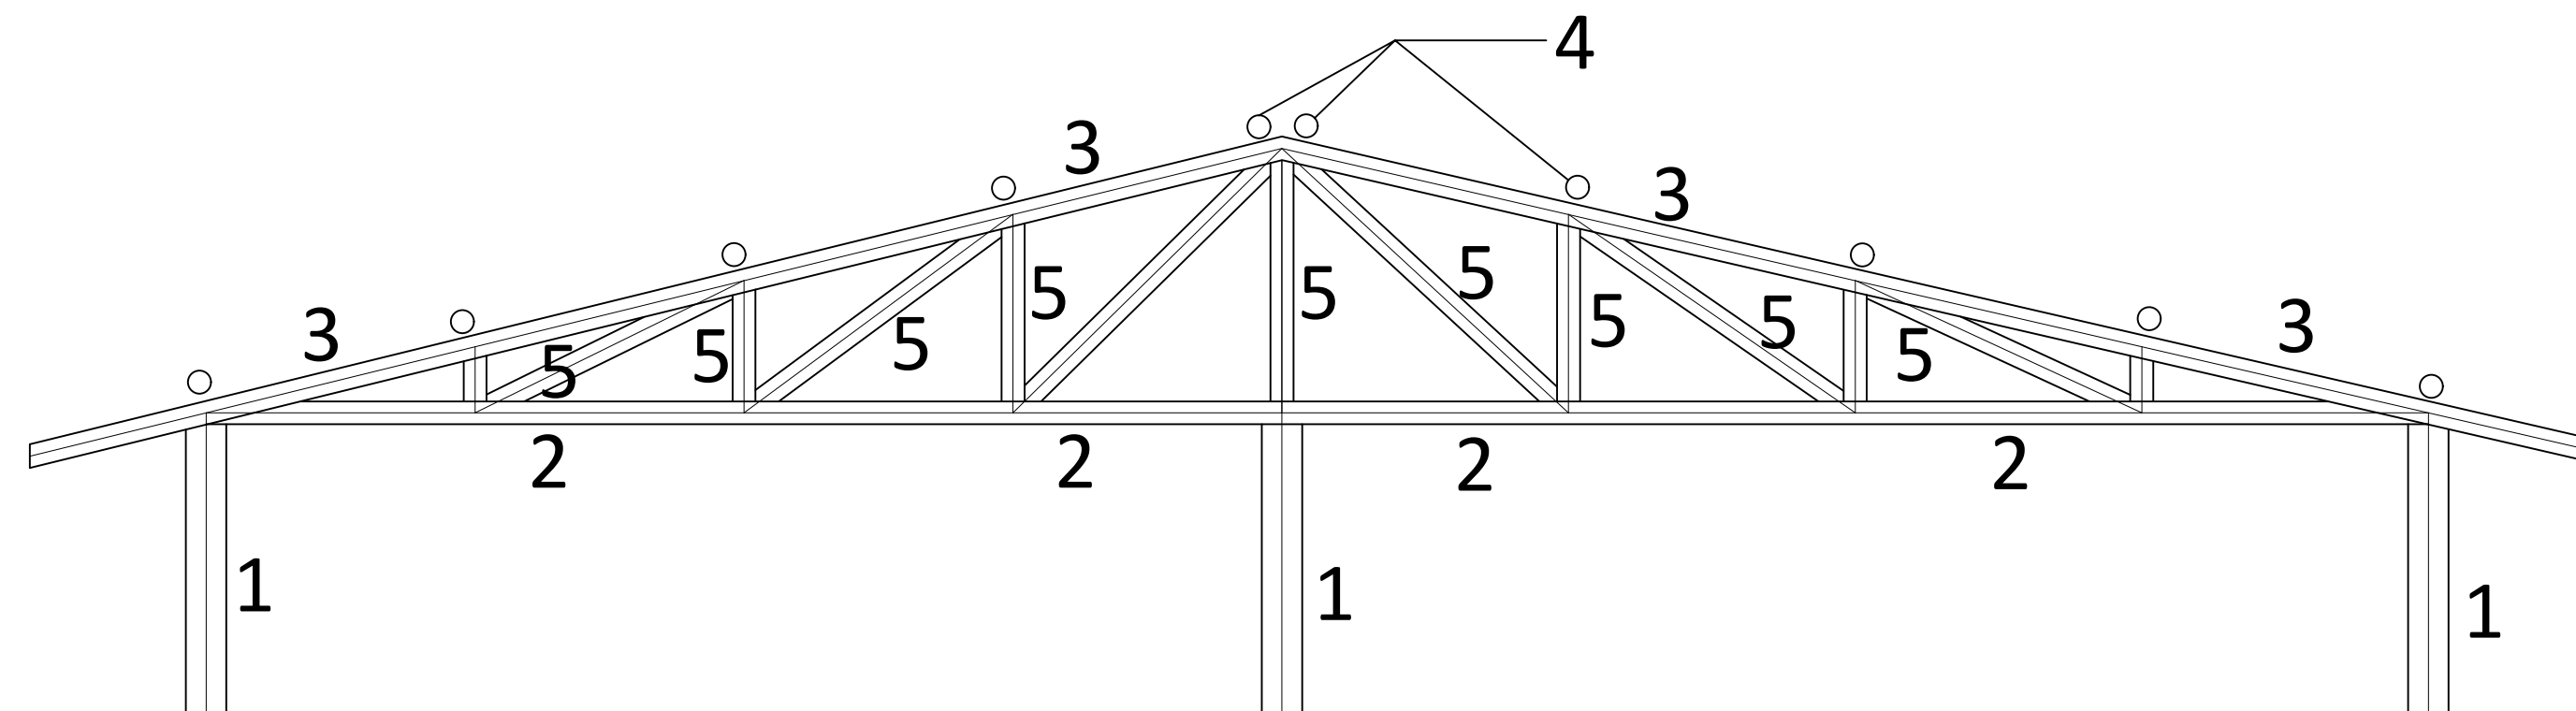



TRUSS MEMBER IDENTIFICATION

FOR DOUBLE SLOPE ROOF		
Member No.	Member Identification	Member Specifiaction
1	Post	ISB 113.5 X 113.5 X 4.8
2	Horizontal ties of truss	ISNB 65M
3	Rafter	ISNB 65M
4	Purlin	ISNB 65M
5	Struts	ISNB 65M

PROJECT: DPR OF 500MT COLD STORE AT JIRI, DOLAKHA	CONTENT: ADMIN BLOCK		CHECKED BY:		CONSULTANT: Sworaj Consultants Pvt. Ltd. Samakhushi, Kathmandu	Sheet No AD 03
			APPROVED BY :			
			SCALE :			
CLIENT: Government of Province Ministry of Land Management, Agriculture and Cooperative Province No. 3, Hetauda	FINAL DRAWING		DATE:	REVISION:		


ELECTRICAL & HVAC DRAWINGS

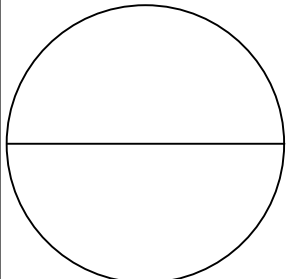PROJECT: DPR OF 500MT COLD STORE AT JIRI, DOLAKHA	CONTENT: FLOOR PLAN		CHECKED BY: APPROVED BY :	CONSULTANT: Sworaj Consultants Pvt. Ltd. Samkhushi, Kathmandu	Sheet No 
CLIENT: Government of Province Ministry of Land Management, Agriculture and Cooperative Province No. 3, Hetauda	FINAL DRAWING		SCALE : DATE: REVISION:		

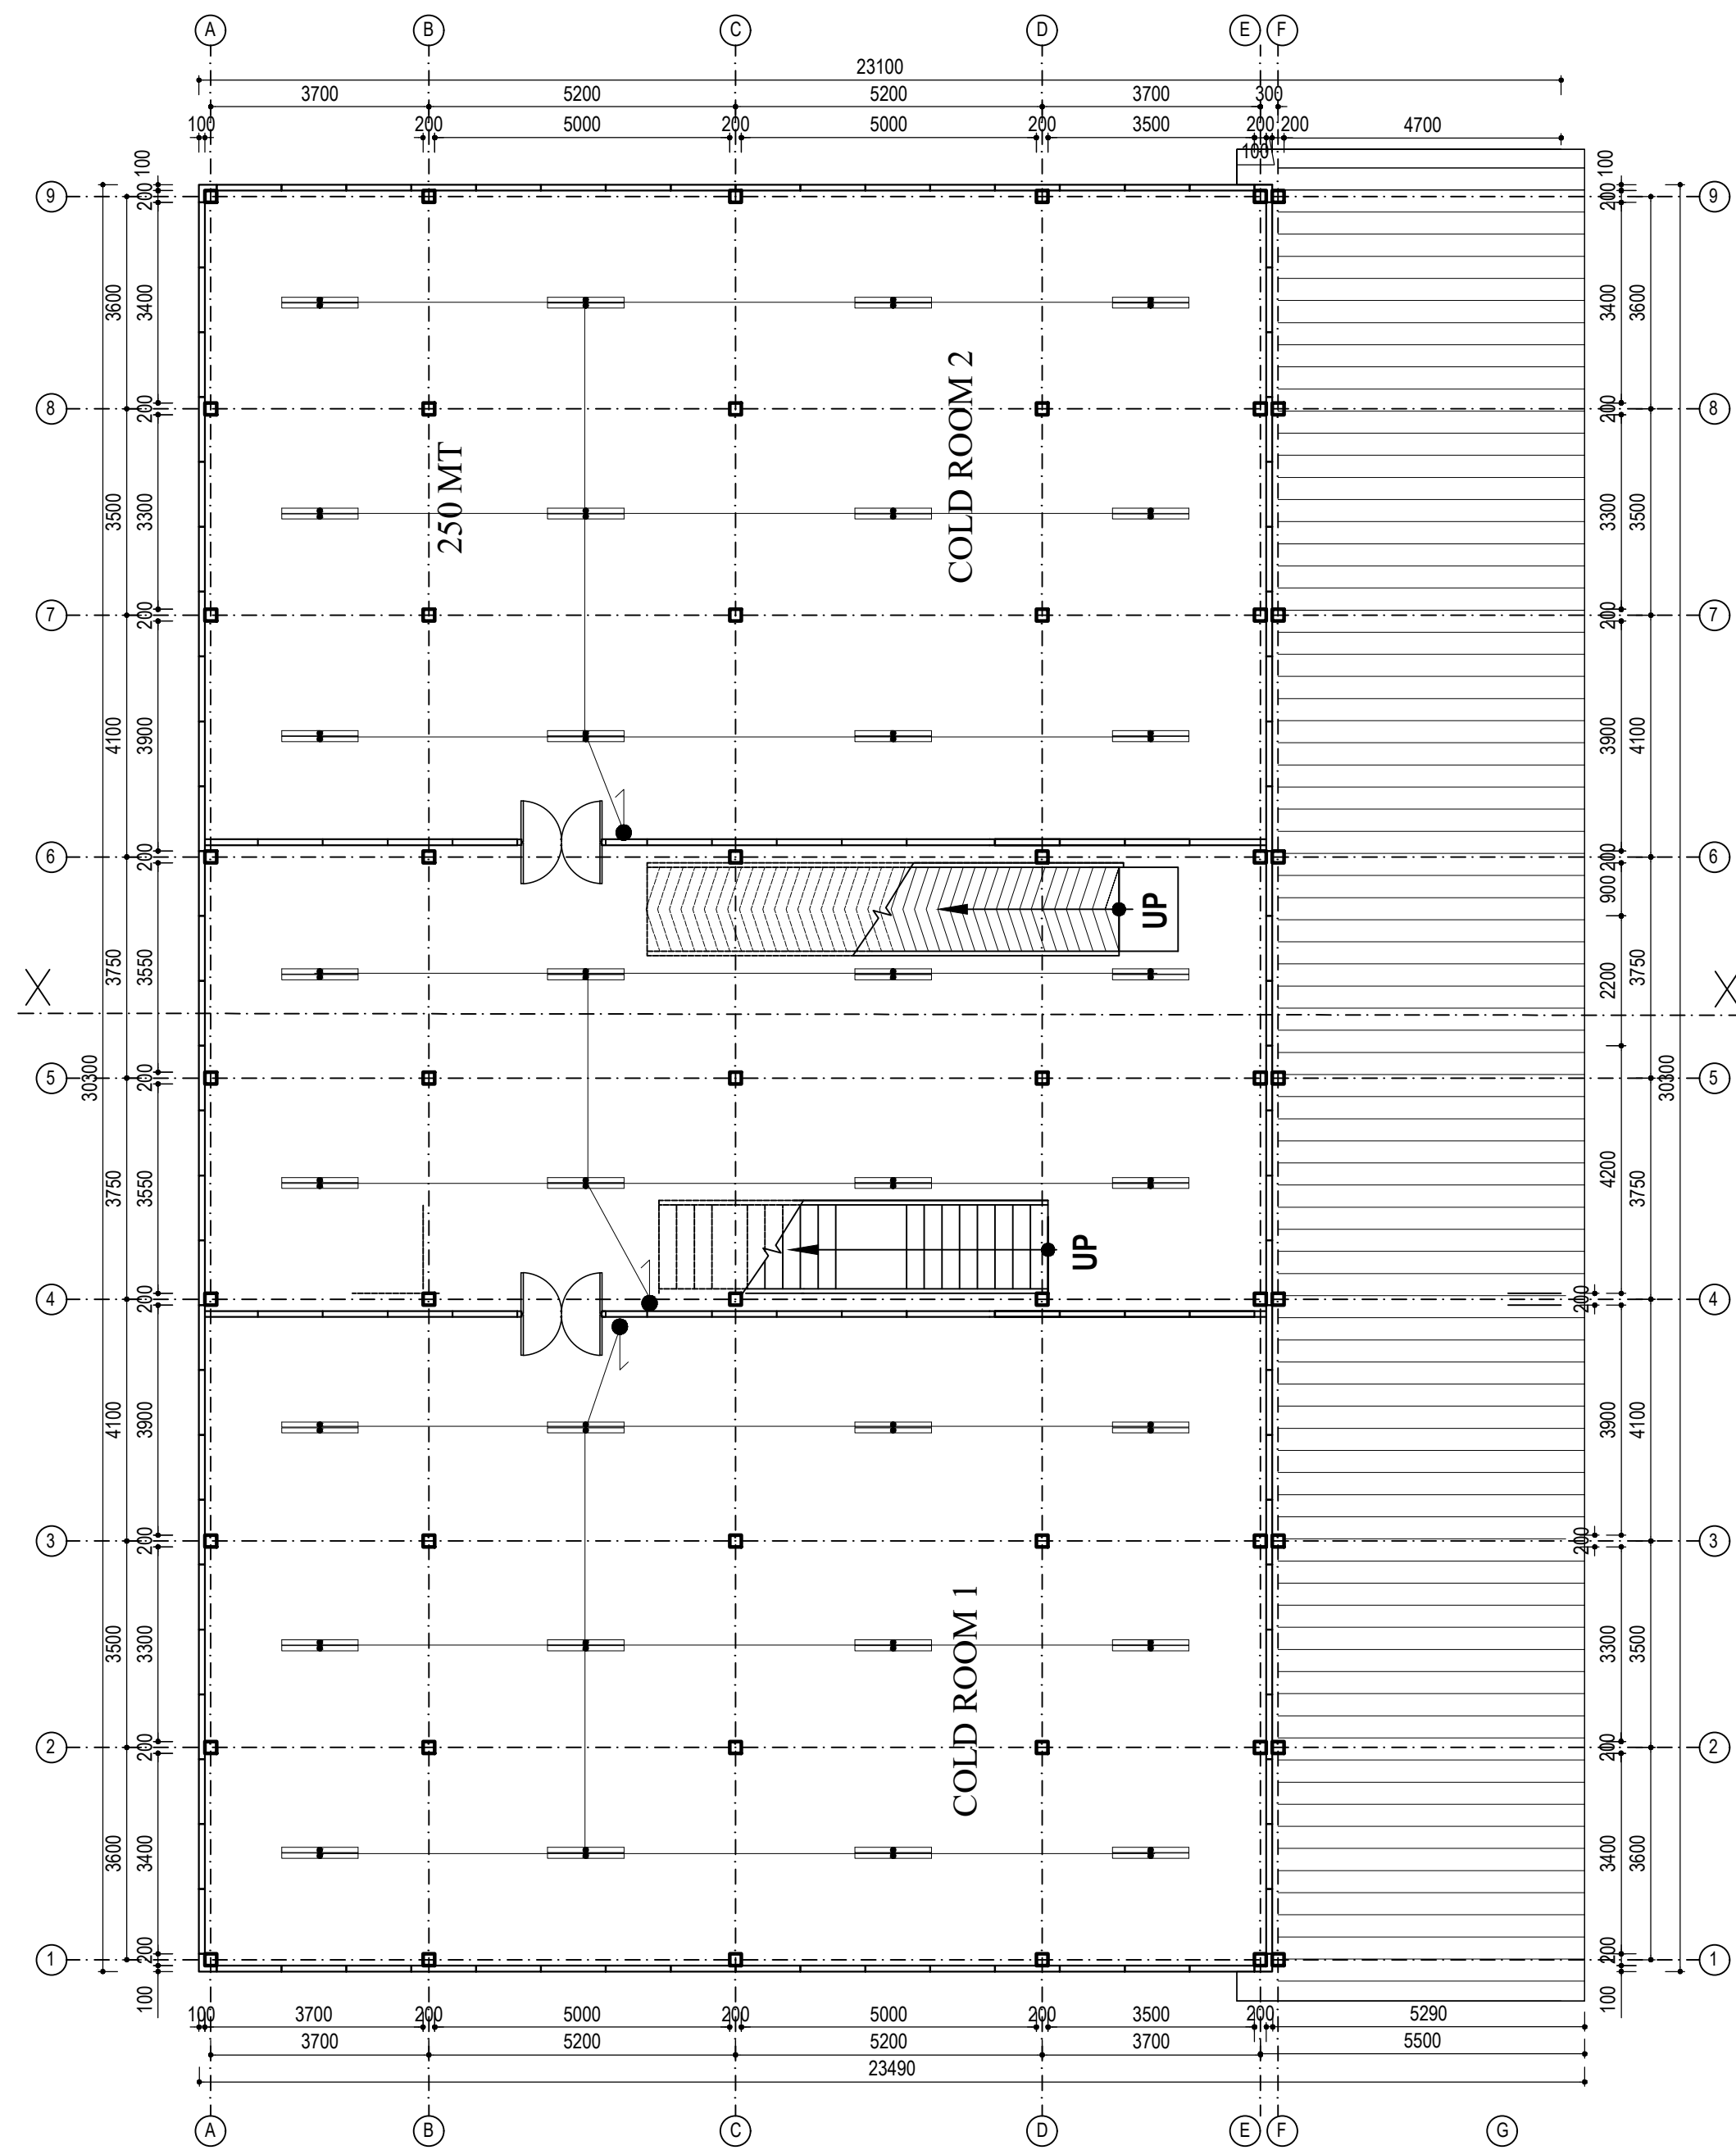

FIRST Floor Plan


Floor Area: 551.4576 sq.m

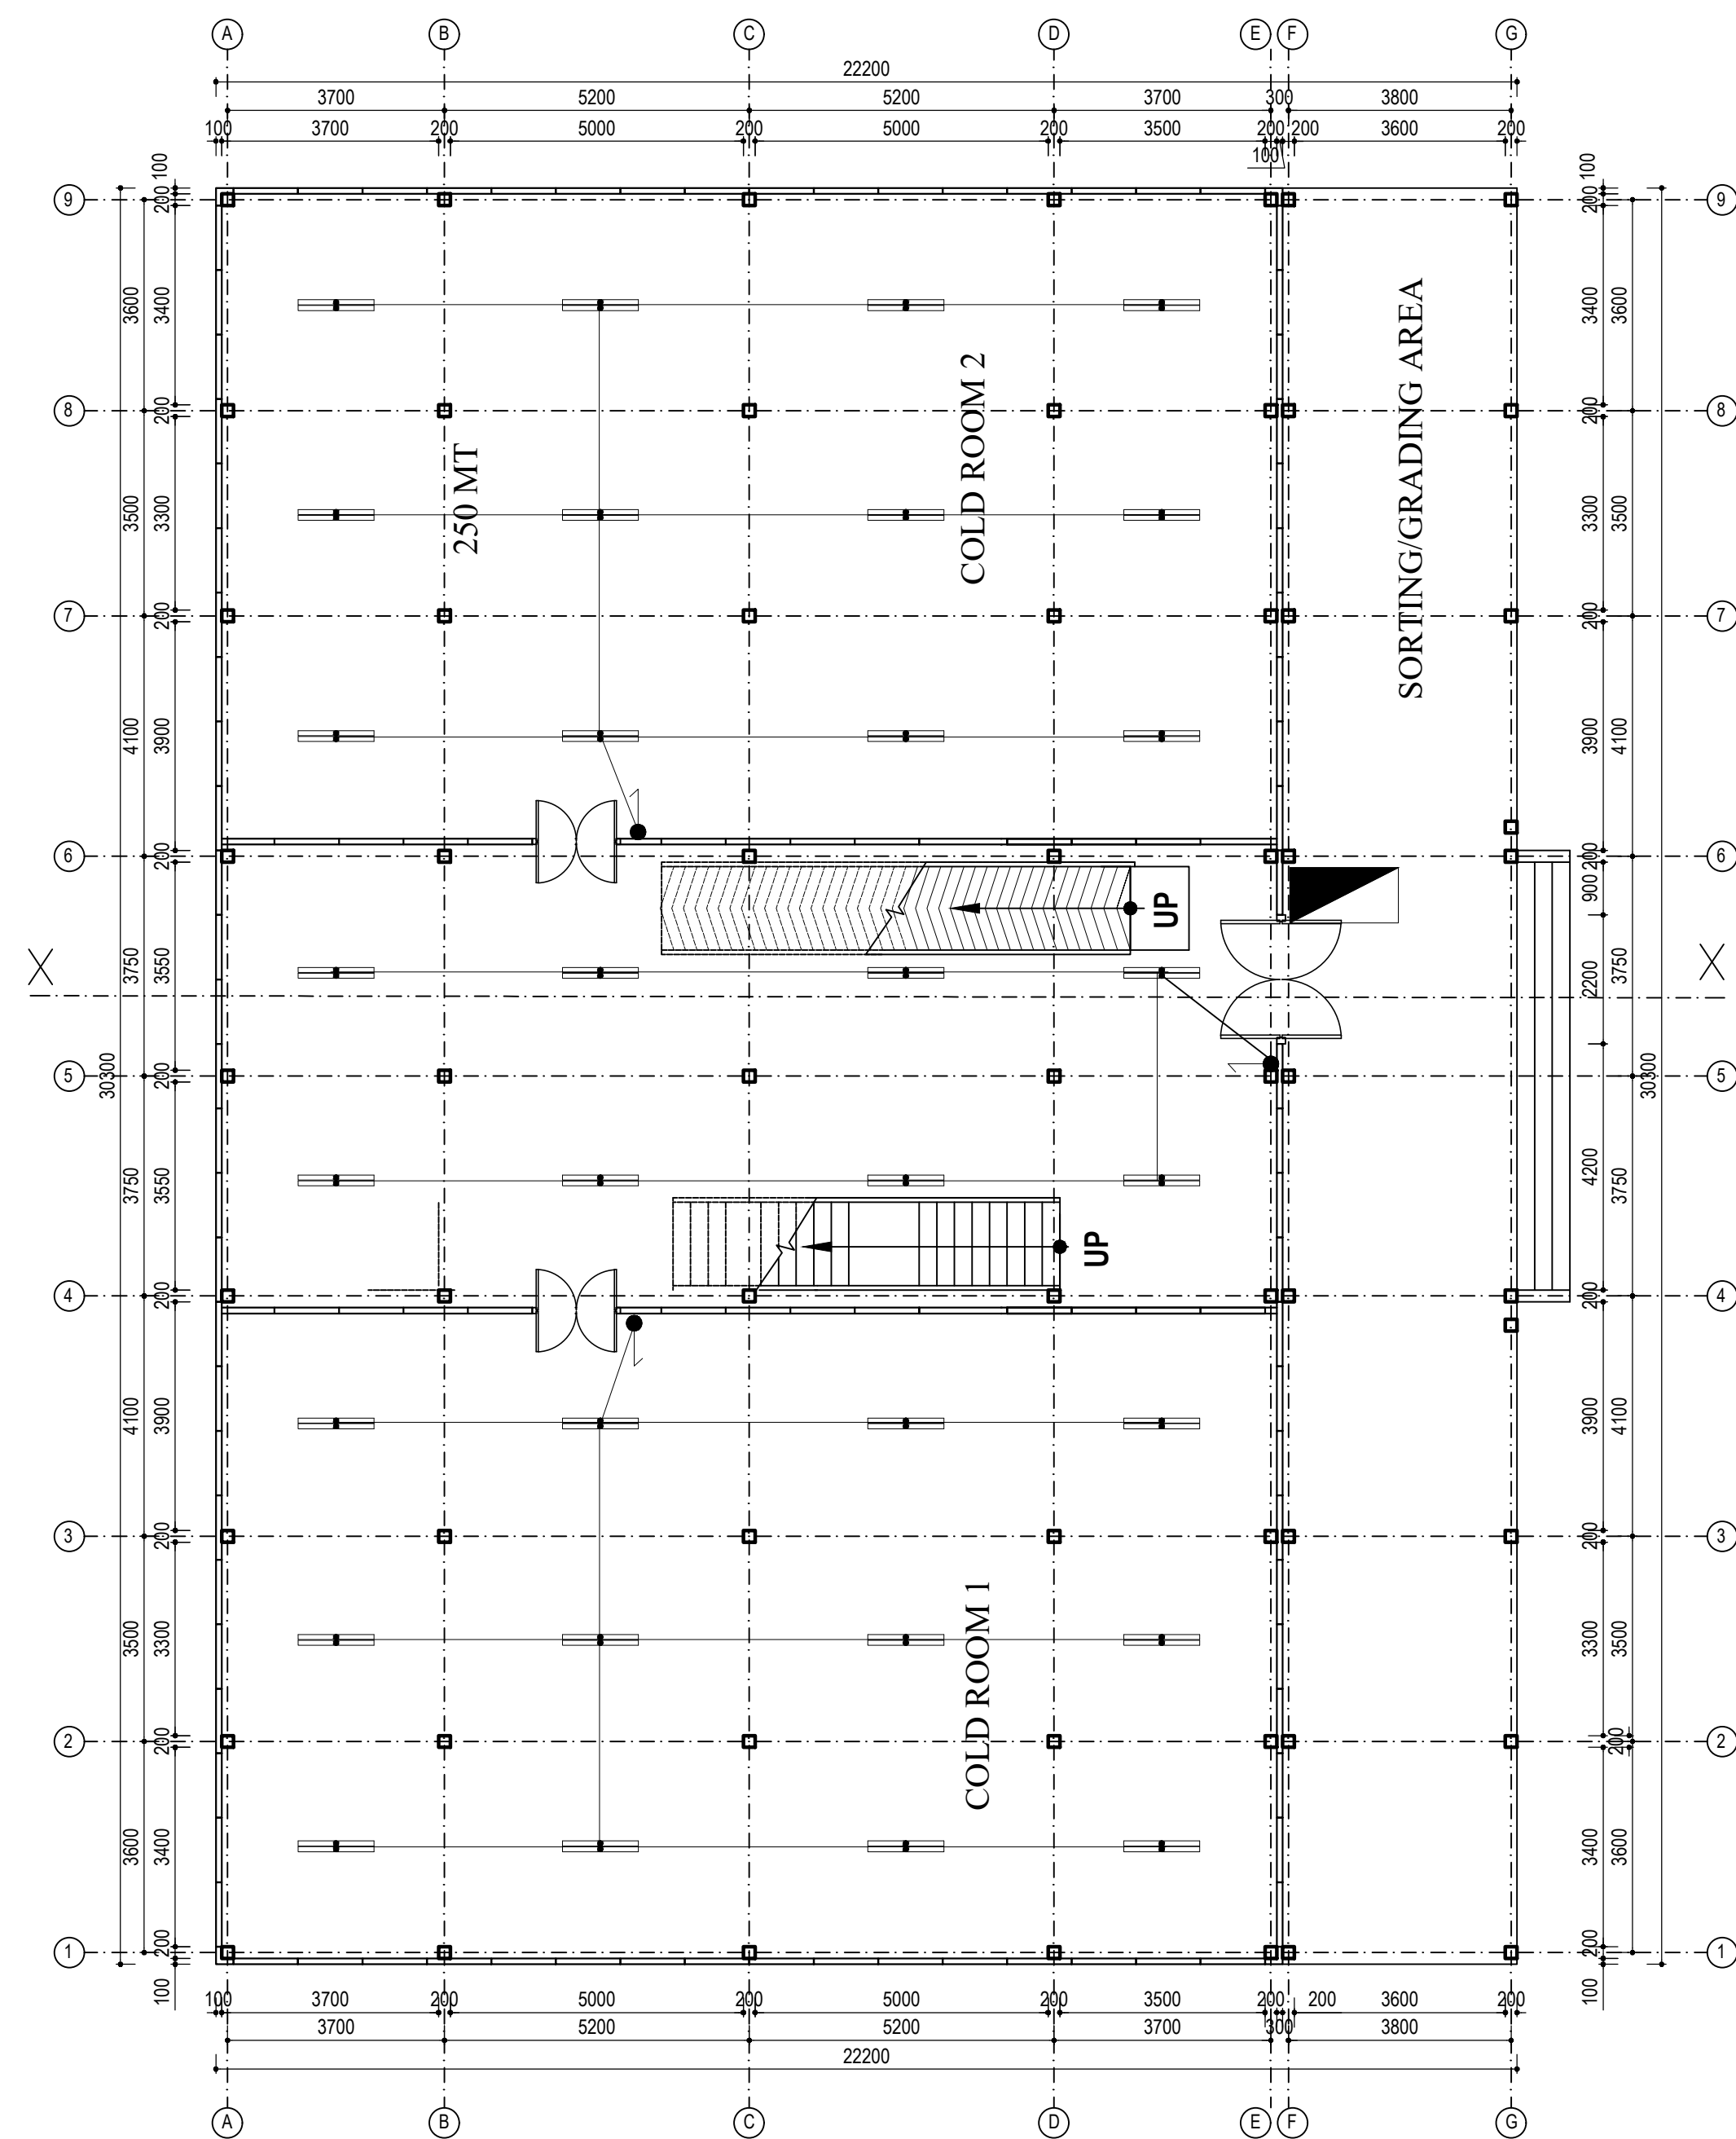


Ground Floor Plan

Floor Area: 672.660 sq.m

PROJECT: DPR OF 1500MT COLD STORE AT JIRI, DOLAKHA	CONTENT: FLOOR PLAN		CHECKED BY: APPROVED BY :	CONSULTANT: Sworaj Consultants Pvt. Ltd. Samkhushi, Kathmandu	Sheet No
CLIENT: Government of Province Ministry of Land Management, Agriculture and Cooperative Province No. 3, Hetauda	FINAL DRAWING		SCALE : DATE: REVISION:		EL 01

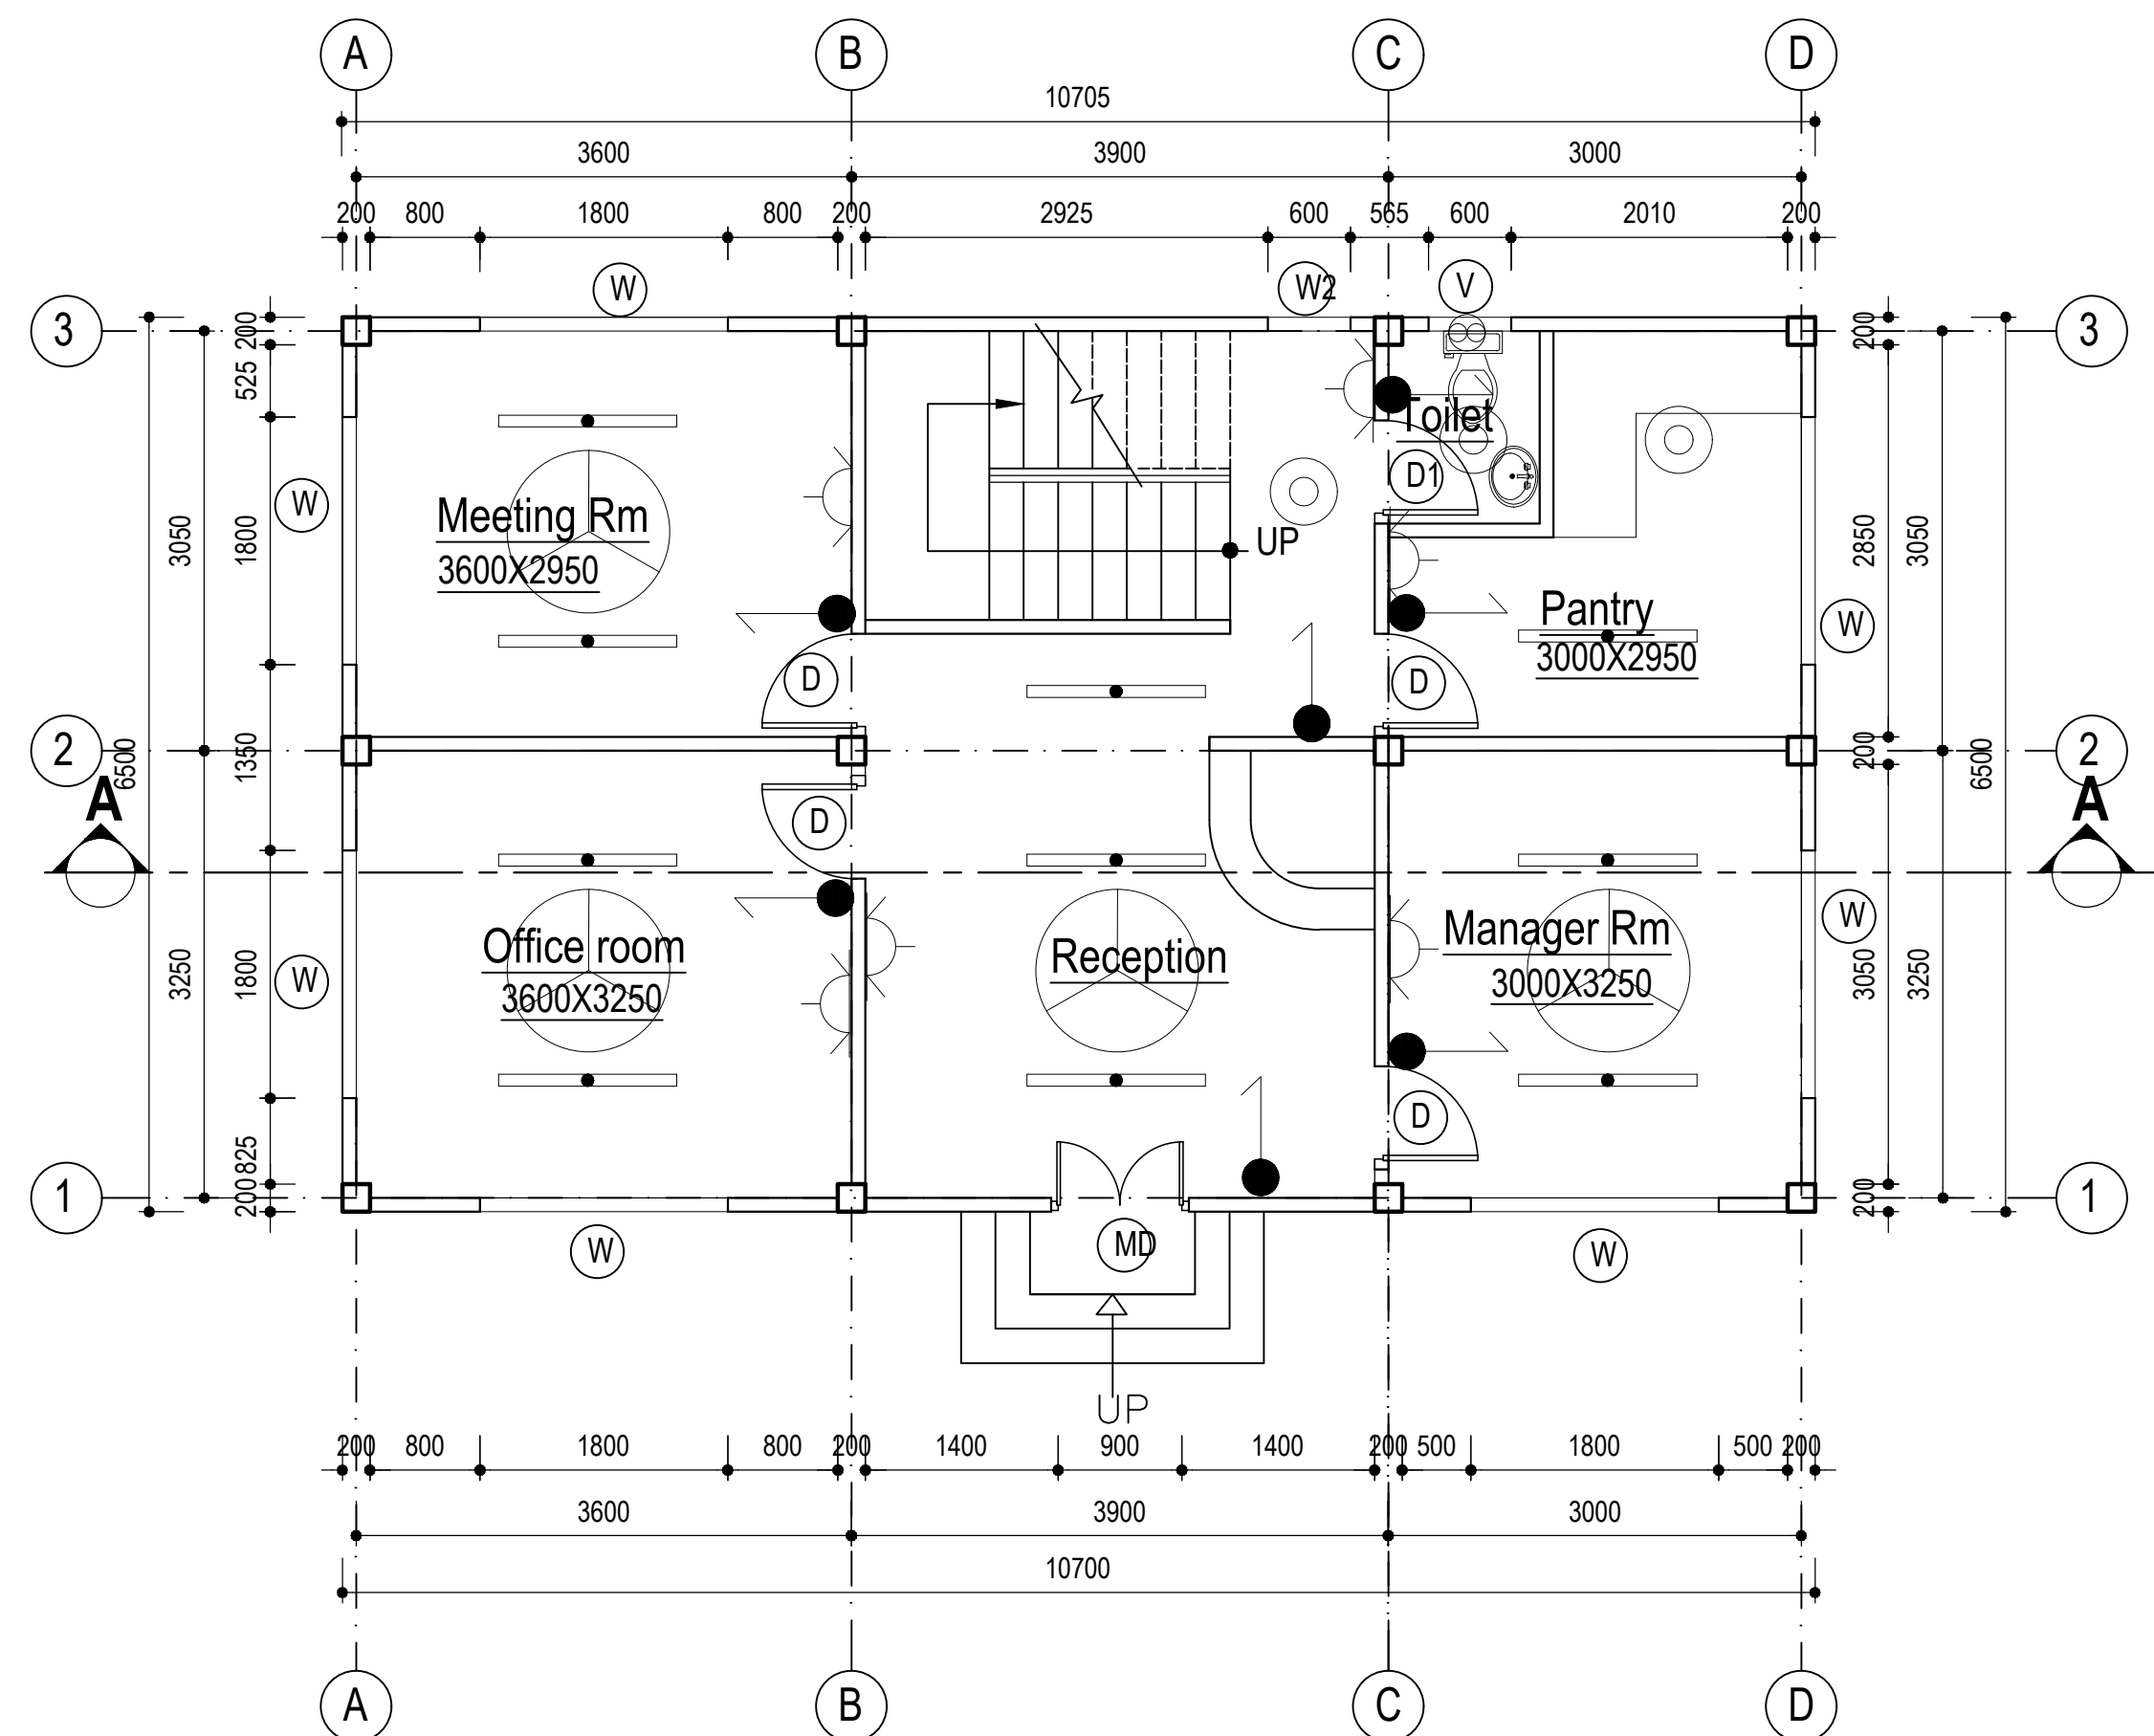

Ground Floor Plan
Floor Area:69.550 Sq.m

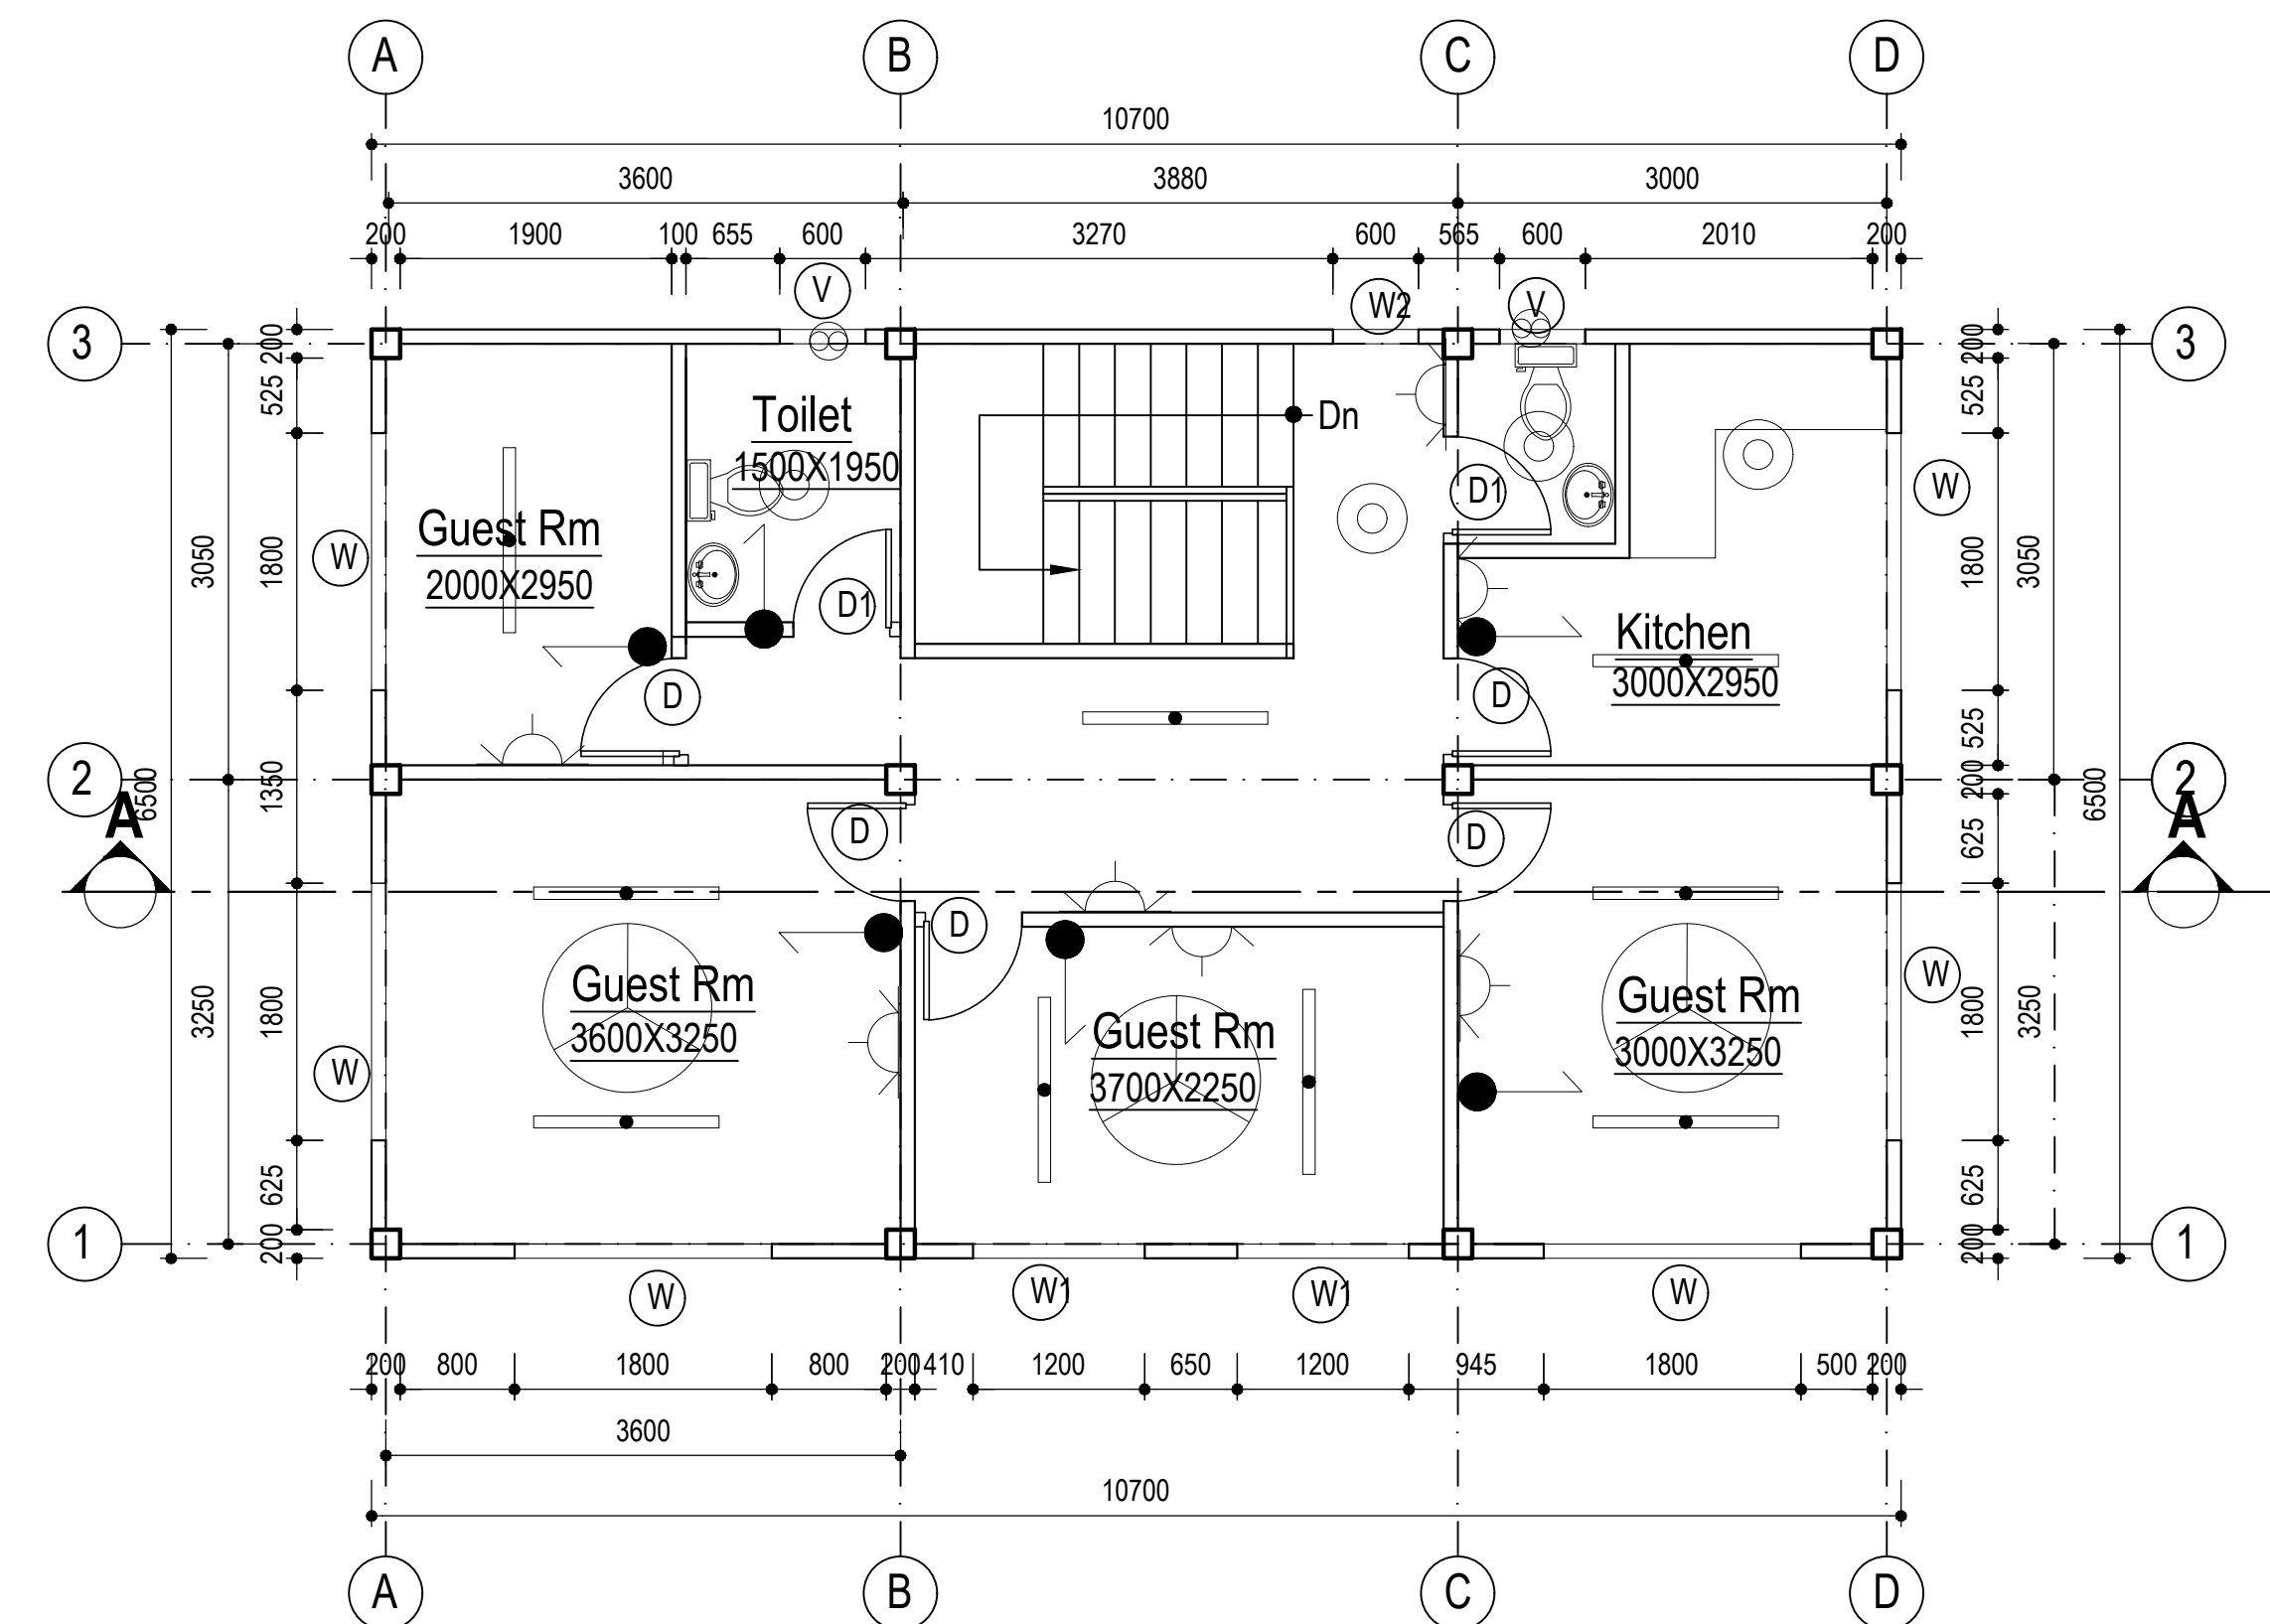

FIRST Floor Plan
Floor Area:69.550 Sq.m

PROJECT:
DPR OF 500MT COLD STORE AT JIRI, DOLAKHA

CLIENT:
Government of Province
Ministry of Land Management, Agriculture and Cooperative
Province No. 3, Hetauda

CONTENT:
FLOOR PLAN

FINAL DRAWING

CHECKED BY:

APPROVED BY :

SCALE :

DATE:

REVISION:



CONSULTANT:

Sworaj Consultants Pvt. Ltd.
Samkhushi, Kathmandu

Sheet No

EL
02


	LEGEND: -
	VACUUM CIRCUIT BREAKER
	AIR CIRCUIT BREAKER
	CONTACTOR
	CURRENT TRANSFORMER
	TRANSFORMER
	DIESEL GENERATING SET
	PROTECTION FUSE
	VOLTMETER
	VOLTMETER SELECTOR SWITCH
	AMMETER
	AMMETER SELECTOR SWITCH
	UNDER VOLTAGE RELAY
	OVER VOLTAGE RELAY
	TRIP CIRCUIT SUPERVISION RELAY
	OVER CURRENT RELAY (INSTANTANEOUS)
	OVER CURRENT RELAY
	AUXILLARY RELAY
	MASTER TRIP RELAY
	ANTI PUMPING RELAY
	EARTH FAULT RELAY (INSTANTANEOUS)
	EARTH FAULT RELAY
	FREQUENCY METER
	KILO WATT HOUR METER
	POWER FACTOR METER
	REVERSE POWER RELAY
	AUTOMATIC POWER FACTOR CORRECTION RELAY
	ENERGY ANALYSER
	CAPACITOR BANK
	SWITCH DISCONNECTER FUSE UNIT
	TRIP CIRCUIT HEALTHY
	BREAKER ON
	BREAKER OFF
	AUTO TRIP
	PHASE INDICATING LAMP
	HOOTER
	VOLTAGE NEGATIVE PHASE SEQUENCE RELAY (PHASE REVERSAL RELAY)

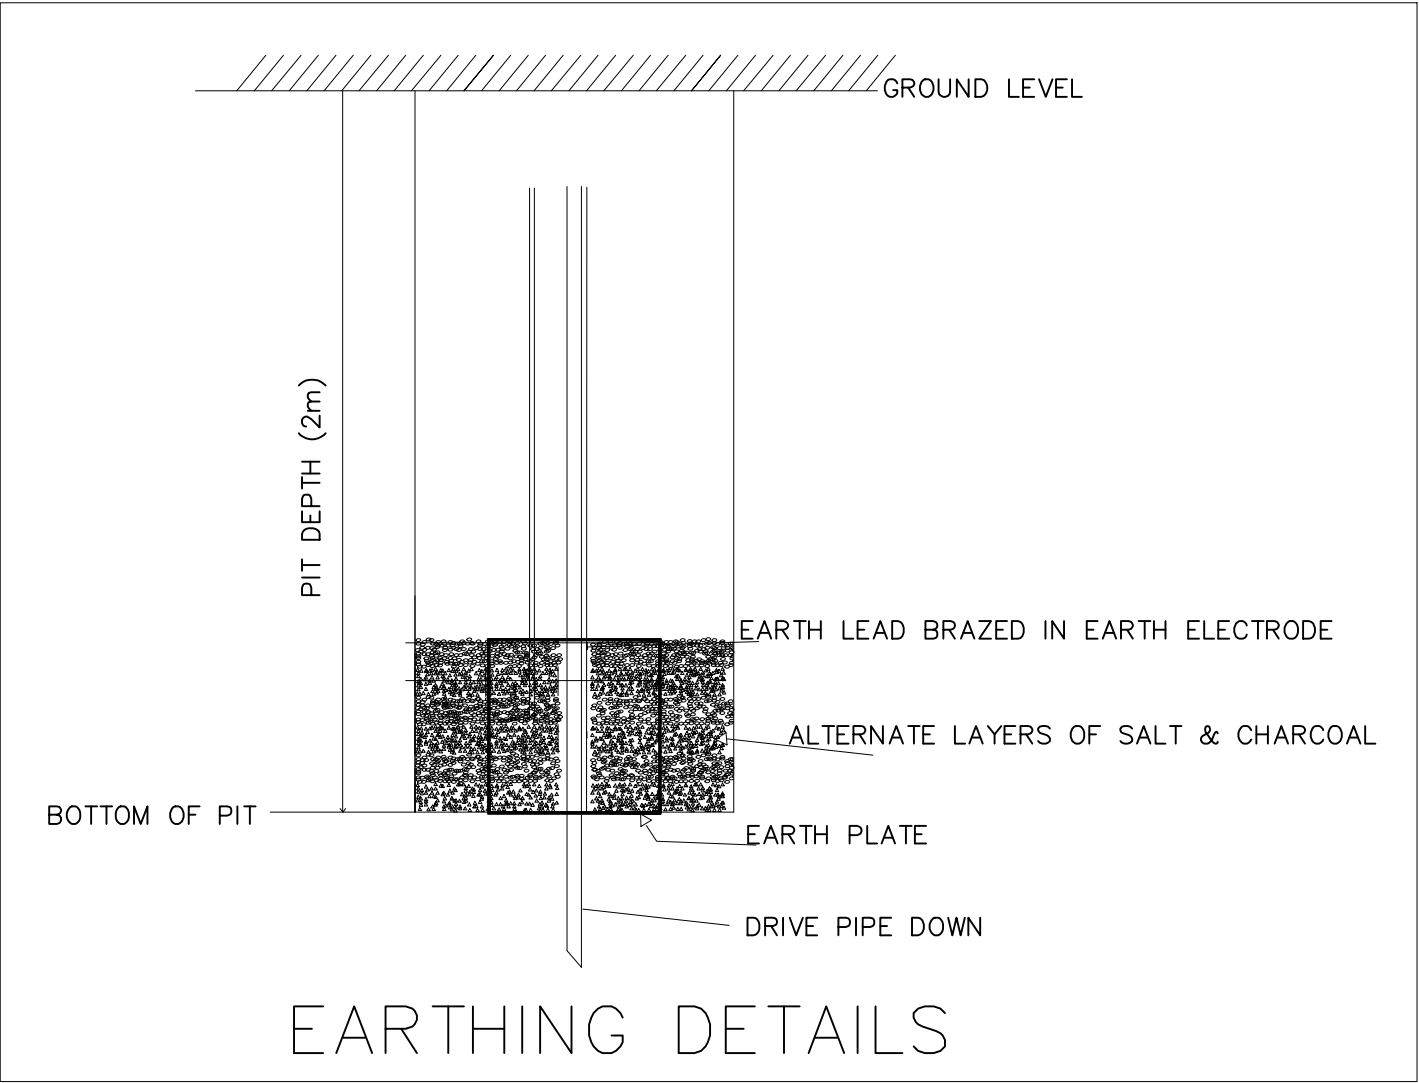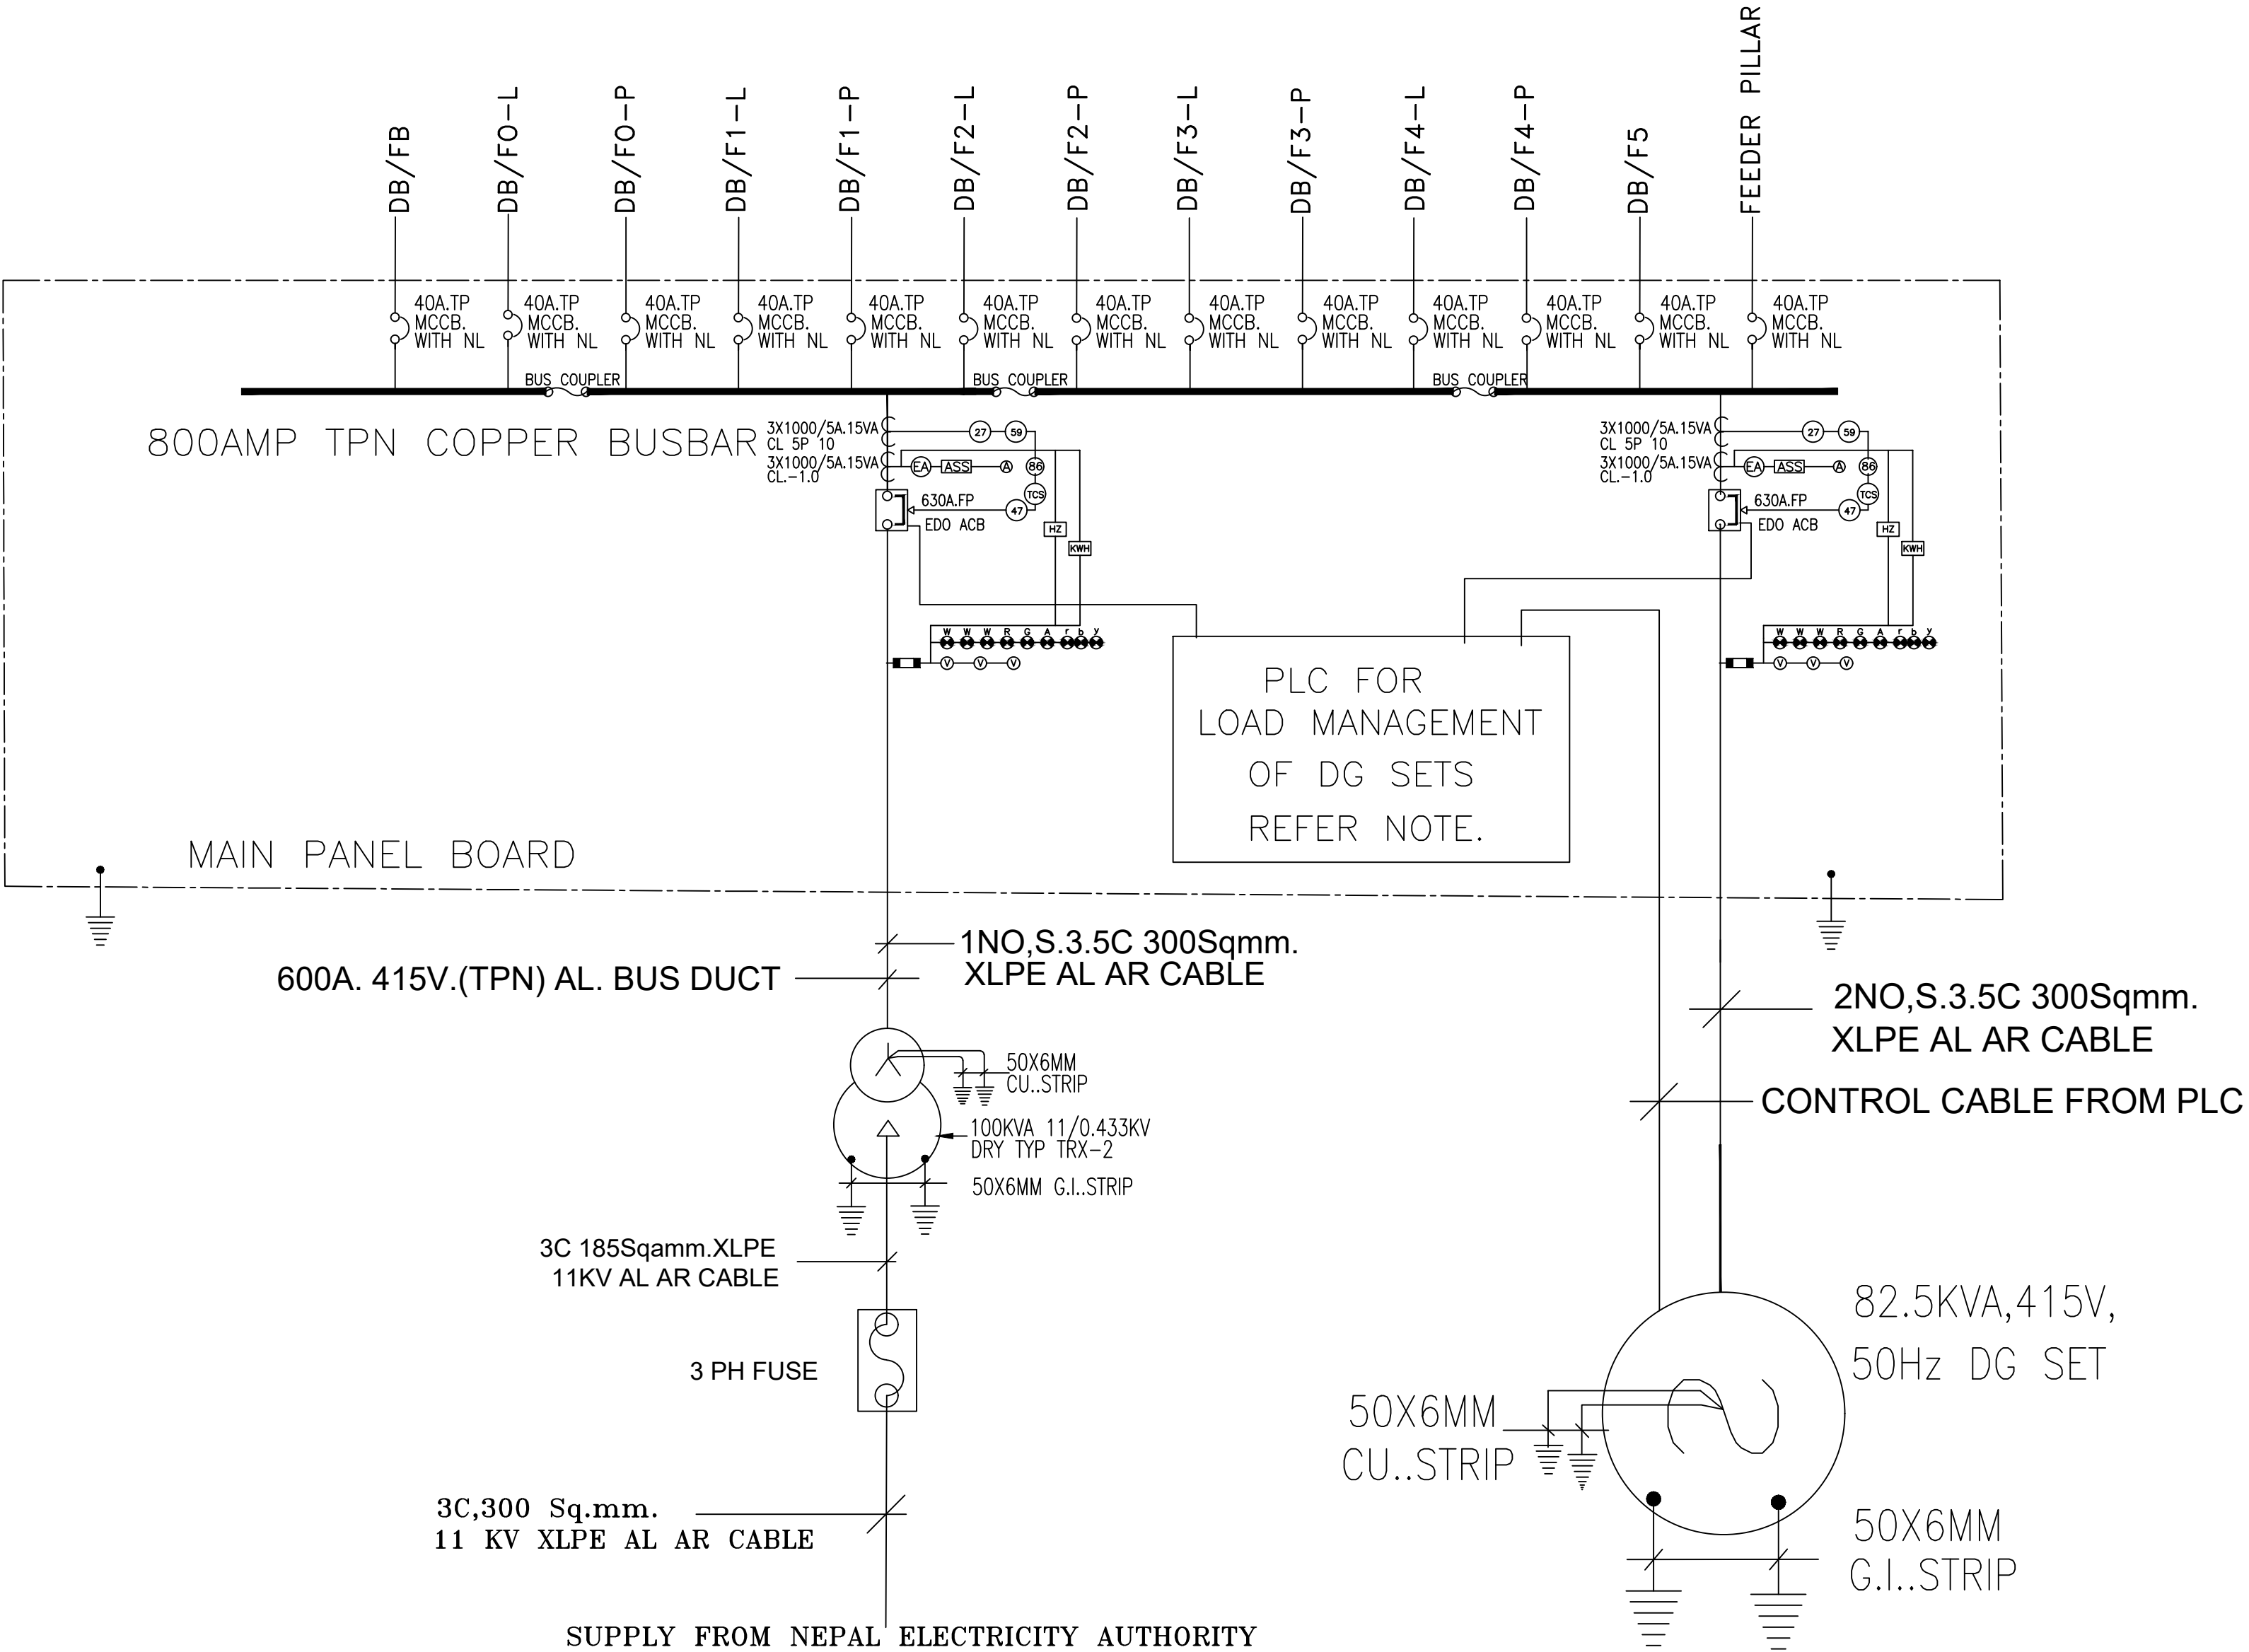


Substation


PROJECT: DPR OF 500MT COLD STORE AT JIRI, DOLAKHA	CONTENT: FLOOR PLAN		CHECKED BY:	CONSULTANT:	Sheet No
CLIENT: Government of Province Ministry of Land Management, Agriculture and Cooperative Province No. 3, Hetauda	FINAL DRAWING		APPROVED BY :	Sworaj Consultants Pvt. Ltd. Samkhushi, Kathmandu	EL
			SCALE :		03
			DATE:	REVISION:	

MECHANICAL BLOCK

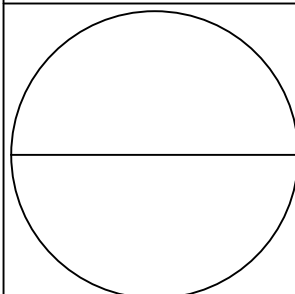
PROJECT: DPR OF 500MT COLD STORE AT JIRI, DOLAKHA	CONTENT: MECHANICAL BLOCK		CHECKED BY:	CONSULTANT: Sworaj Consultants Pvt. Ltd. Samkhushi, Kathmandu	Sheet No
CLIENT: Government of Province Ministry of Land Management, Agriculture and Cooperative Province No. 3, Hetauda	FINAL DRAWING		APPROVED BY :		
			SCALE :		
			DATE:		

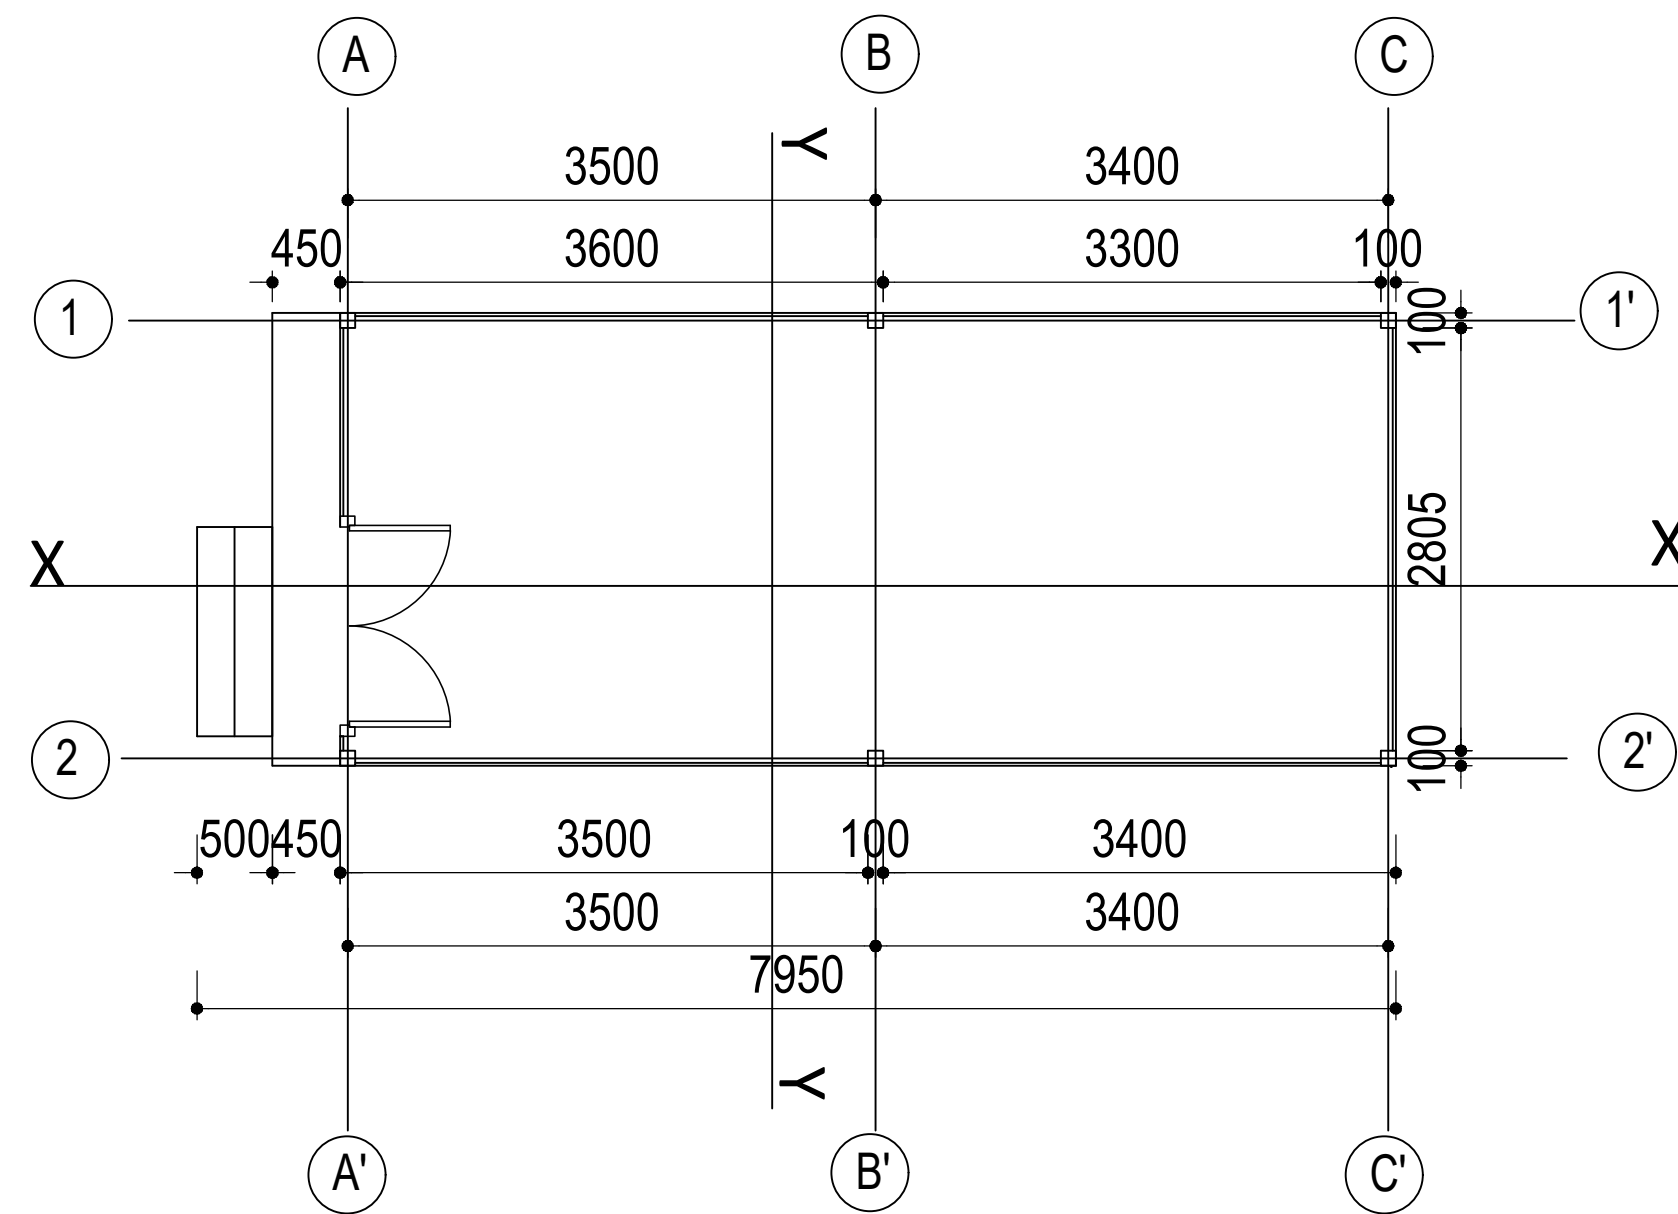


FLOOR PLAN

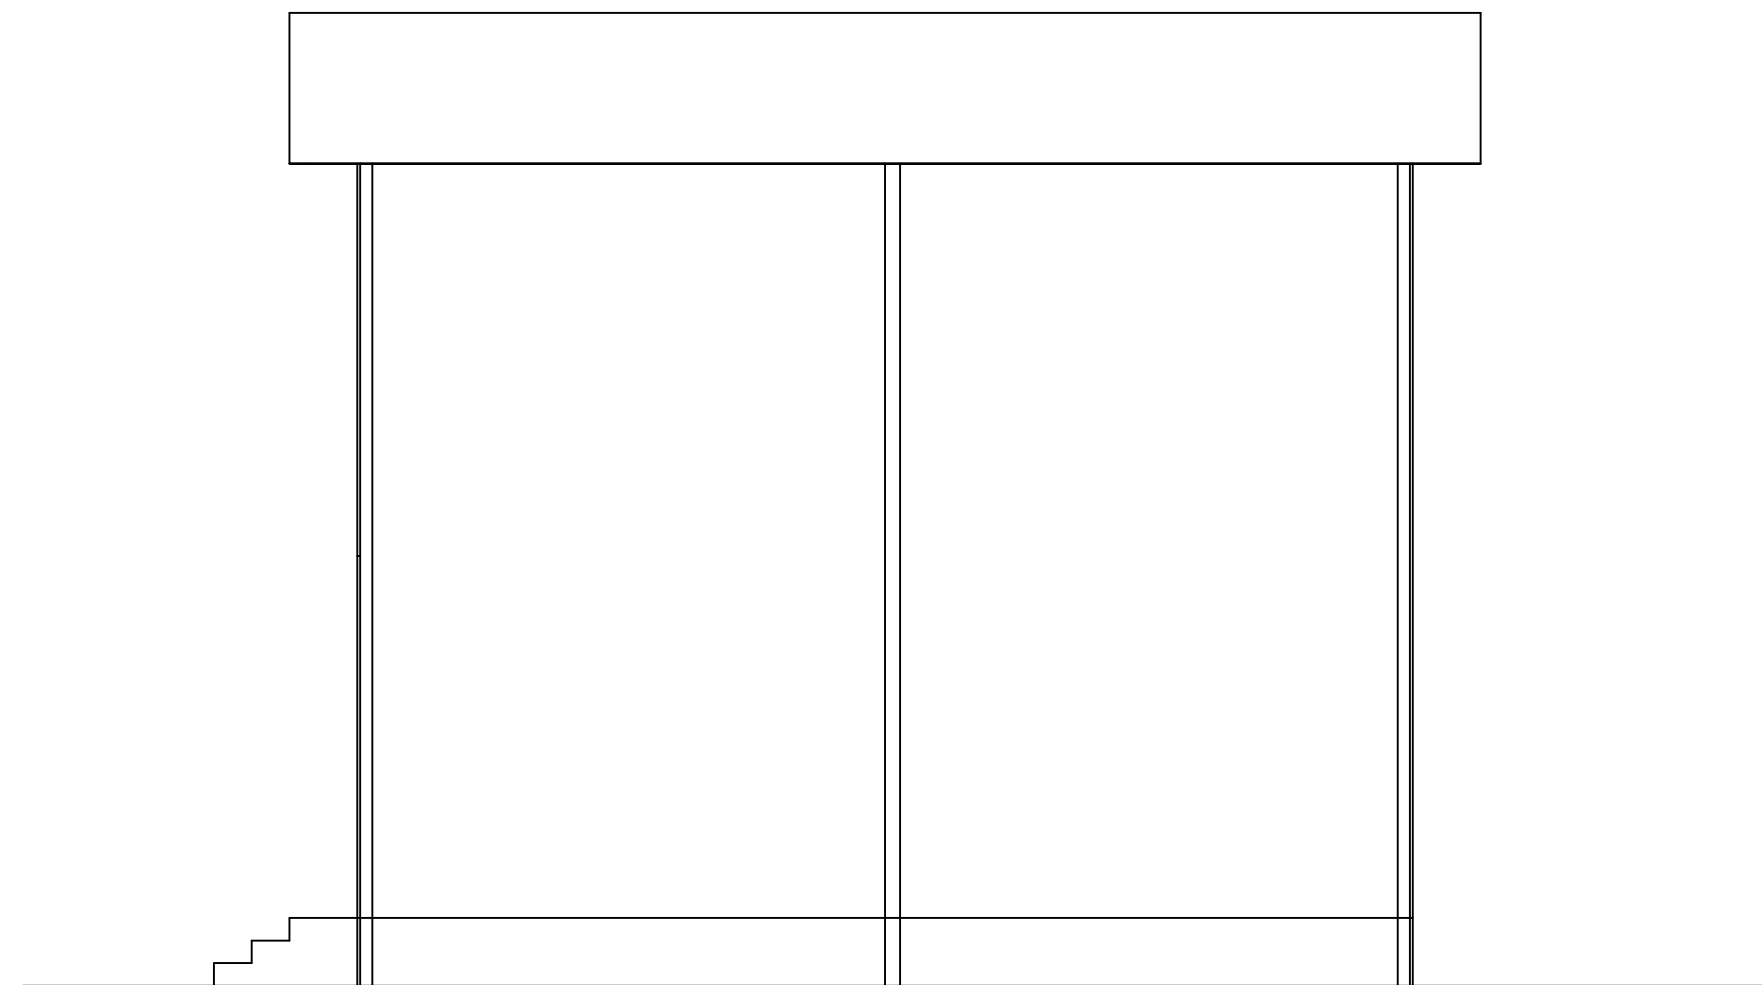


SECTION AT X-X

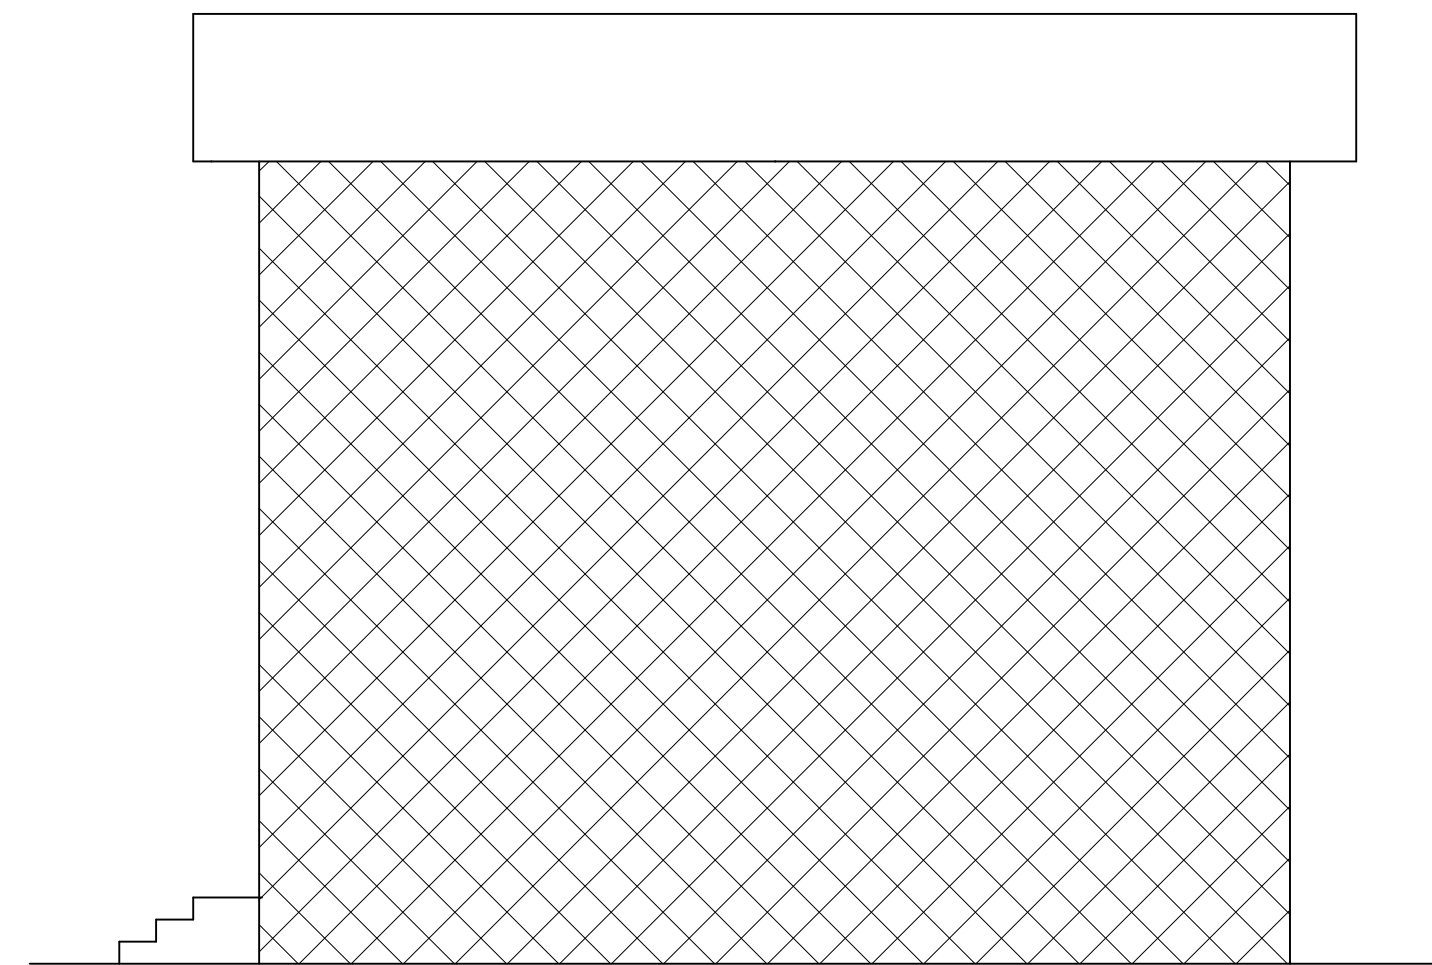


RIGHT ELEVATION

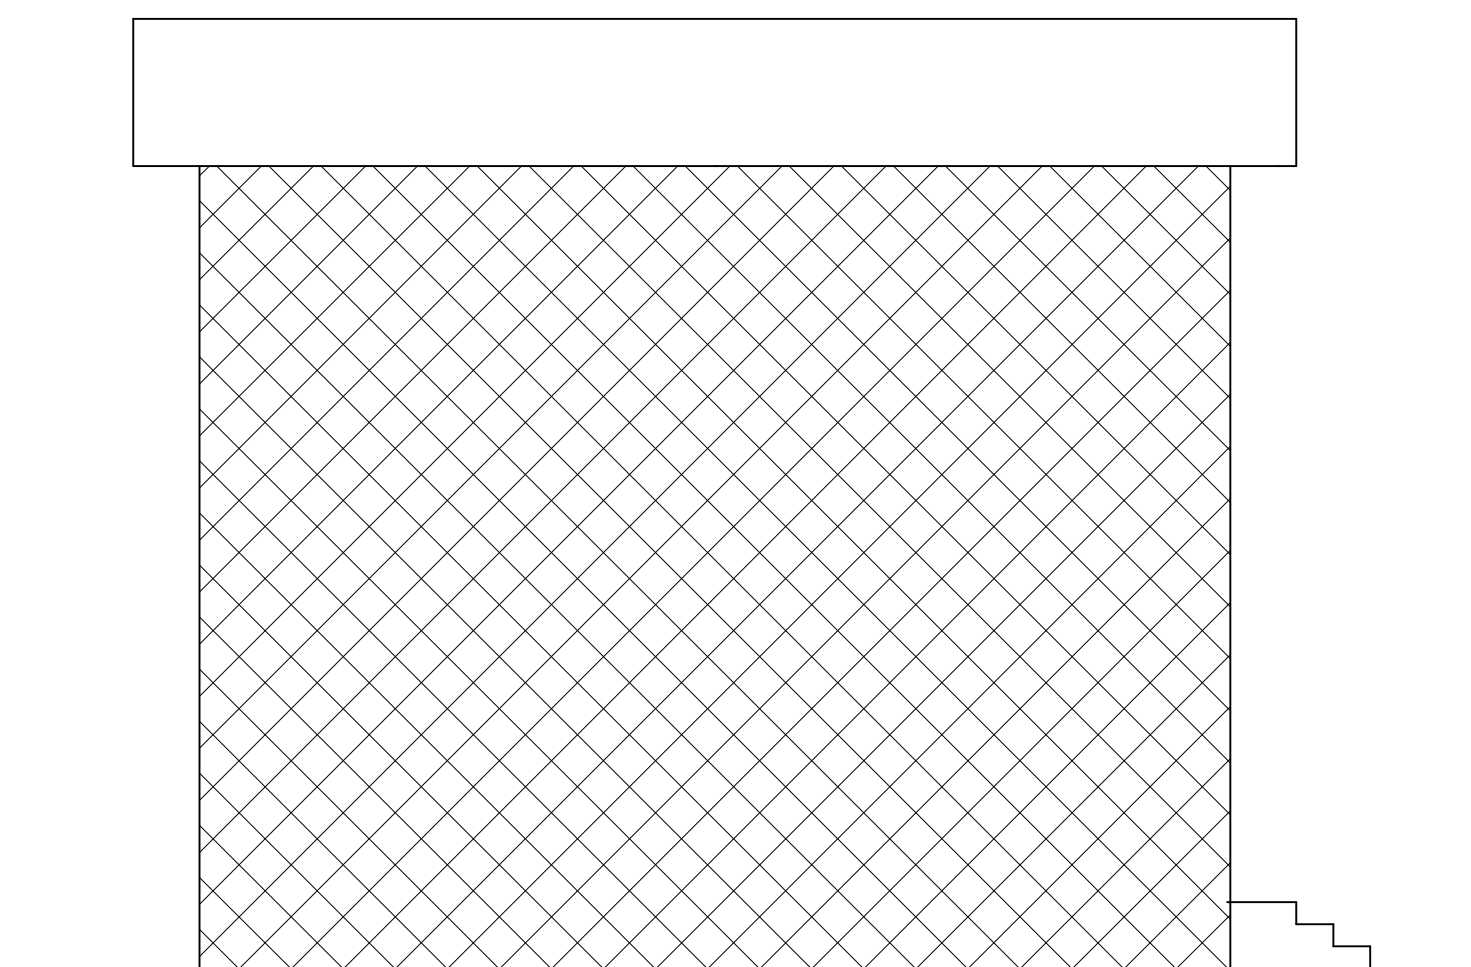


LEFT ELEVATION

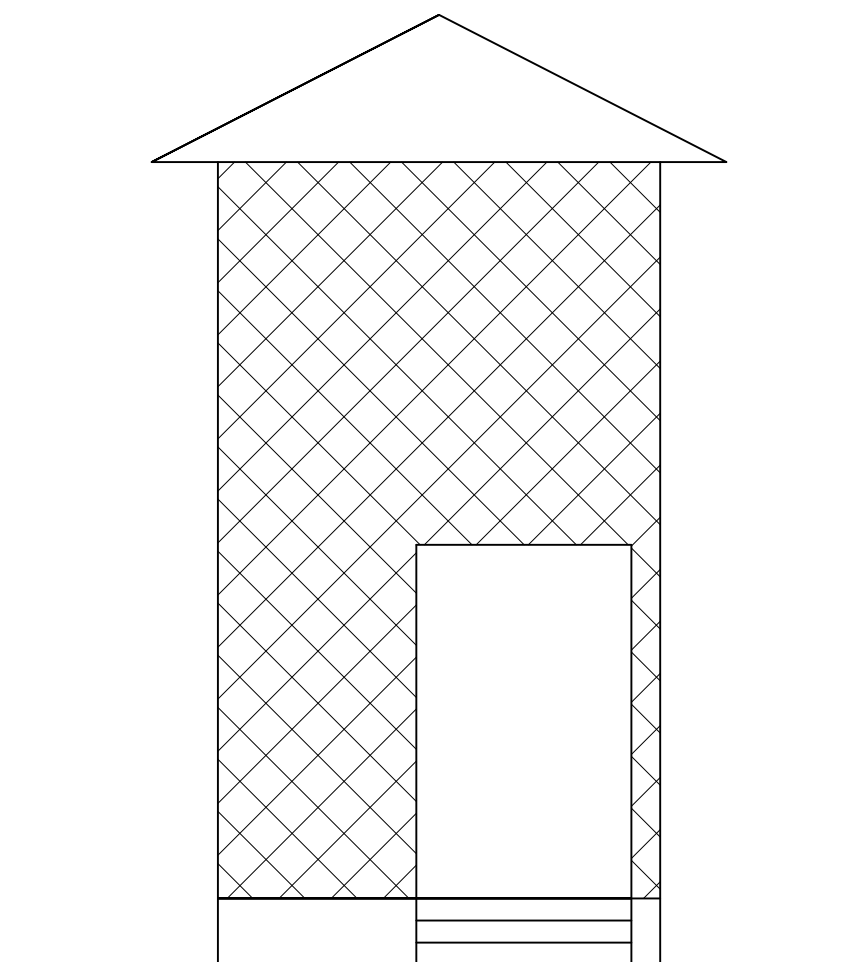

FRONT ELEVATION

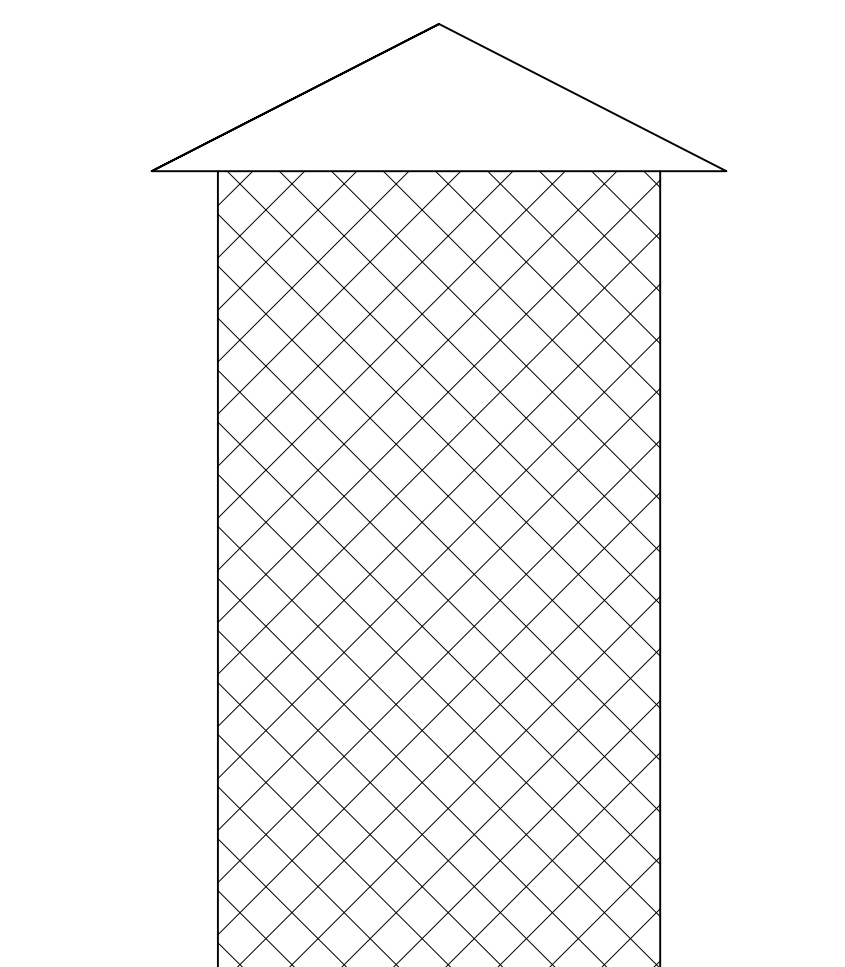


BACK ELEVATION

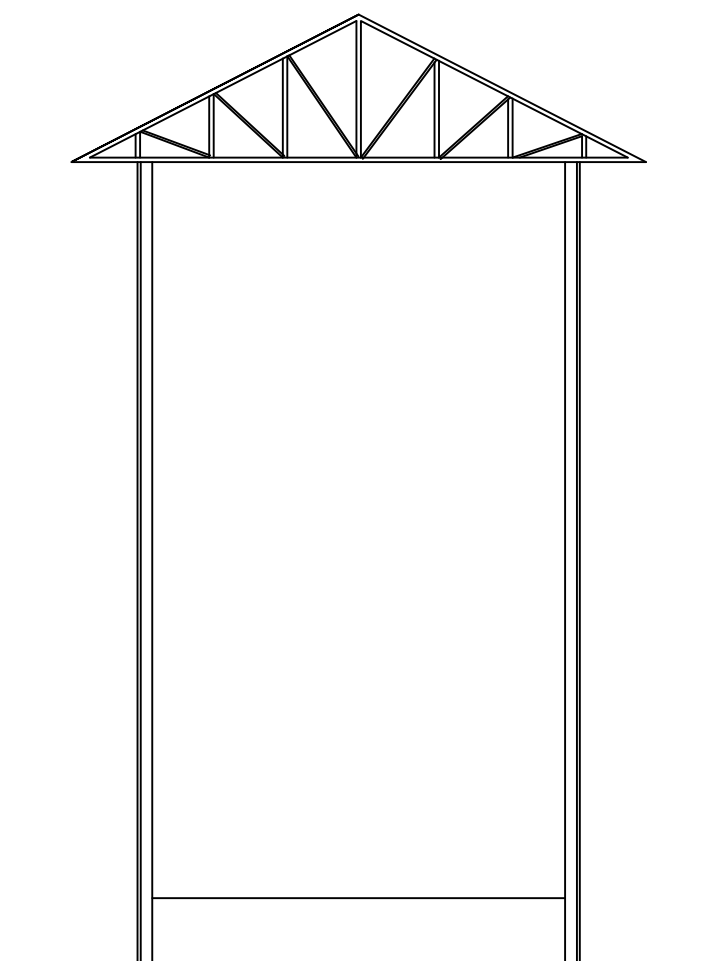


SECTION AT Y-Y


PROJECT: DPR OF 500MT COLD STORE AT JIRI, DOLAKHA	CONTENT: MECHANICAL BLOCK		CHECKED BY: APPROVED BY :	CONSULTANT: Sworaj Consultants Pvt. Ltd. Samkhushi, Kathmandu	Sheet No
CLIENT: Government of Province Ministry of Land Management, Agriculture and Cooperative Province No. 3, Hetauda	FINAL DRAWING		SCALE :		MB 01
		DATE:	REVISION:		

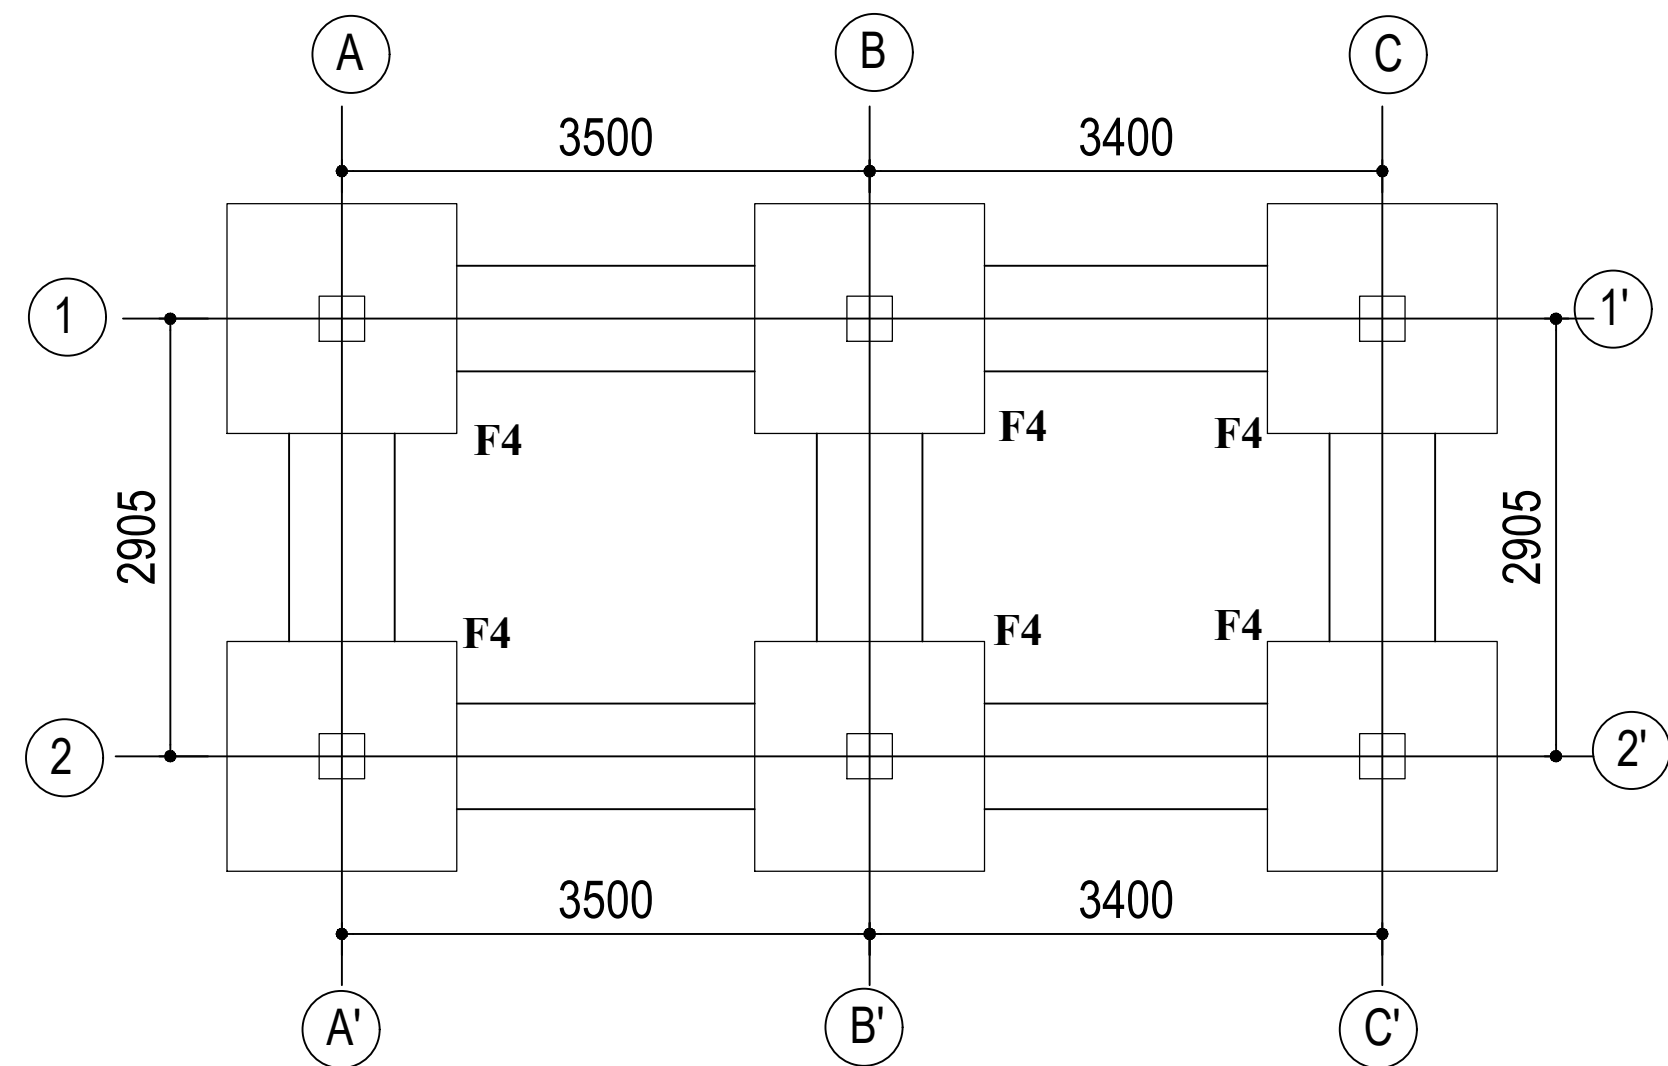


FOOTING TRENCH PLAN

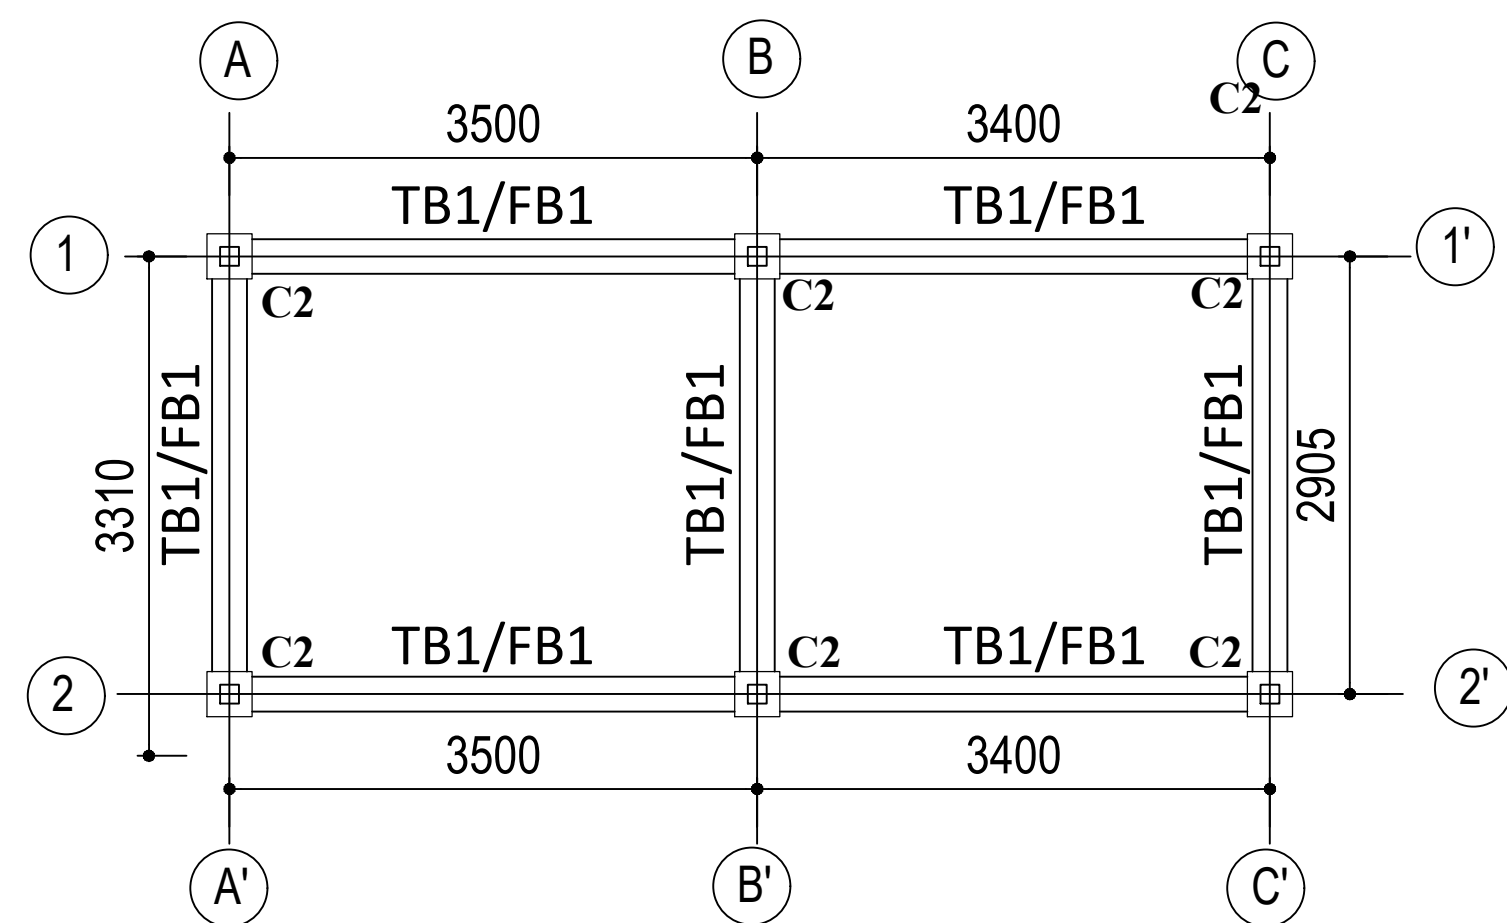


TIE BEAM LAYOUT PLAN

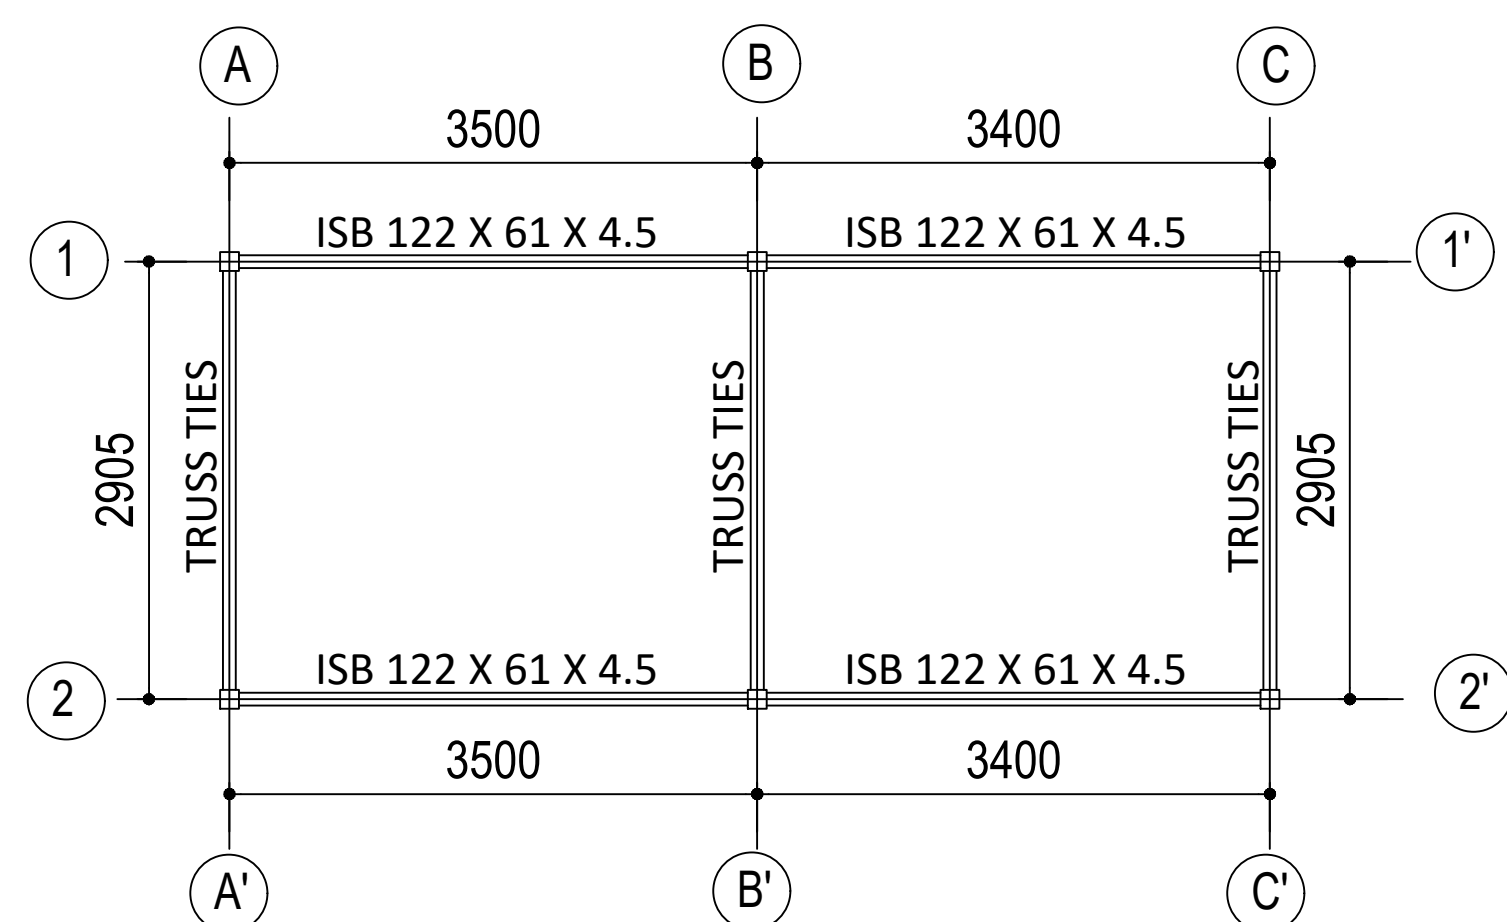

FLOOR BEAM LAYOUT PLAN

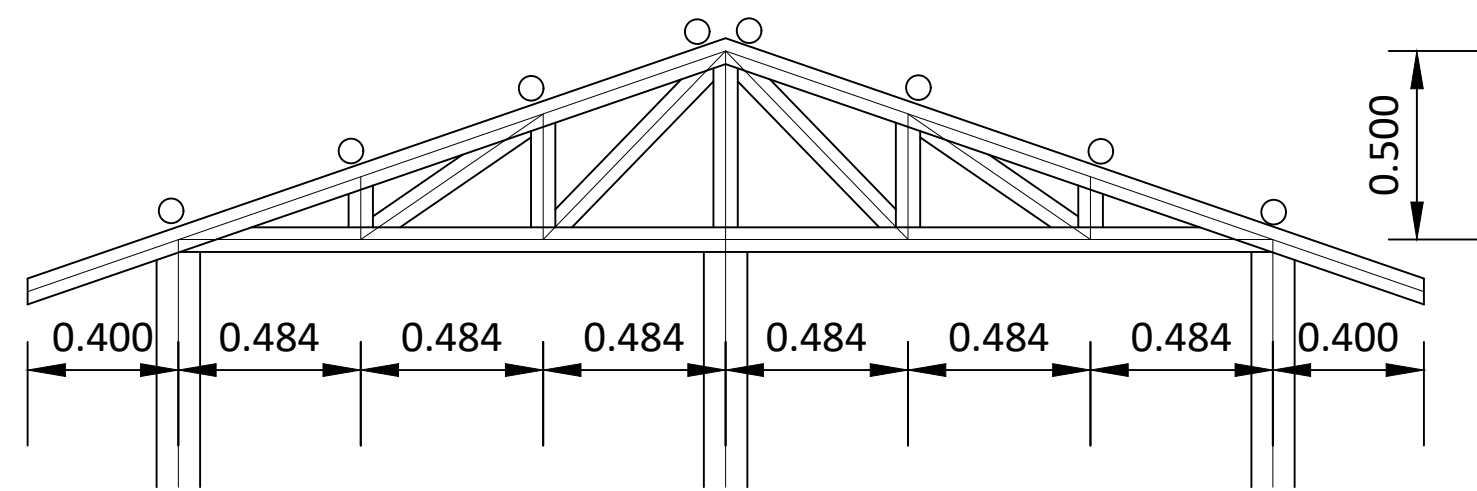


TRUSS MEMBER SIZES

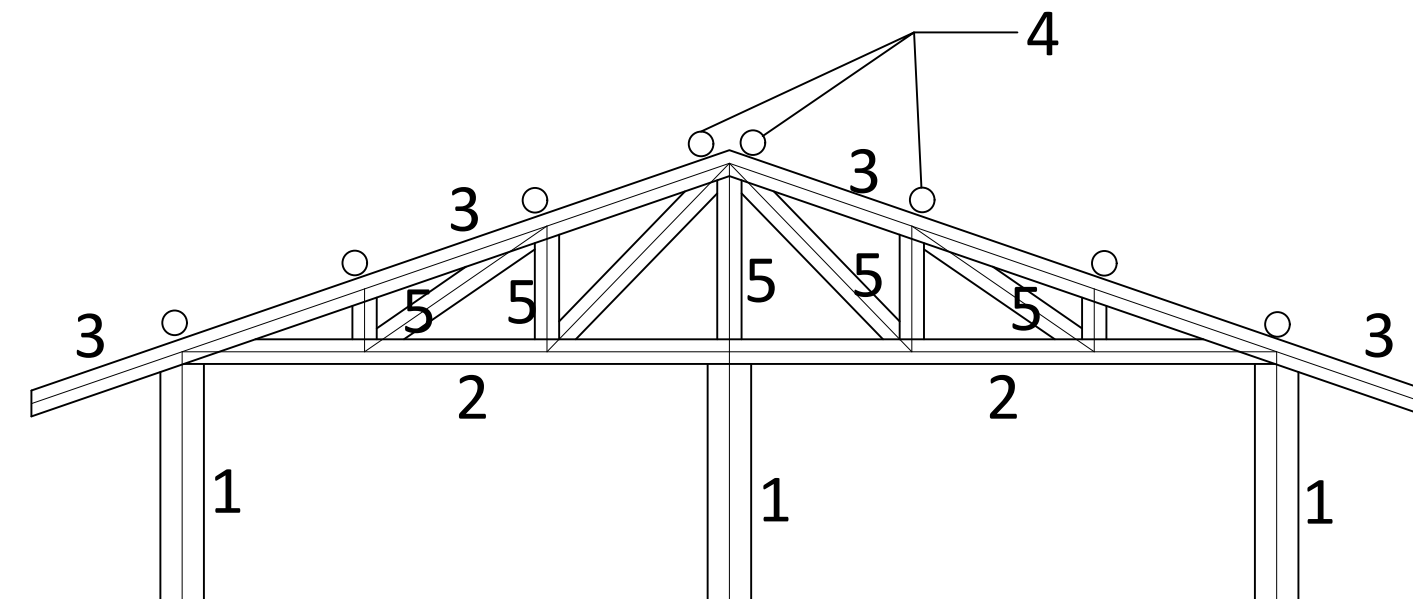


TRUSS MEMBER IDENTIFICATION


FOR DOUBLE SLOPE ROOF		
Member No.	Member Identification	Member Specifiacion
1	Post	ISB 113.5 X 113.5 X 4.8
2	Horizontal ties of truss	ISNB 65M
3	Rafter	ISNB 65M
4	Purlin	ISNB 65M
5	Struts	ISNB 65M

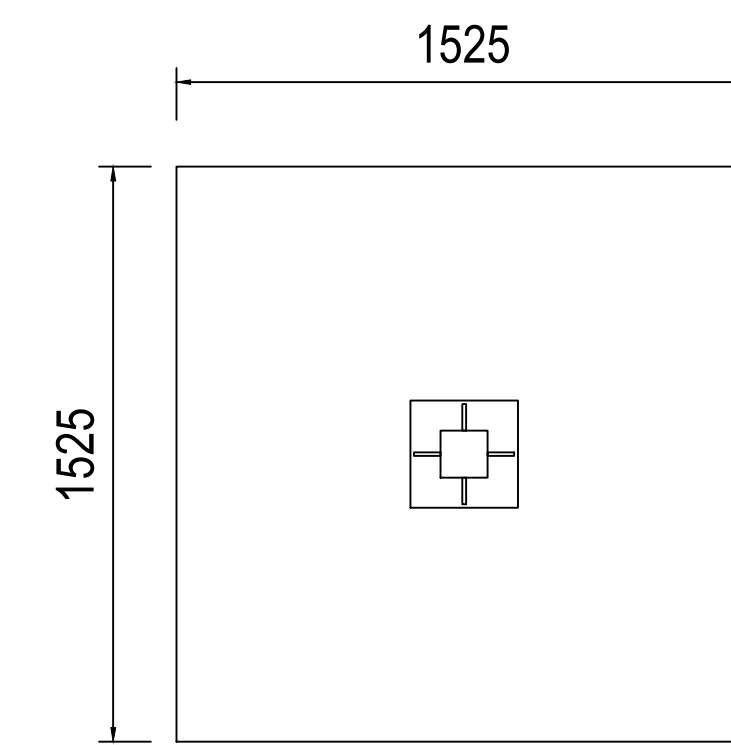


FOUNDATION-F4

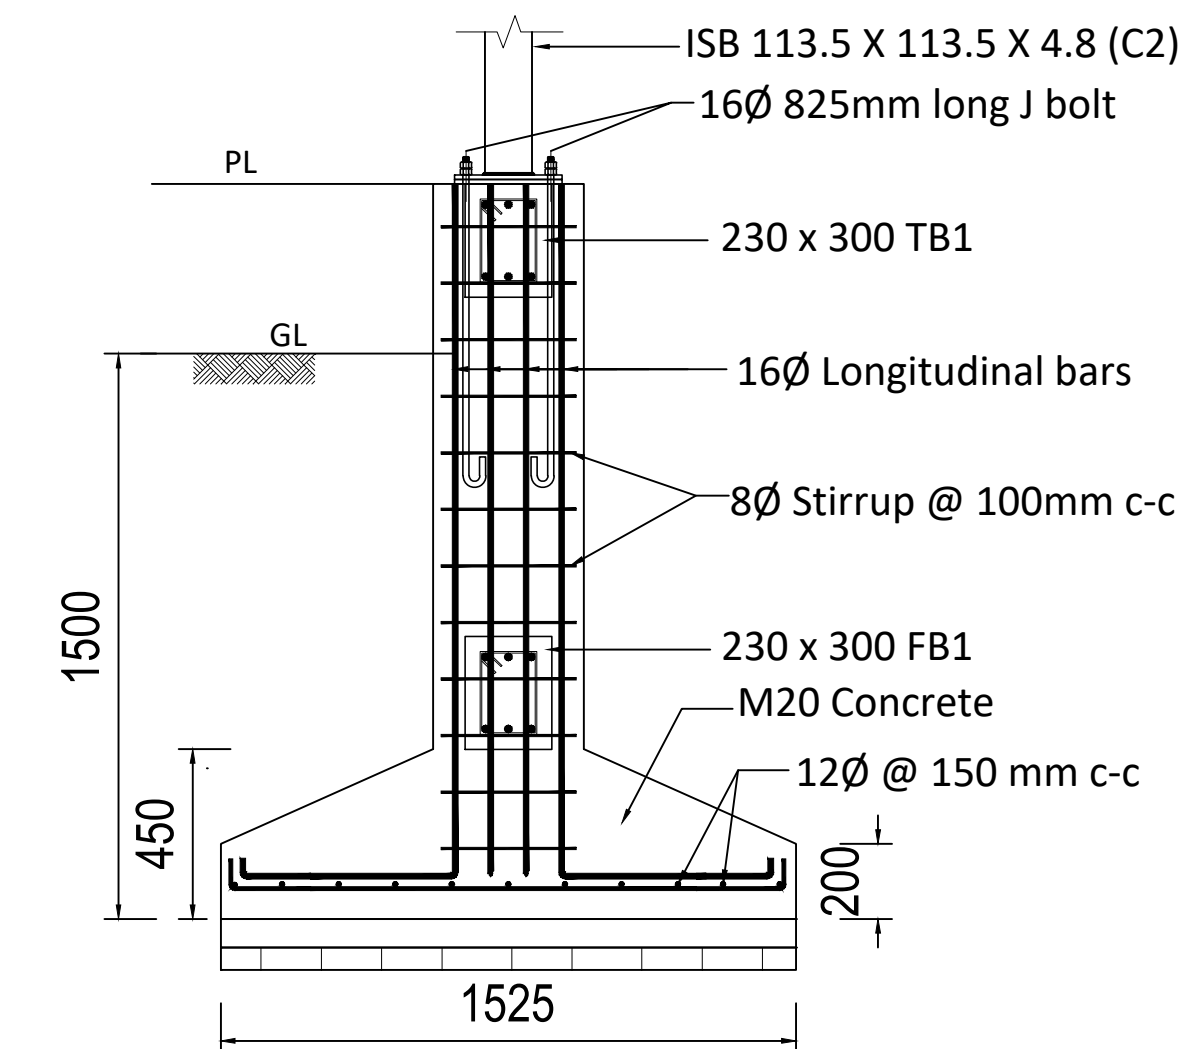



SECTION OF FOUNDATION-F4

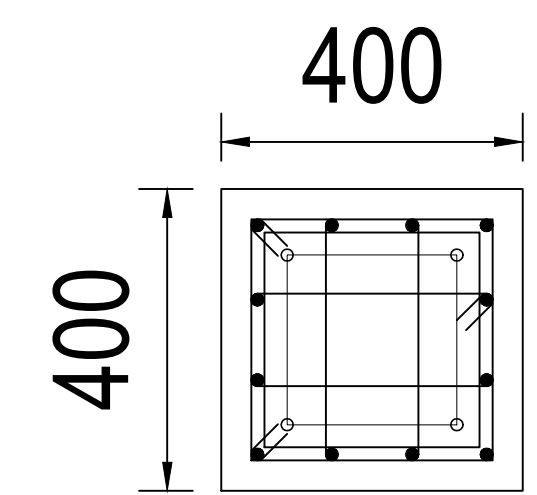


PEDESTAL DETAIL OF FOUNDATION-F1

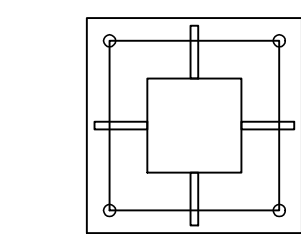


BASE PLATE DETAIL (285x285x12) (For Vertical Post - C2)

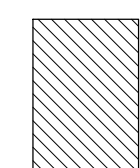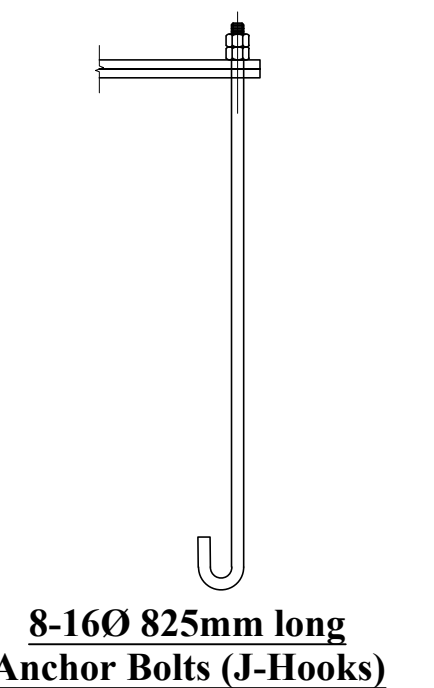

STIFFENER - S1 (10mm thick)

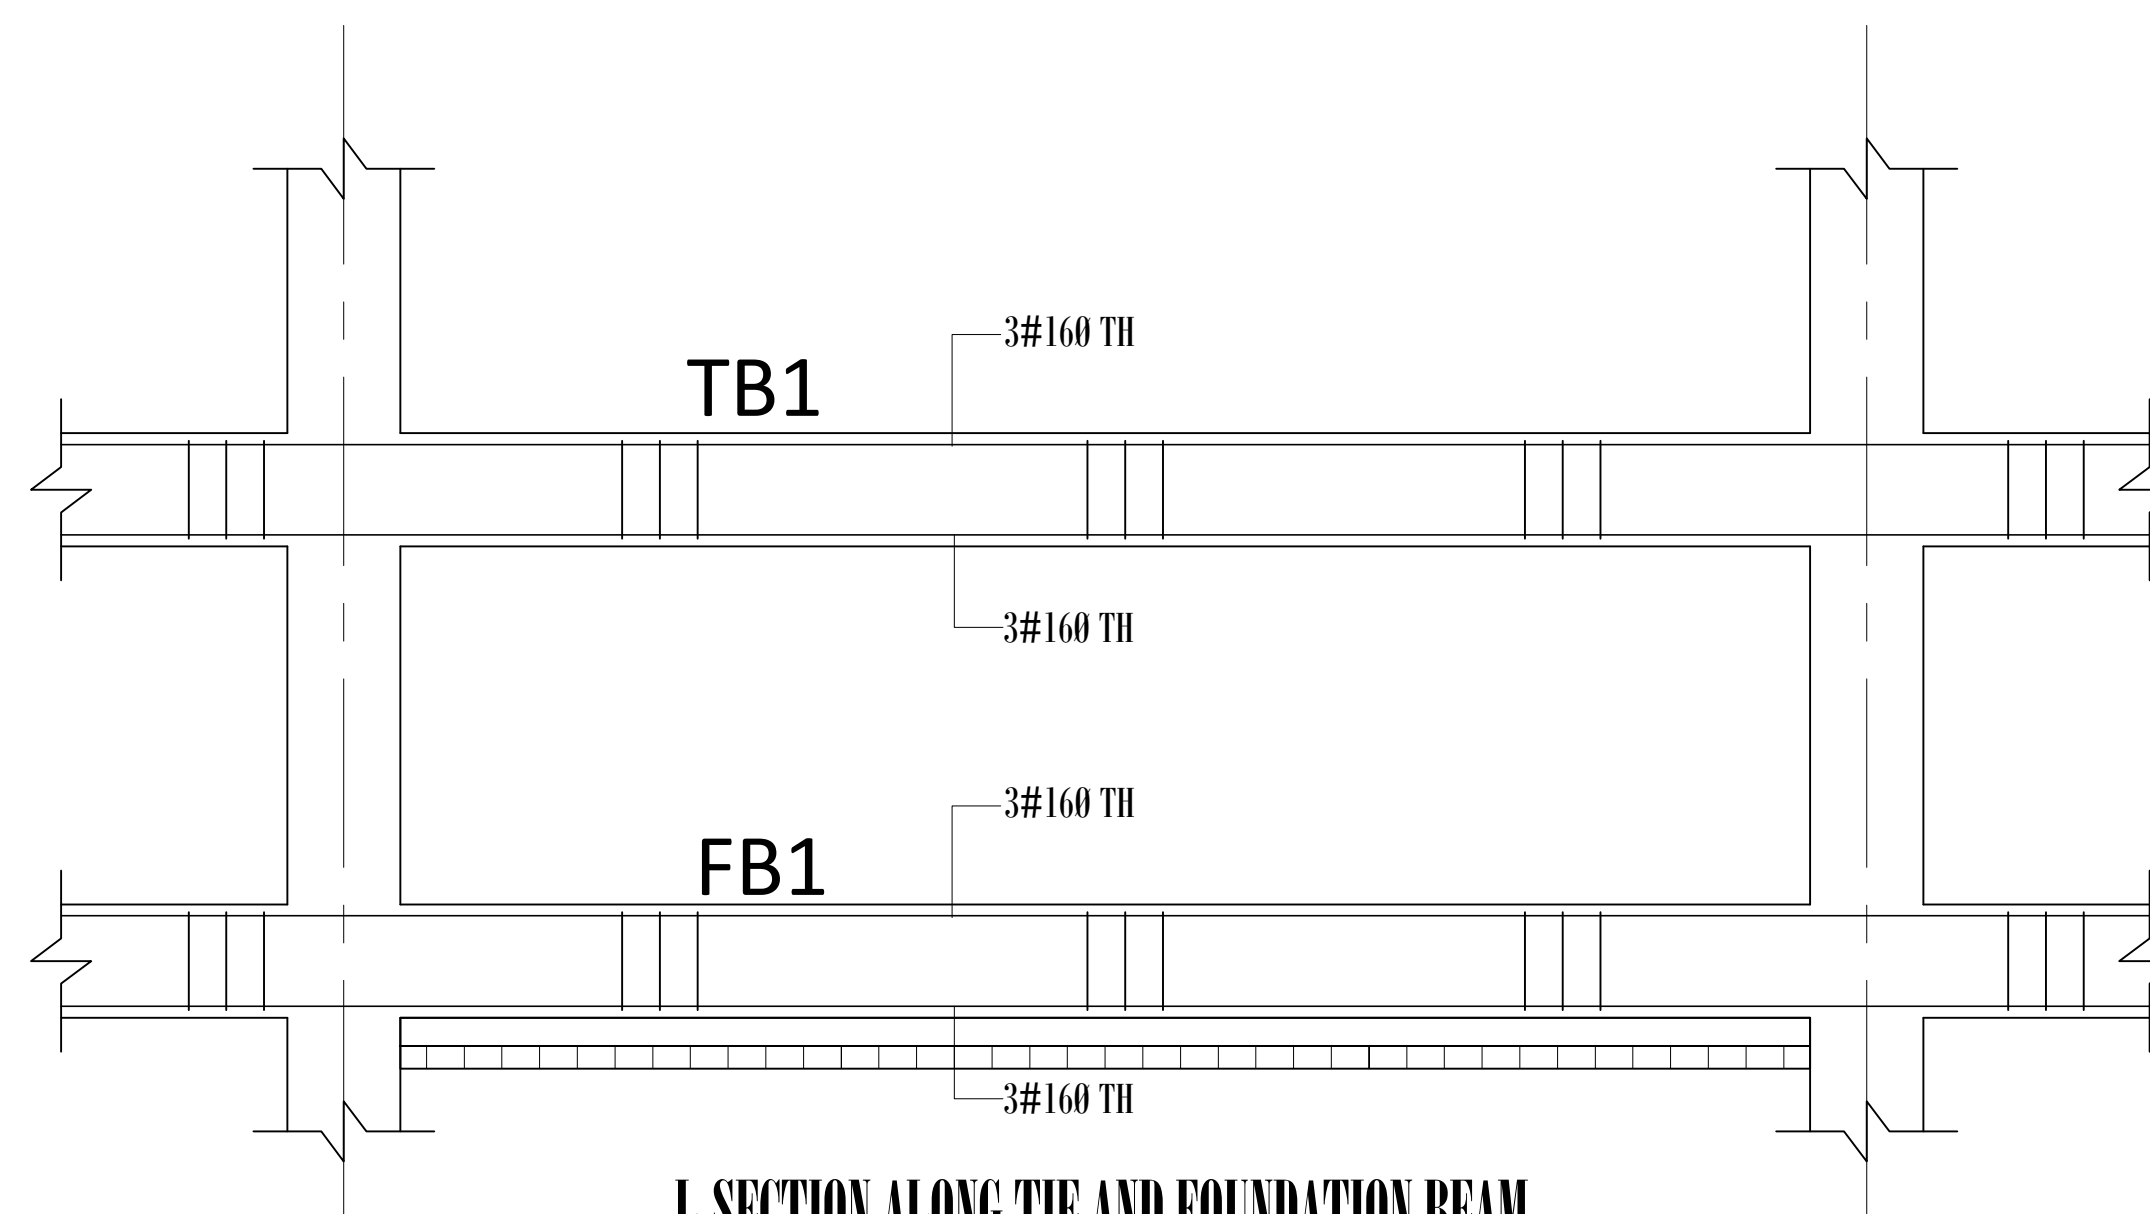

L-SECTION ALONG TIE AND FOUNDATION BEAM

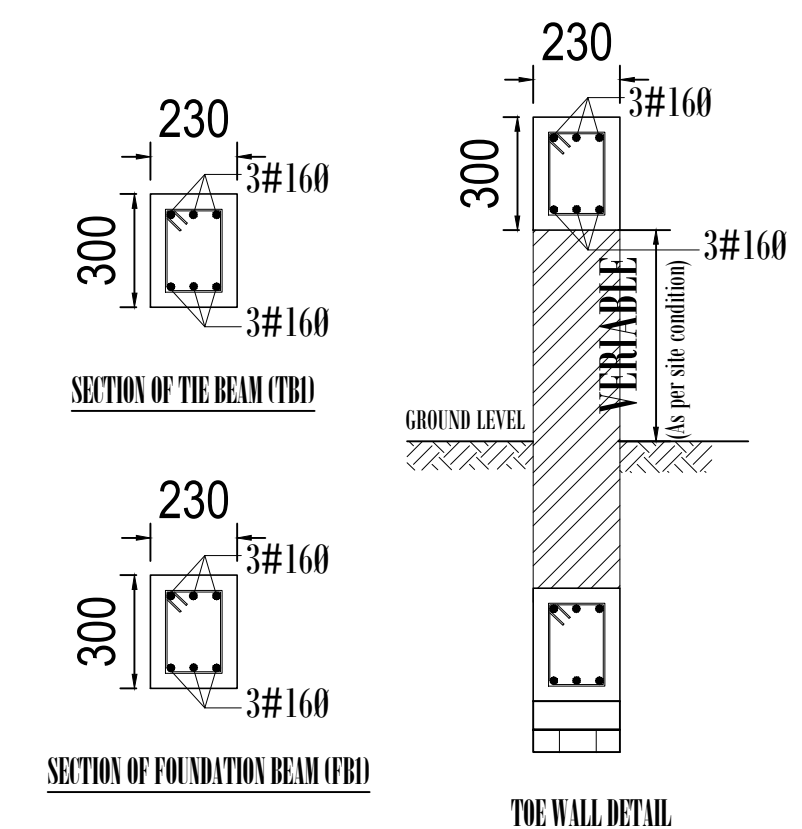

PROJECT:
DPR OF 500MT COLD STORE AT JIRI, DOLAKHA

CONTENT:
MECHANICAL BLOCK

CHECKED BY:

CONSULTANT:

CLIENT:
Government of Province
Ministry of Land Management, Agriculture and Cooperative
Province No. 3, Hetauda

FINAL DRAWING

APPROVED BY :

Sworaj Consultants Pvt. Ltd.
Samkhushi, Kathmandu

SCALE :

DATE:


REVISION:


Sheet No

MB

02

TOILET BLOCK

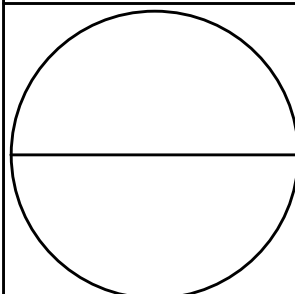
PROJECT: DPR OF 500MT COLD STORE AT JIRI, DOLAKHA	CONTENT: TOILET BLOCK		CHECKED BY:	CONSULTANT: Sworaj Consultants Pvt. Ltd. Samkhushi, Kathmandu	Sheet No
CLIENT: Government of Province Ministry of Land Management, Agriculture and Cooperative Province No. 3, Hetauda	FINAL DRAWING		APPROVED BY :		
			SCALE :		
			DATE:		

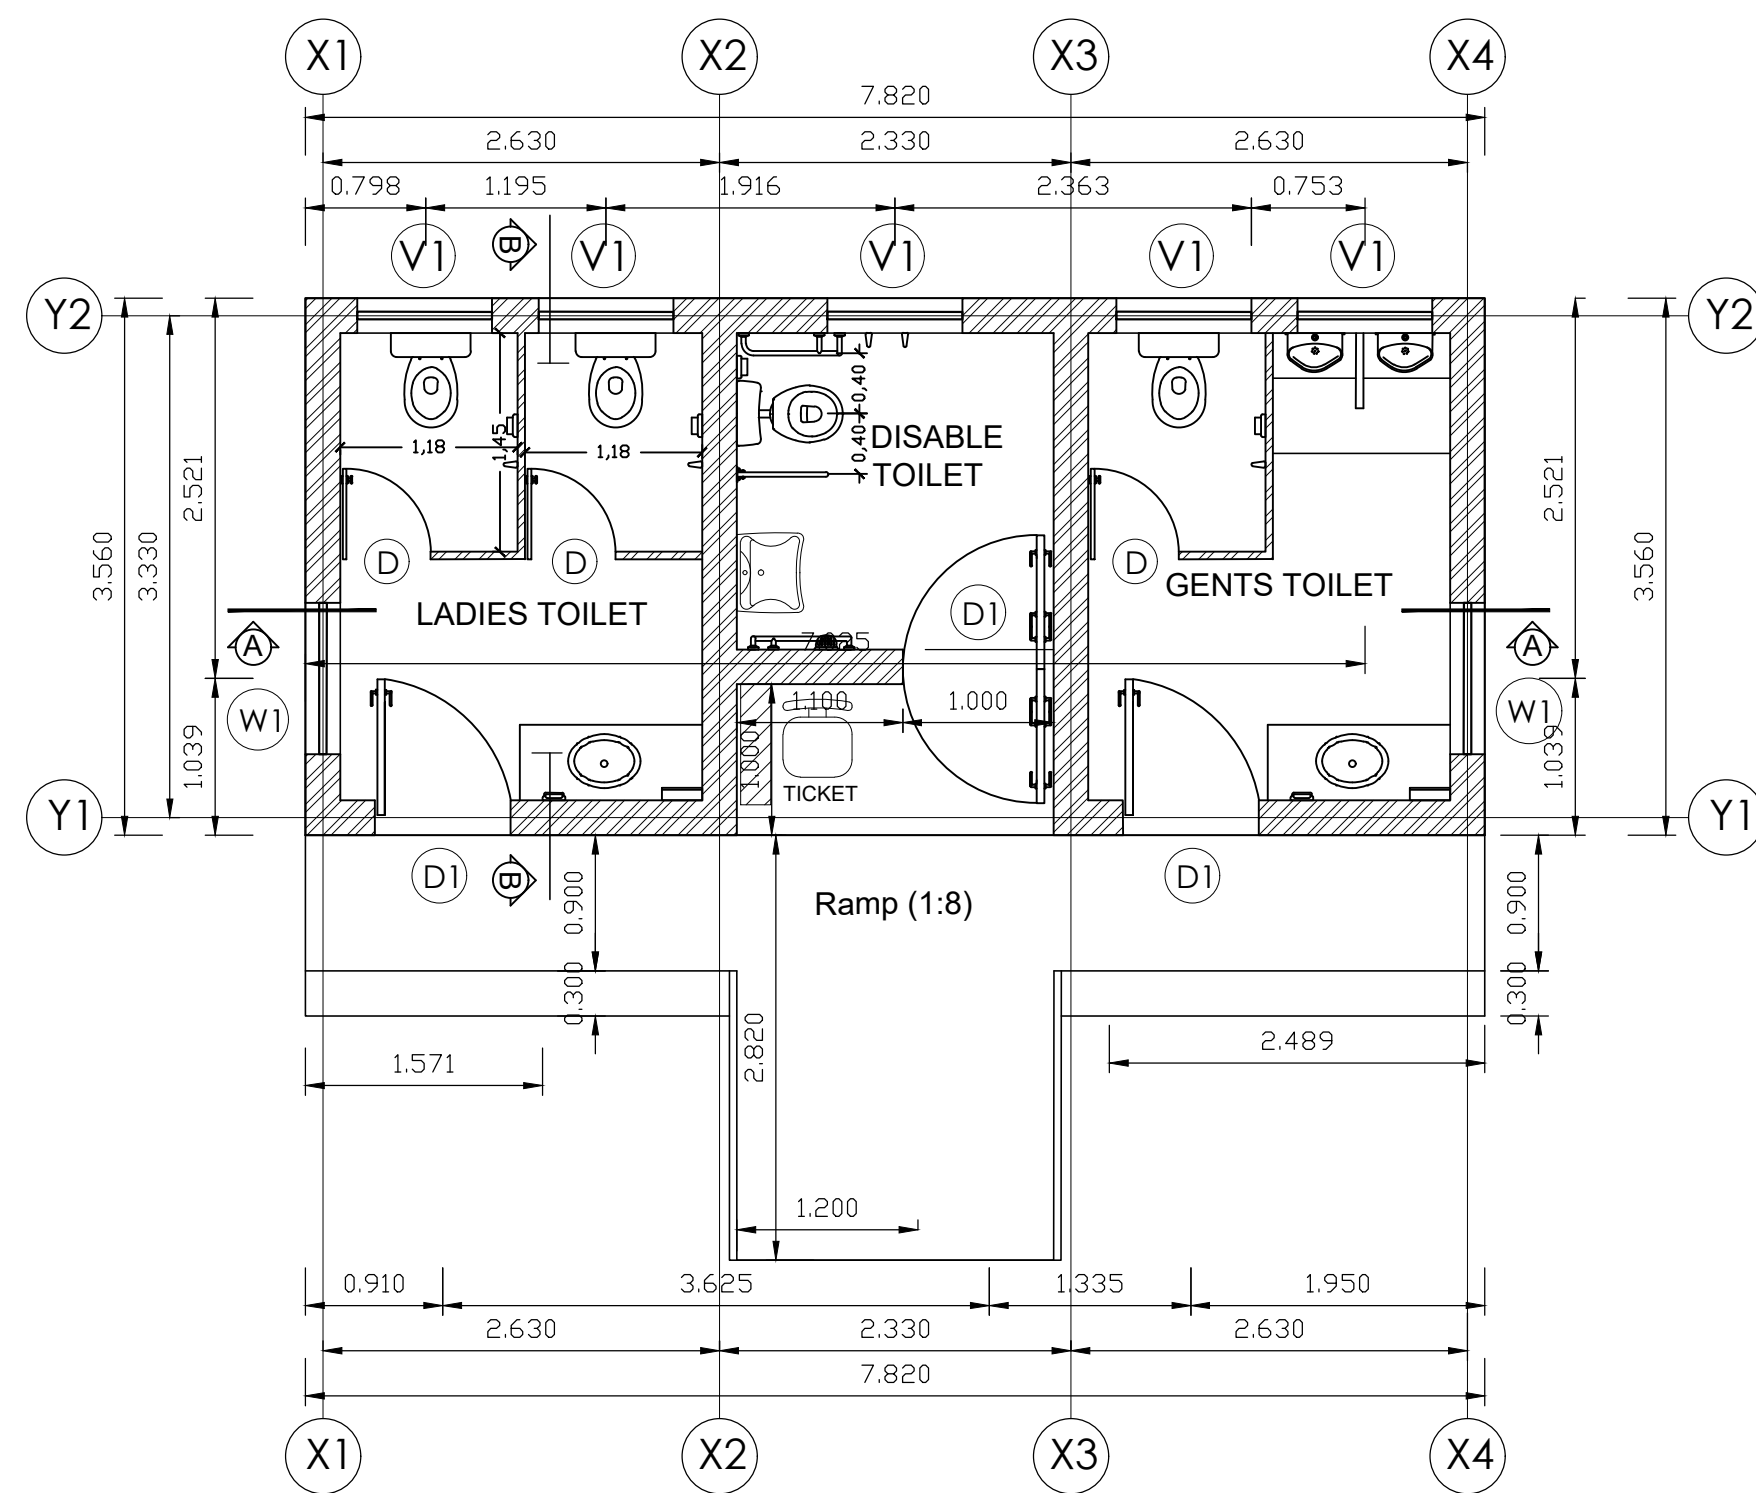

GROUND FLOOR PLAN

AREA: 27.8 SQ.M

SCALE: 1:100

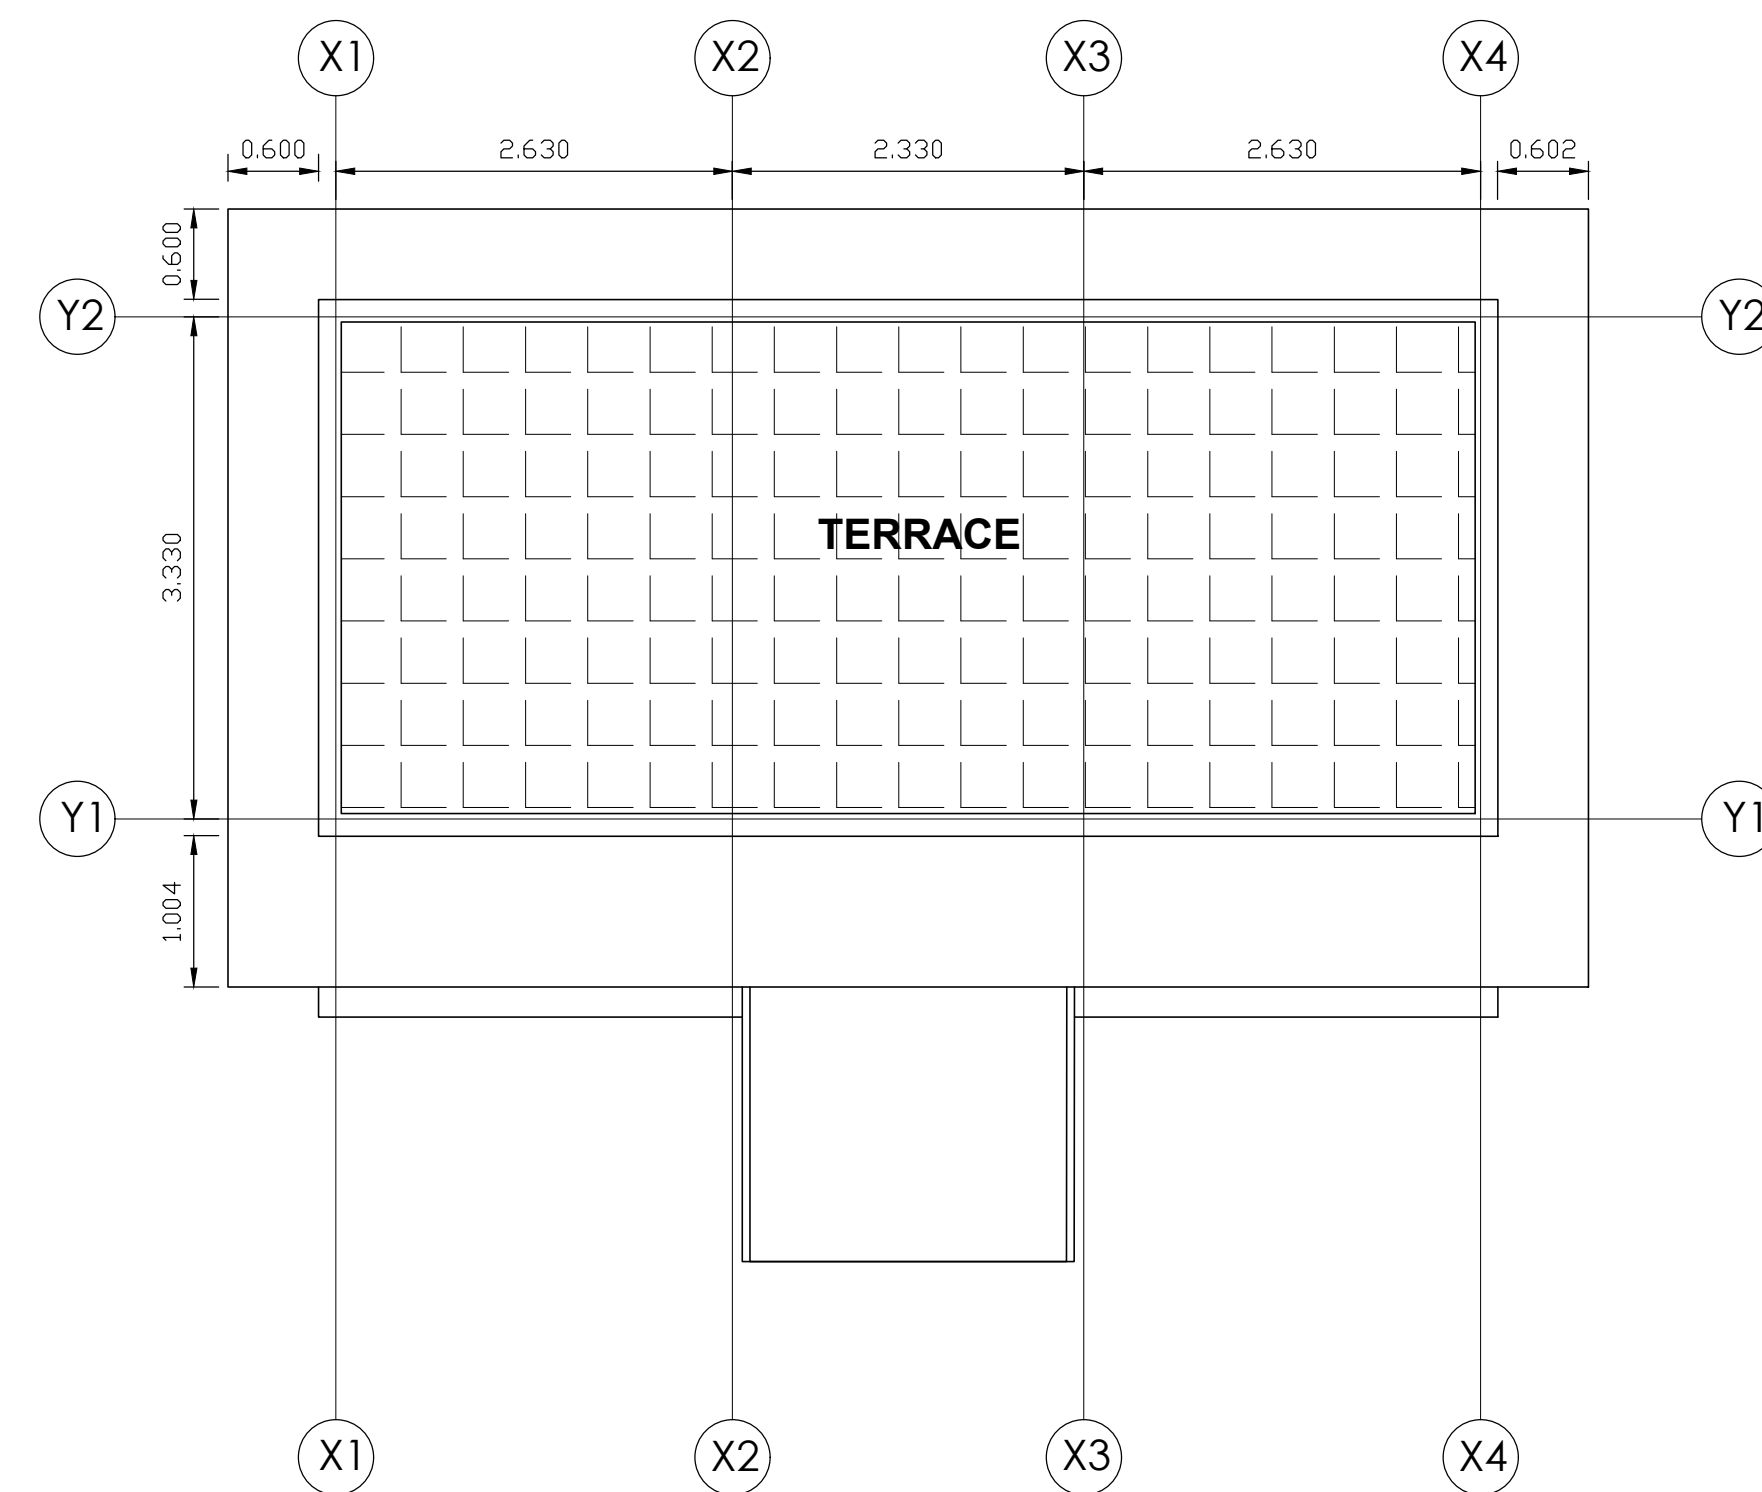

ROOF PLAN

SCALE: 1:100

PROJECT:
DPR OF 500MT COLD STORE AT JIRI, DOLAKHA

CONTENT:
TOILET BLOCK

CHECKED BY:

CONSULTANT:

Sheet No

CLIENT:
Government of Province
Ministry of Land Management, Agriculture and Cooperative
Province No. 3, Hetauda

FINAL DRAWING

APPROVED BY :

Sworaj Consultants Pvt. Ltd.
Samkhushi, Kathmandu


SCALE :

DATE:


REVISION:



TB

01

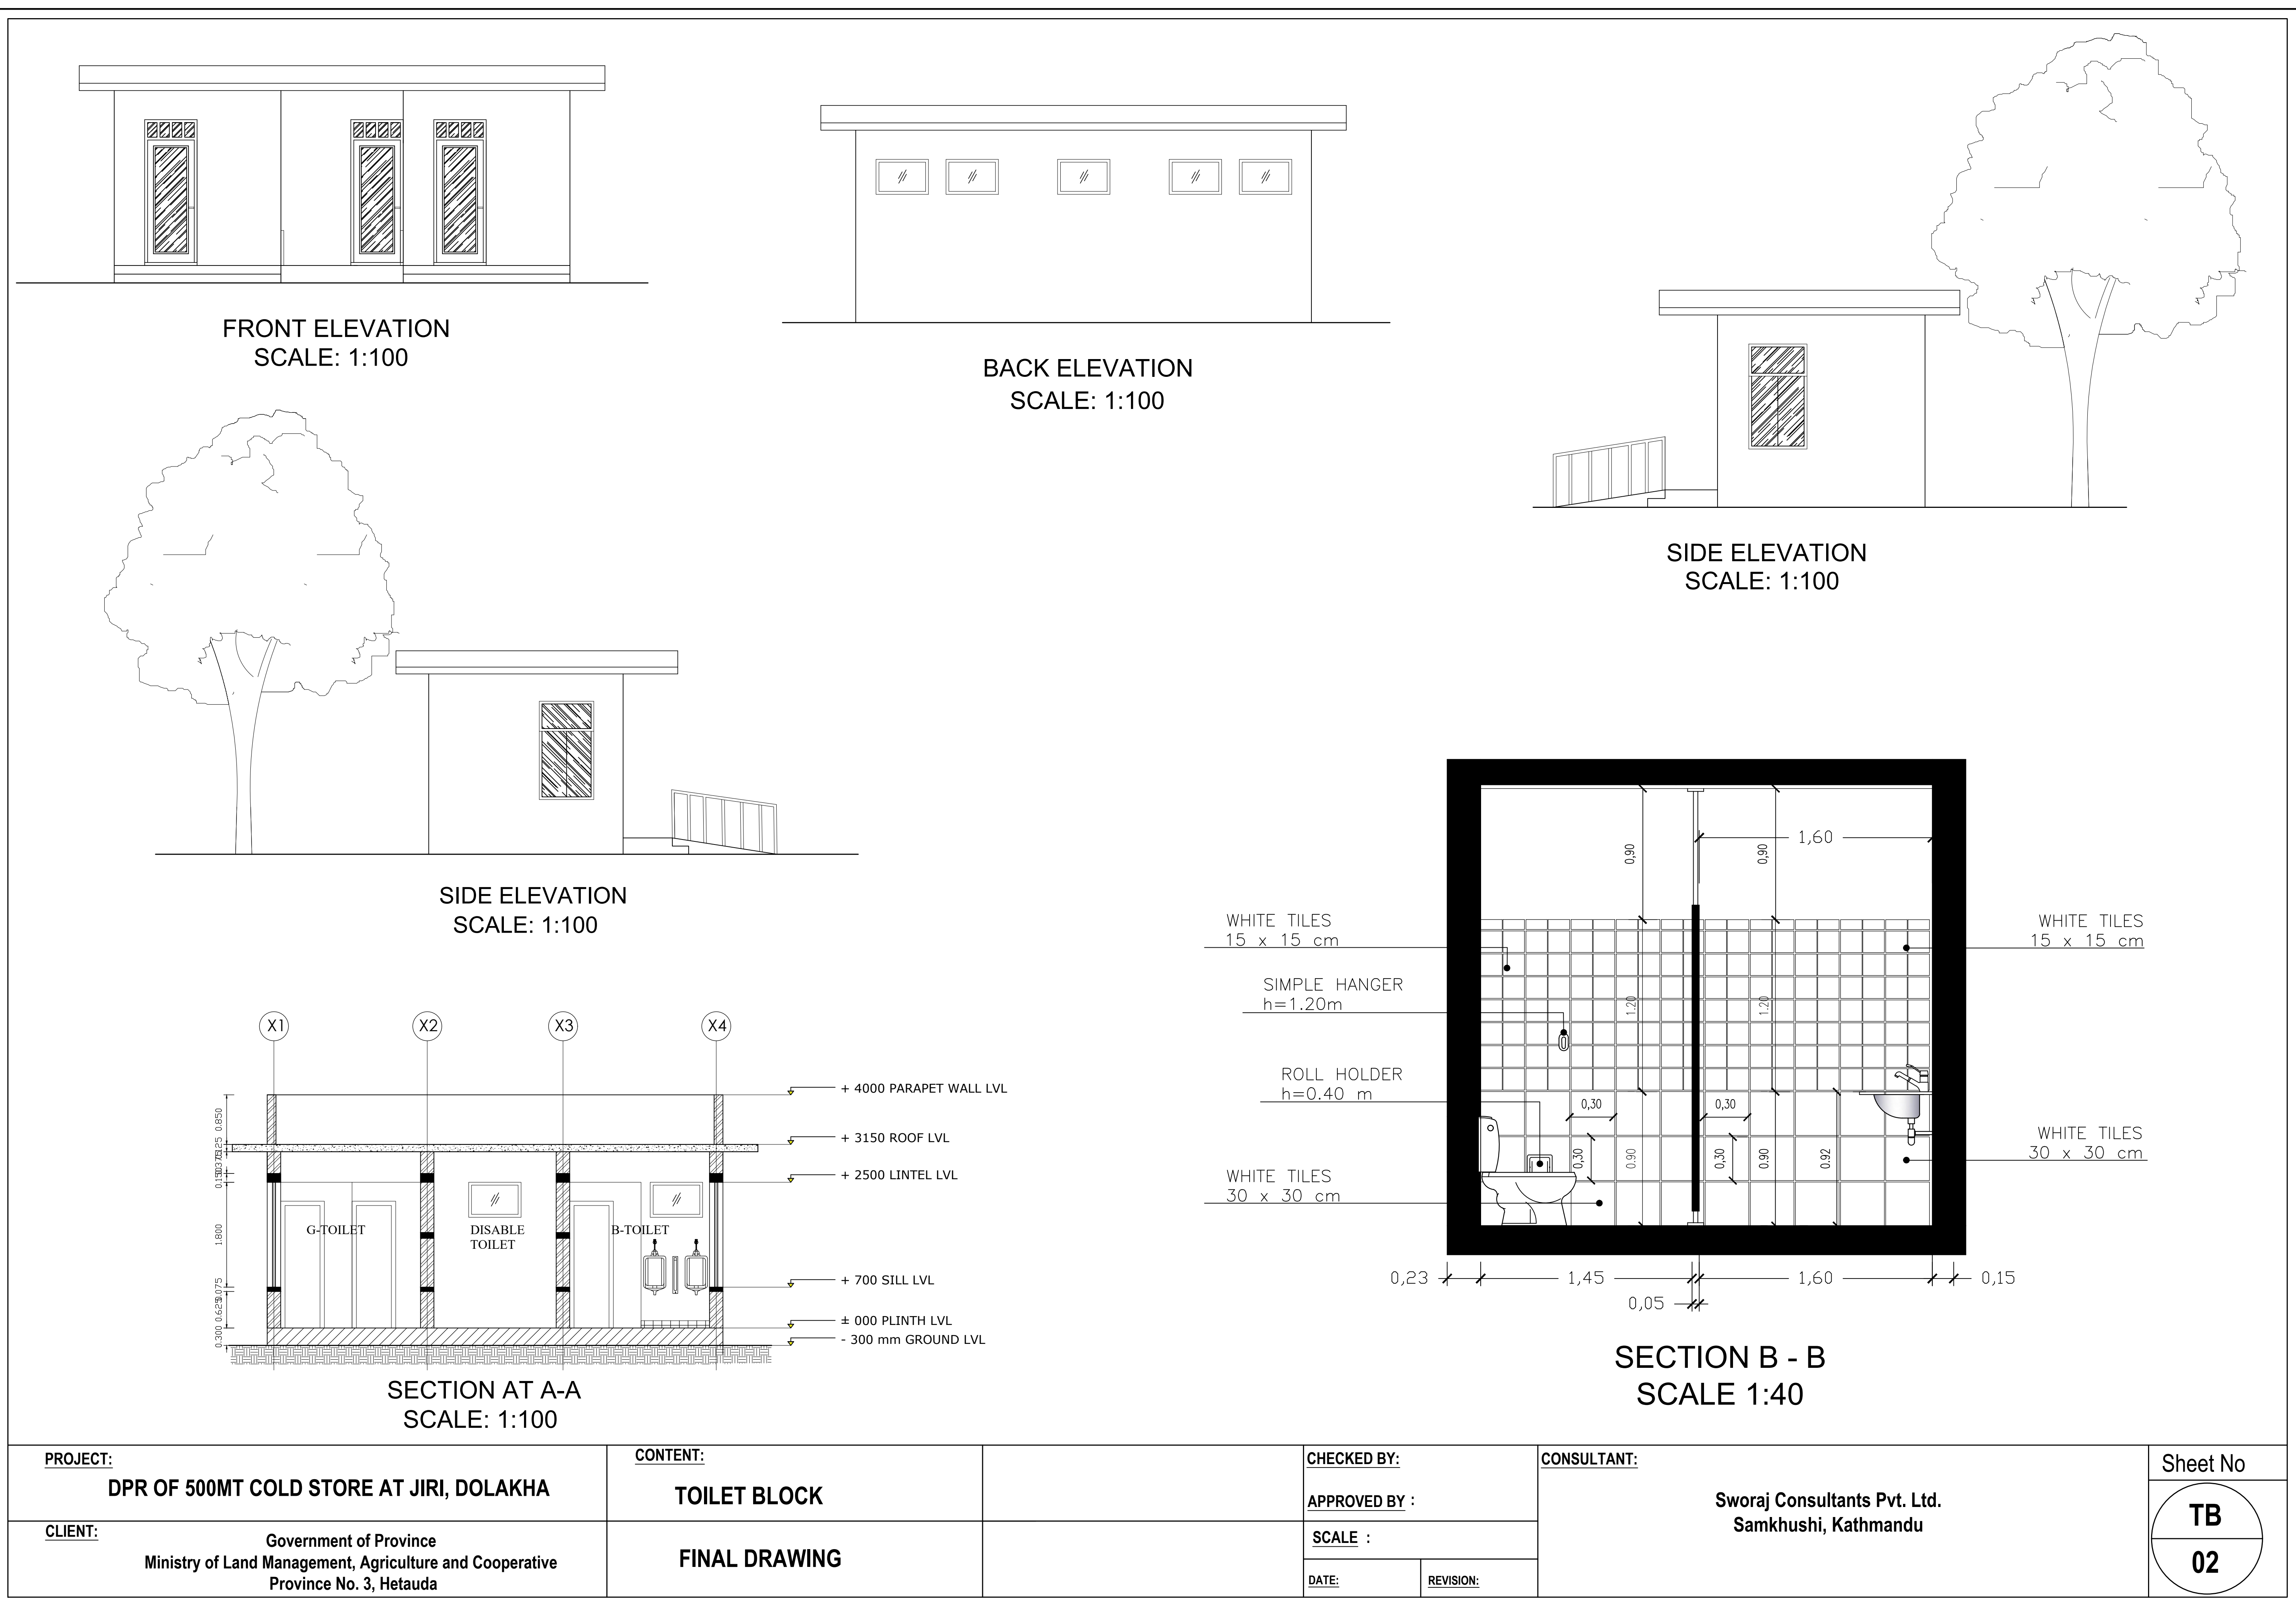


APPROACH ROAD DRAWINGS

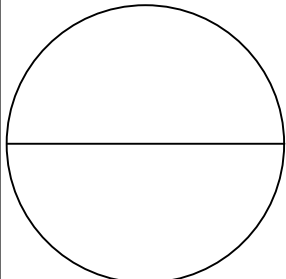PROJECT: DPR OF 500MT COLD STORE AT JIRI, DOLAKHA	CONTENT: APPROACH ROAD		CHECKED BY: APPROVED BY :	CONSULTANT: Sworaj Consultants Pvt. Ltd. Samkhushi, Kathmandu	Sheet No 
CLIENT: Government of Province Ministry of Land Management, Agriculture and Cooperative Province No. 3, Hetauda	FINAL DRAWING		SCALE : DATE: Falgun, 2075 REVISION:		






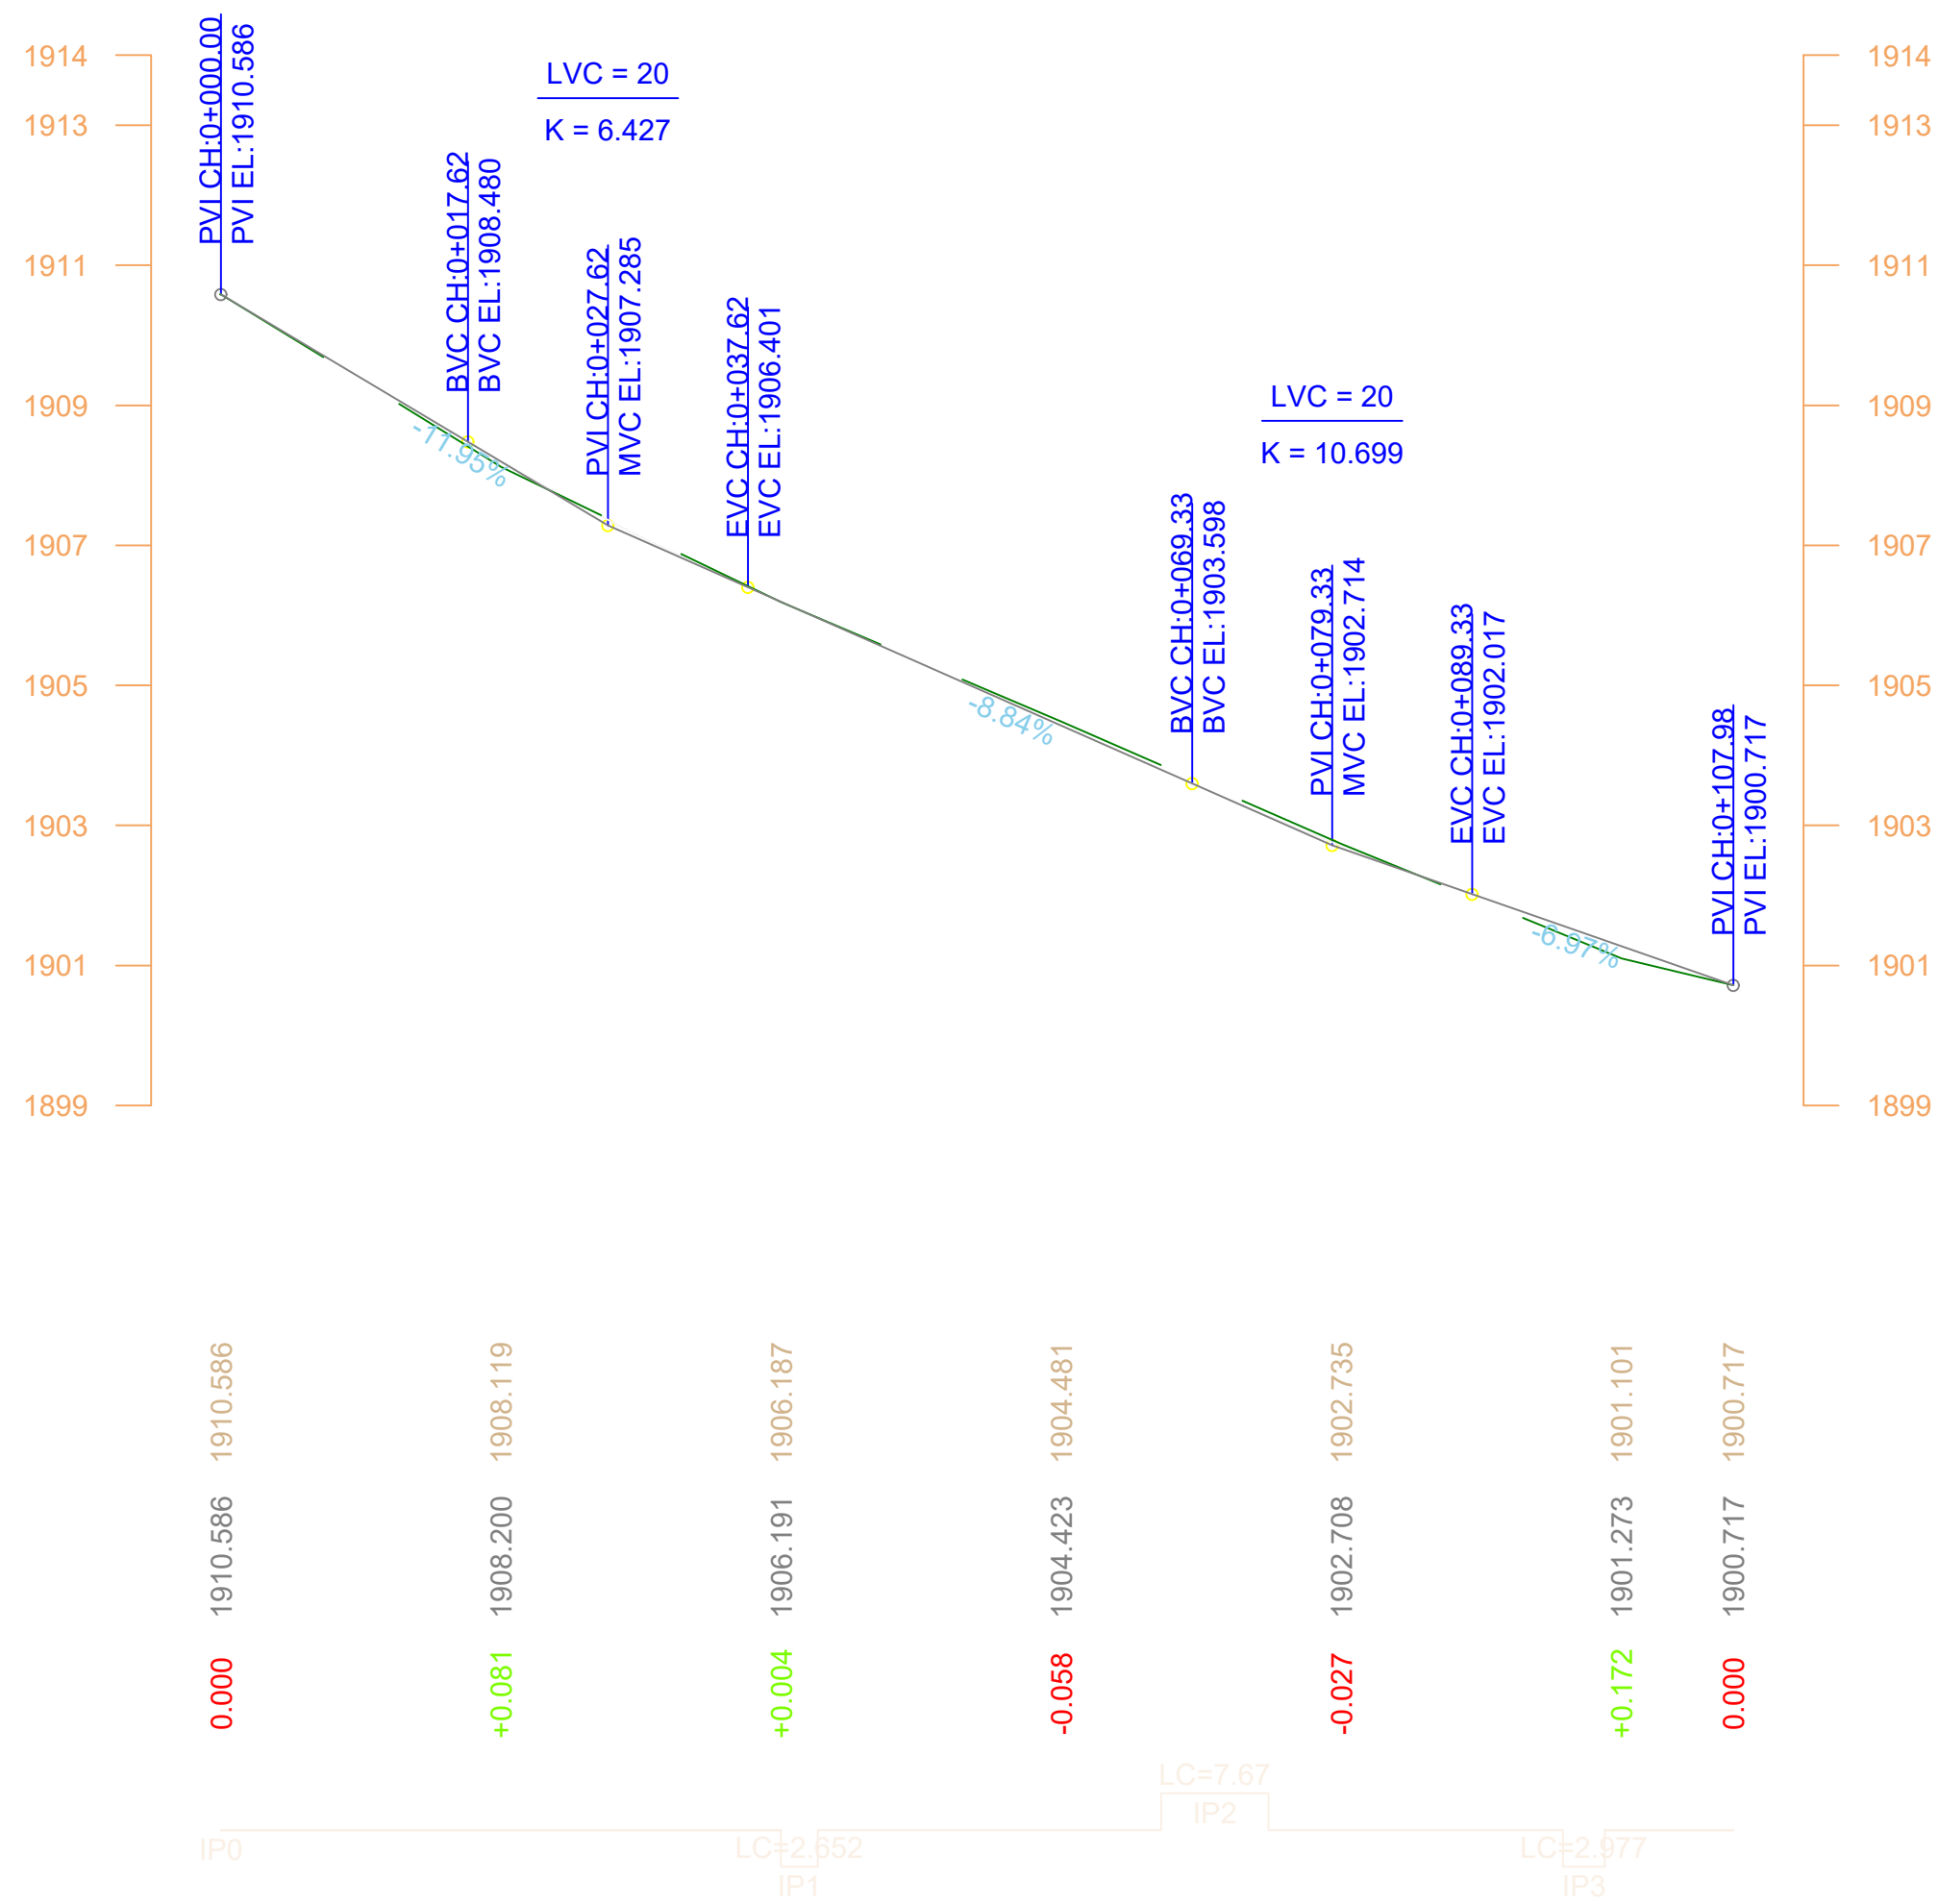
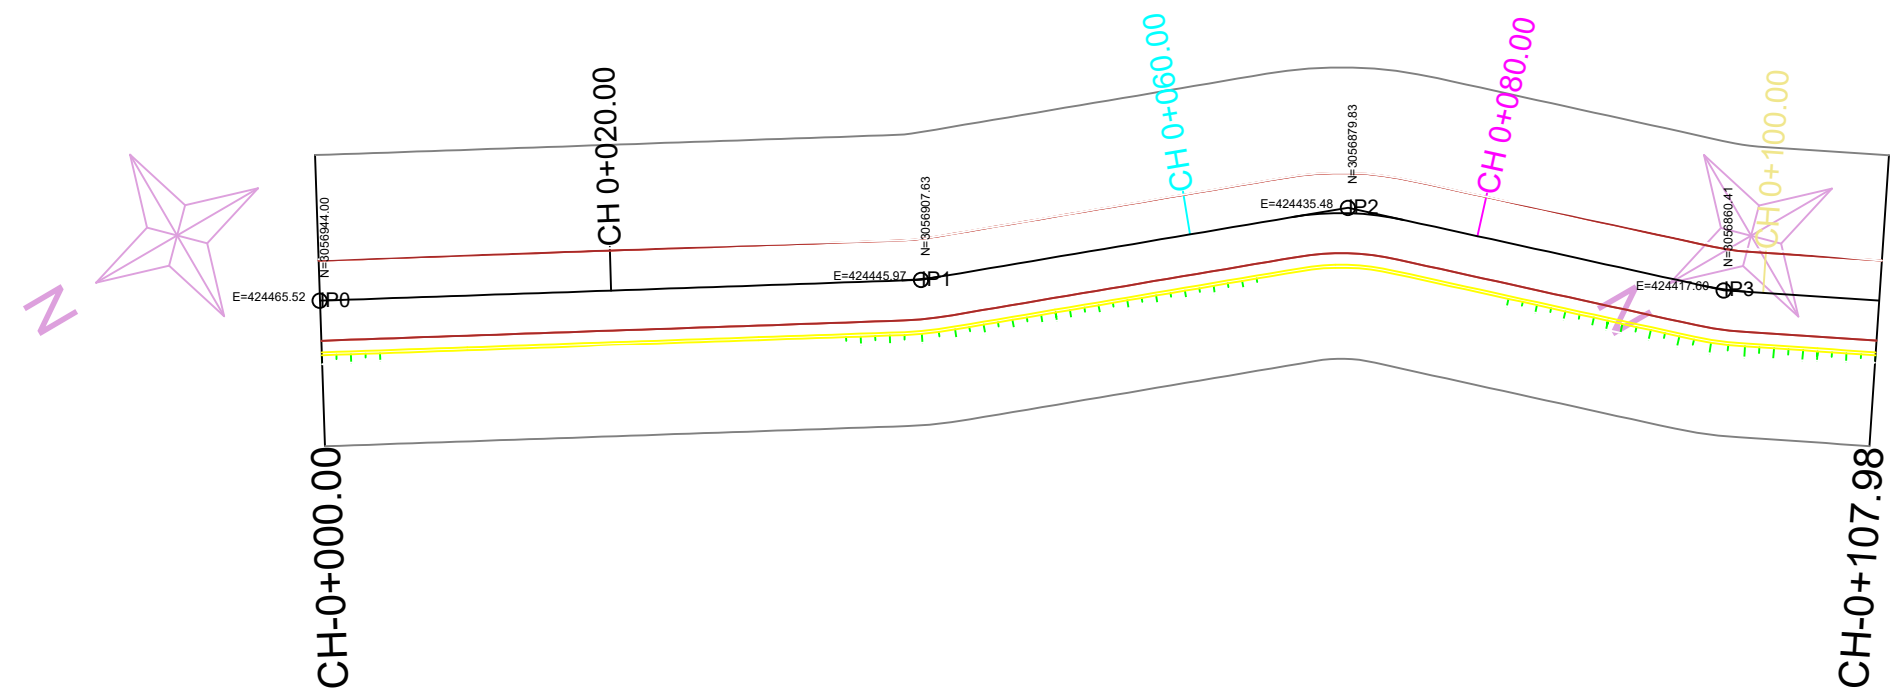


Horizontal Alignment Data											
IP	Easting	Northing	Radius	Chainage	BC	MC	EC	Deflection Angle	Tangent	Transition Length	Superelevation
IP0	424465.52	3056943.997	0	0+000.00	0+000.00	0+000.00	0+000.00	0	0	0	0
IP1	424445.967	3056907.632	20	0+041.29	0+039.96	0+041.29	0+042.61	7.596	1.328	0	0
IP2	424435.478	3056879.829	20	0+071.00	0+067.12	0+070.95	0+074.79	21.973	3.883	0	0
IP3	424417.597	3056860.414	20	0+097.30	0+095.81	0+097.30	0+098.78	8.529	1.491	0	0

PROJECT: DPR OF 500MT COLD STORE AT JIRI, DOLAKHA		CONTENT: ROAD - PLAN & PROFILE SHEETS		CHECKED BY: APPROVED BY :		CONSULTANT: Sworaj Consultants Pvt. Ltd. Samkhushi, Kathmandu		Sheet No	
CLIENT: Government of Province Ministry of Land Management, Agriculture and Cooperative Province No. 3, Hetauda		FINAL DRAWING		SCALE :				AR 01	
				DATE: Falgun, 2075 REVISION:					

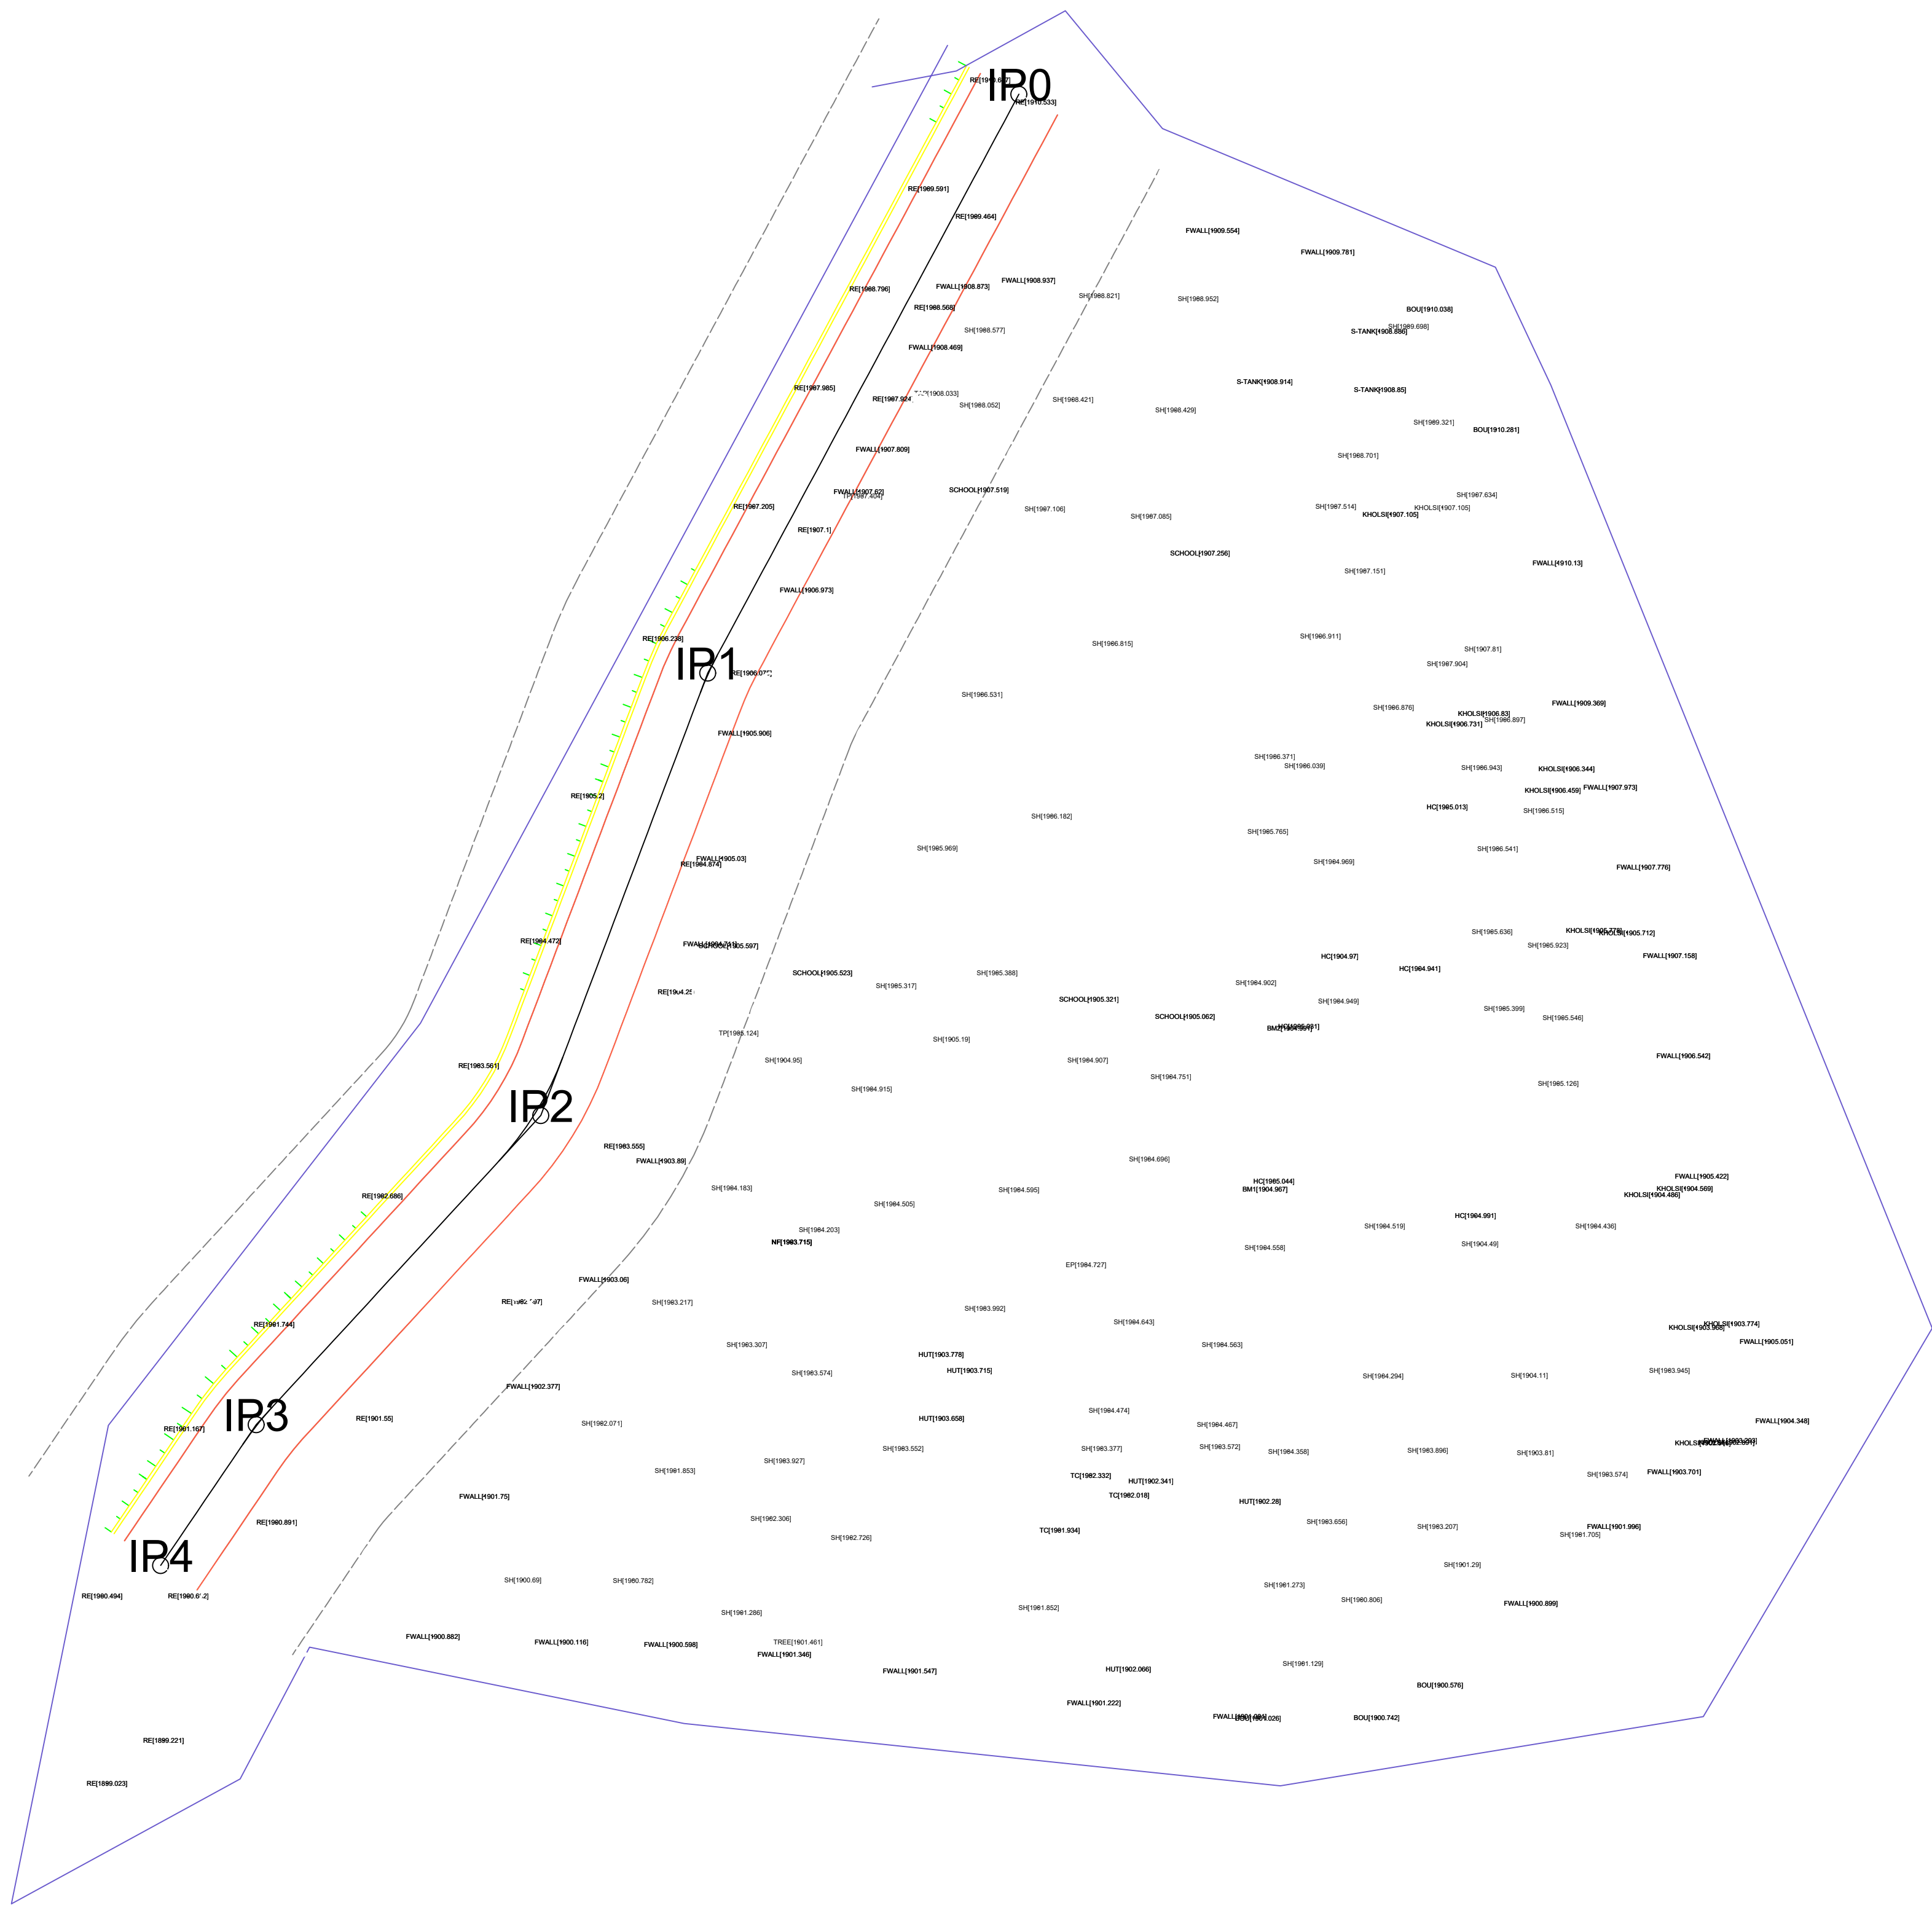

PROJECT: DPR OF 500MT COLD STORE AT JIRI, DOLAKHA		CONTENT: ROAD - PLAN AND TERRAIN		CHECKED BY: APPROVED BY :		CONSULTANT: Sworaj Consultants Pvt. Ltd. Samkhushi, Kathmandu		Sheet No	
CLIENT: Government of Province Ministry of Land Management, Agriculture and Cooperative Province No. 3, Hetauda		FINAL DRAWING		SCALE :				AD 01	
				DATE: REVISION:					

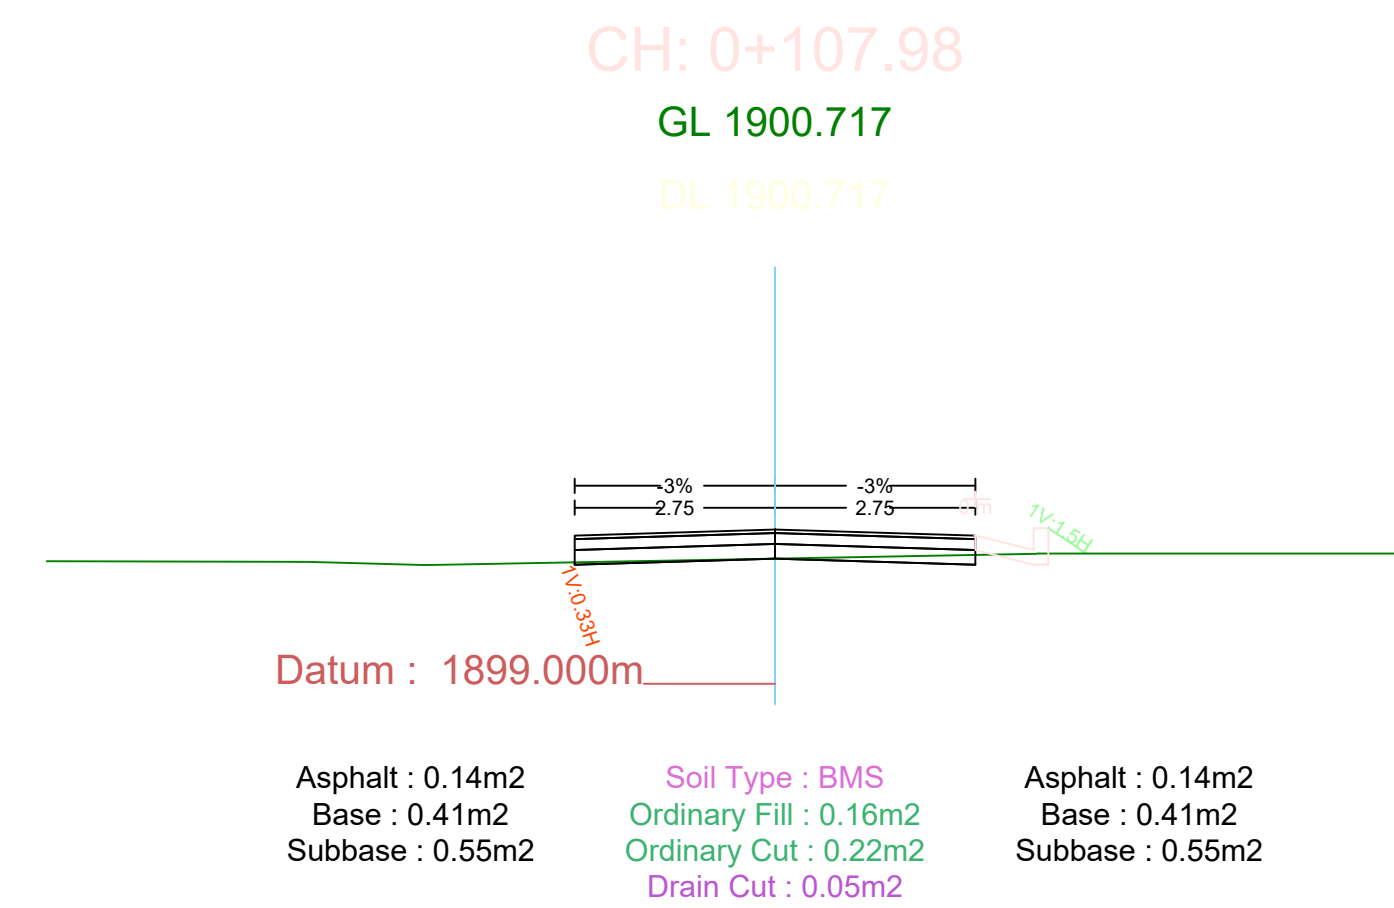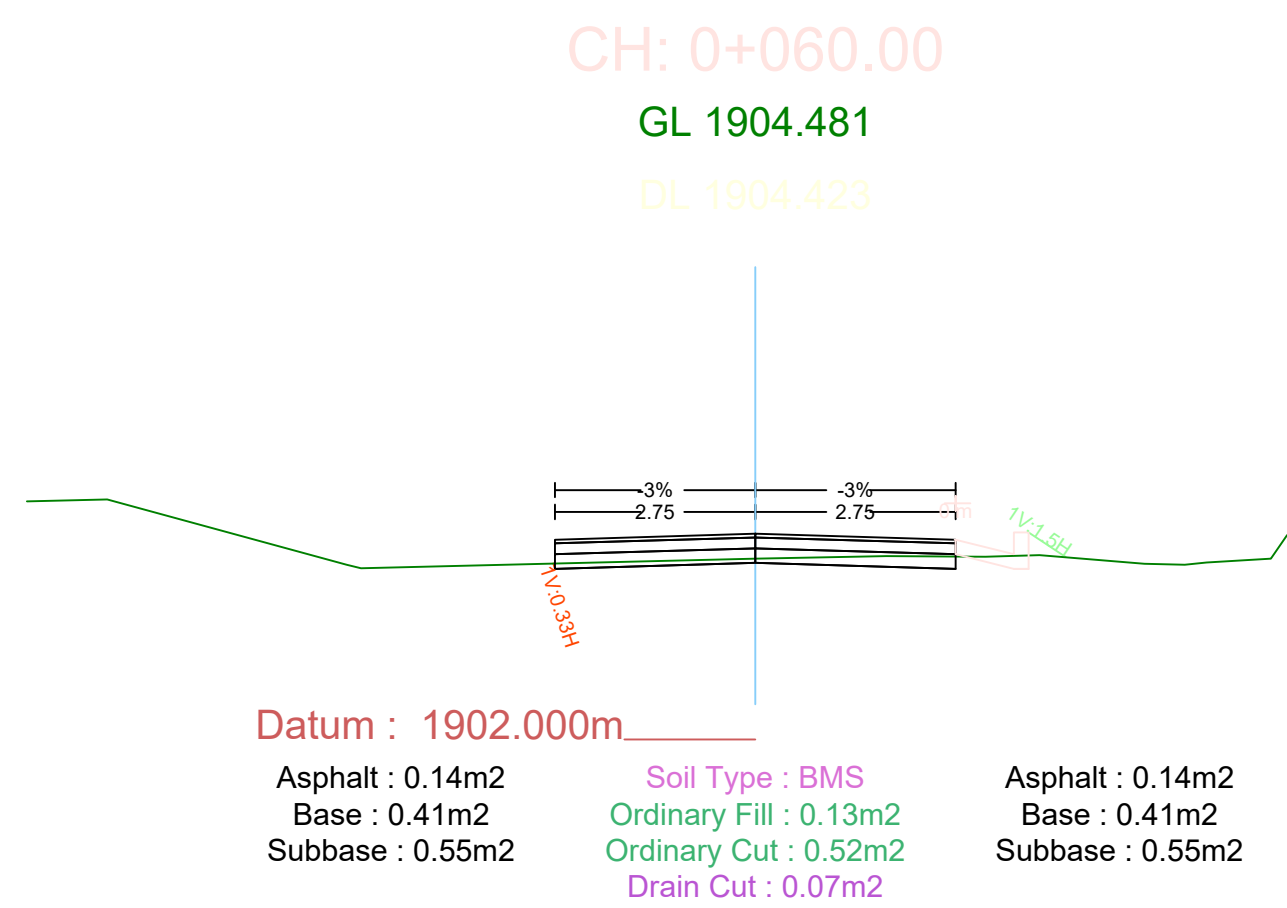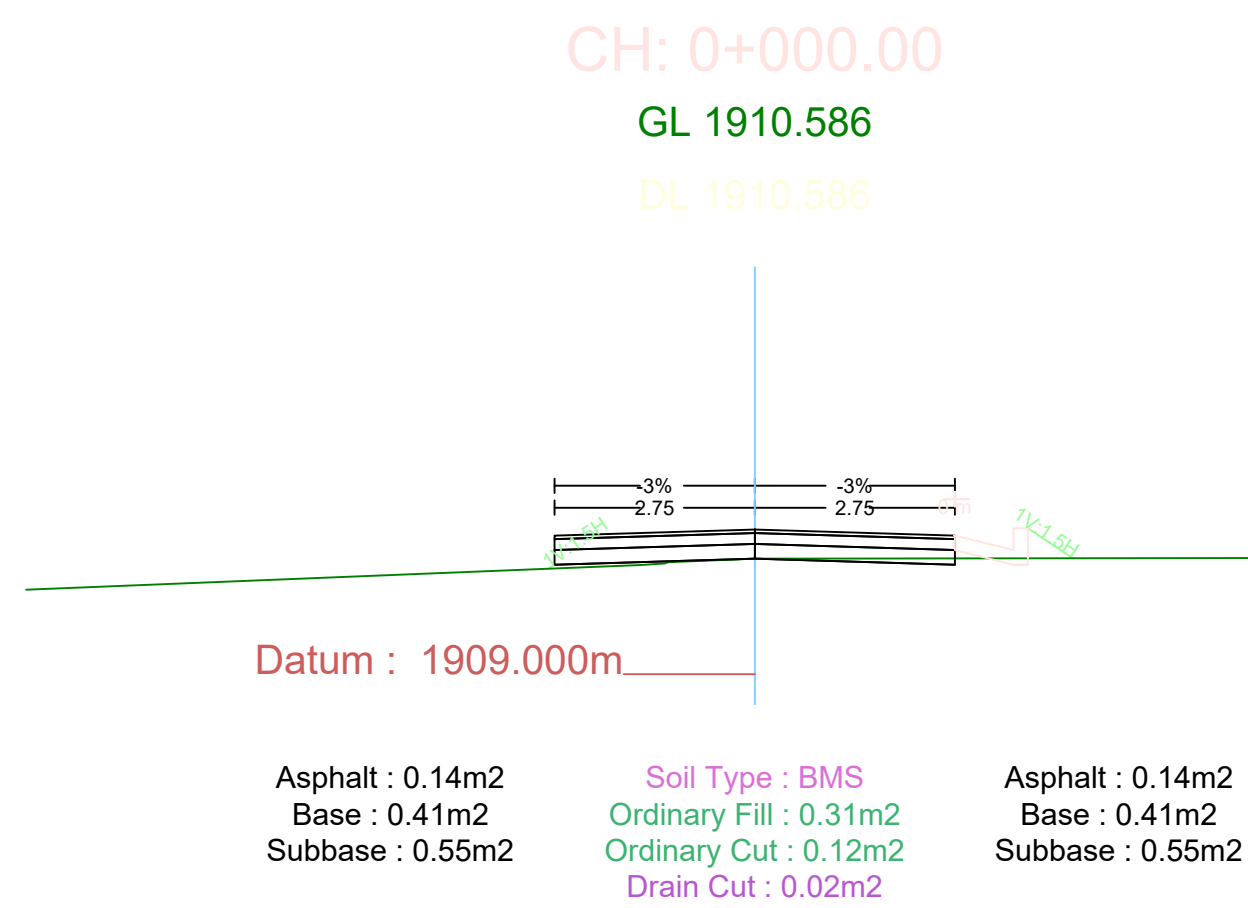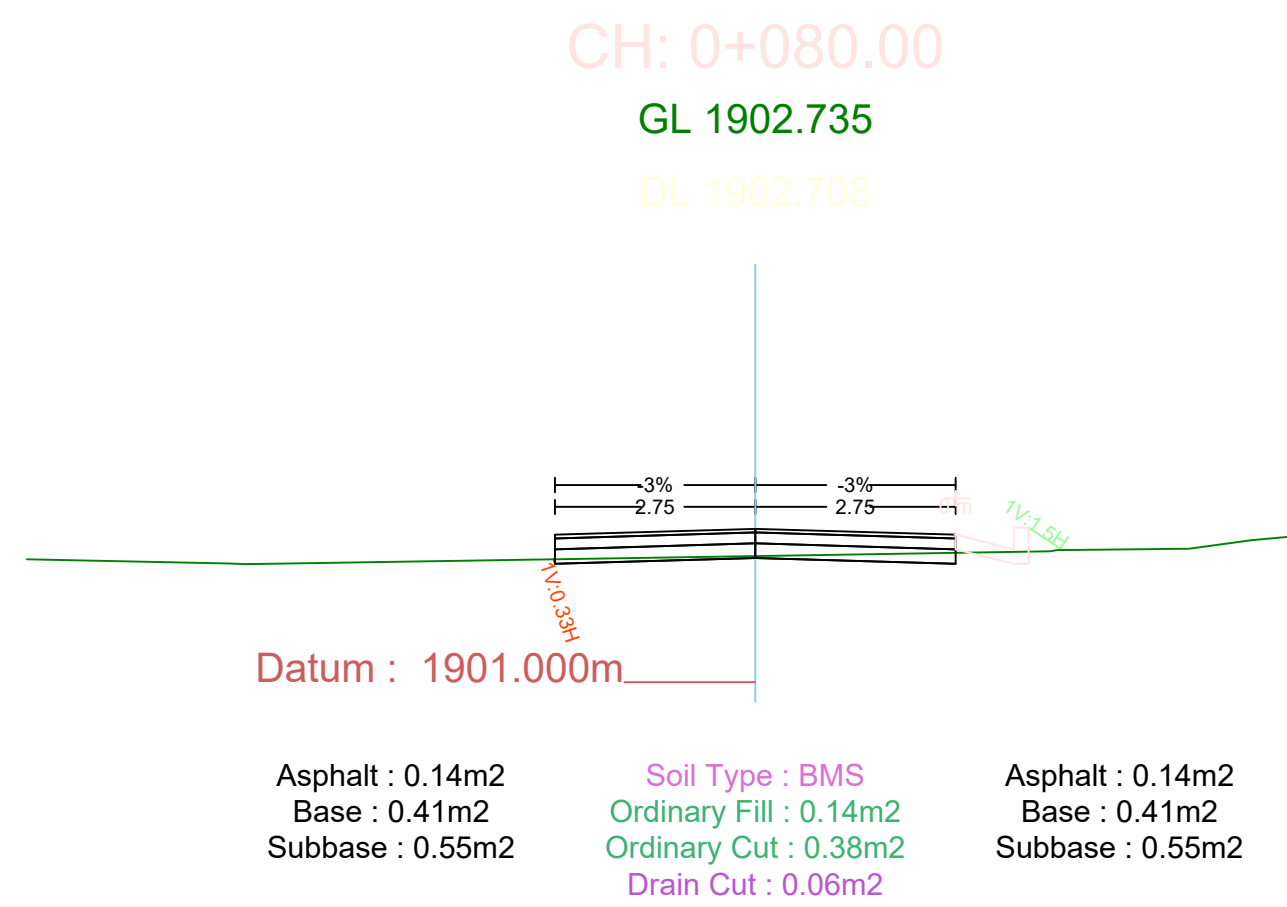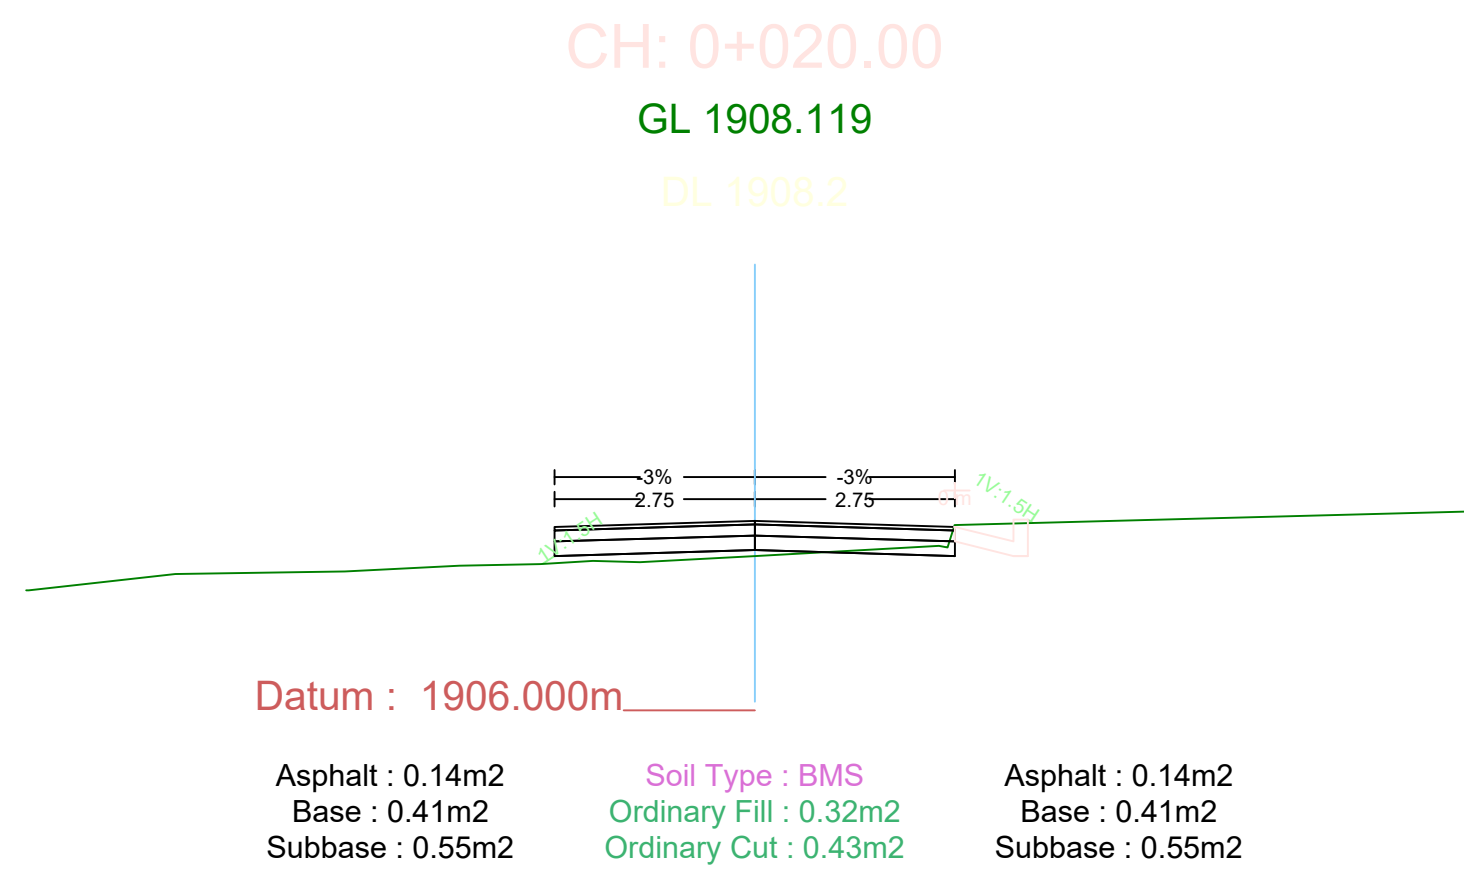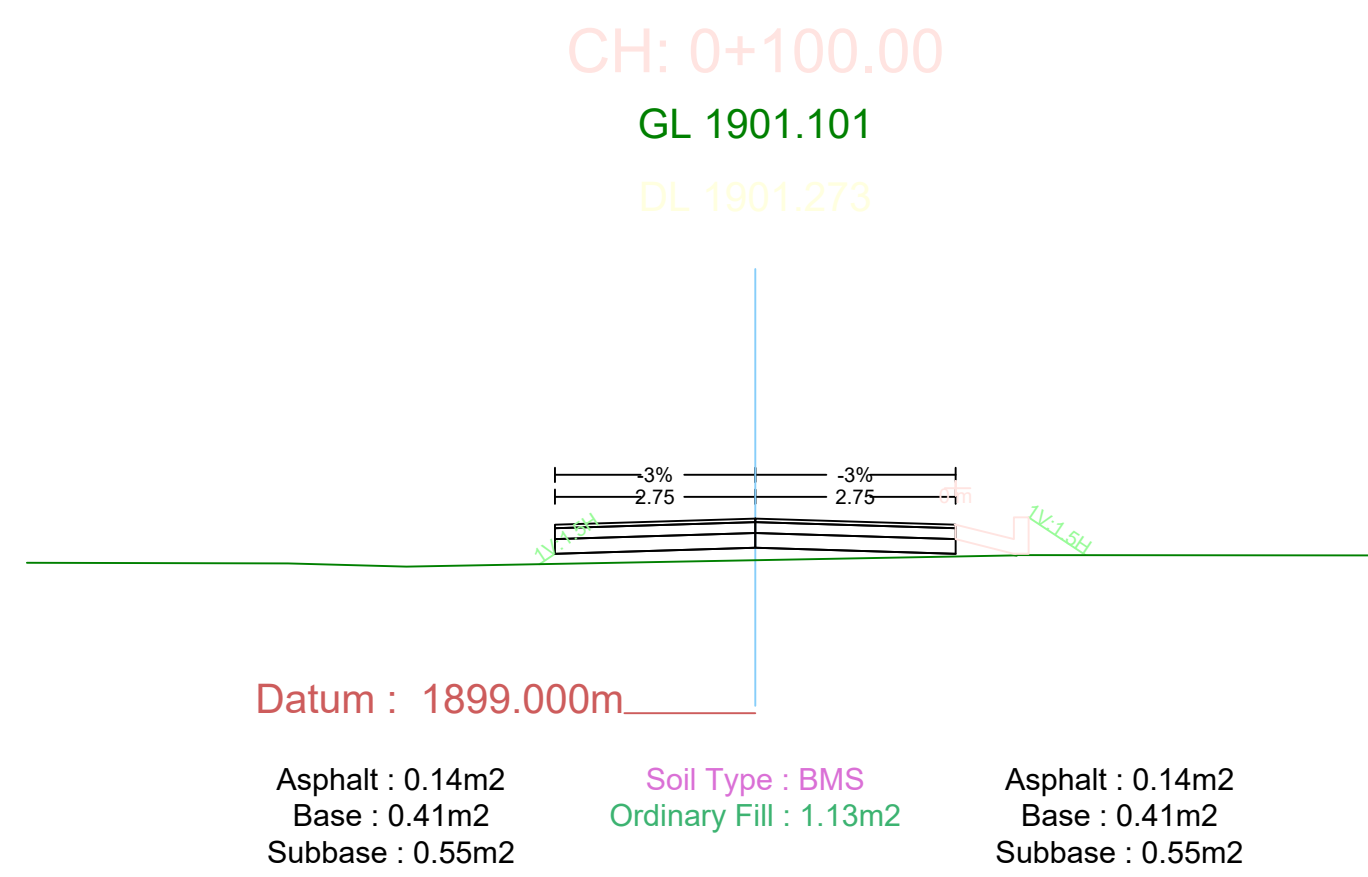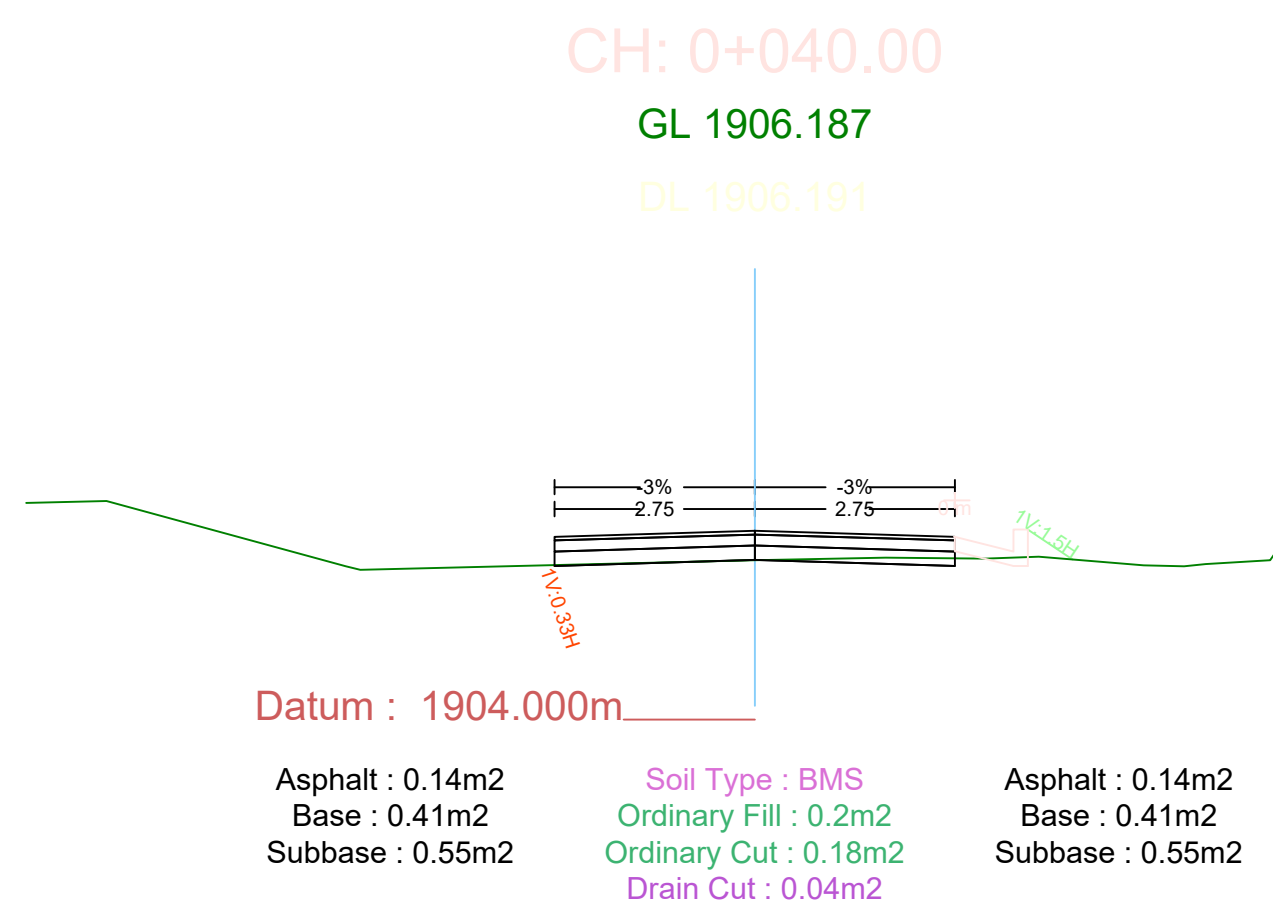

PROJECT:
DPR OF 500MT COLD STORE AT JIRI, DOLAKHA

CONTENT:
ROAD - CROSS SECTION SHEETS

CHECKED BY:

APPROVED BY :

SCALE :

DATE:

REVISION:

CONSULTANT:


Sworaj Consultants Pvt. Ltd.
Samkhushi, Kathmandu

Sheet No

AD
01

CLIENT:
Government of Province
Ministry of Land Management, Agriculture and Cooperative
Province No. 3, Hetauda

FINAL DRAWING

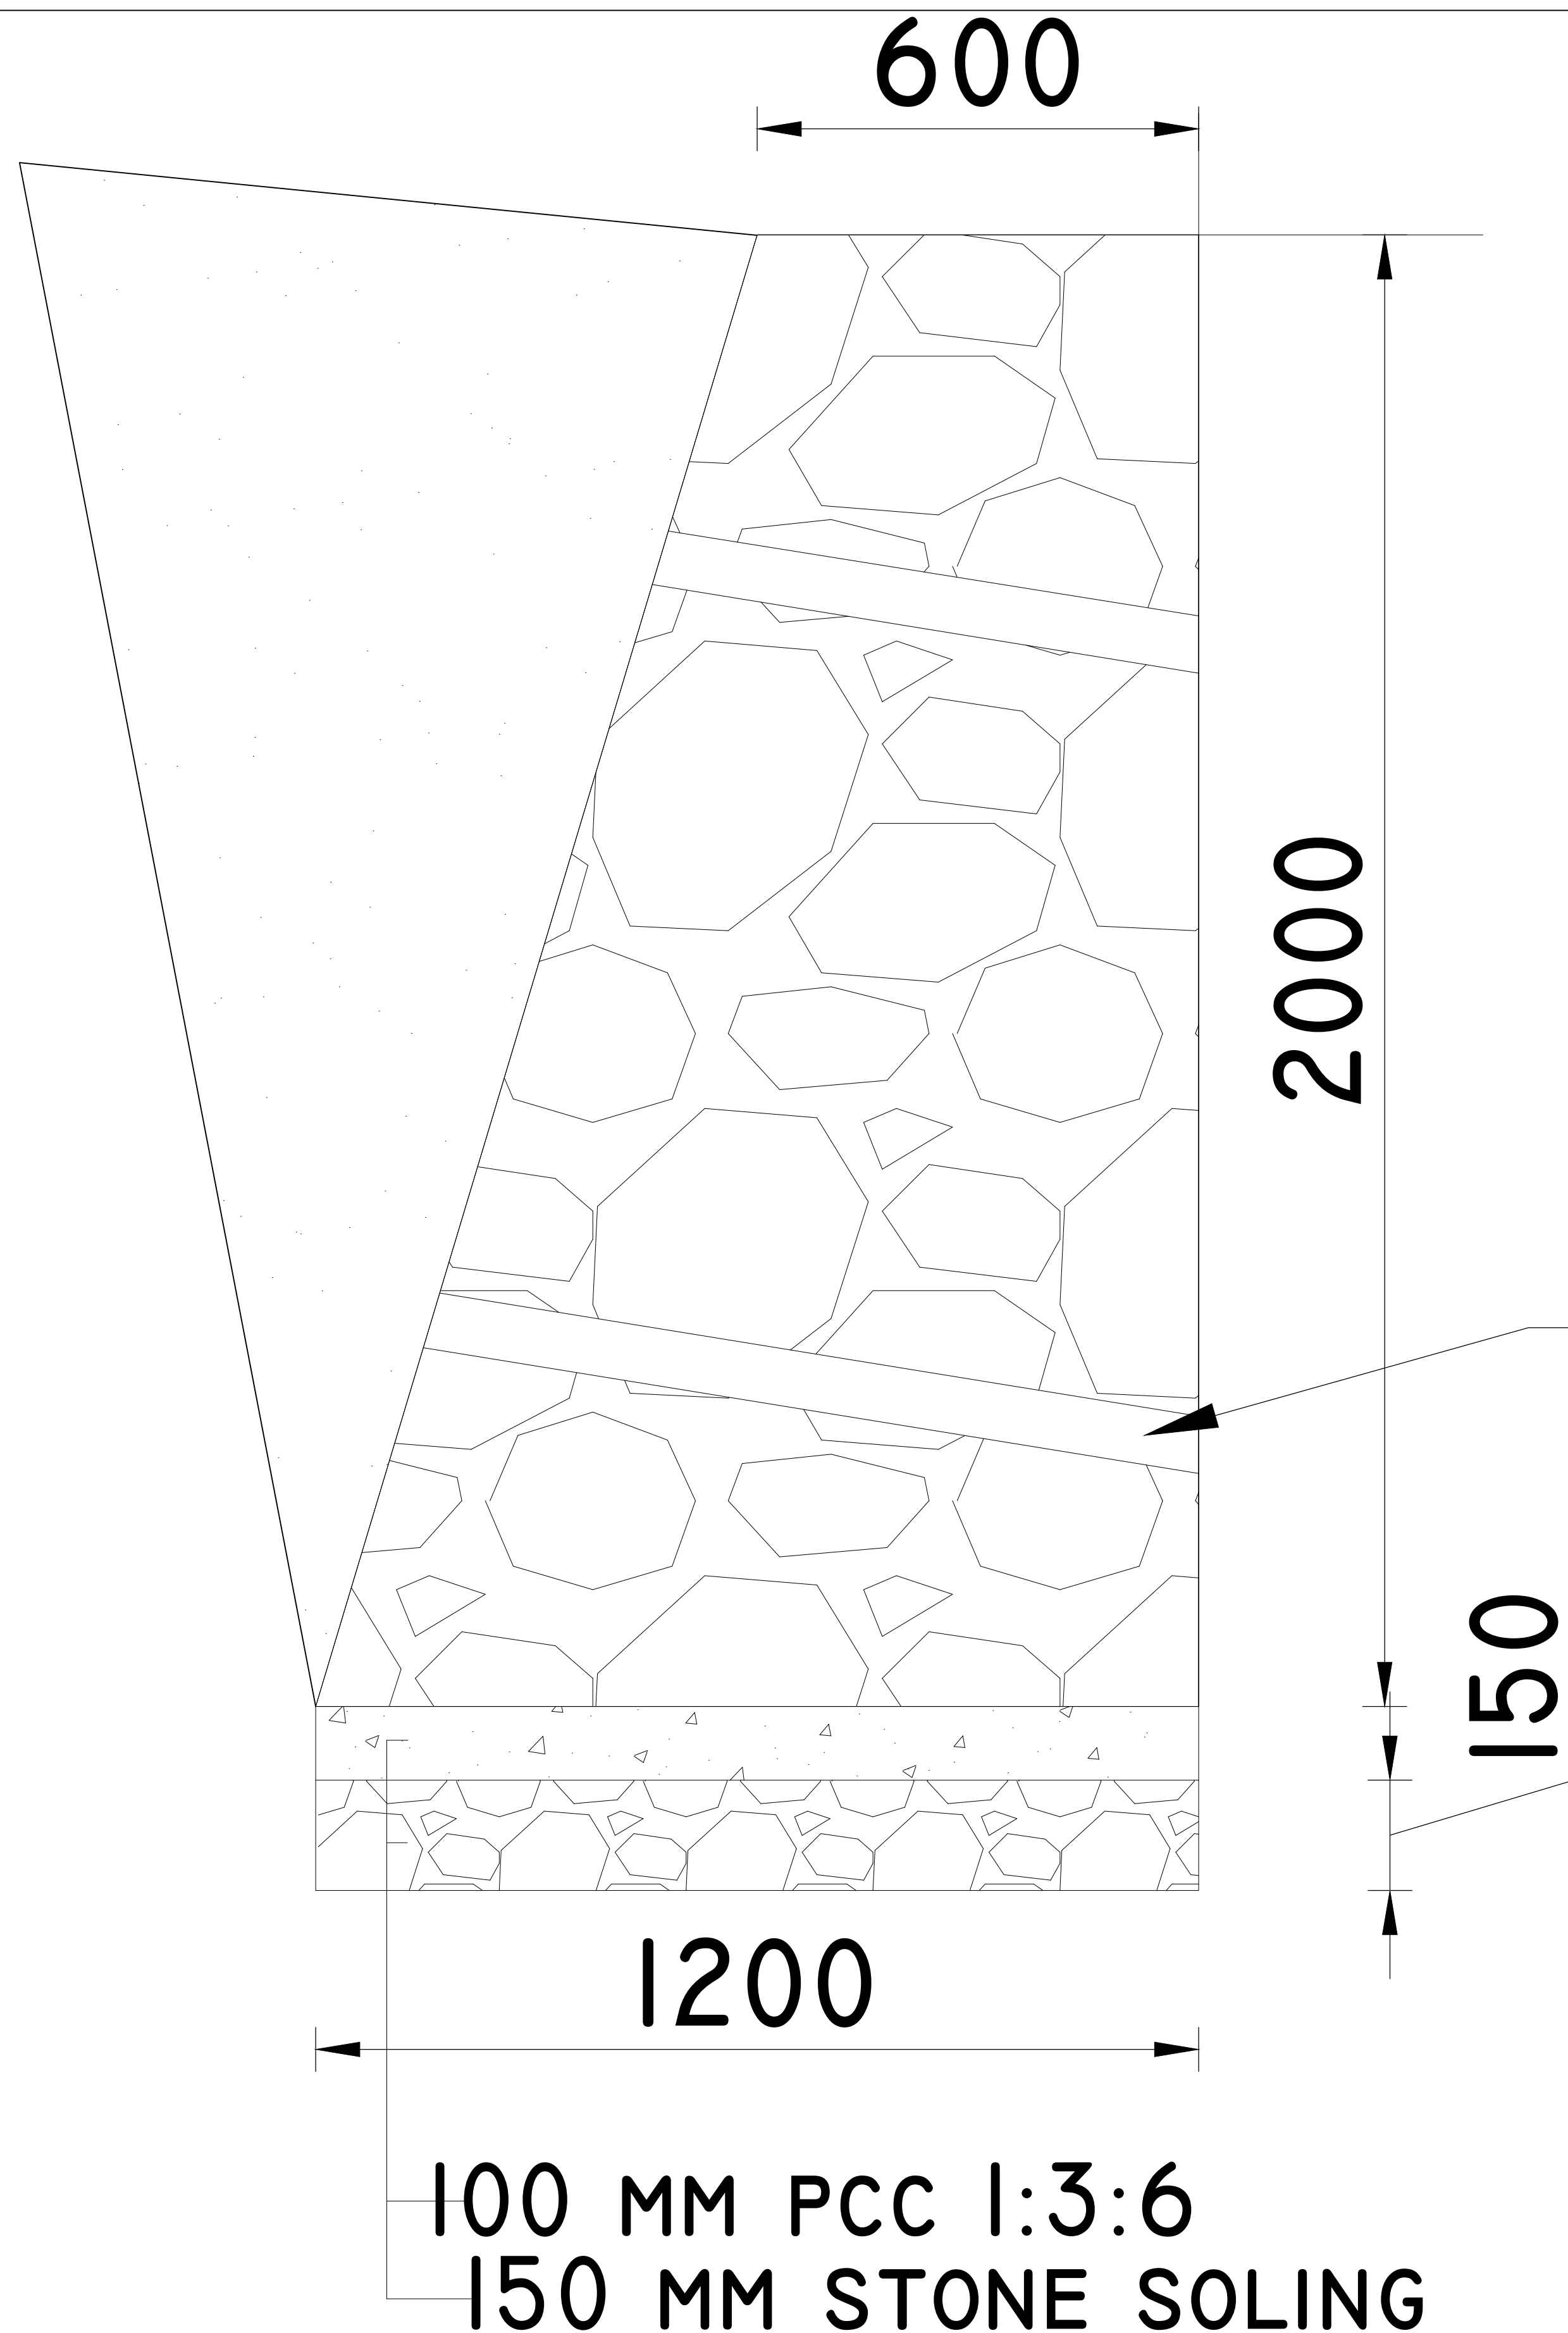

NOTE: RETAINING WALL WORKS TO BE IMPLEMENTED AS PER THE INSTRUCTION OF THE ENGINEER.

75MM PIPE

150

100 MM PCC 1:3:6
150 MM STONE SOLING

PROJECT: DPR OF 500MT COLD STORE AT JIRI, DOLAKHA	CONTENT: RETAINING WALL		CHECKED BY: APPROVED BY :	CONSULTANT: Sworaj Consultants Pvt. Ltd. Samkhushi, Kathmandu	Sheet No
CLIENT: Government of Province Ministry of Land Management, Agriculture and Cooperative Province No. 3, Hetauda	FINAL DRAWING		SCALE :		MB 02
			DATE: REVISION:		